

ТИПОВОЙ ПРОЕКТ

на алюминиевые светопрозрачные конструкции

Объекты расположены: Московская область, Одинцовский район, д. Жуковка,
ДП "Жуковка-2", участок 52 дома 94, 95, участок 15 дома 450, 452.

Рабочие чертежи конструкций остекления.

Шифр: 20022020

Заказчик

ГАП



ООО "Гармония"
Генеральный директор

_____ Кудрявцев Д.С.

_____ Кораблев Р.

_____ Коноплич С.В.

Москва 2020 г.

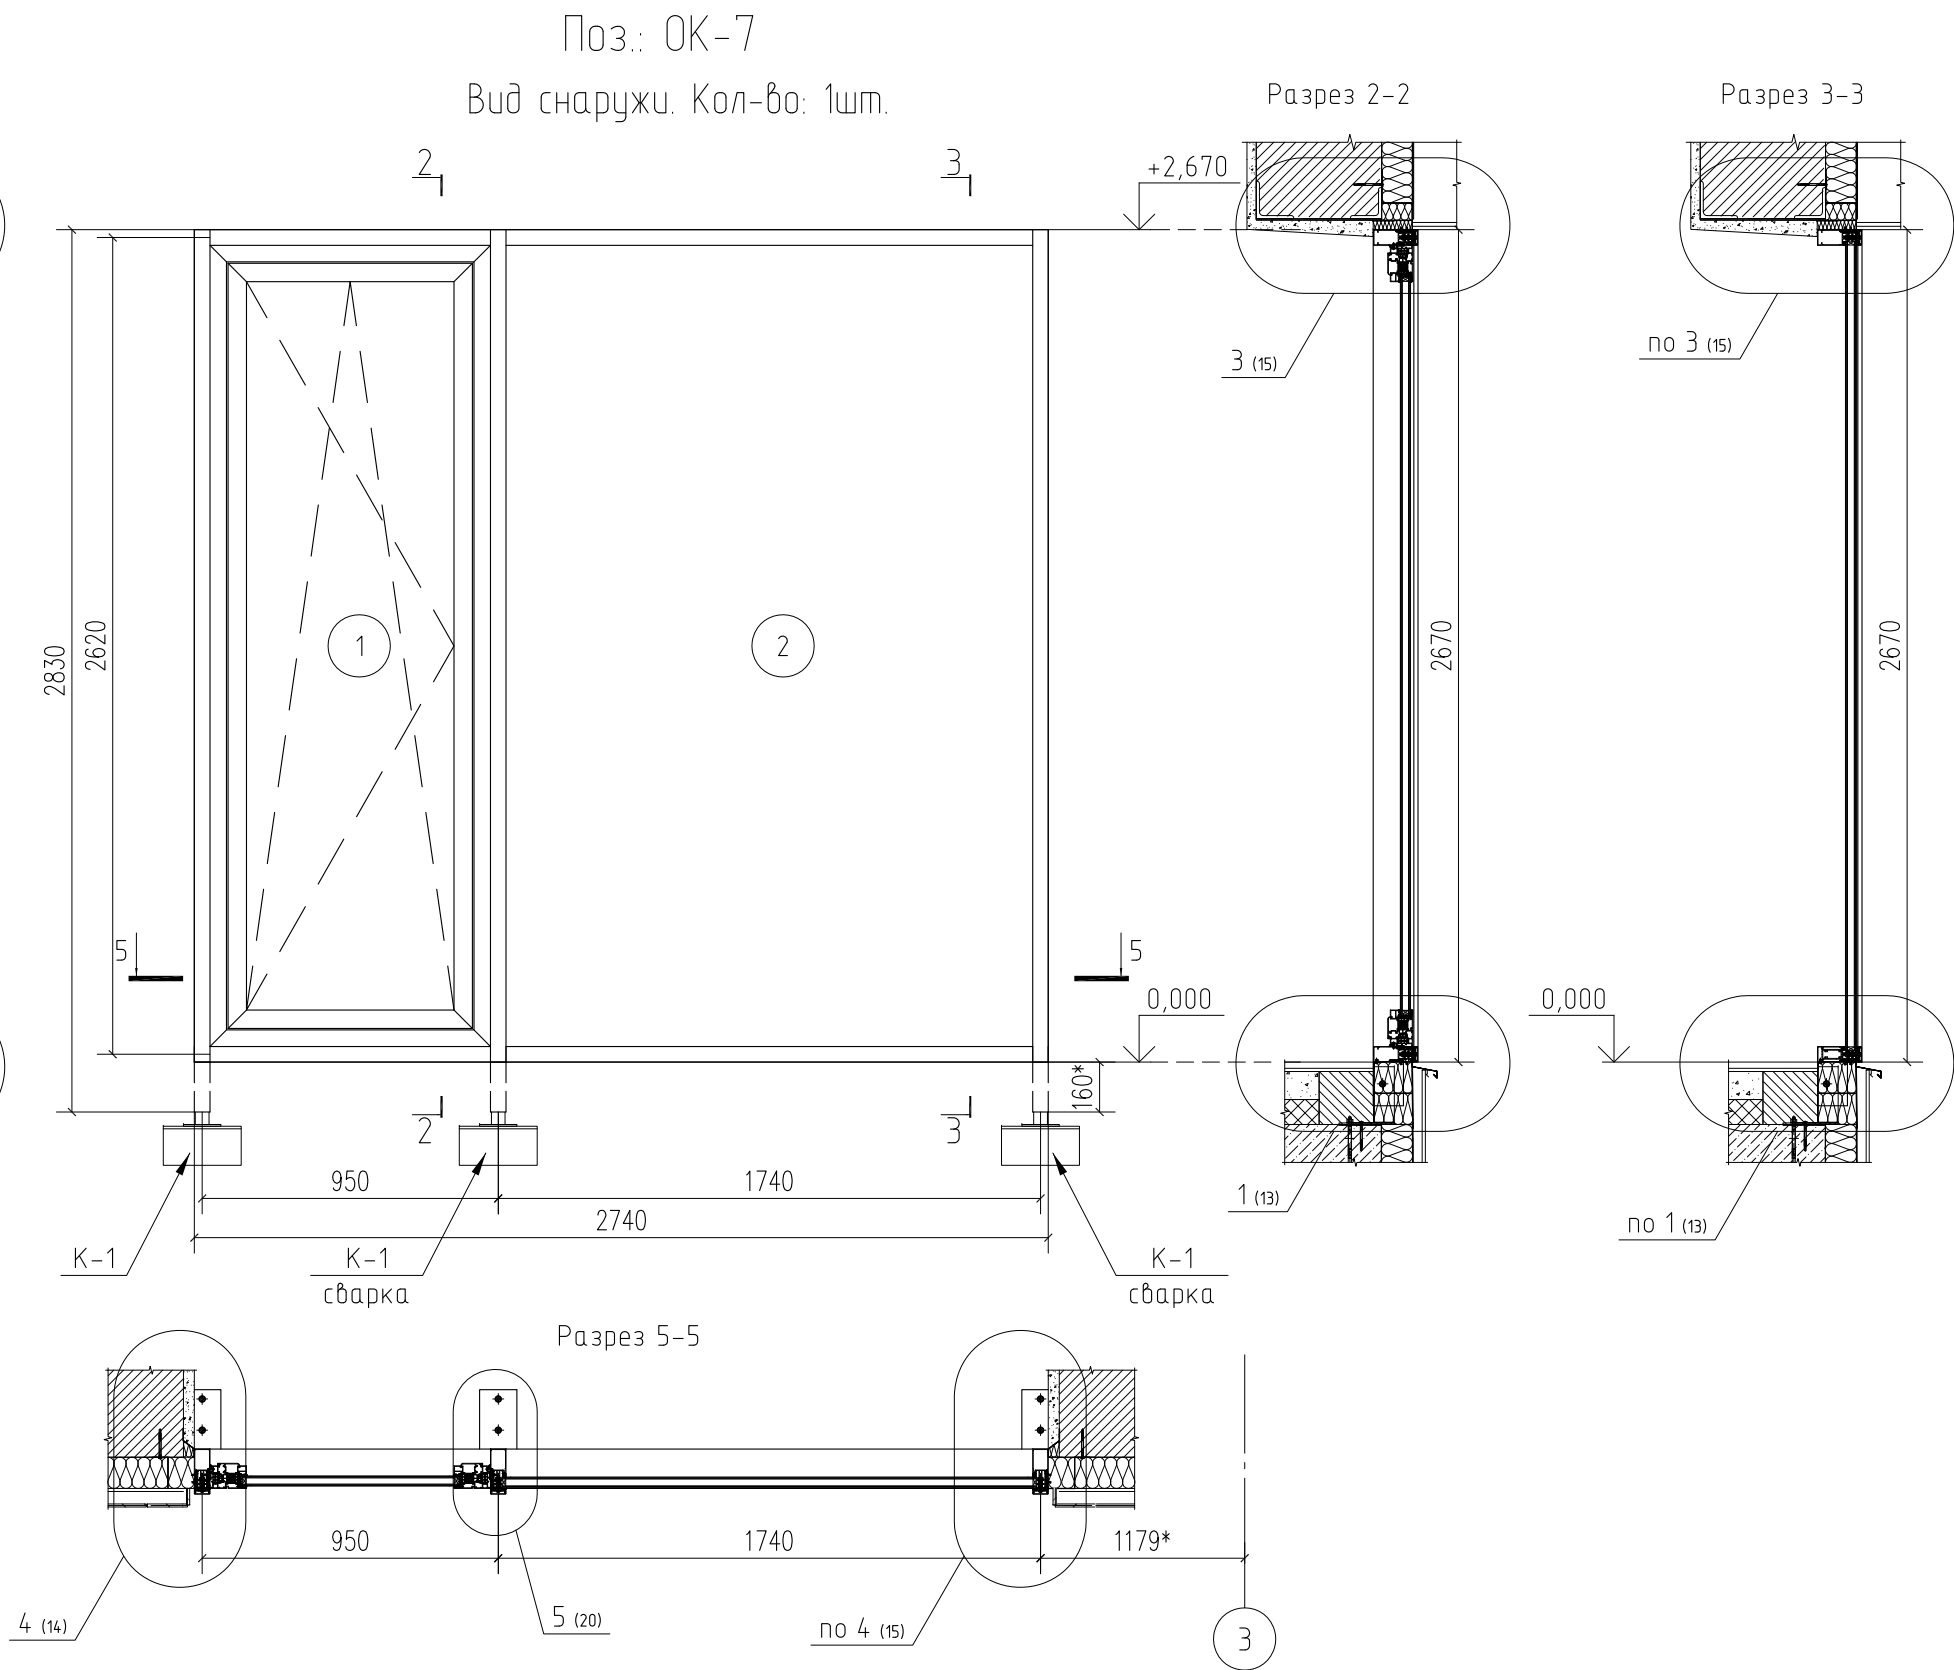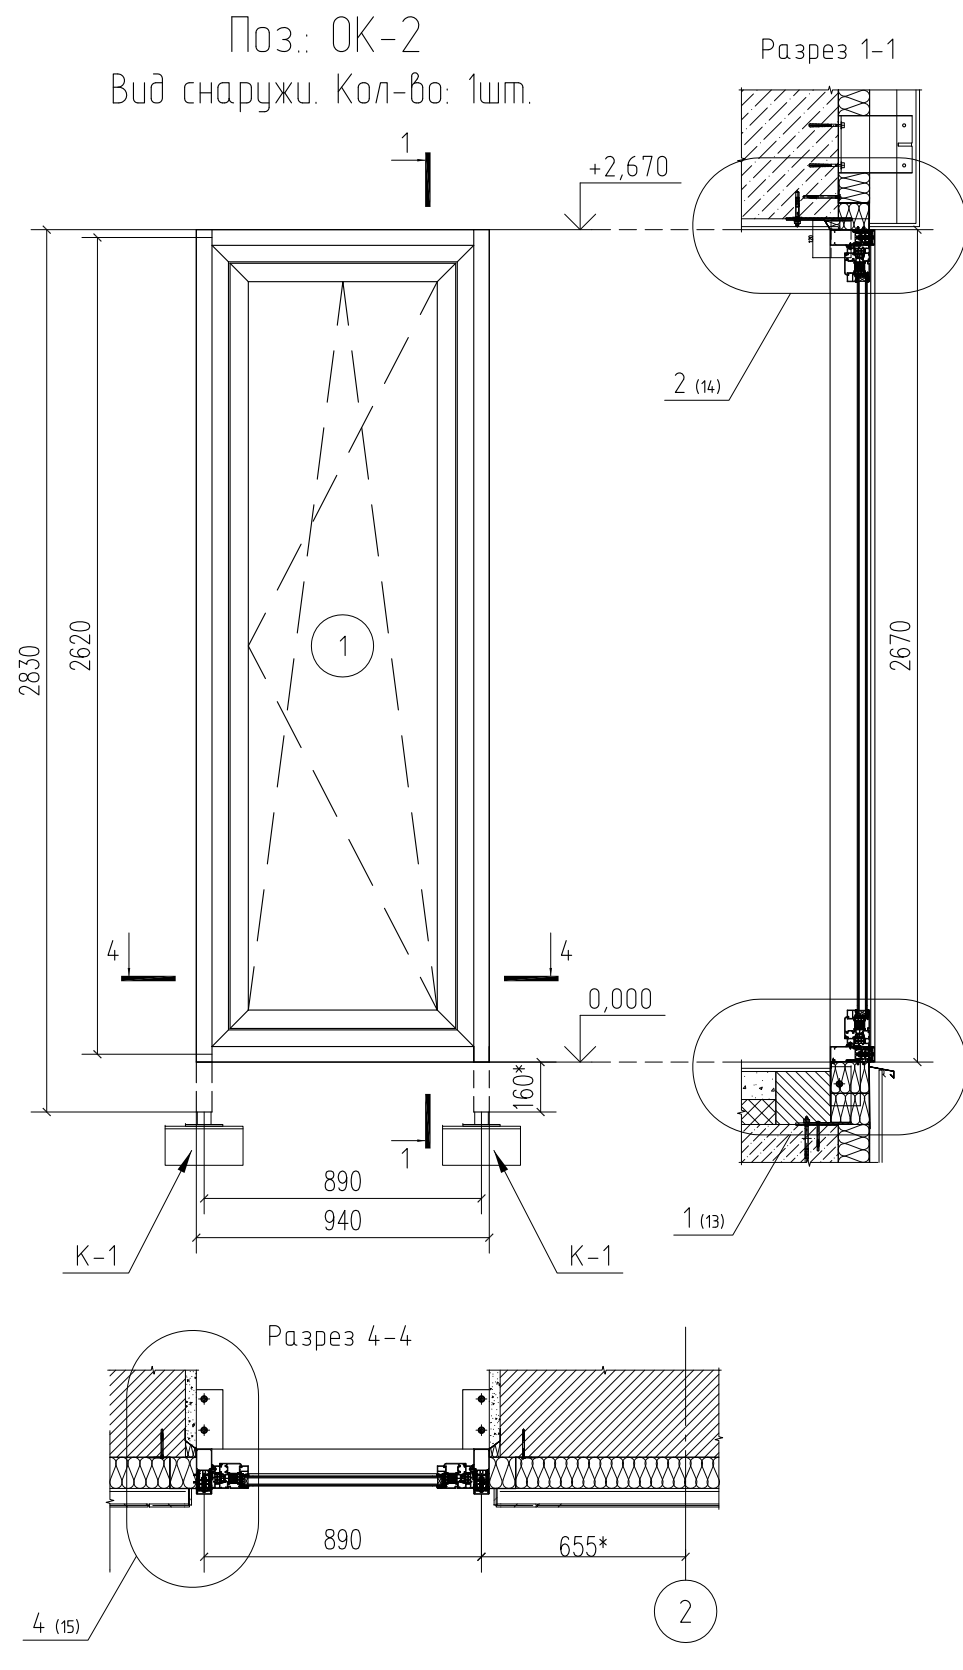


Примечания:

- 1 - стеклопакет однокамерный 32мм.: 6M1-20Ag-6TopN
- 2 - стеклопакет однокамерный 36мм.: 8M1-22Ag-6TopN

						20022020			
						Московская обл., Одинцовский р-н, д.Жуковка, ДП "Жуковка-2"			
Изм.	Кол.уч.	Лист	№ док.	Подп.	Дата	Светопрозрачные алюминиевые конструкции	Стадия	Лист	Листов
Разраб.		Ланцева Н.А.			20.02.2022		Р	4	25
Провер.		Кириянов А.М.				ОК-2, ОК-17. Разрезы 1-1, 2-2, 3-3, 4-4, 5-5.	ООО "Гармония"		
Утвердил		Коноплич С.В.							
ГИП									


Поз.: ОК-2

Вид снаружи. Кол-во: 1шт.

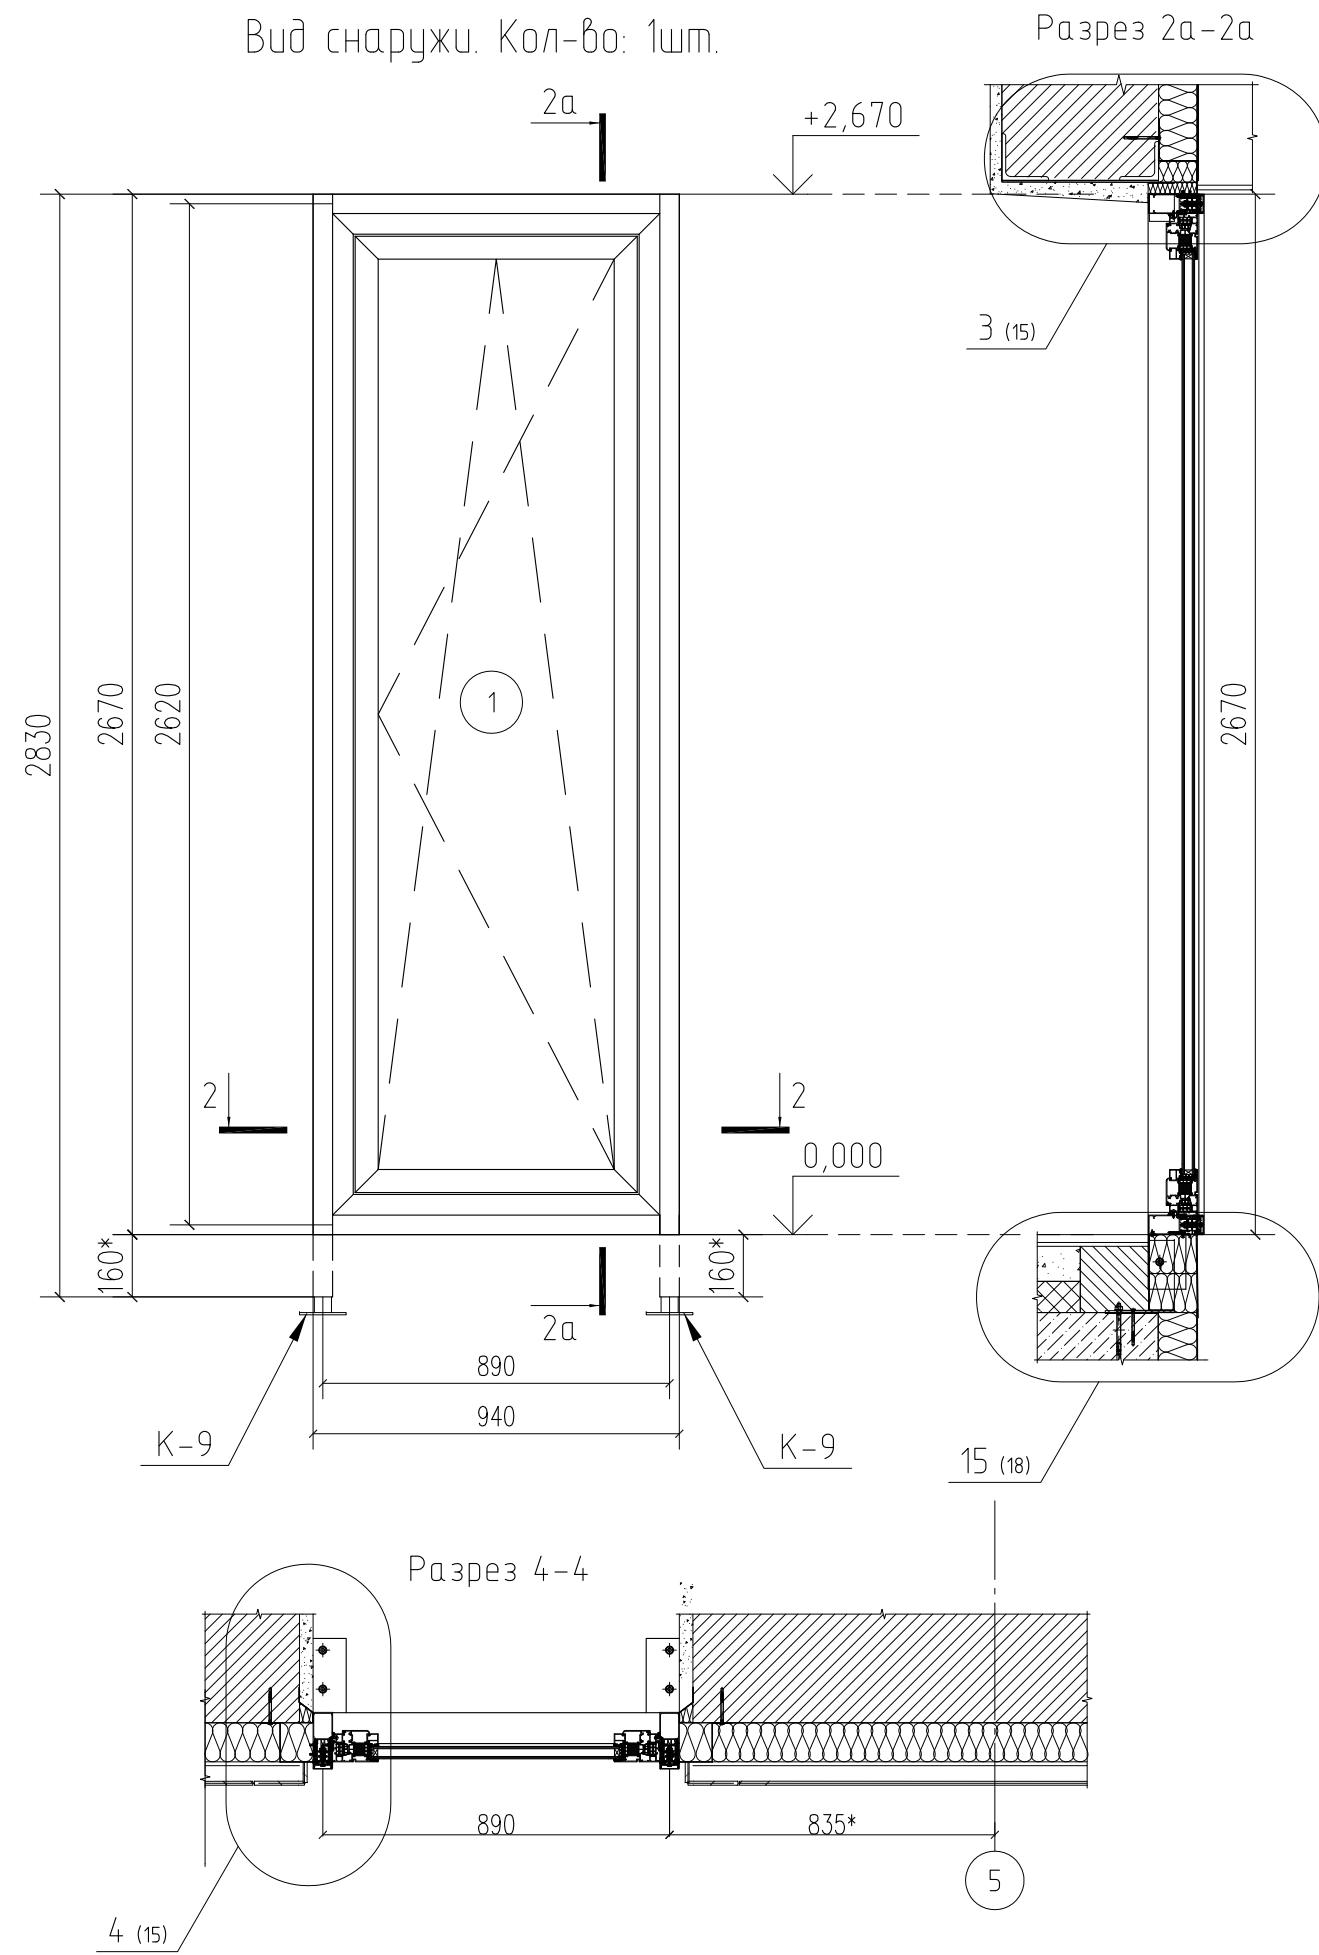

Поз.: ОК-19

Вид снаружи. Кол-во: 1шт.


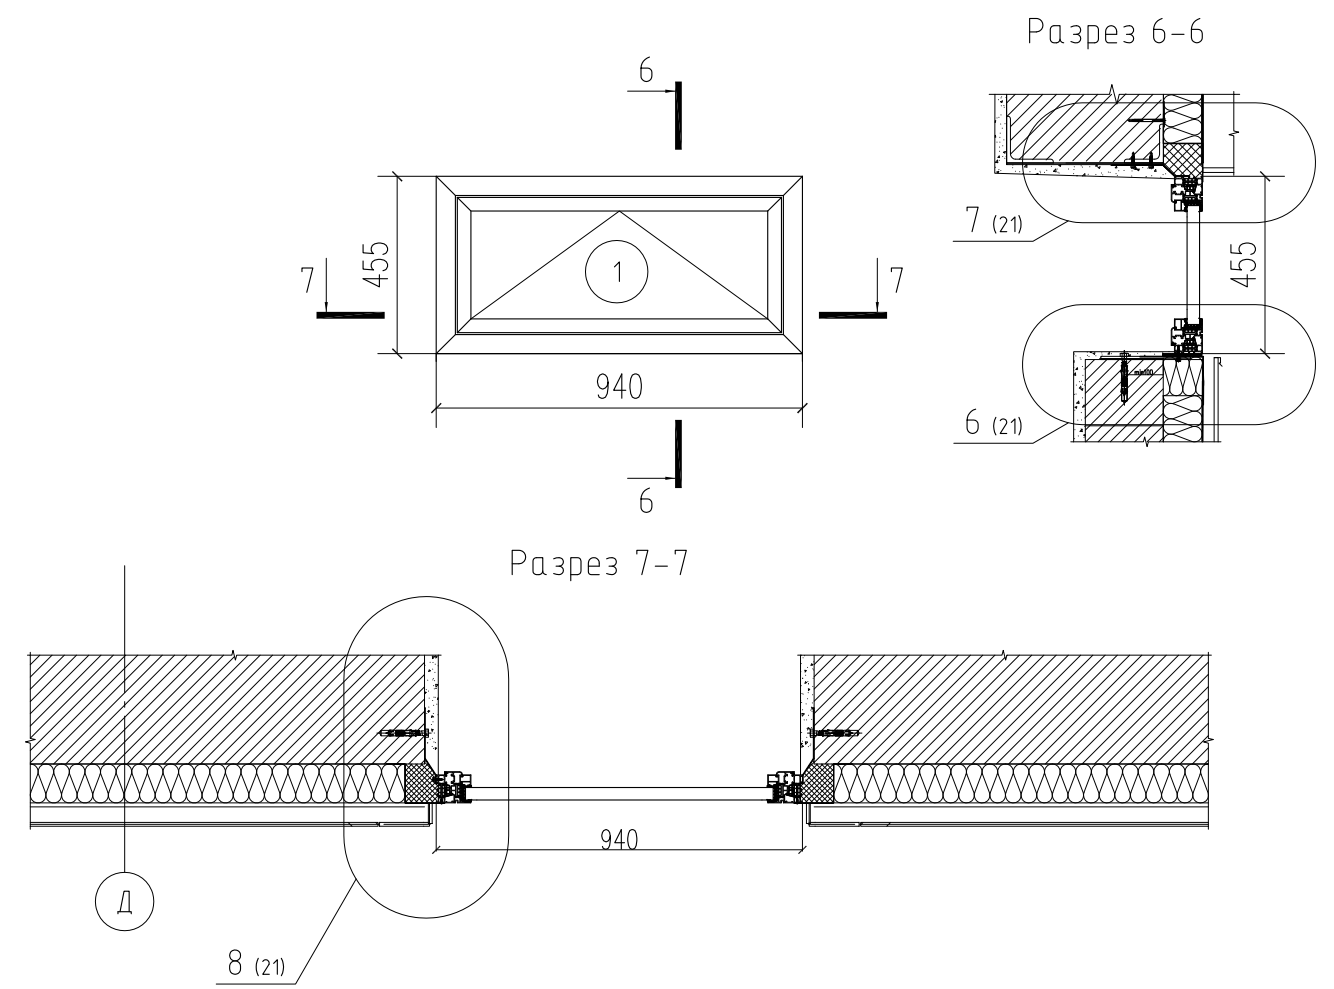


Примечания:




1 - стеклопакет однокамерный 32мм.: 6M1-20Ag-6TopN

						20022020			
						Московская обл., Одинцовский р-н, д.Жуковка, ДП “Жуковка-2”			
Изм.	Кол.уч.	Лист	№ док.	Подп.	Дата	Светопрозрачные алюминиевые конструкции	Стадия	Лист	Листов
Разраб.		Ланцева Н.А.			20.02.20г.		Р	5	25
Провер.		Кириянов А.М.				ОК-2, ОК-19. Разрезы 2а-2а, 4-4, 6-6, 7-7	ООО "Гармония"		
Утвердил		Коноплич С.В.							
ГИП									

Поз.: ОК-3
Вид снаружи. Кол-во: 1шт.

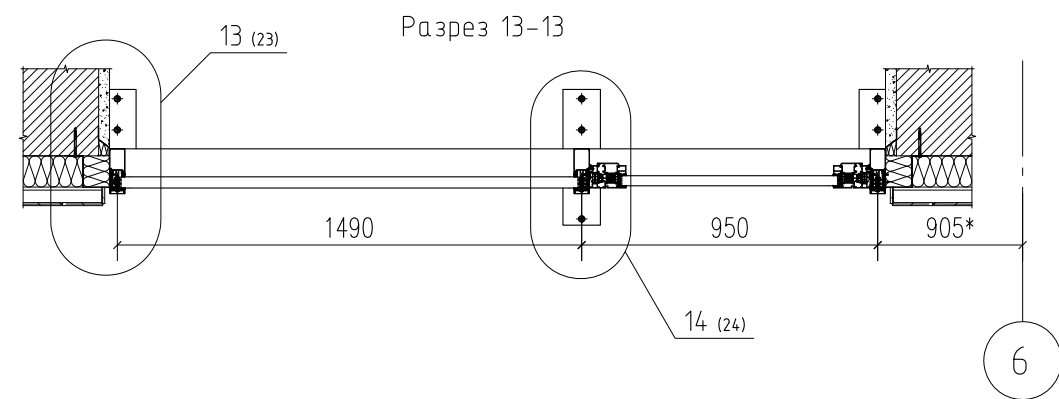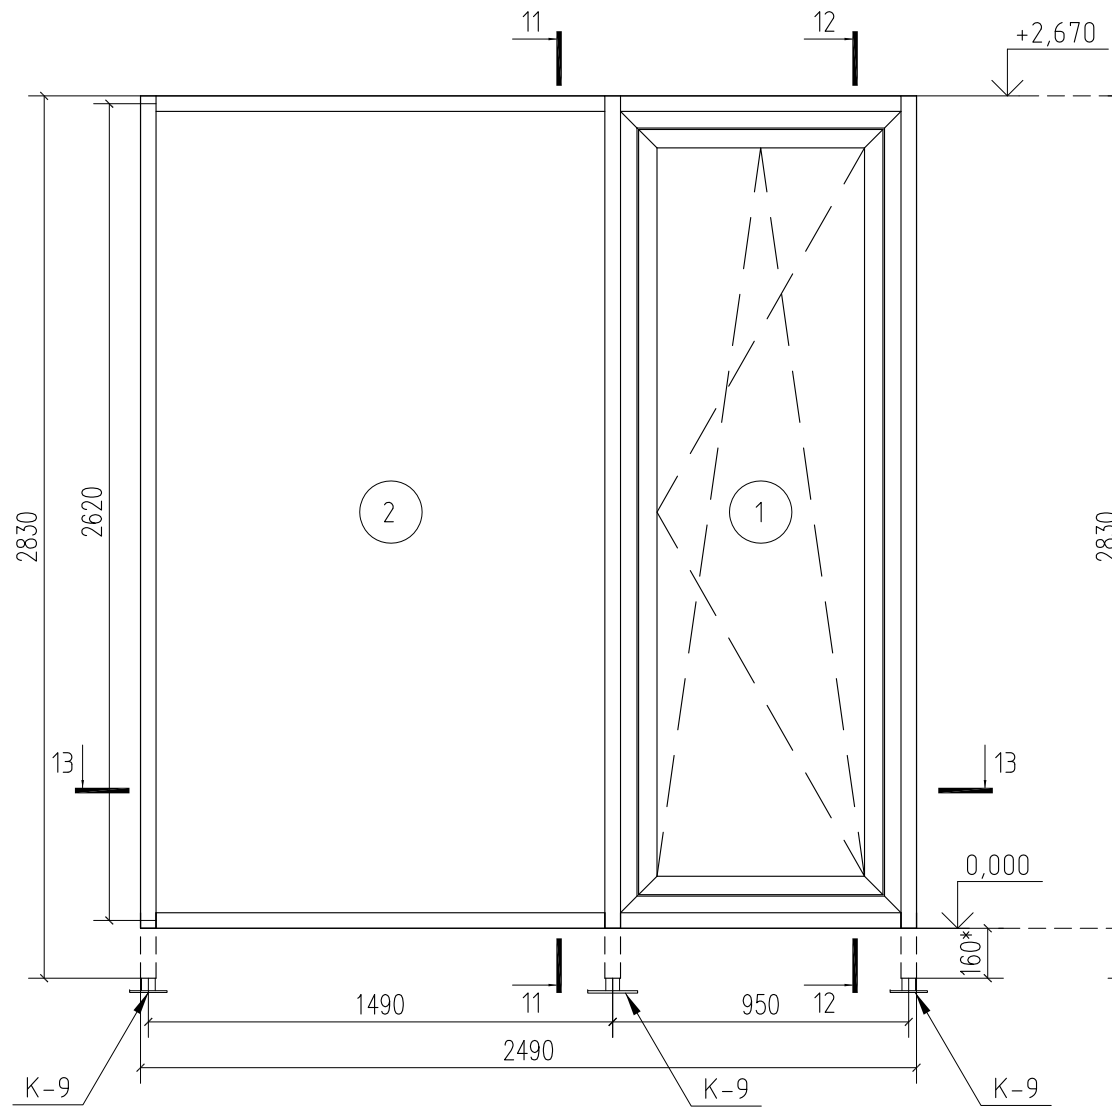


Поз.: ОК-11
Вид снаружи. Кол-во: 1шт.

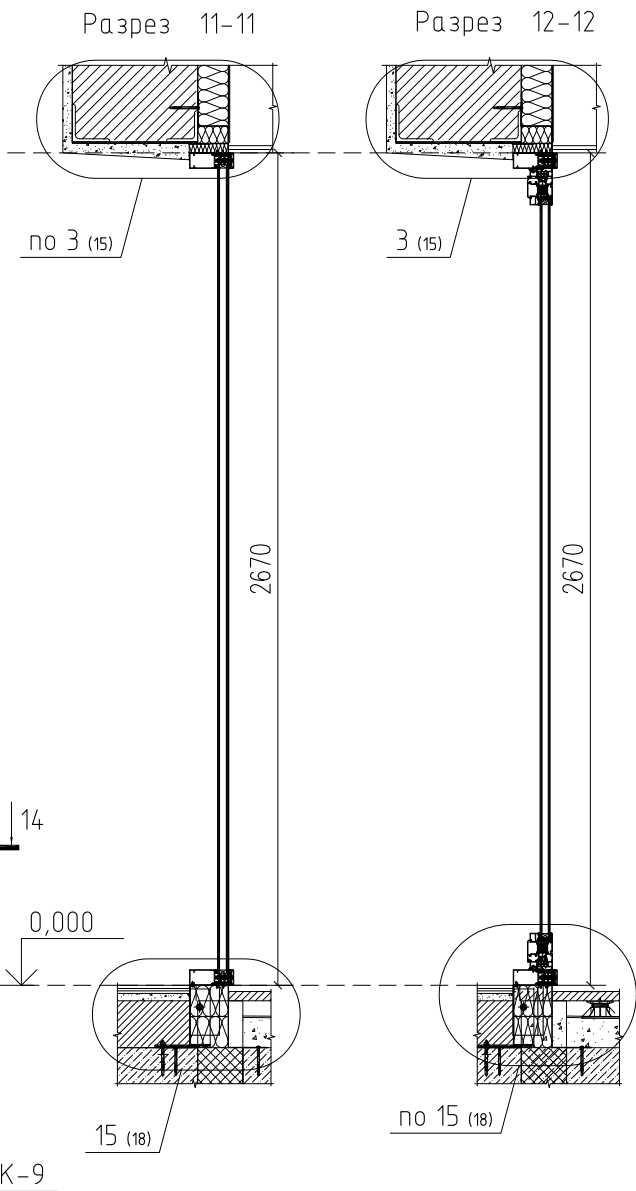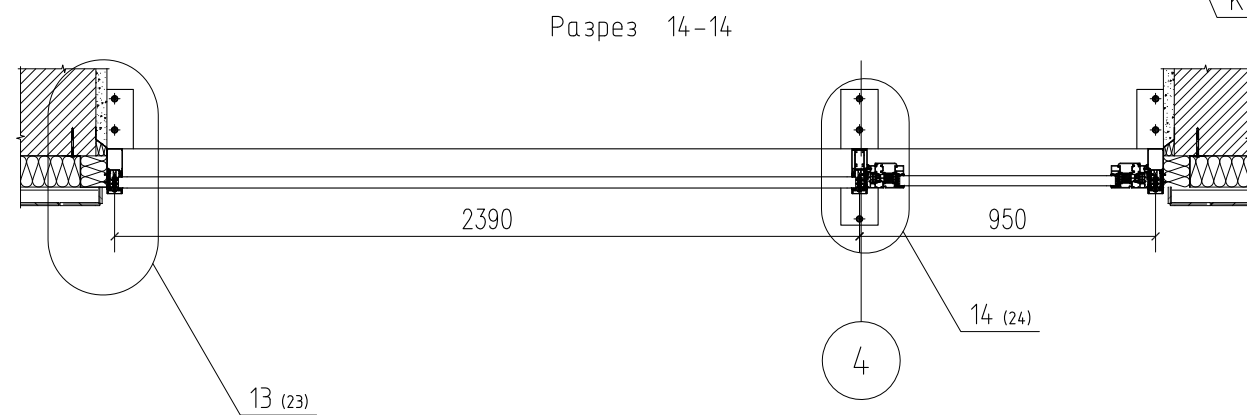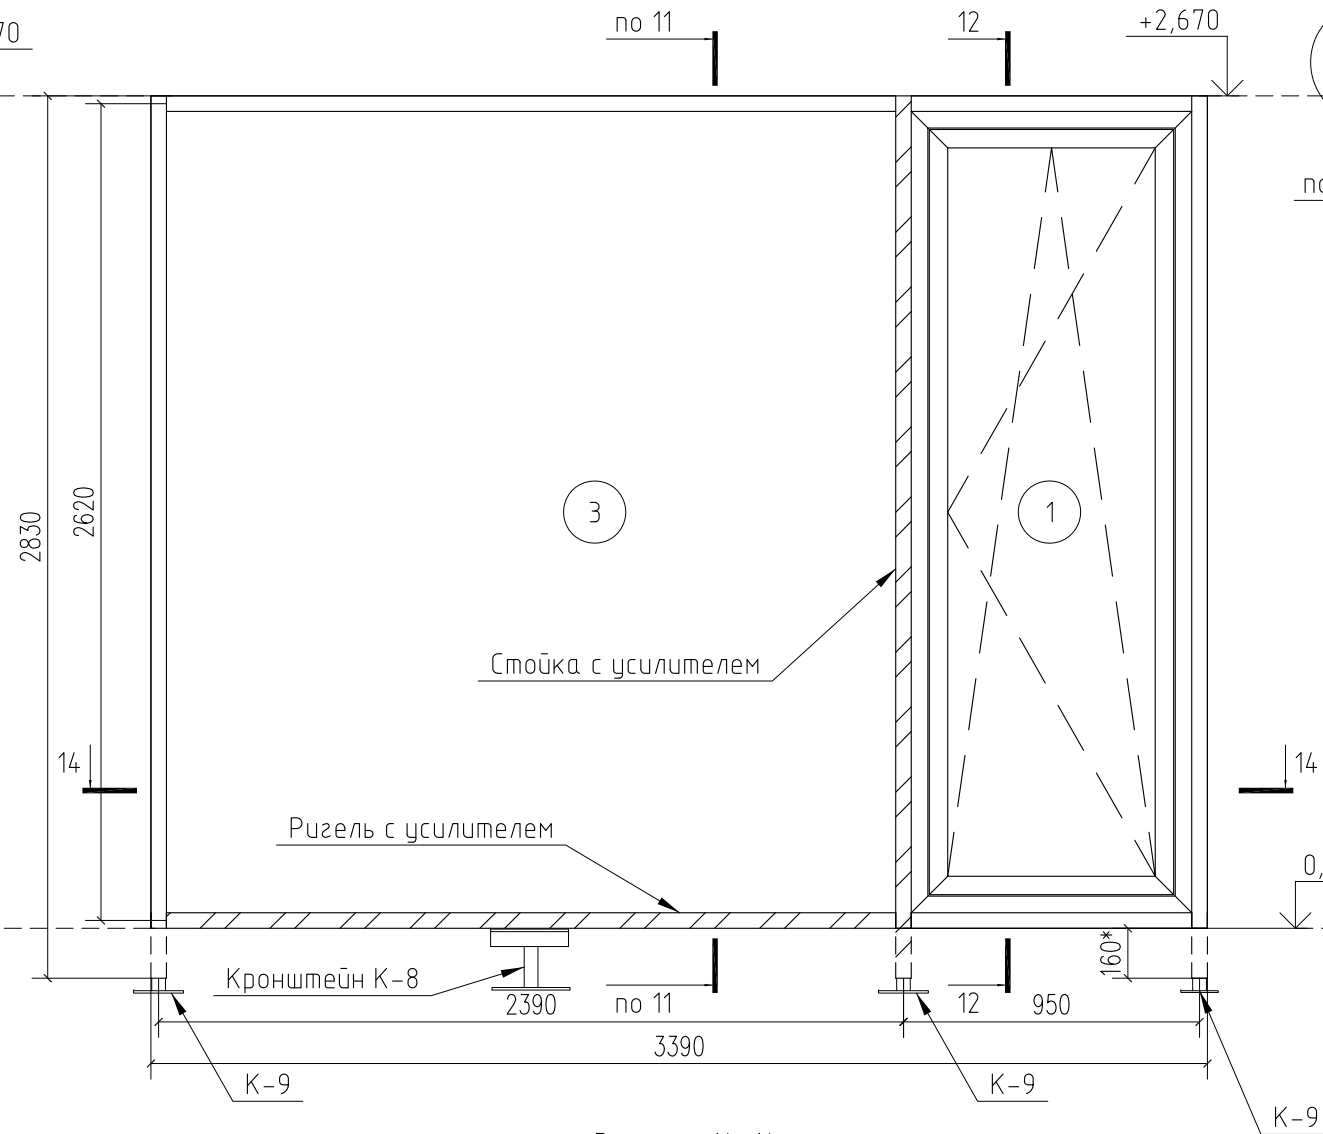

Примечания:

- 1 - стеклопакет однокамерный 32мм.: 6M1-20Ag-6TopN
- 2 - стеклопакет однокамерный 36мм.: 8M1-22Ag-6TopN
- 3 - стеклопакет однокамерный 36мм.: 10зак.-16Ag-10зак.TopN

						20022020			
						Московская обл., Одинцовский р-н, д.Жуковка, ДП "Жуковка-2"			
Изм.	Кол.уч.	Лист	№ док.	Подп.	Дата	Светопрозрачные алюминиевые конструкции	Стадия	Лист	Листов
Разраб.		Ланцева Н.А.			20.02.2020		Р	7	25
Провер.		Кирьянов А.М.							
Утвердил		Коноплич С.В.				ОК-3, ОК-11. Разрез 11-11, 12-12, 13-13, 14-14.		ООО "Гармония"	
ГИП									

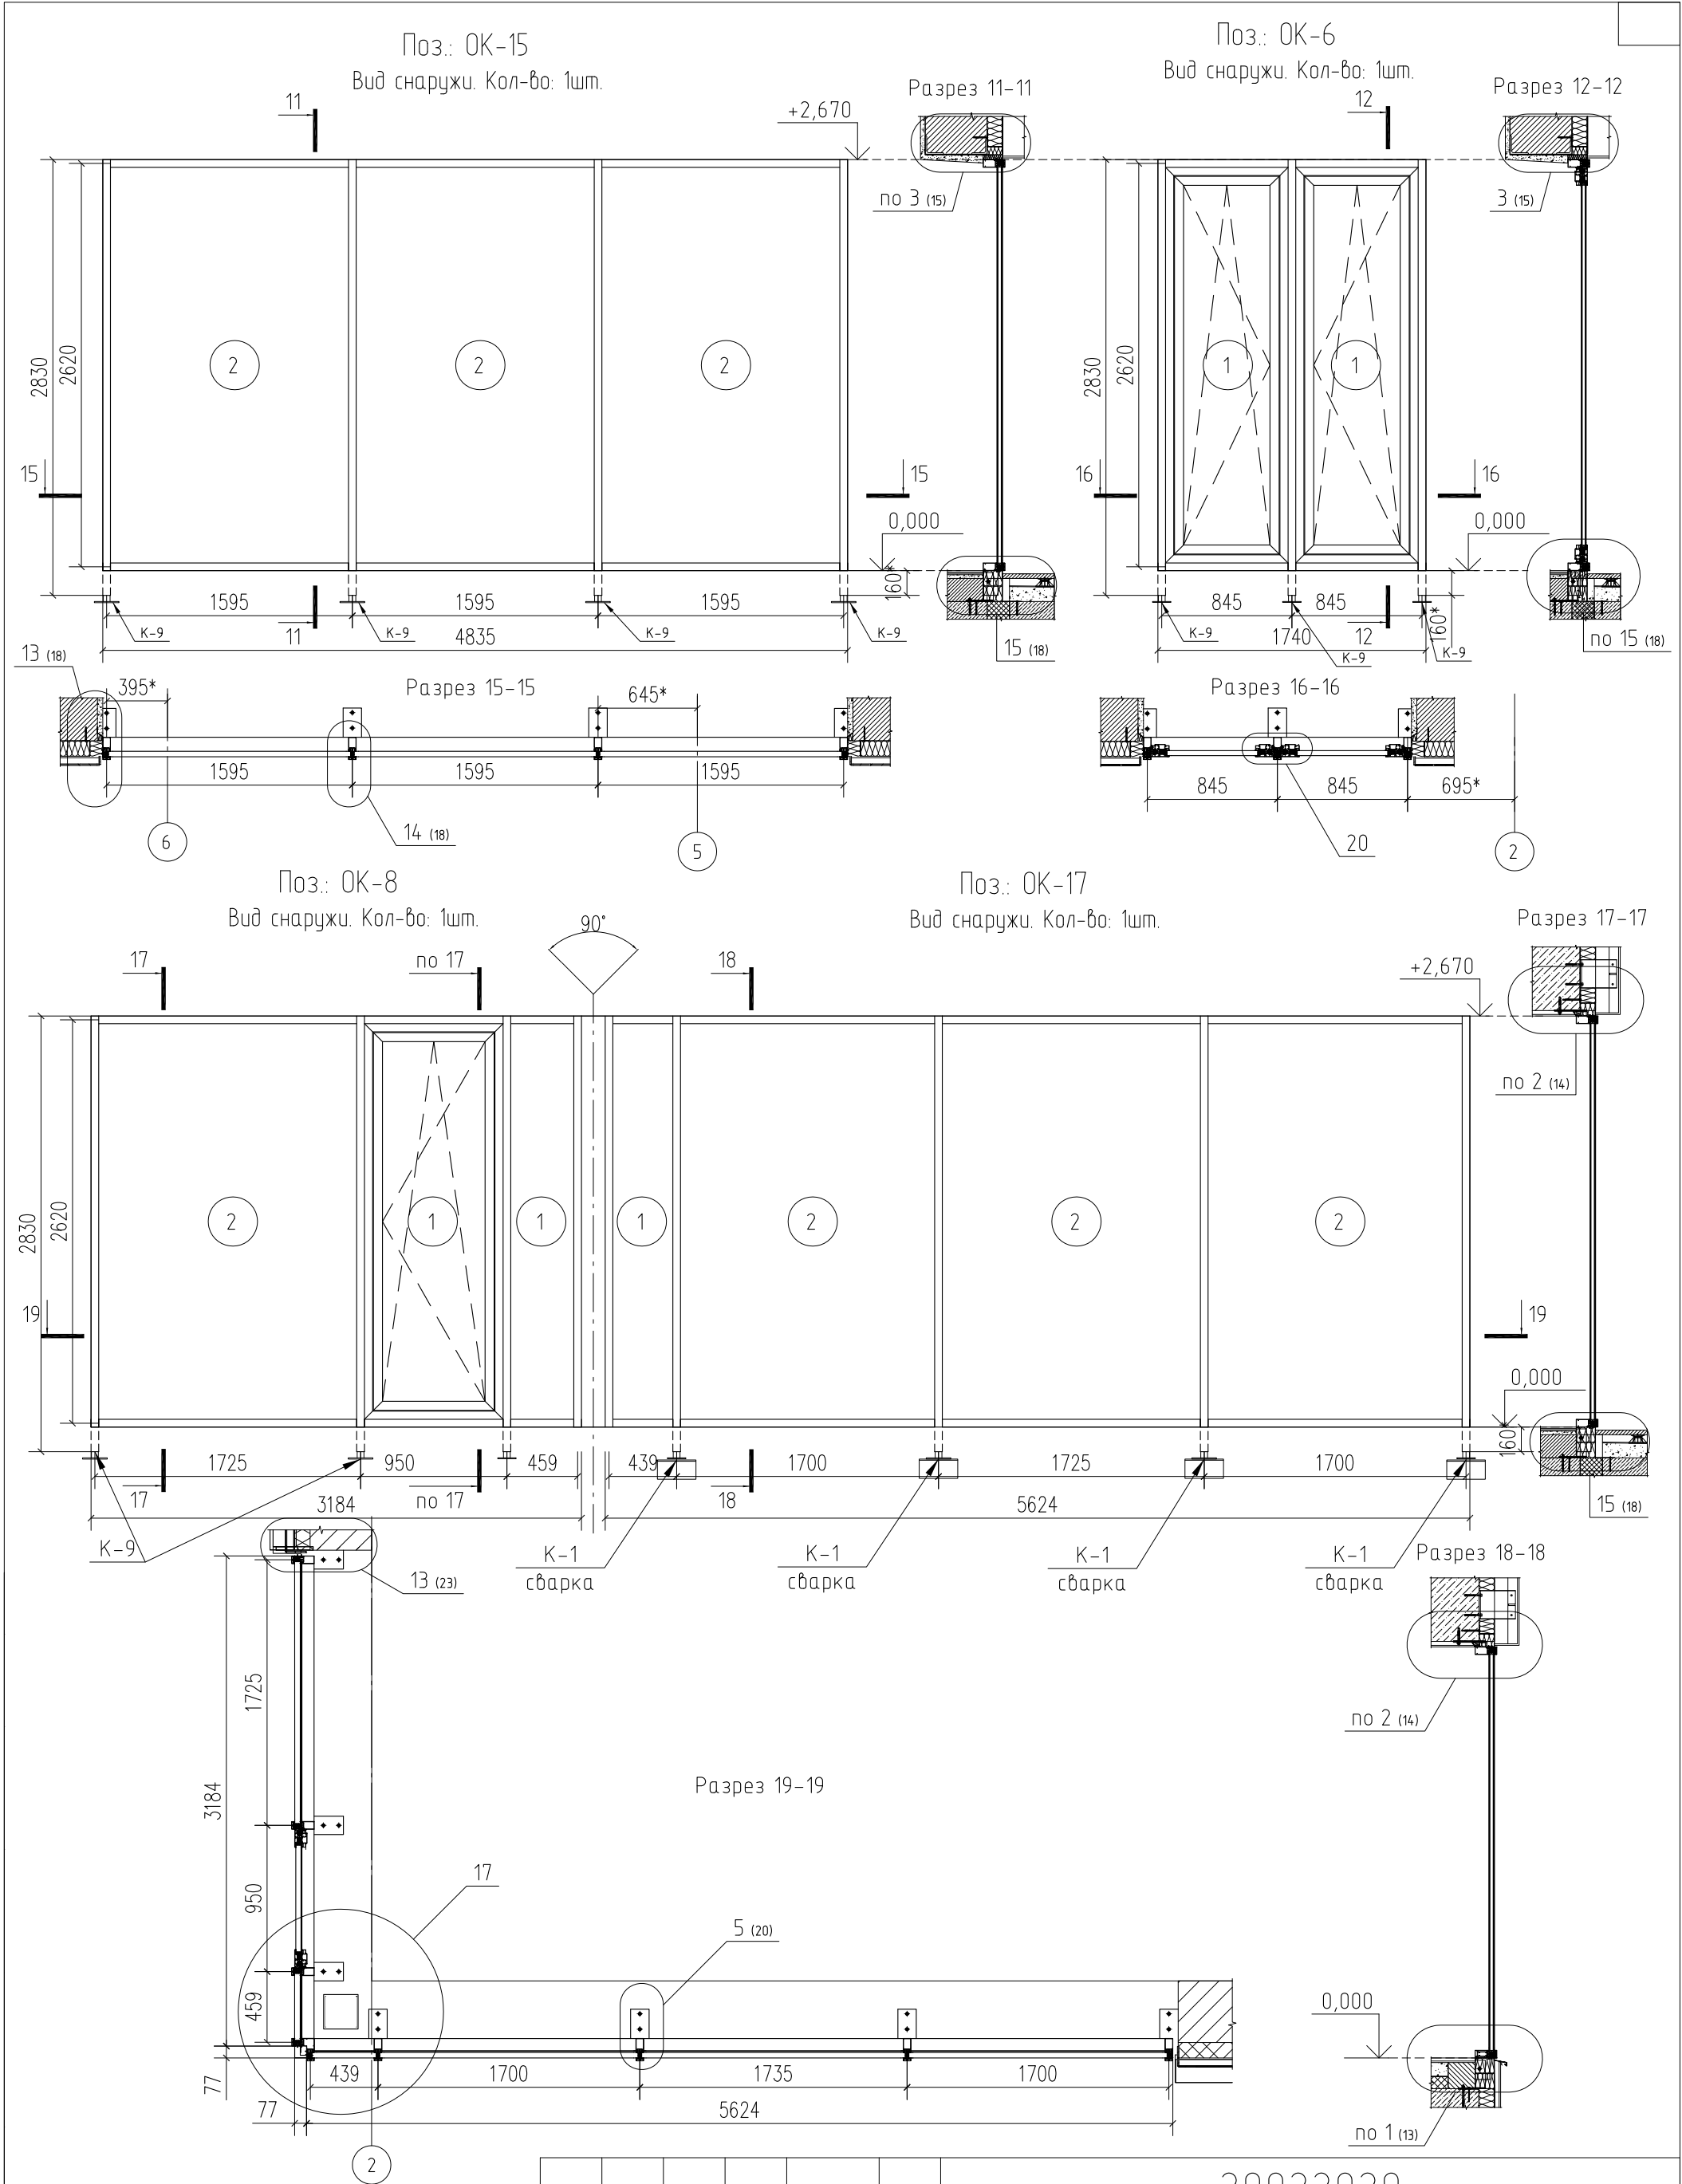

Примечания:

- ① - стеклопакет однокамерный 32мм.: 6M1-20Ag-6TopN
- ② - стеклопакет однокамерный 36мм.: 8M1-22Ag-6TopN

						20022020			
						Московская обл., Одинцовский р-н, д. Жуковка, ДП "Жуковка-2"			
Изм.	Кол. уч.	Лист	№ док.	Подп.	Дата	Светопрозрачные алюминиевые конструкции	Стадия	Лист	Листов
Разраб.		Ланцева Н.А.			20.02.2020		Р	8	25
Провер.		Кириянов А.М.				ОК-15, ОК-6, ОК-8, ОК-17. Разрез 11-11, 12-12, 15-15, 16-16, 17-17, 18-18, 19-19.	ООО "Гармония"		
Утвердил		Коноплич С.В.							
ГИП									

Вид снаружи. Кол-во: 1шт.

Вид снаружи. Кол-во: 1шт.

Вид снаружи. Кол-во: 1шт.


Разрез 21-21

по 18 (19) /

Разрез 23-23

② - стеклопакет однокамерный 36мм.: 8М1-22Аг-6ТорN


						20022020				
						Московская обл., Одинцовский р-н, д.Жуковка, ДП "Жуковка-2"				
Изм.	Кол.уч.	Лист	№ док.	Подп.	Дата					
						Светопрозрачные алюминиевые конструкции		Стадия	Лист	Листов
Разраб.		Ланцева Н.А.						Р	9	25
Провер.		Кирьянов А.М.				ОК-20, ОК-12, ОК-18. Разрез 20-20, 21-21, 22-22, 23-23.		ООО "Гармония"		
Утвердил		Коноплич С.В.								
ГИП										

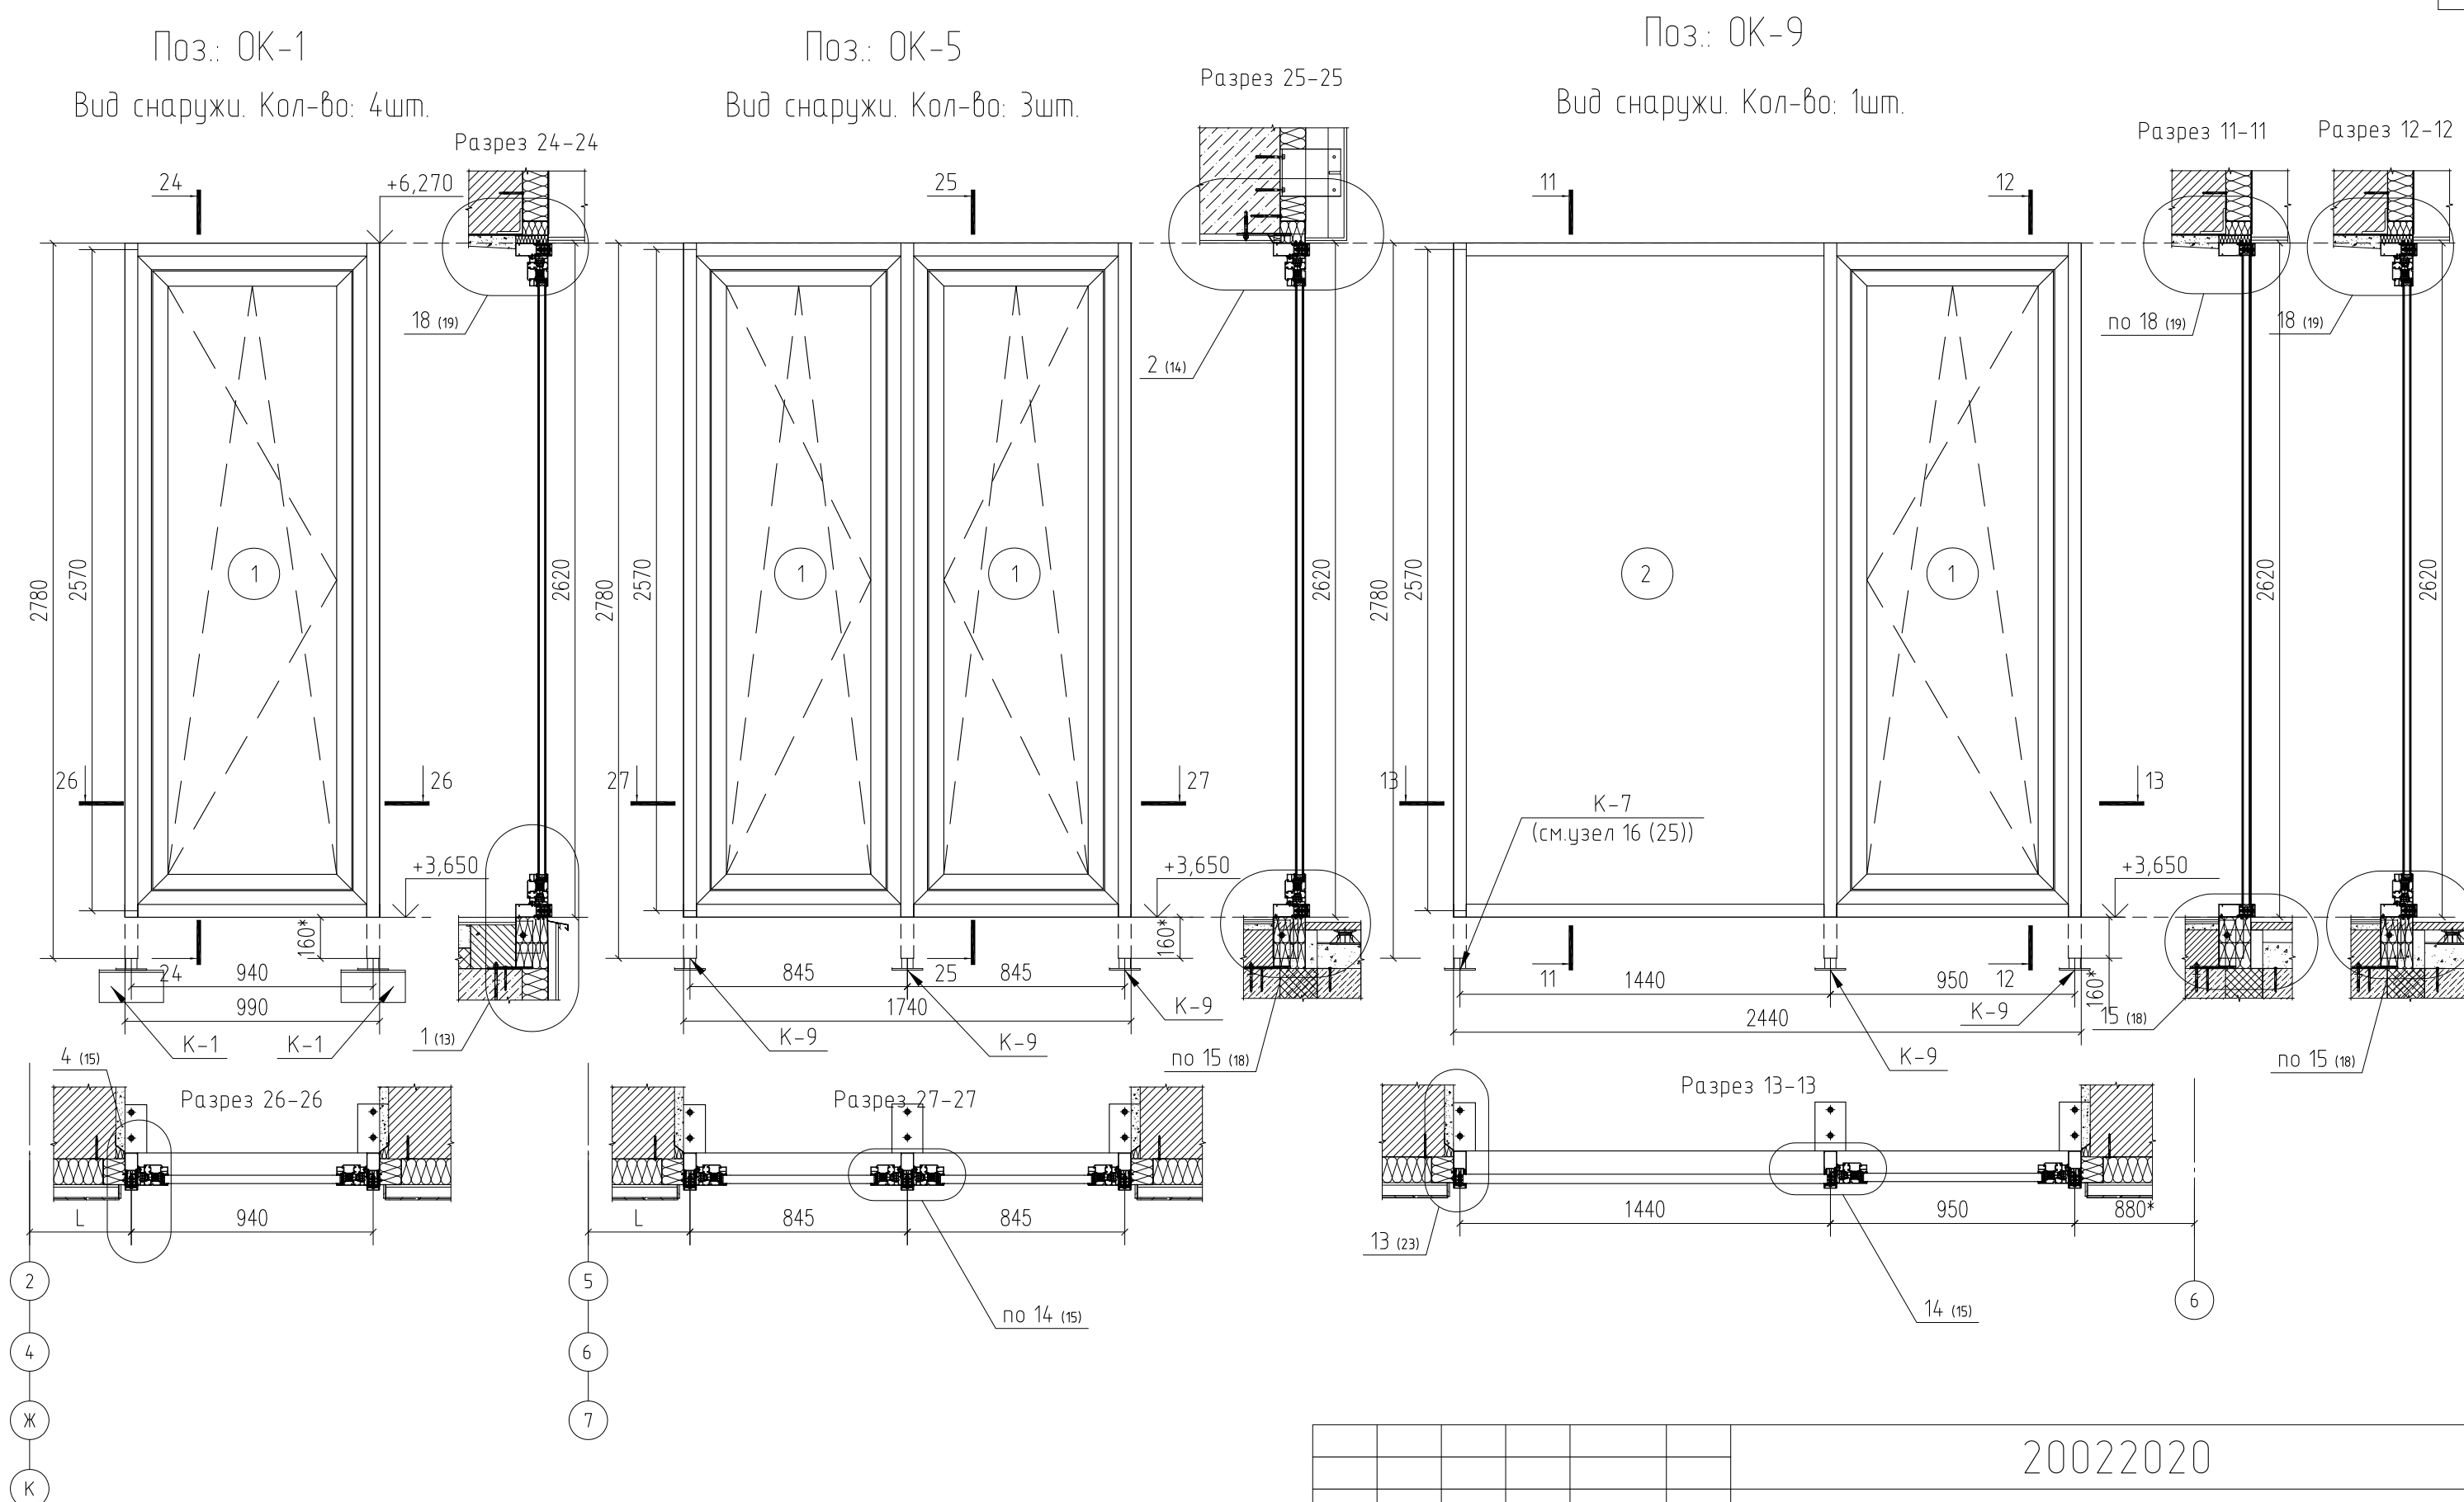

Примечания:

- 1 - стеклопакет однокамерный 32мм.: 6M1-20Ag-6TopN
- 2 - стеклопакет однокамерный 36мм.: 8M1-22Ag-6TopN

						20022020			
						Московская обл., Одинцовский р-н, д.Жуковка, ДП "Жуковка-2"			
Изм.	Кол.уч.	Лист	№ док.	Подп.	Дата	Светопрозрачные алюминиевые конструкции	Стадия	Лист	Листов
Разраб.		Ланцева Н.А.					Р	10	25
Провер.		Кирьянов А.М.							
Утвердил		Коноплич С.В.				ОК-1, ОК-5, ОК-9. Разрез 11-11, 12-12, 24-24, 25-25, 26-26, 27-27.			
ГИП									
						ООО "Гармония"			

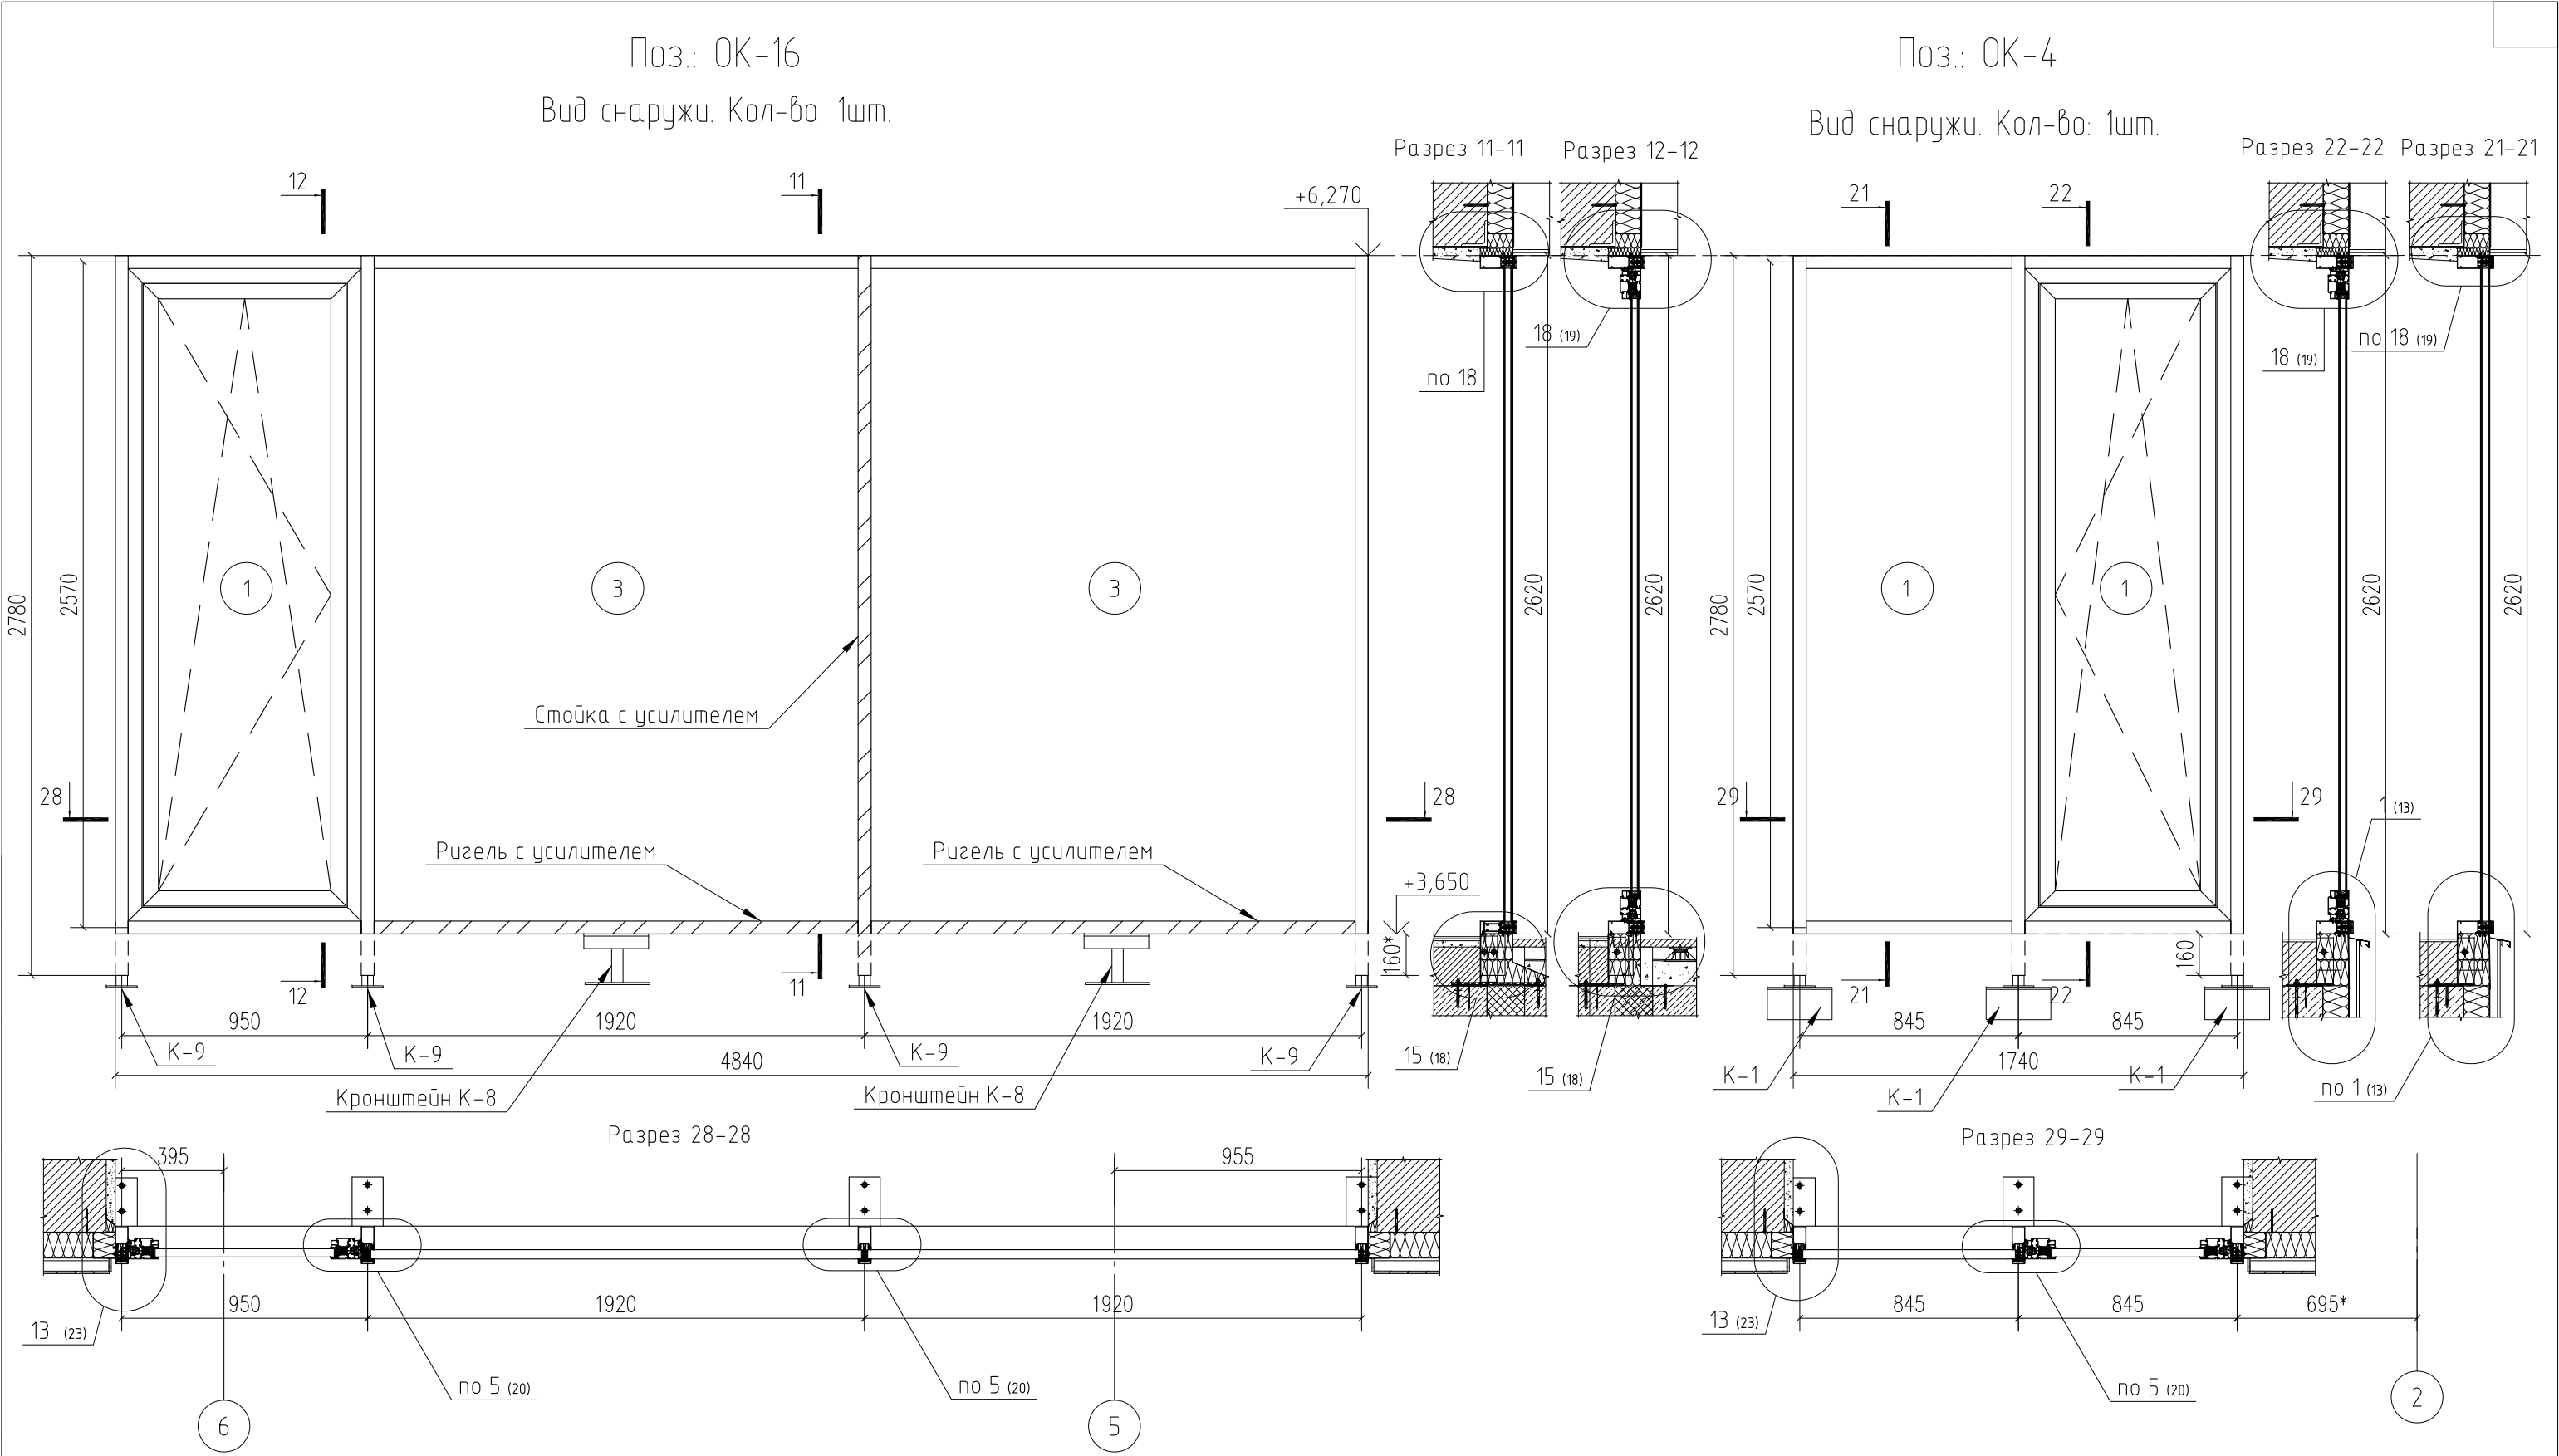


Примечания:

- 1 - стеклопакет однокамерный 32мм.: 6M1-20Ag-6TopN
- 3 - стеклопакет однокамерный 36мм.: 10зак.-16Ag-10зак.TopN

						20022020			
						Московская обл., Одинцовский р-н, д.Жуковка, ДП "Жуковка-2"			
Изм.	Кол.уч.	Лист	№ док.	Подп.	Дата	Светопрозрачные алюминиевые конструкции	Стадия	Лист	Листов
Разраб.		Ланцева Н.А.					Р	11	25
Провер.		Кириянов А.М.							
Утвердил		Коноплич С.В.				ОК-16, ОК-4. Разрез 11-11, 12-12, 21-21, 22-22, 28-28, 29-29.			
ГИП									
						ООО "Гармония"			



Узел 1

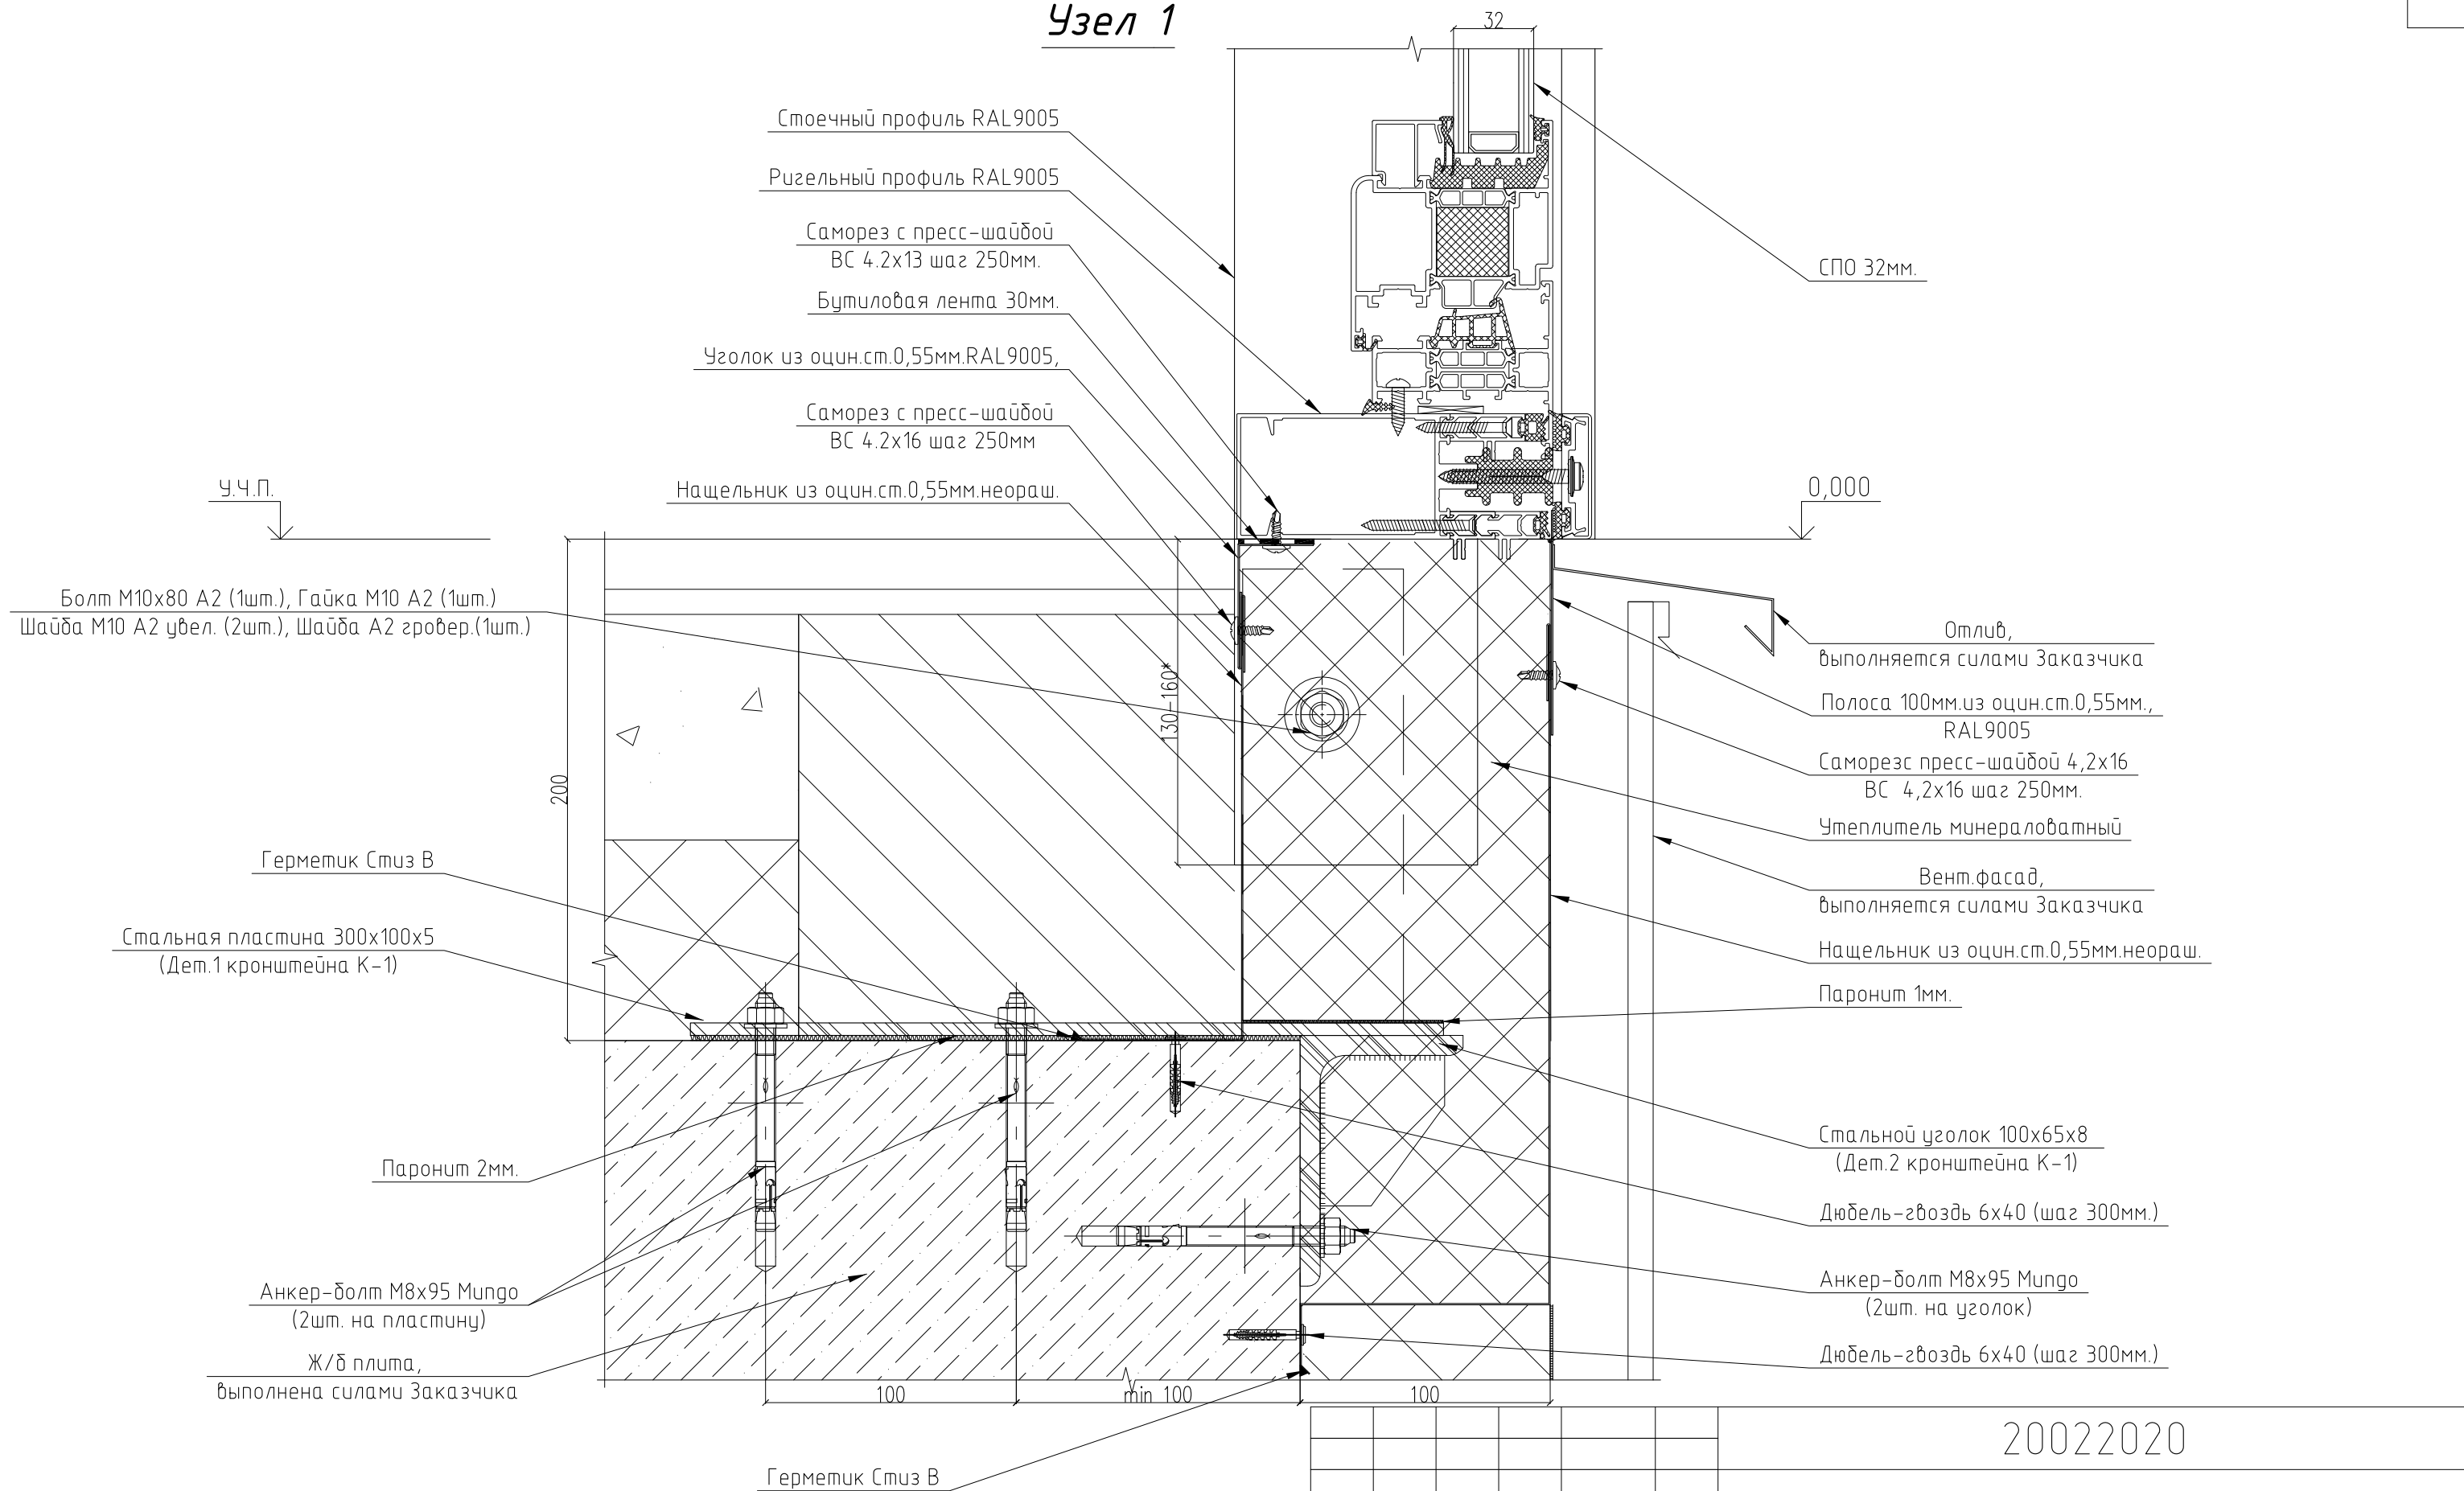

						20022020			
						Московская обл., Одинцовский р-н, д.Жуковка, ДП "Жуковка-2"			
Изм.	Кол.уч.	Лист	№ док.	Подп.	Дата	Светопрозрачные алюминиевые конструкции	Стадия	Лист	Листов
Разраб.		Ланцева Н.А.					Р	13	25
Провер.		Кирьянов А.М.							
Утвердил		Коноплич С.В.				Узел 1	ООО "Гармония"		
ГИП									


Секция

Инв. № подл.	Подп. и дата	Взам. инв. №			

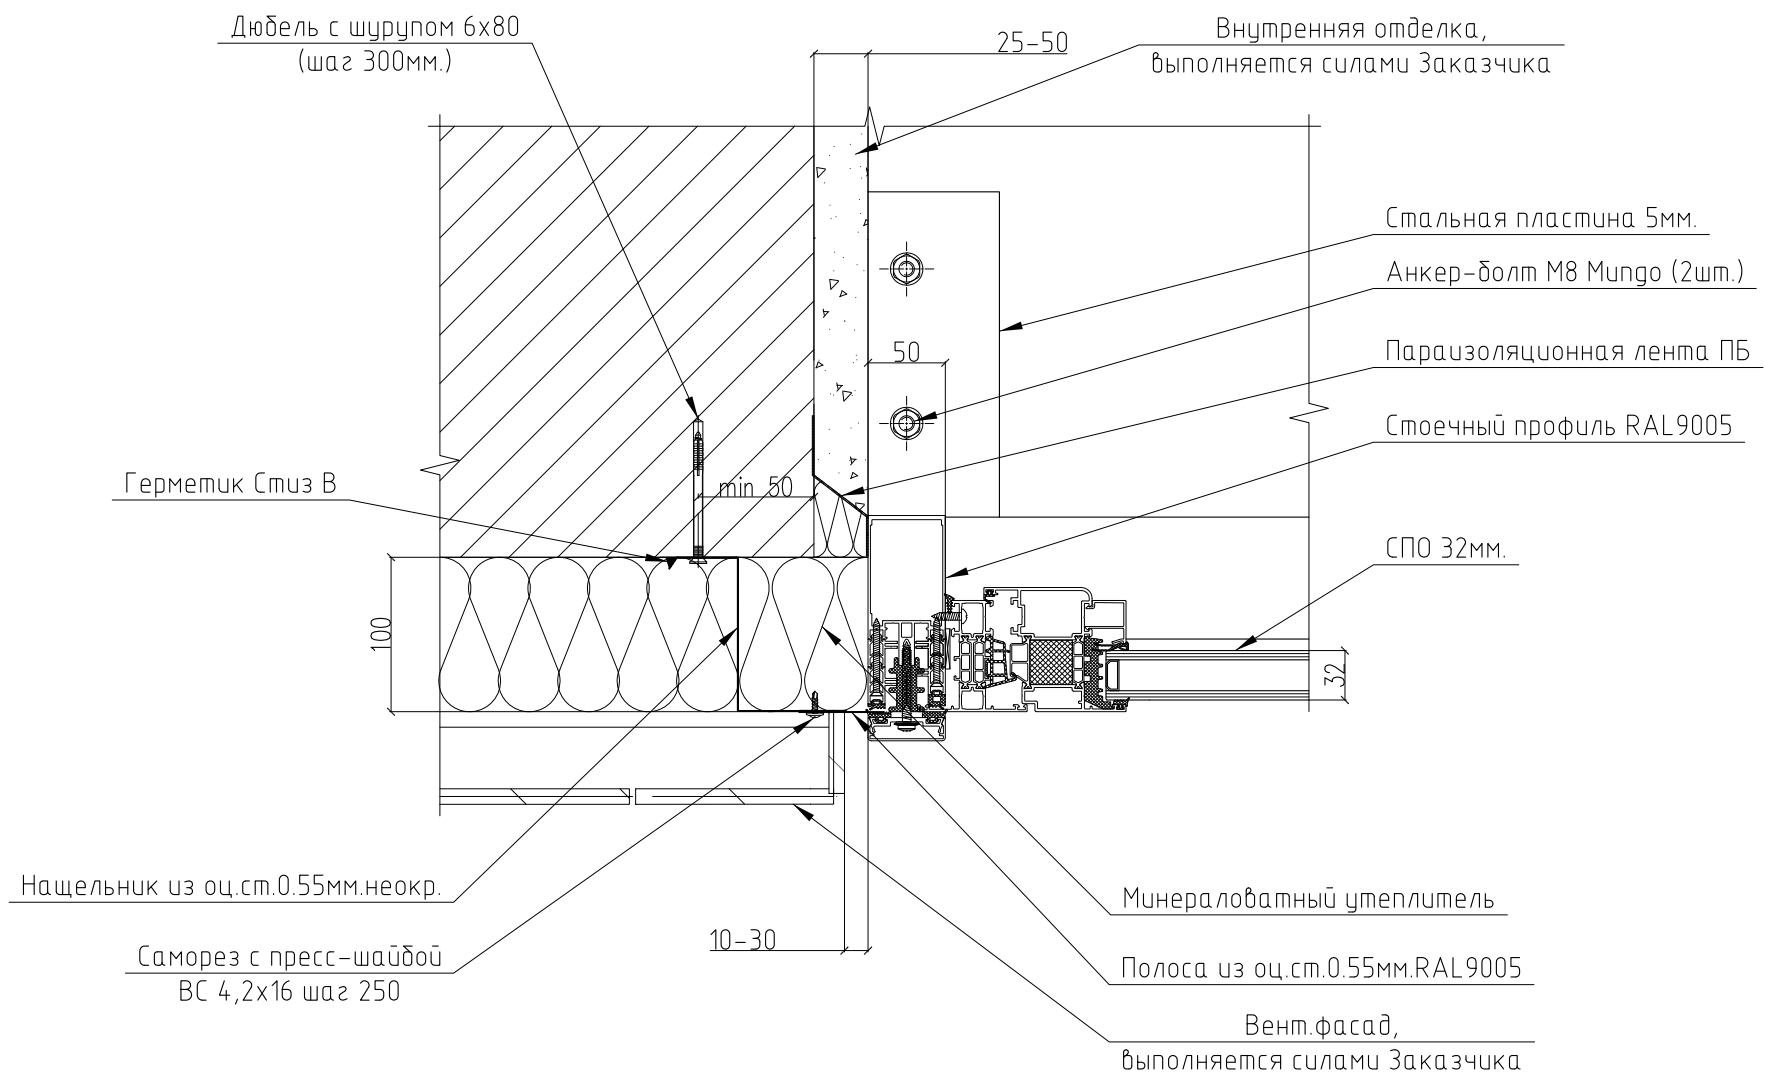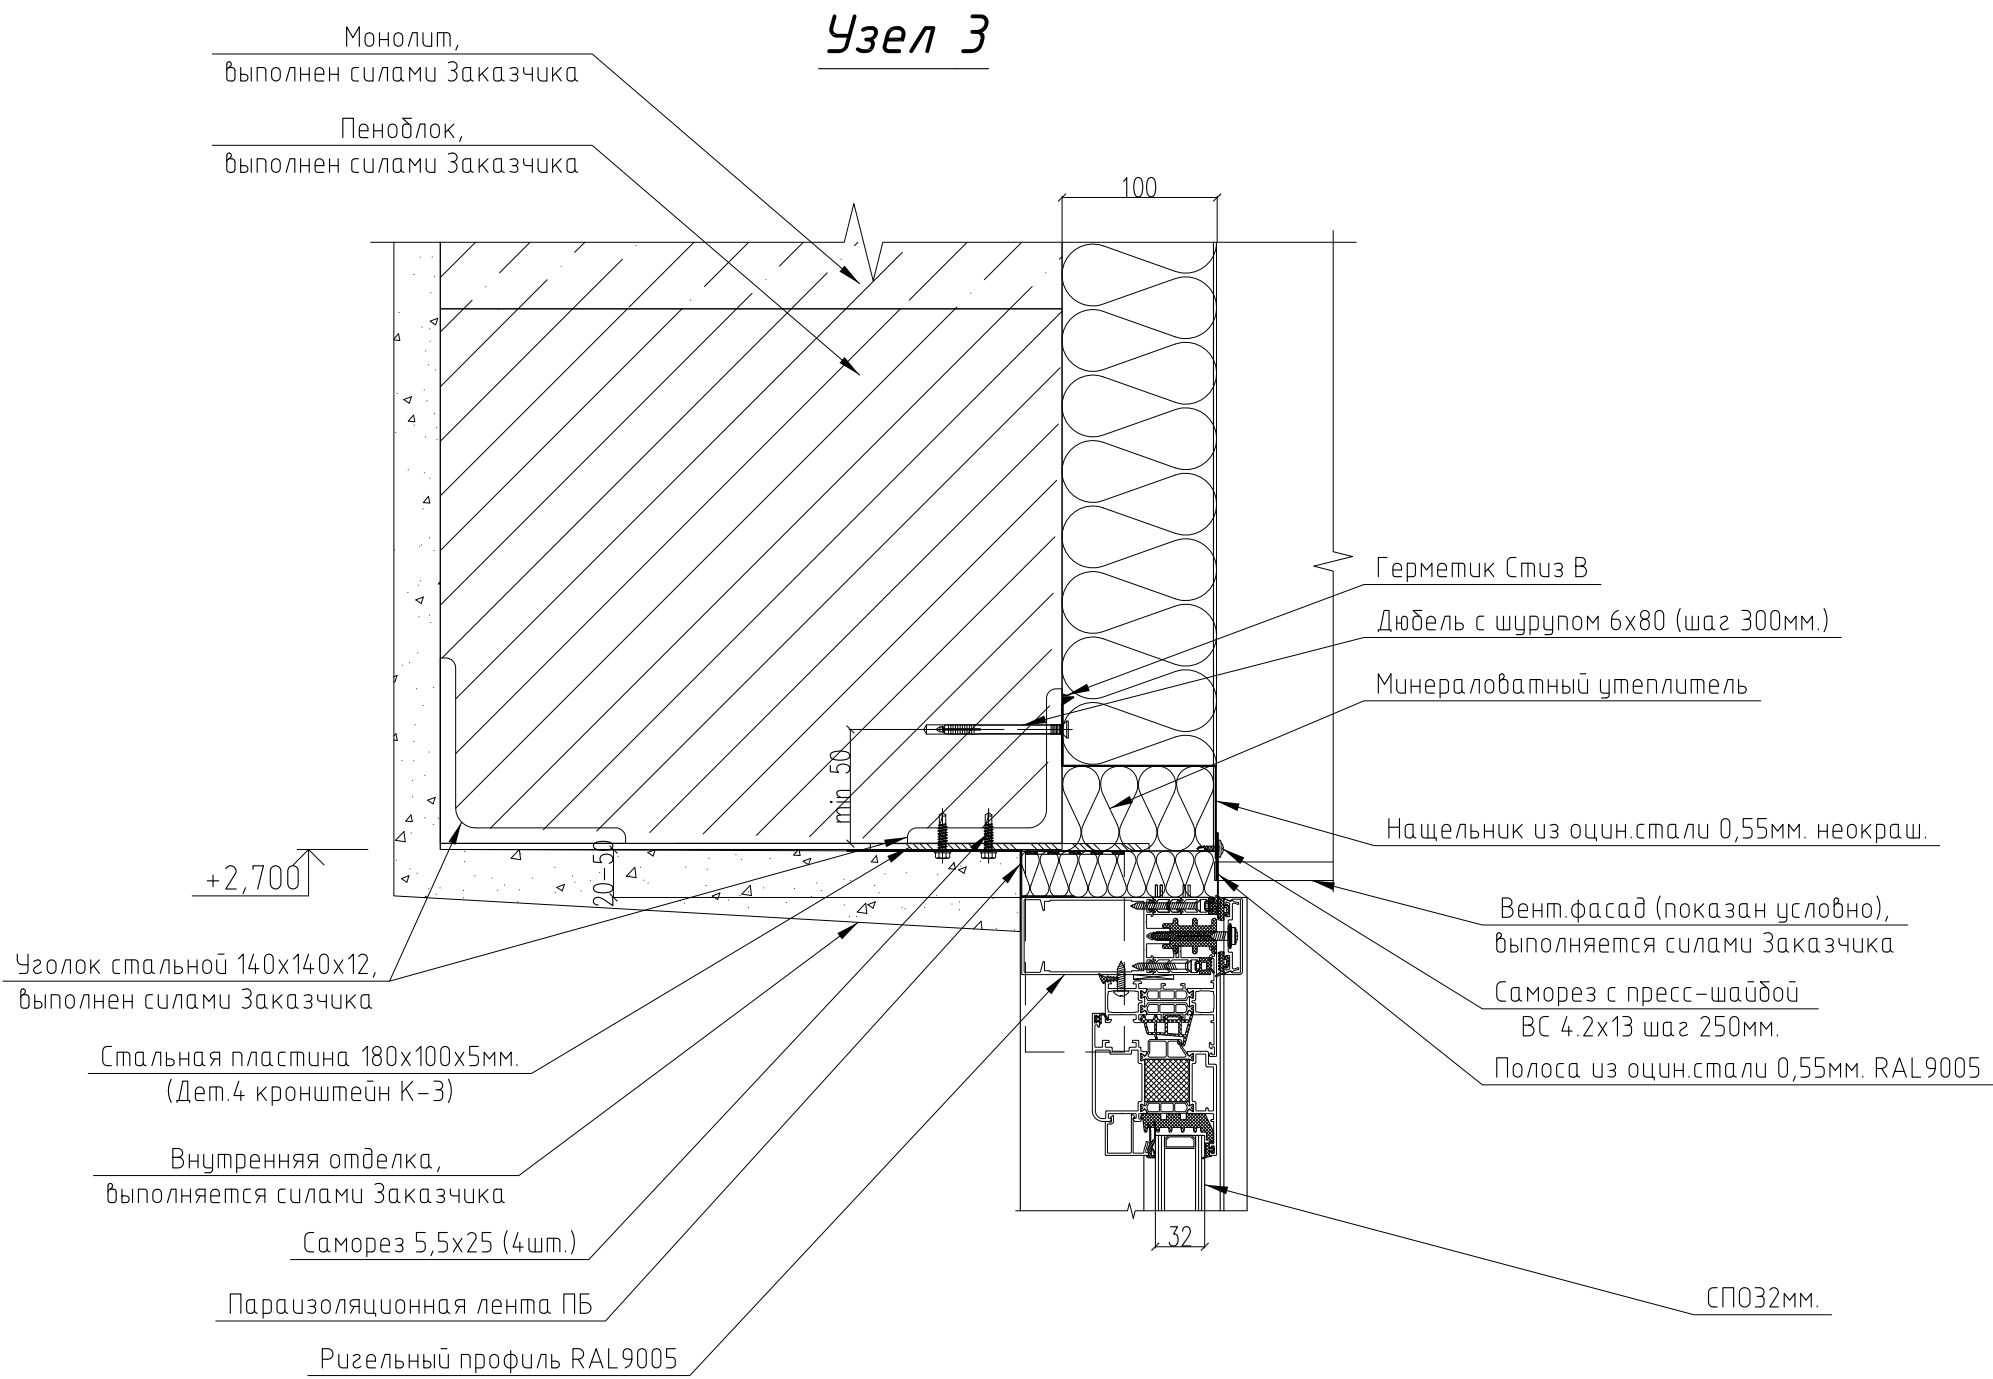


						17022020			
						Московская обл., Одинцовский р-н, д.Жуковка, ДП "Жуковка-2"			
Изм.	Кол.уч.	Лист	№ док.	Подп.	Дата	Светопрозрачные алюминиевые конструкции	Стадия	Лист	Листов
Разраб.		Ланцева Н.А.			20.02.202г.		Р	15	25
Провер.		Кирьянов А.М.							
Утвердил		Коноплич С.В.				Узлы 3,4	ООО "Гармония"		
ГИП									

Узел 10

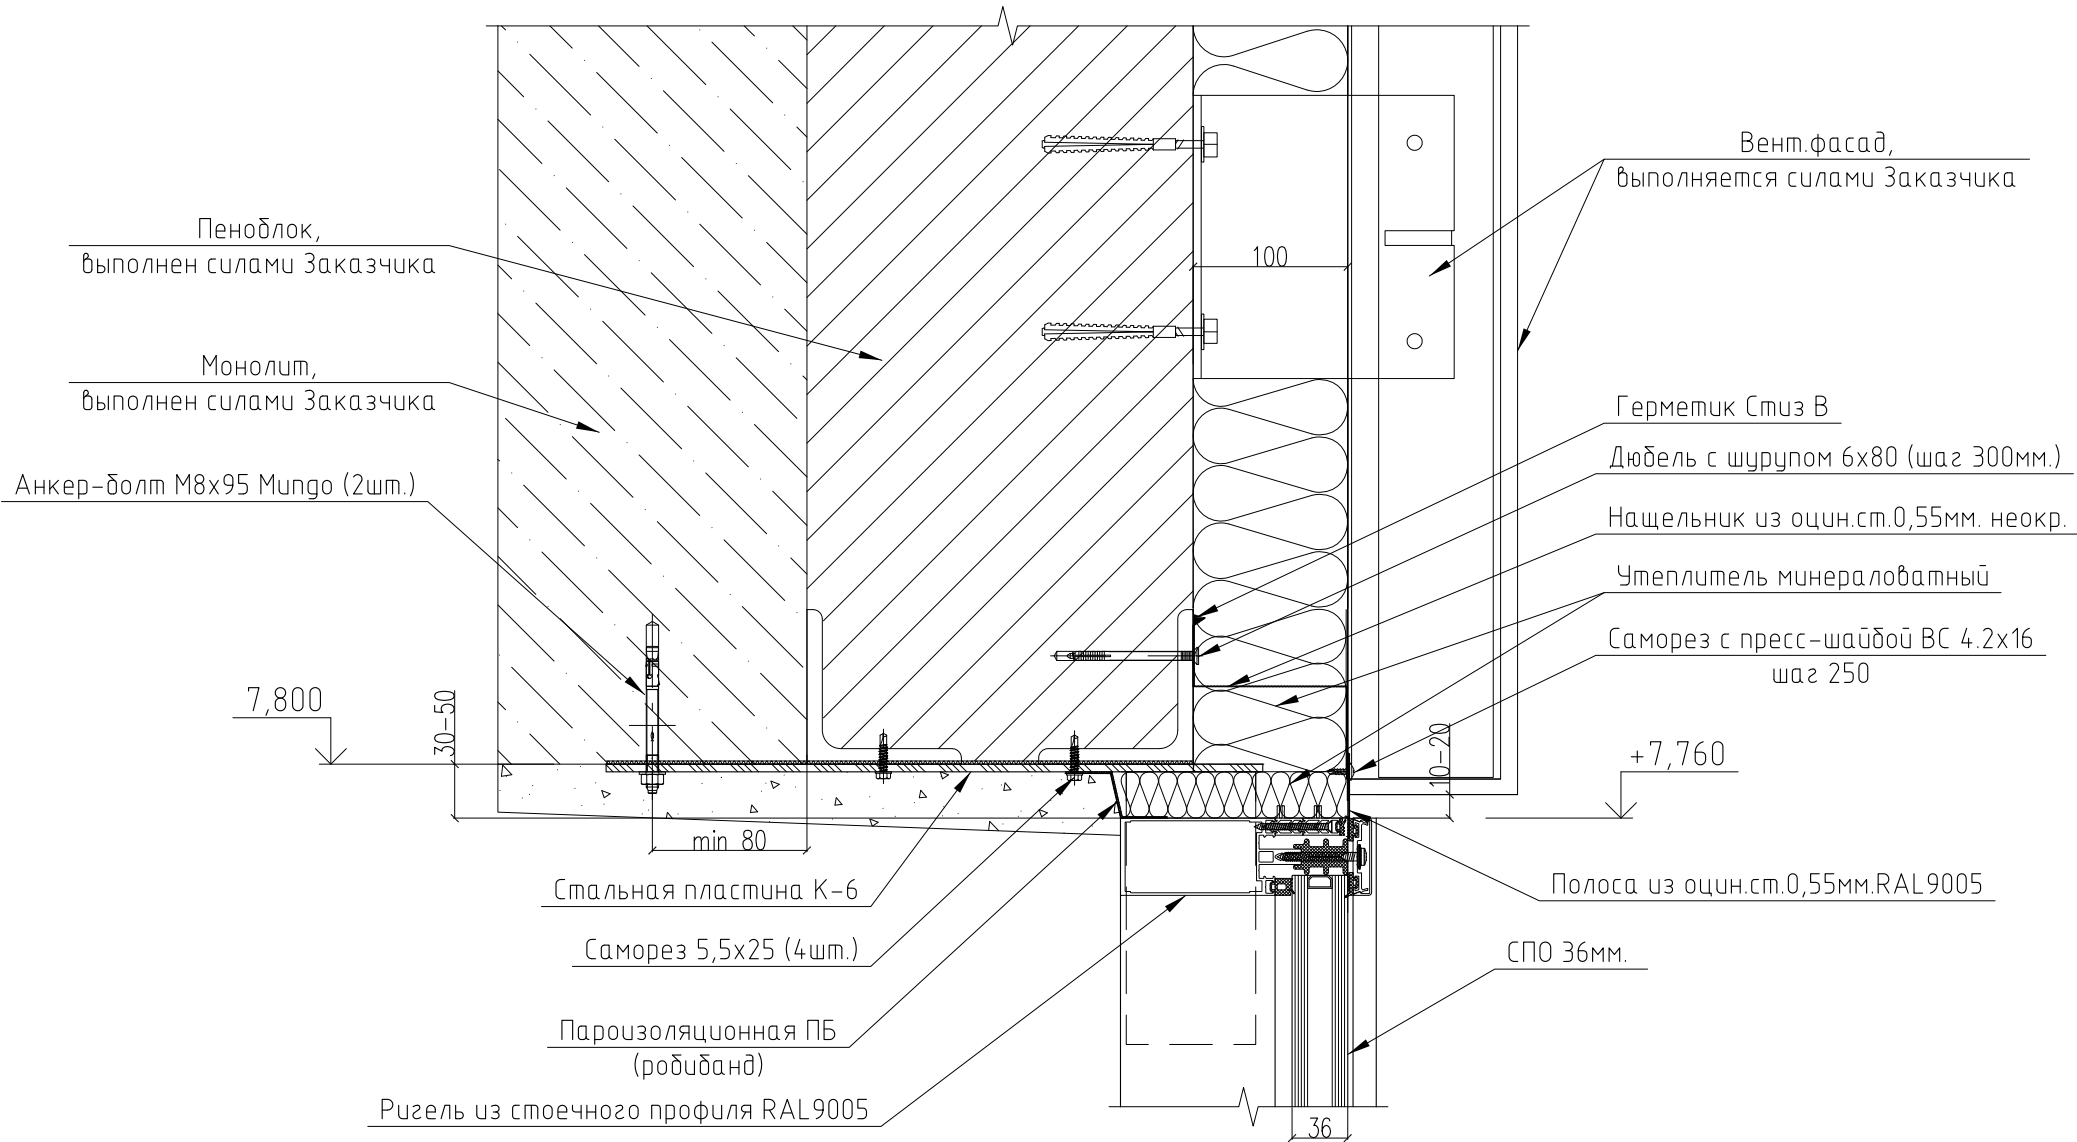


Узел 9

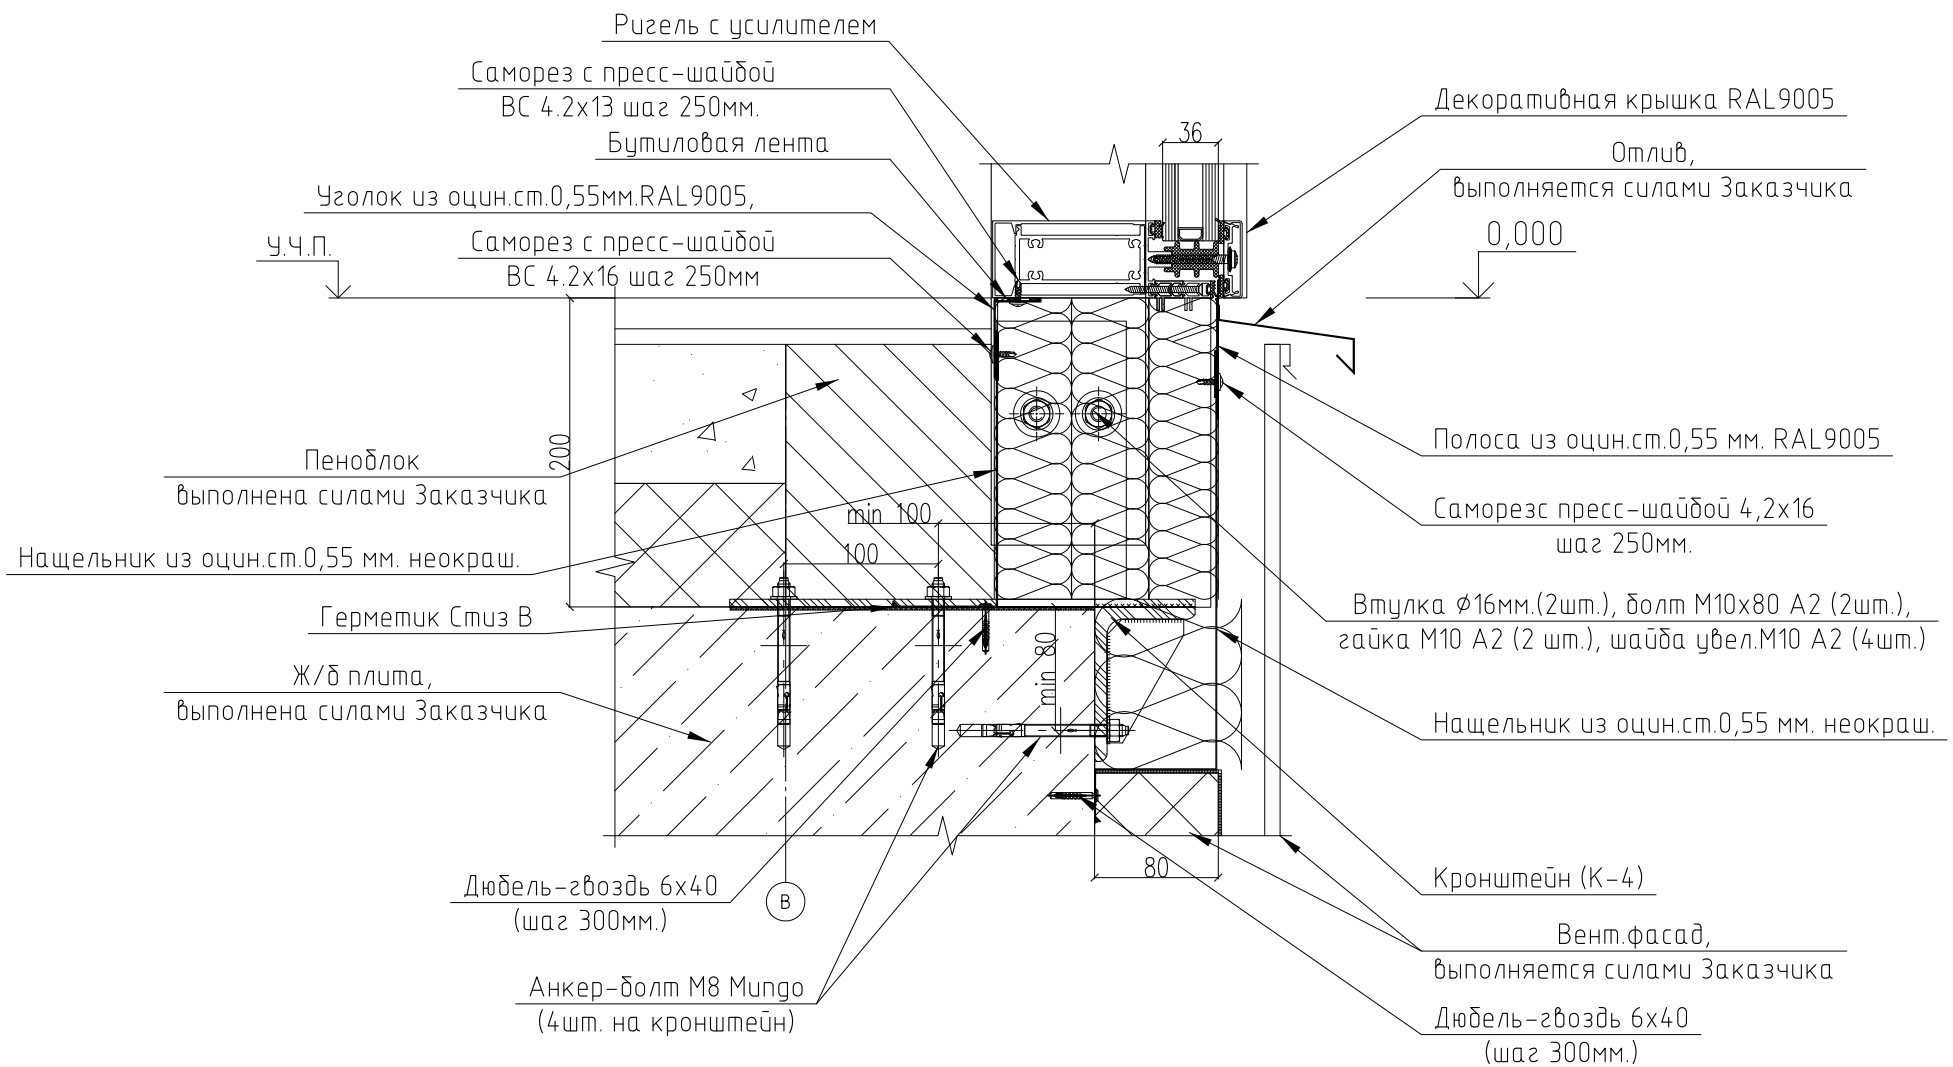


Инв. № подл.	Подп. и дата	Взам. инв. №			

						17022020			
						Московская обл., Одинцовский р-н, д.Жуковка, ДП "Жуковка-2"			
Изм.	Кол.уч.	Лист	№ док.	Подп.	Дата	Светопрозрачные алюминиевые конструкции	Стадия	Лист	Листов
Разраб.		Ланцева Н.А.			20.02.2020		Р	16	25
Провер.		Кирьянов А.М.							
Утвердил		Коноплич С.В.				Узлы 9, 10.	ООО "Гармония"		
ГИП									

Узел 12

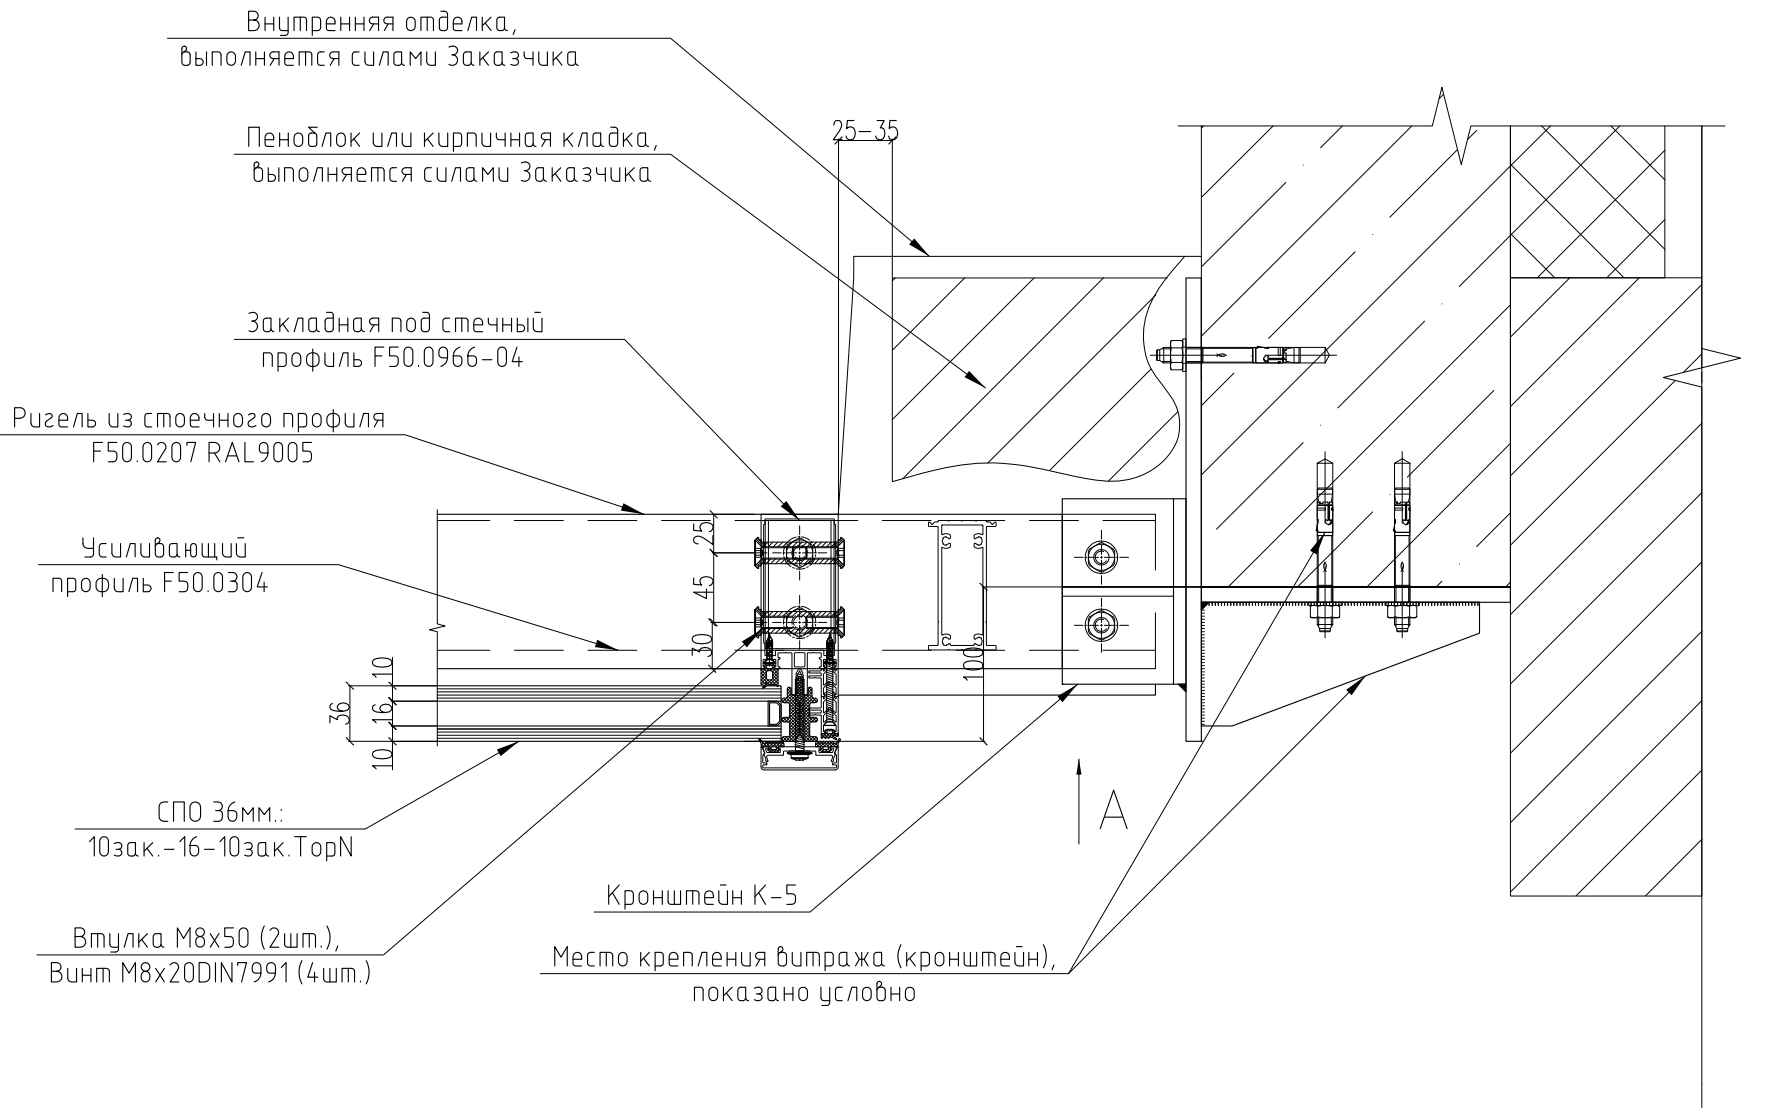


Вид А

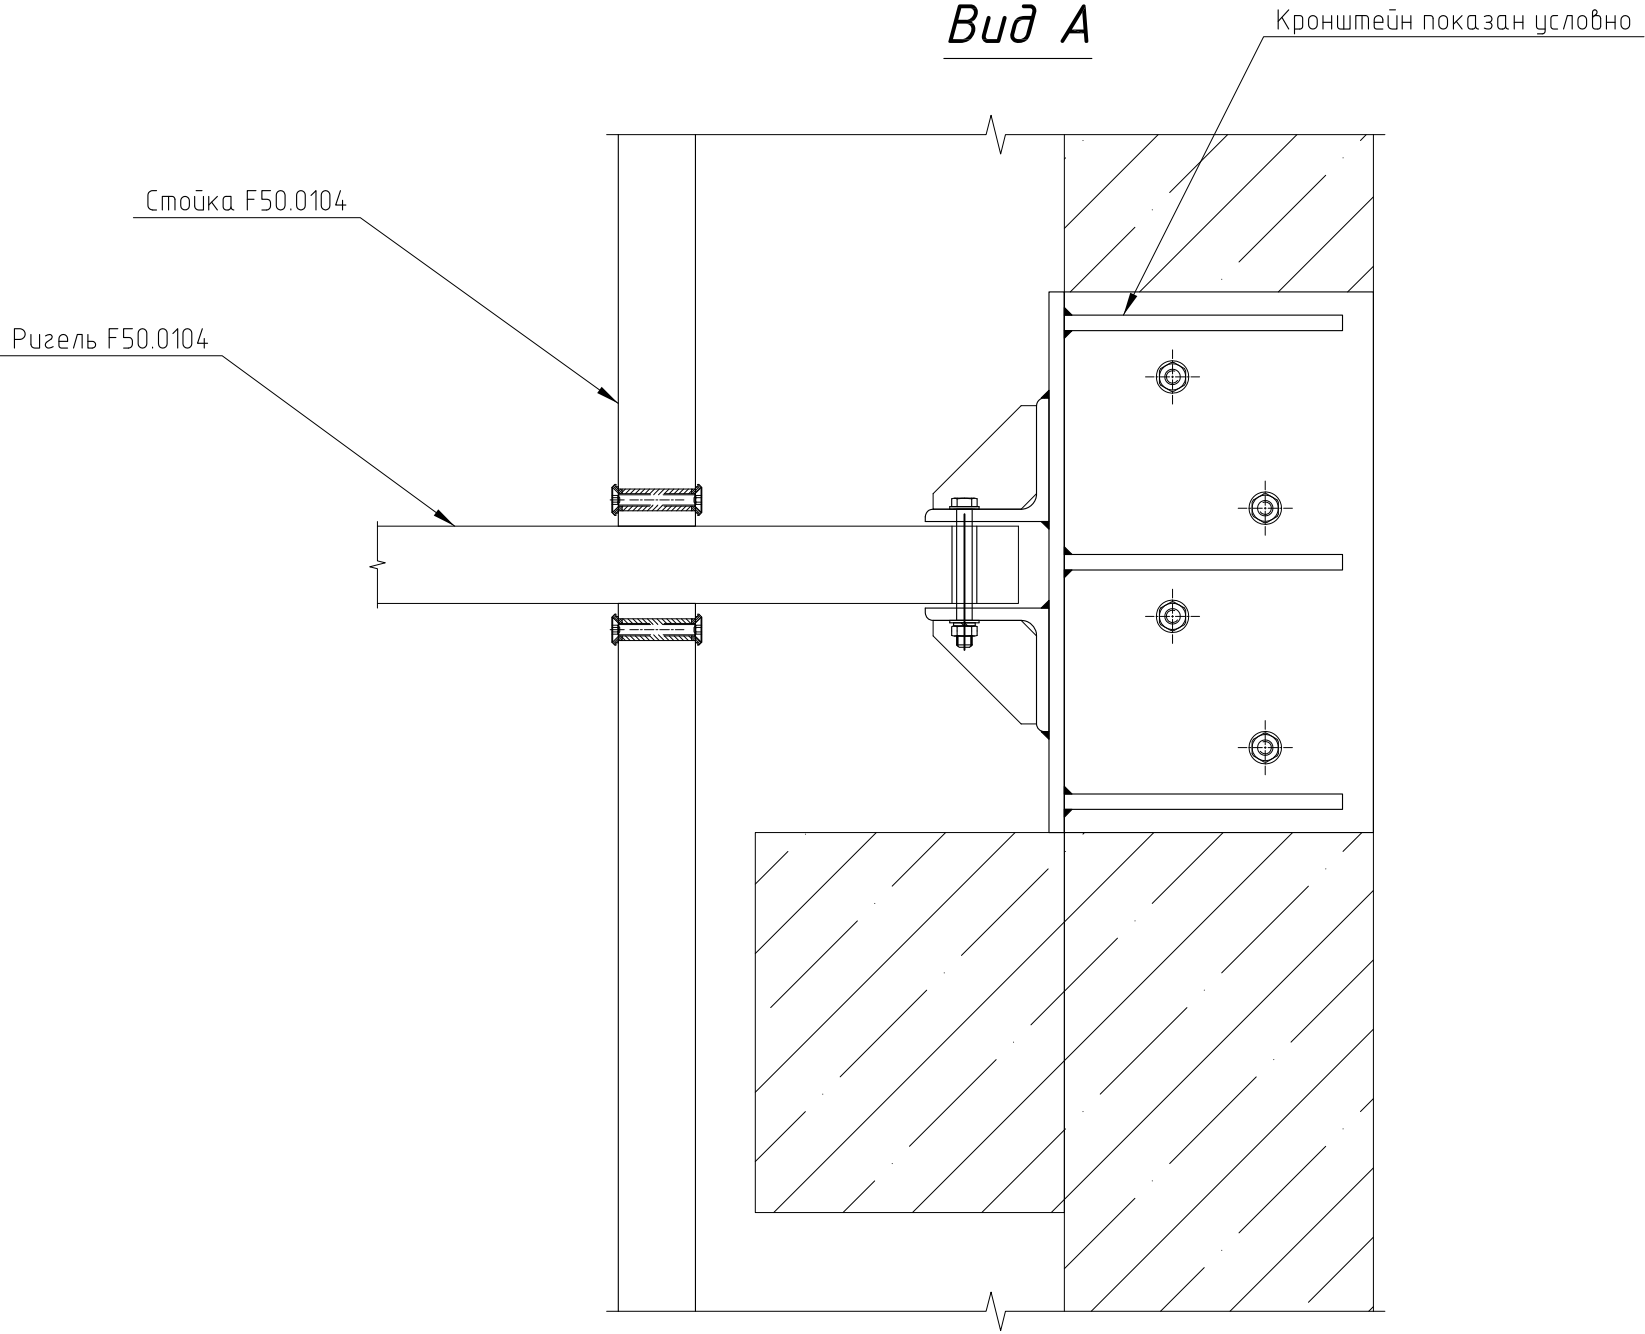


Инв. № подл.	Подп. и дата	Взам. инв. №			

						17022020			
						Московская обл., Одинцовский р-н, д. Жуковка, ДП "Жуковка-2"			
Изм.	Кол. уч.	Лист	№ док.	Подп.	Дата	Светопрзрачные алюминиевые конструкции	Стадия	Лист	Листов
Разраб.		Ланцева Н.А.			20.02.20г.		Р	17	25
Провер.		Кирьянов А.М.							
Утвердил		Коноплич С.В.				Узел 12	ООО "Гармония"		
ГИП									

Узел 12

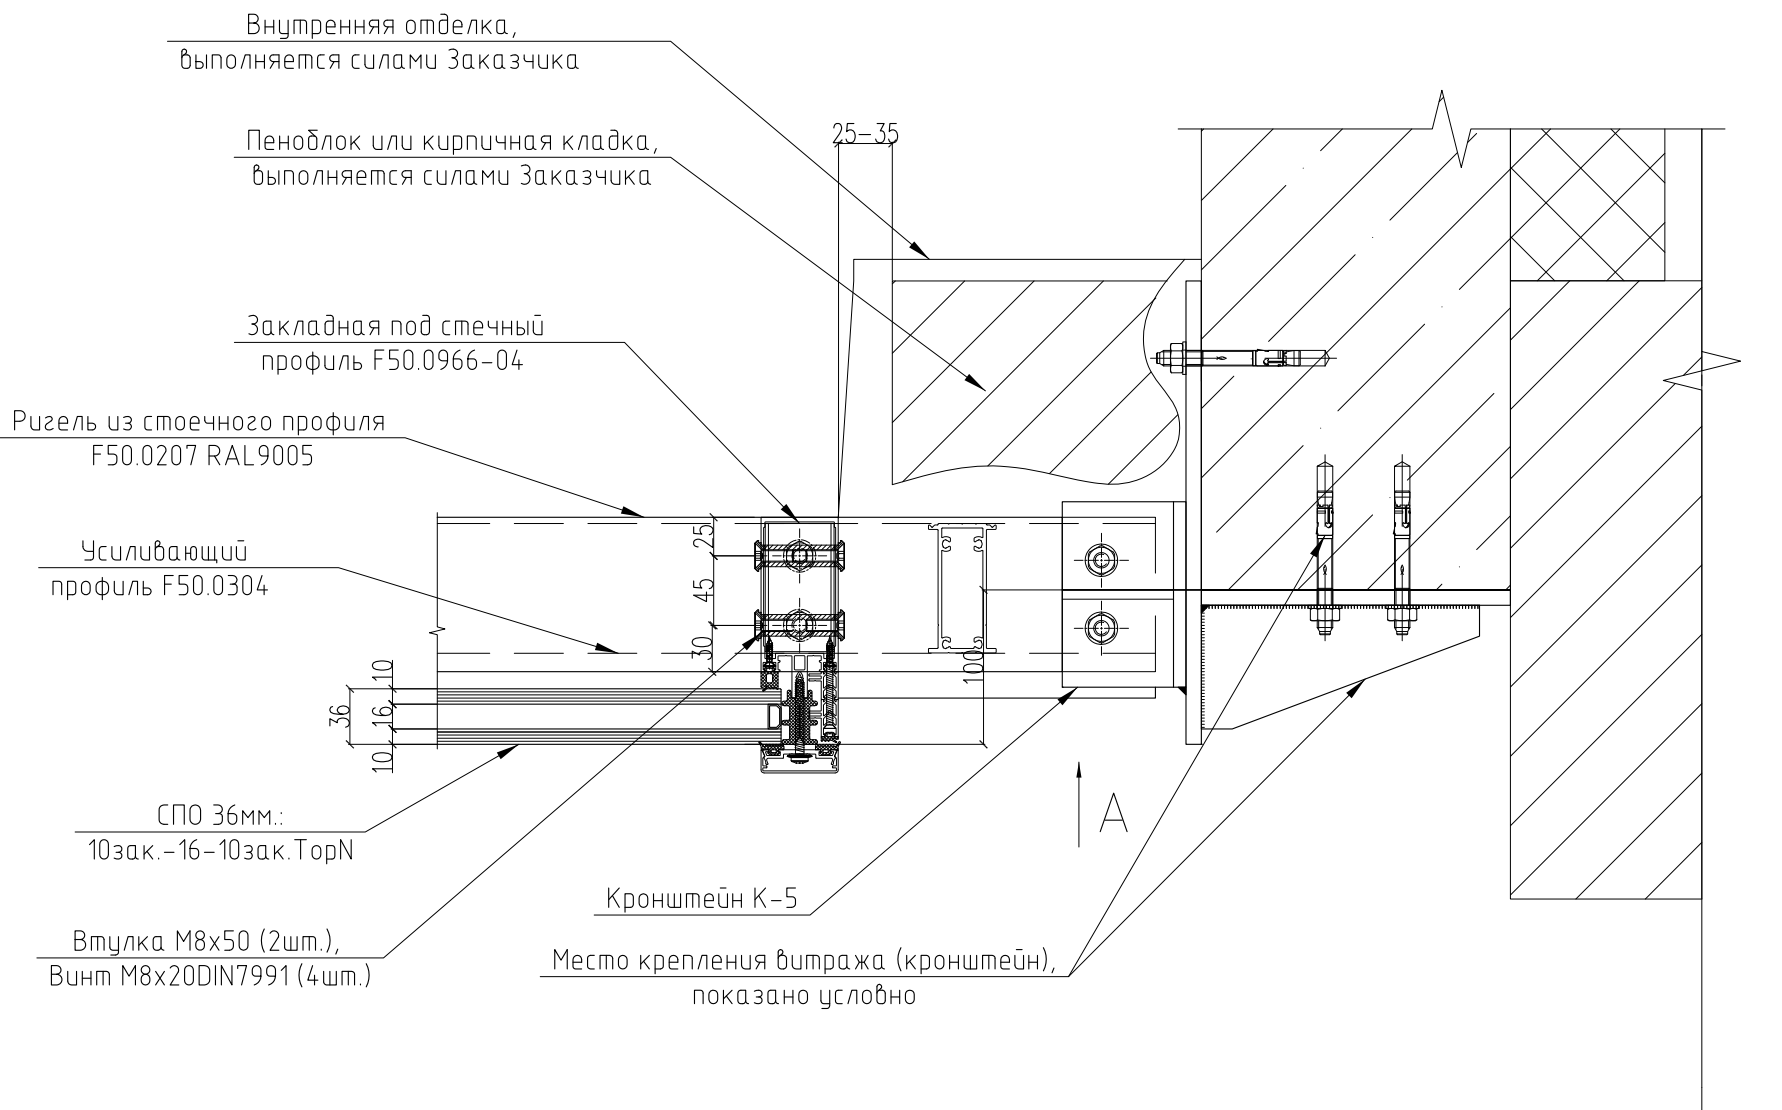


Вид А

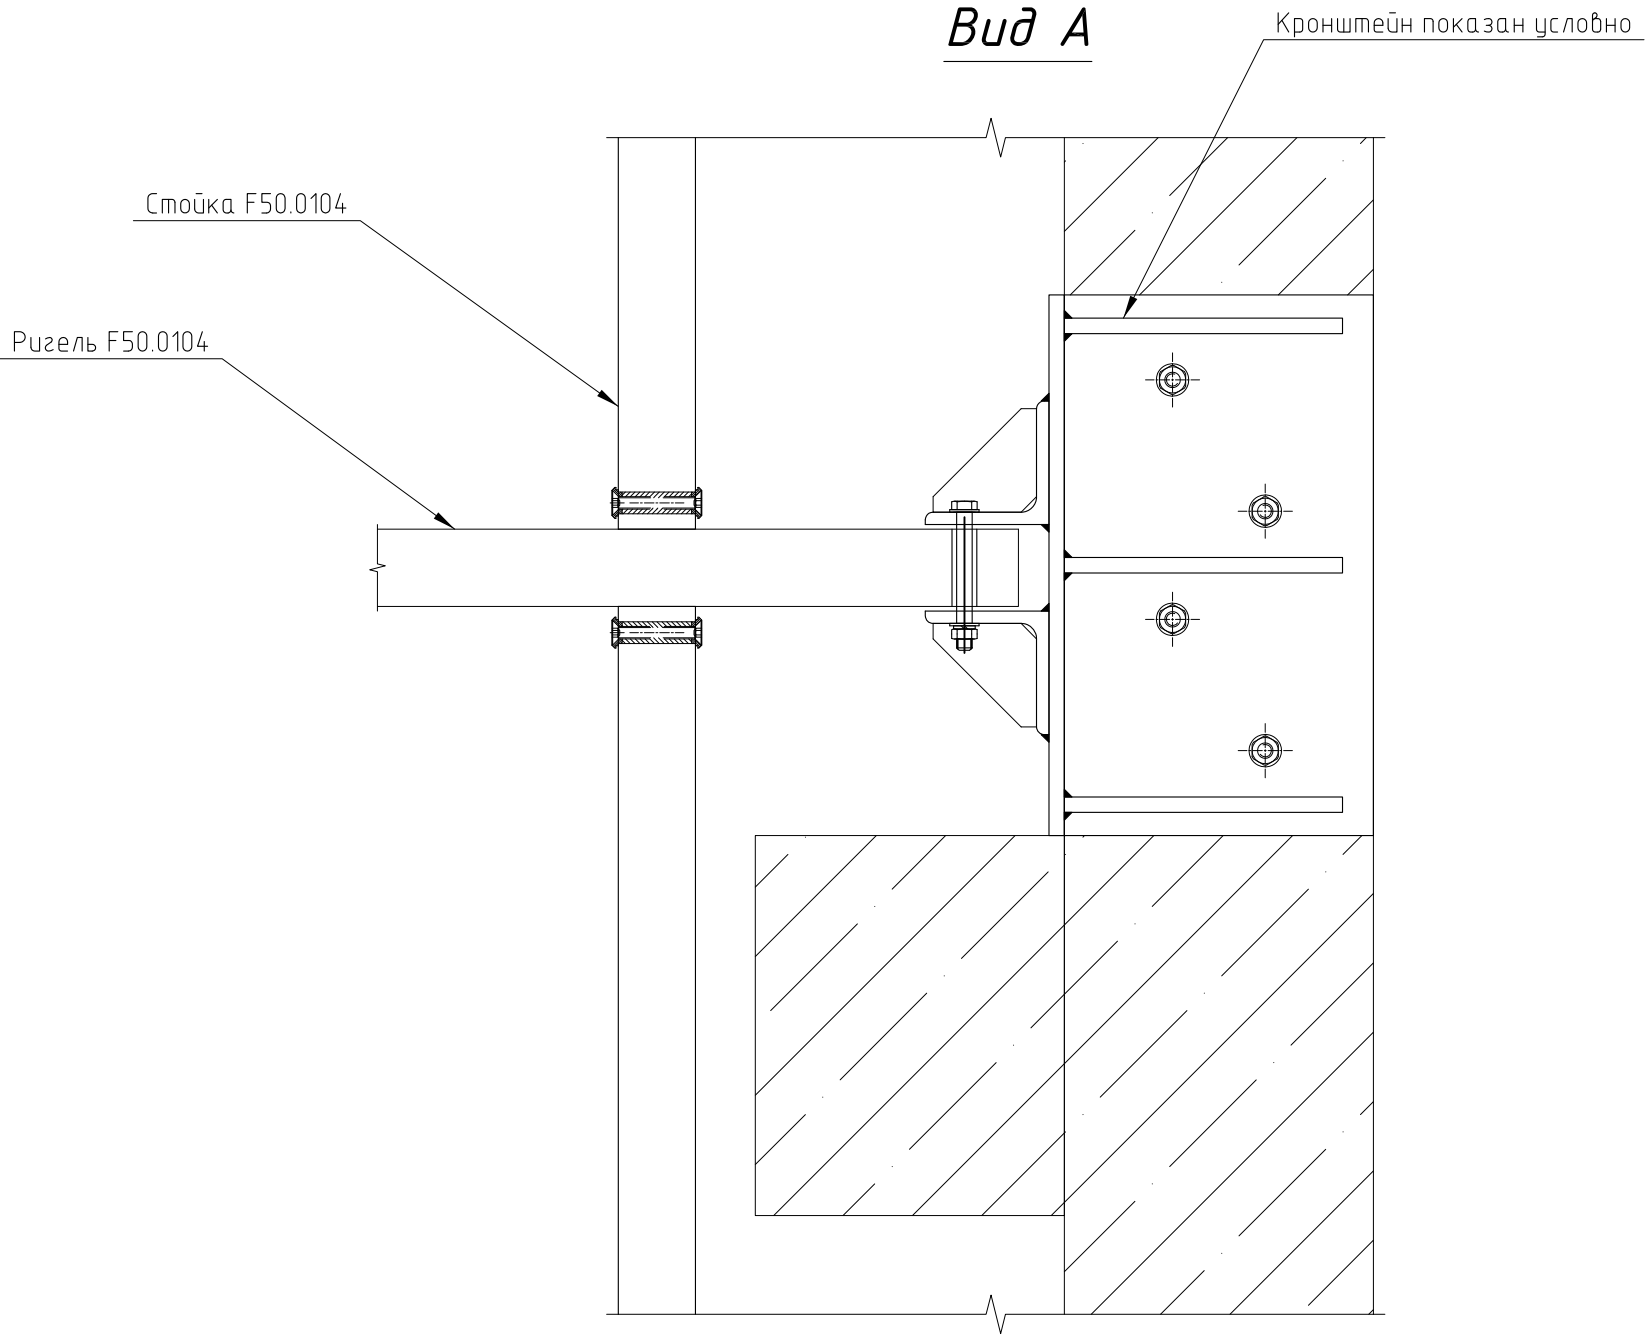

Инв. № подл.	Подп. и дата	Взам. инв. №			


						17022020			
						Московская обл., Одинцовский р-н, д. Жуковка, ДП "Жуковка-2"			
Изм.	Кол. уч.	Лист	№ док.	Подп.	Дата	Светопрозрачные алюминиевые конструкции	Стадия	Лист	Листов
Разраб.		Ланцева Н.А.			20.02.20г.		Р	17	25
Провер.		Кирьянов А.М.							
Утвердил		Коноплич С.В.							
ГИП						Узел 12		ООО "Гармония"	

Узел 15

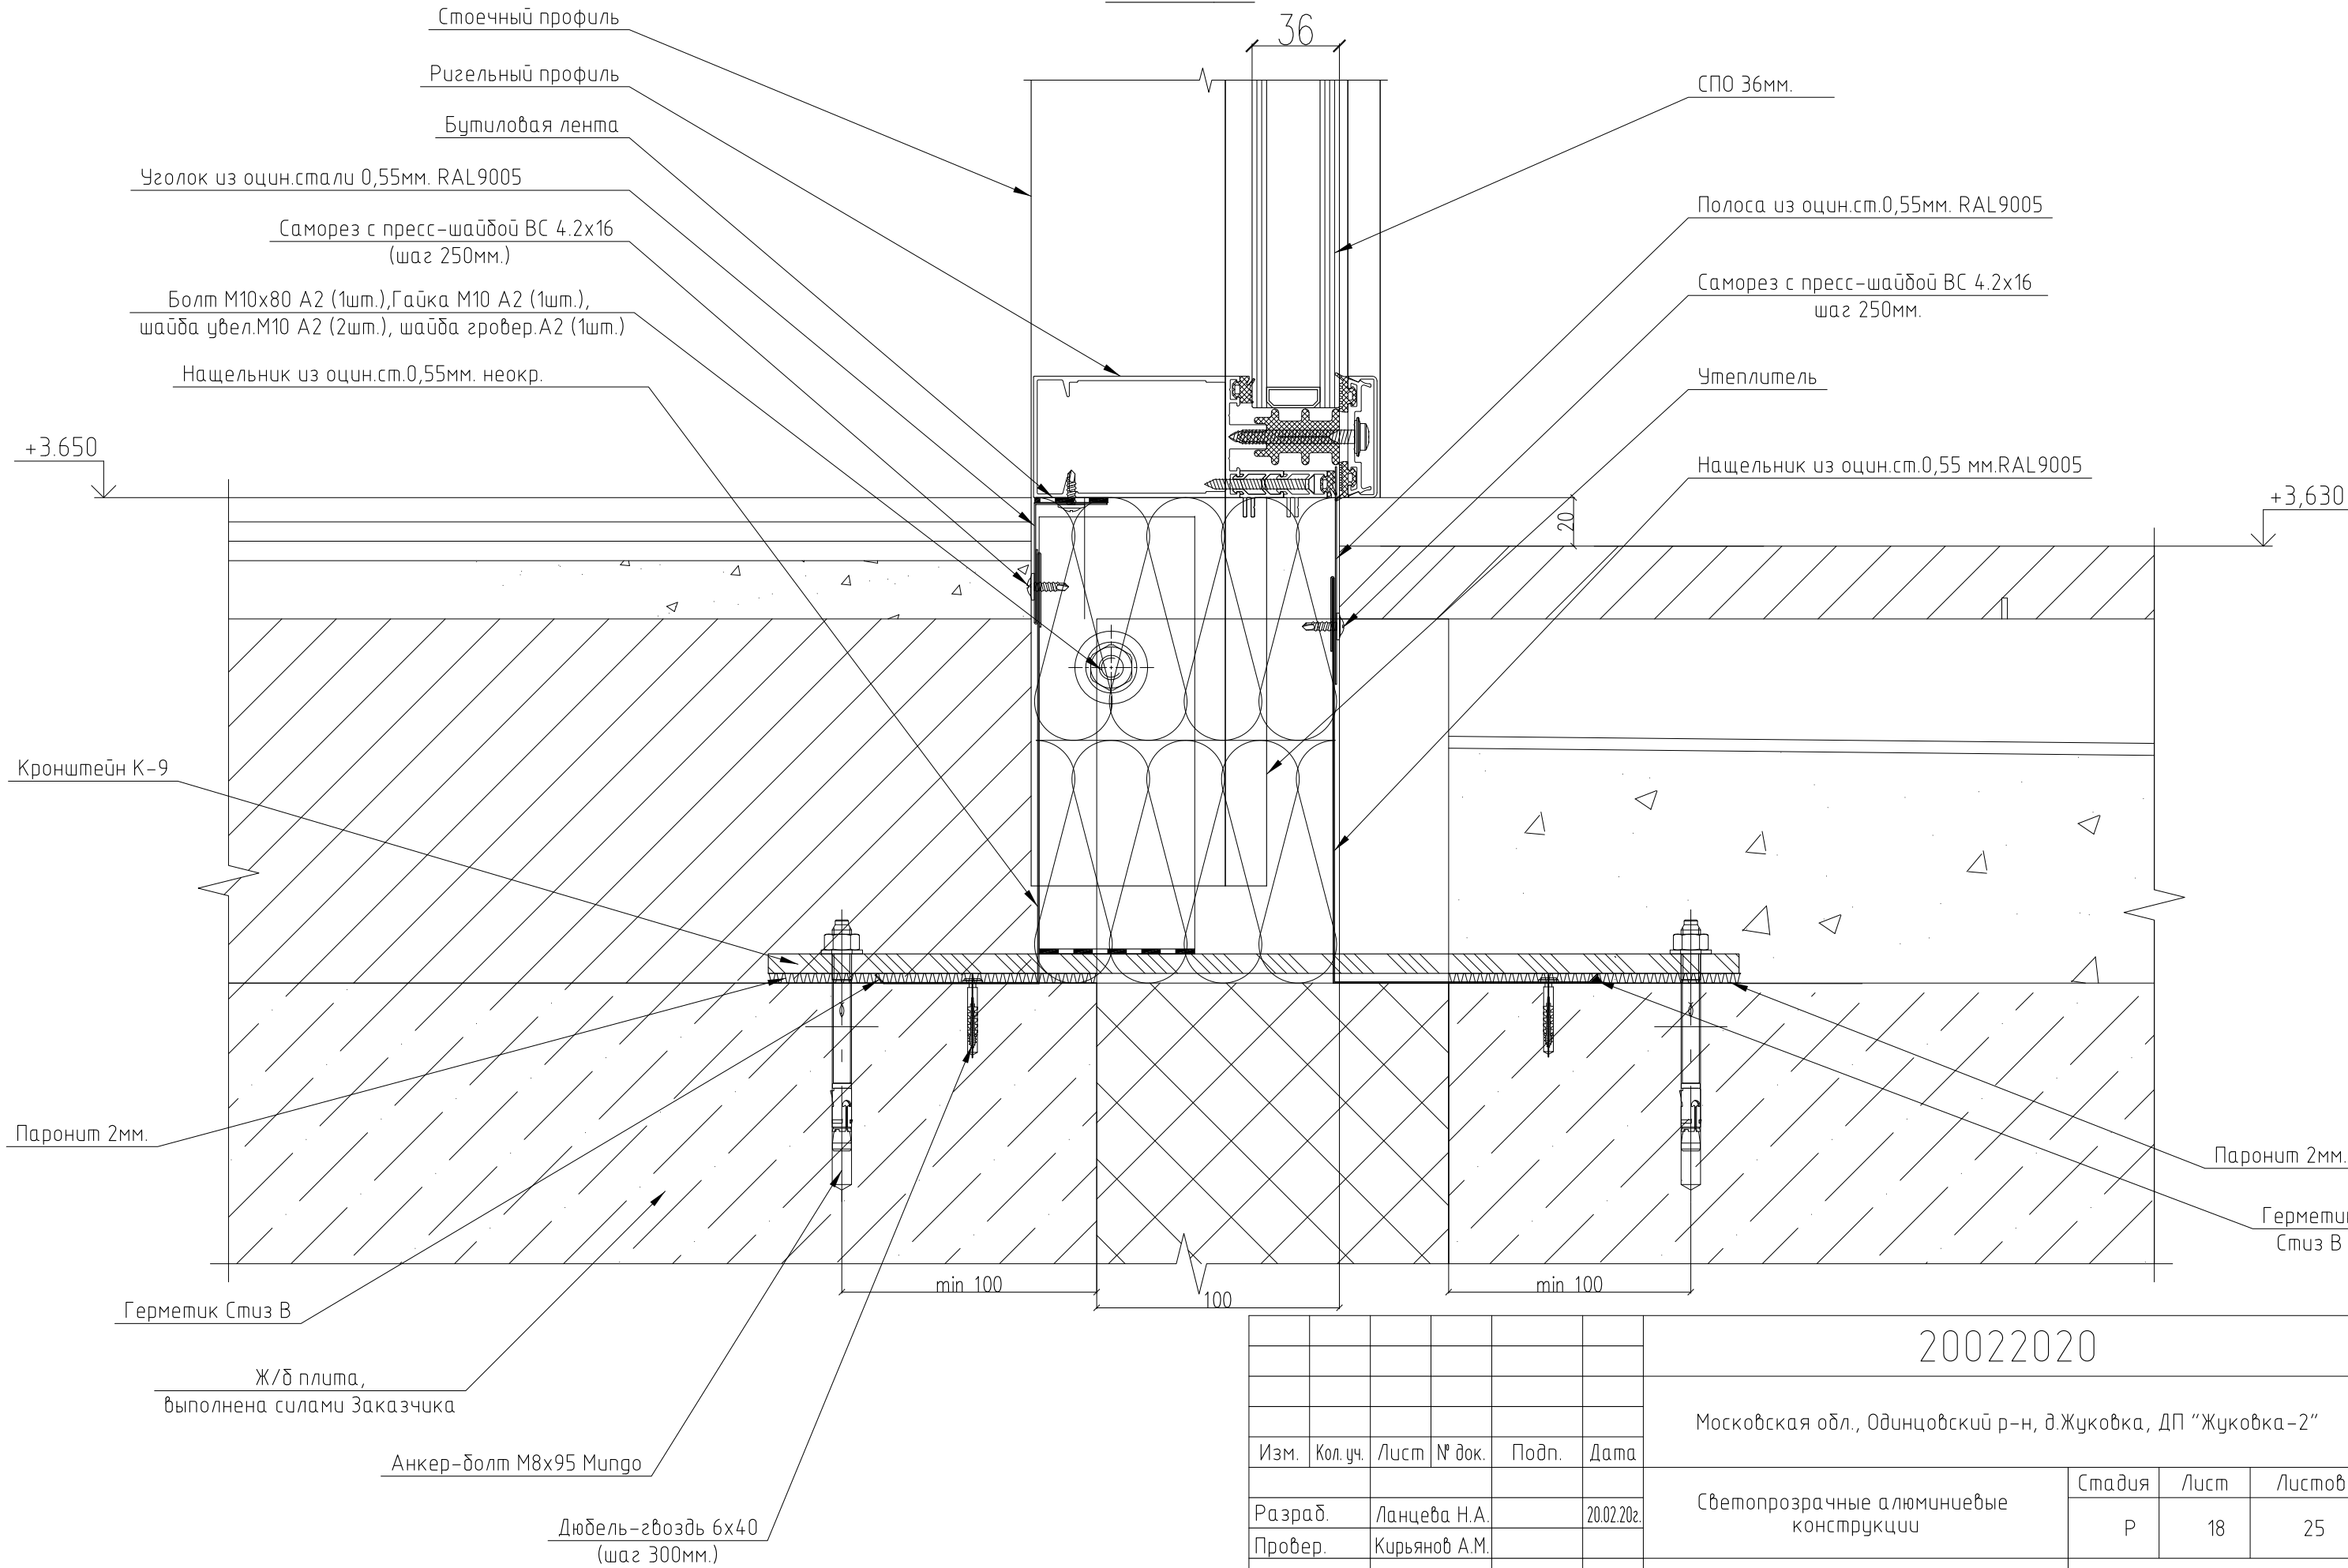


						20022020			
						Московская обл., Одинцовский р-н, д.Жуковка, ДП “Жуковка–2”			
Изм.	Кол.уч.	Лист	№ док.	Подп.	Дата	Светопрозрачные алюминиевые конструкции	Стадия	Лист	Листов
Разраб.		Ланцева Н.А.			20.02.20г.		Р	18	25
Провер.		Кириянов А.М.							
						Узел 15	ООО "Гармония"		
Утвердил		Коноплич С.В.							
ГИП									

Узел 18

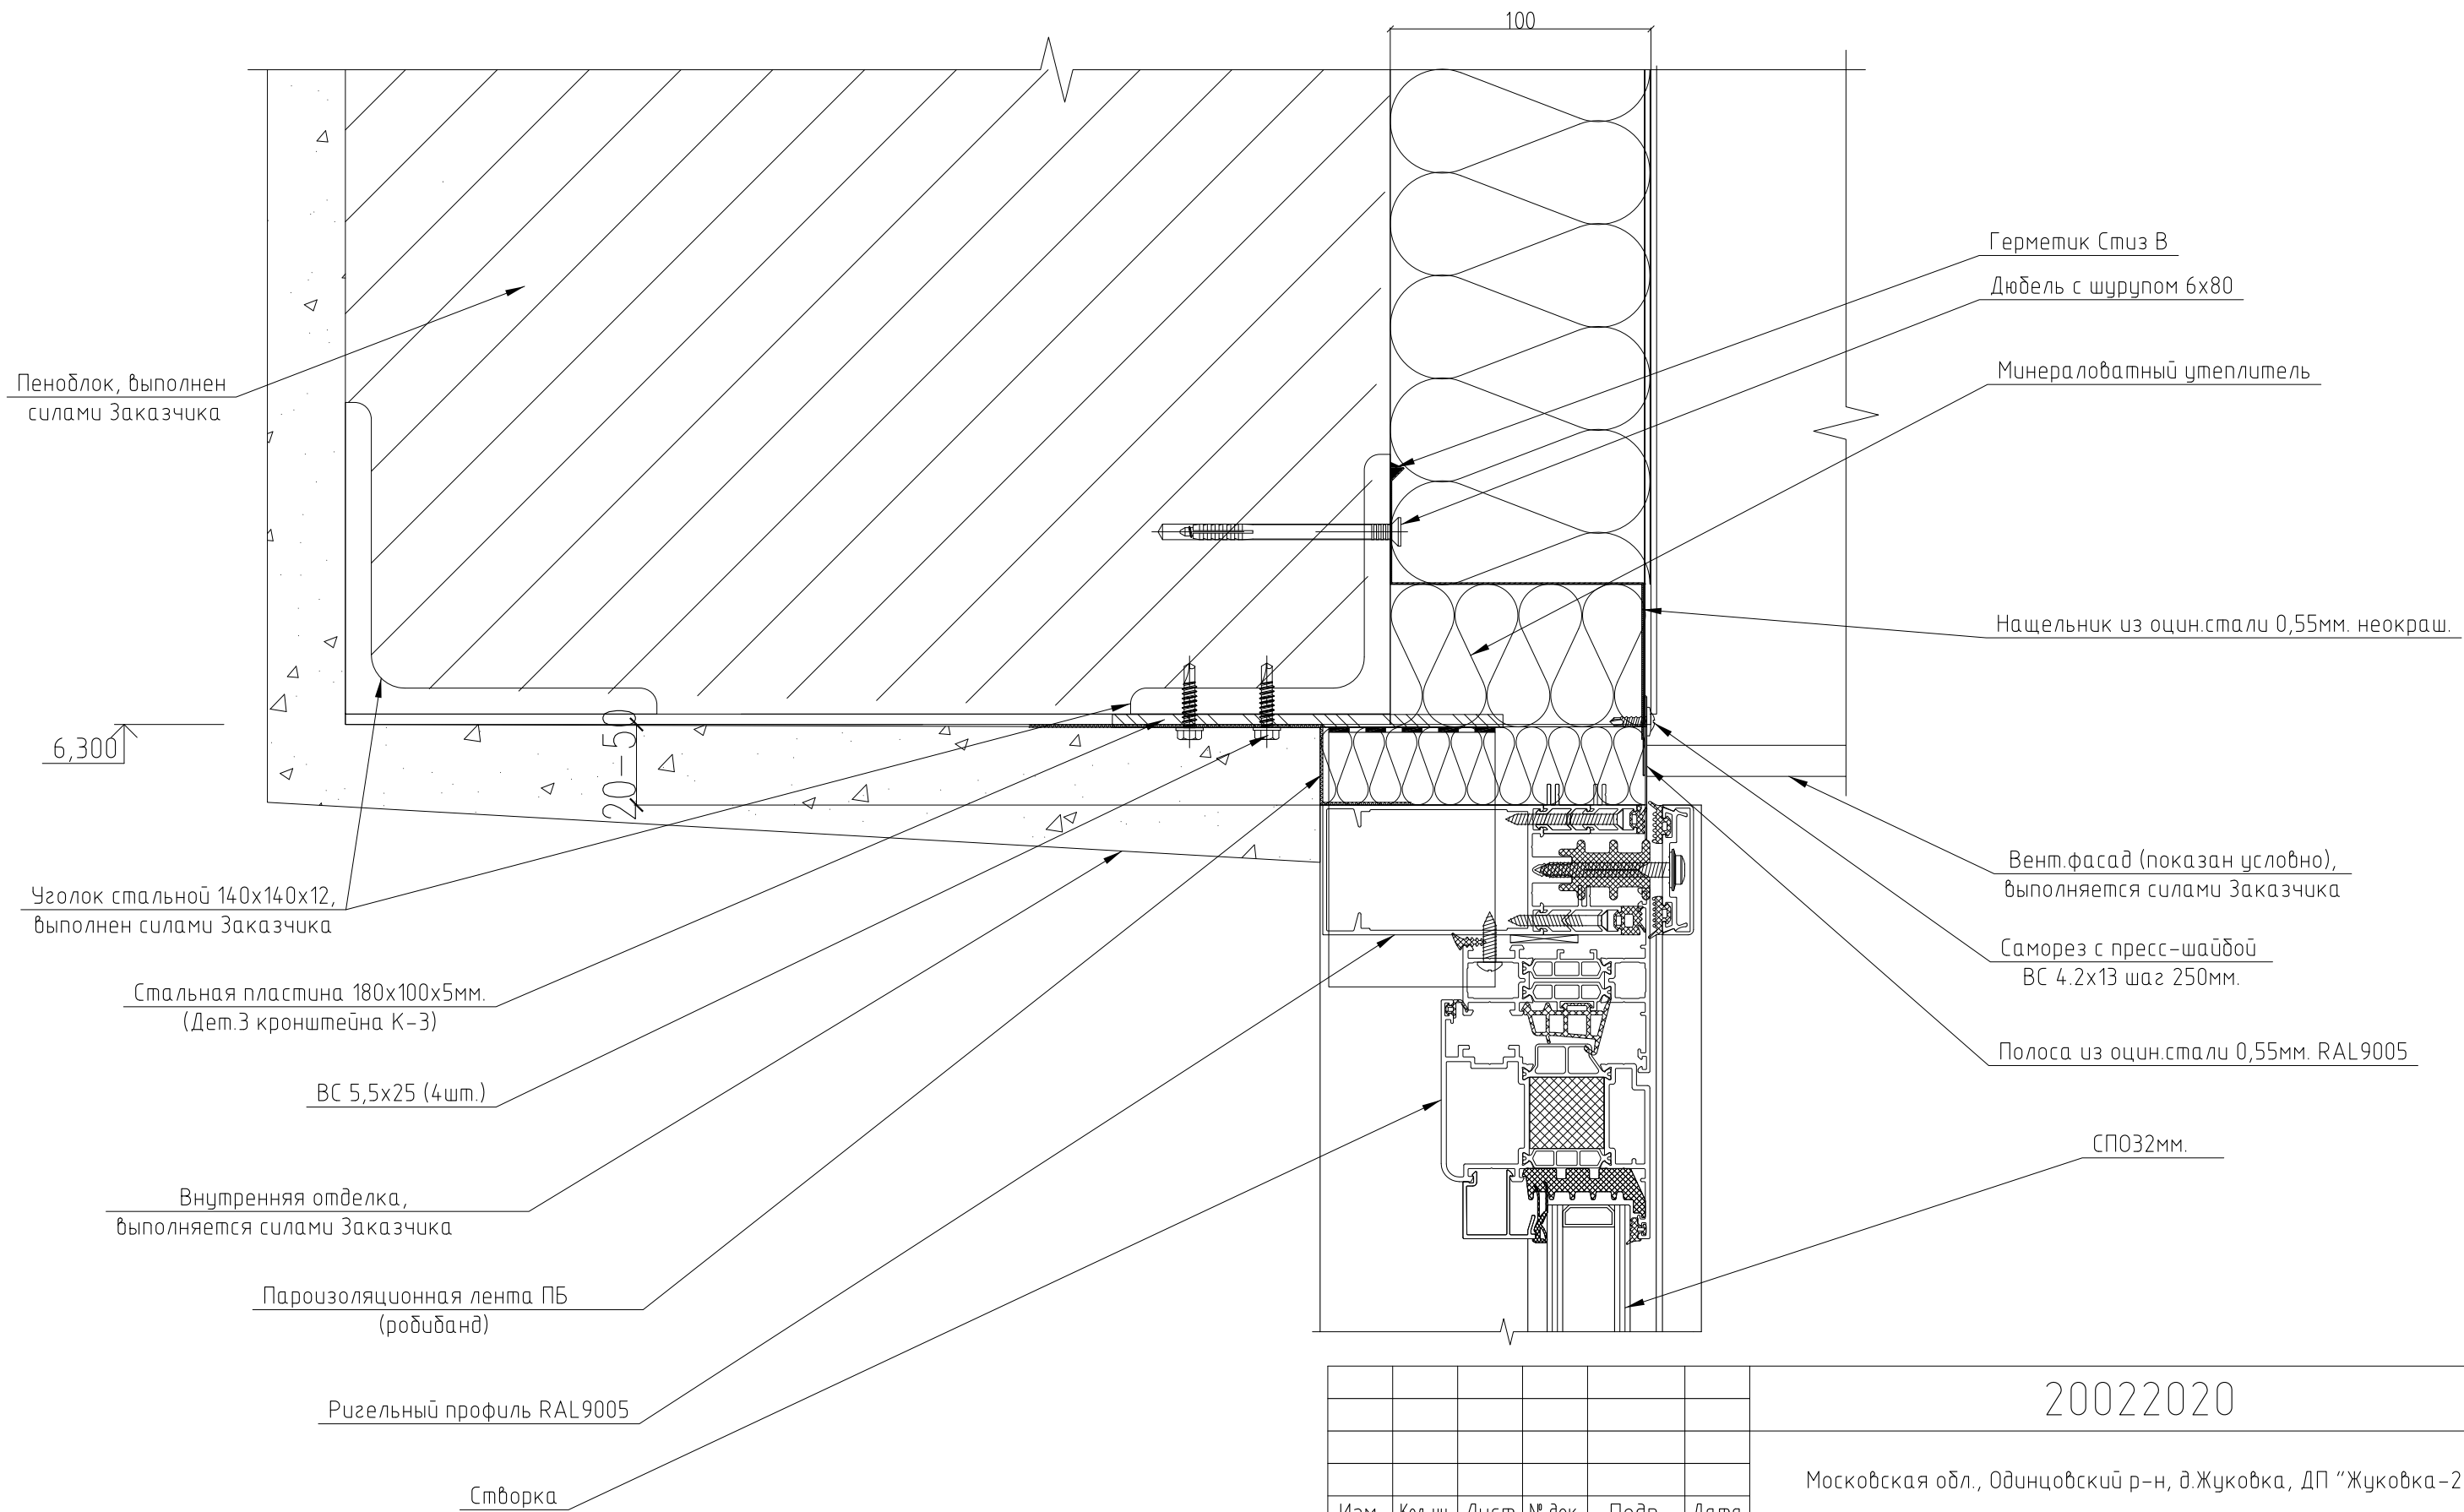


						20022020			
						Московская обл., Одинцовский р-н, д. Жуковка, ДП "Жуковка-2"			
Изм.	Кол. уч.	Лист	№ док.	Подп.	Дата	Светопрозрачные алюминиевые конструкции	Стадия	Лист	Листов
Разраб.		Ланцева Н.А.			20.02.20г.		Р	19	25
Провер.		Кириянов А.М.							
Утвердил		Коноплич С.В.				Узел 18	ООО "Гармония"		
ГИП									

Узел 5

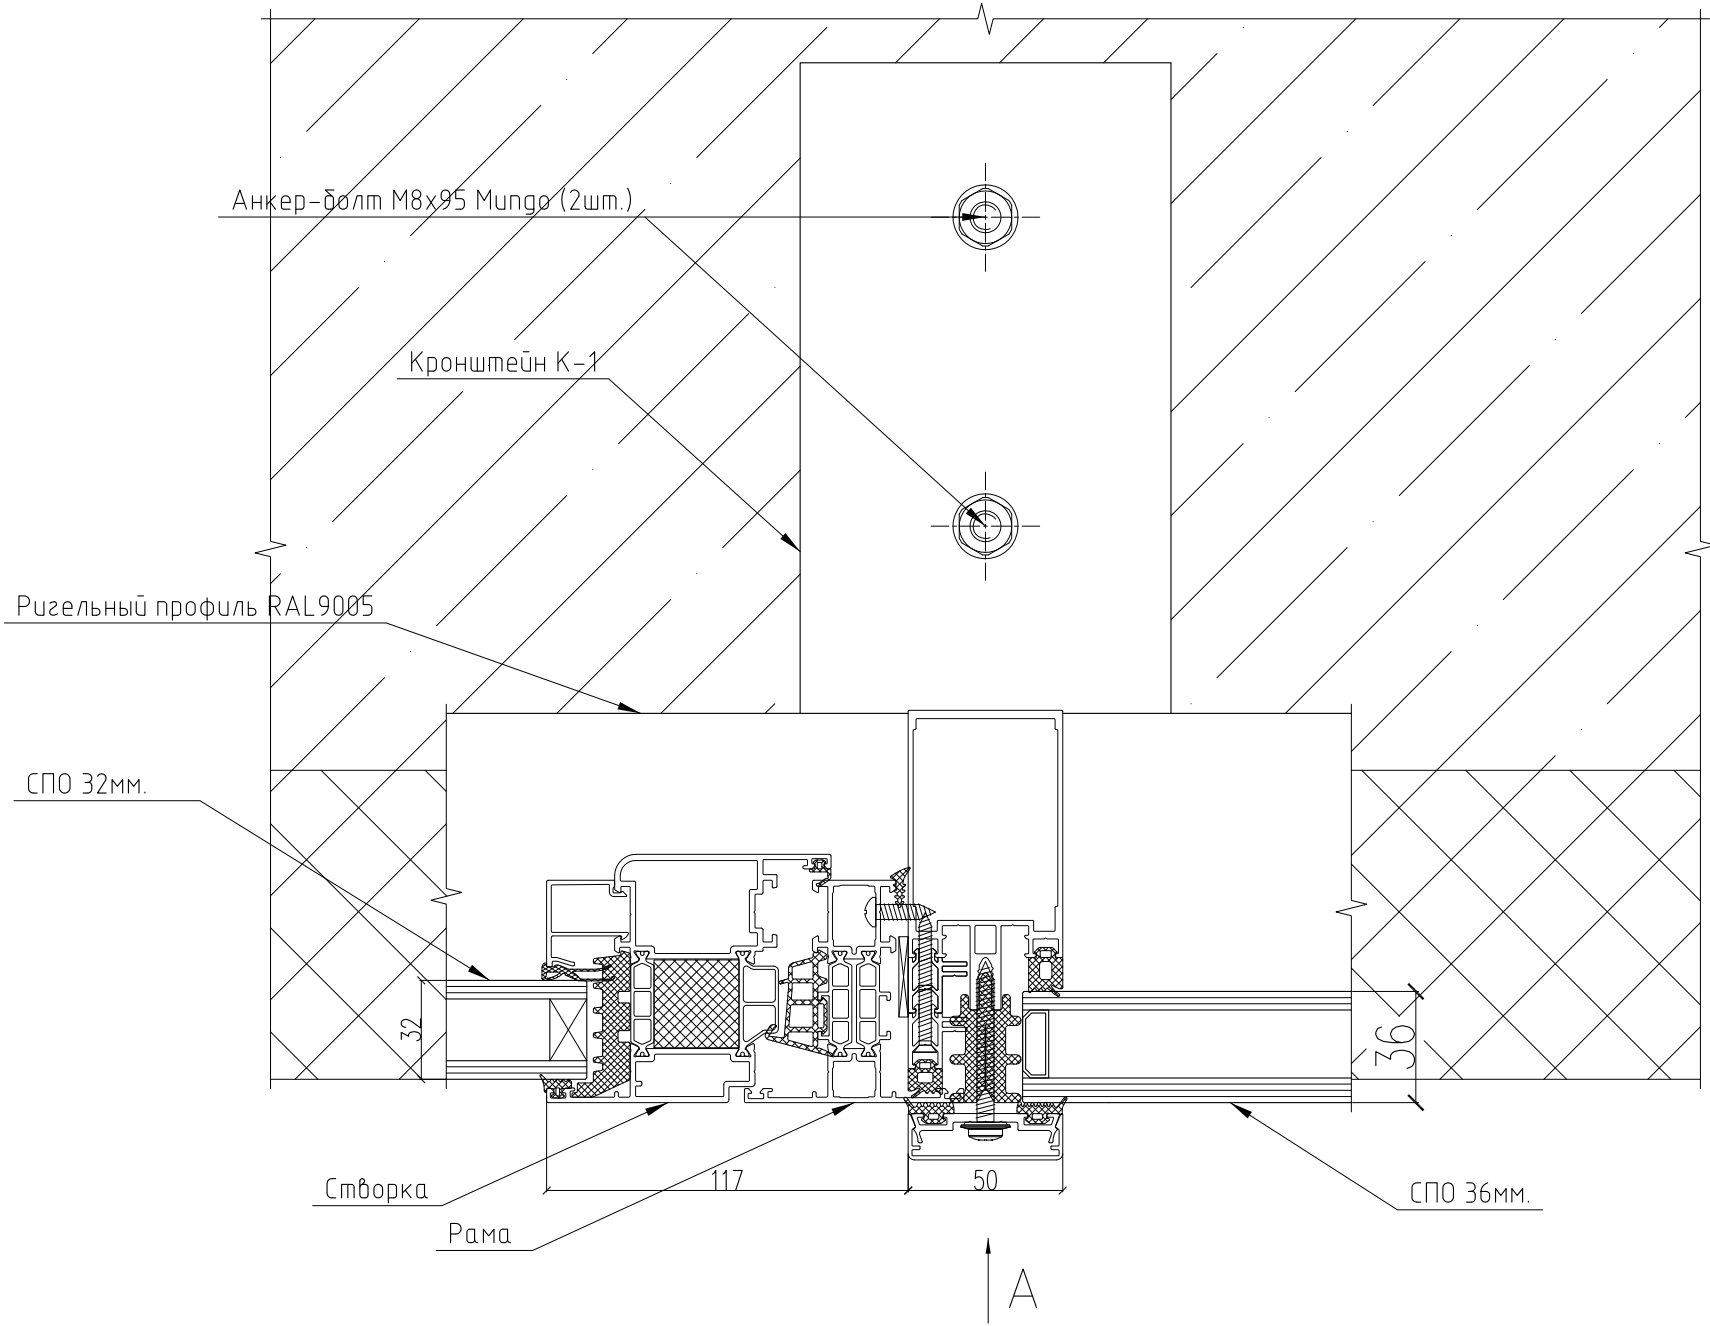

Вид А

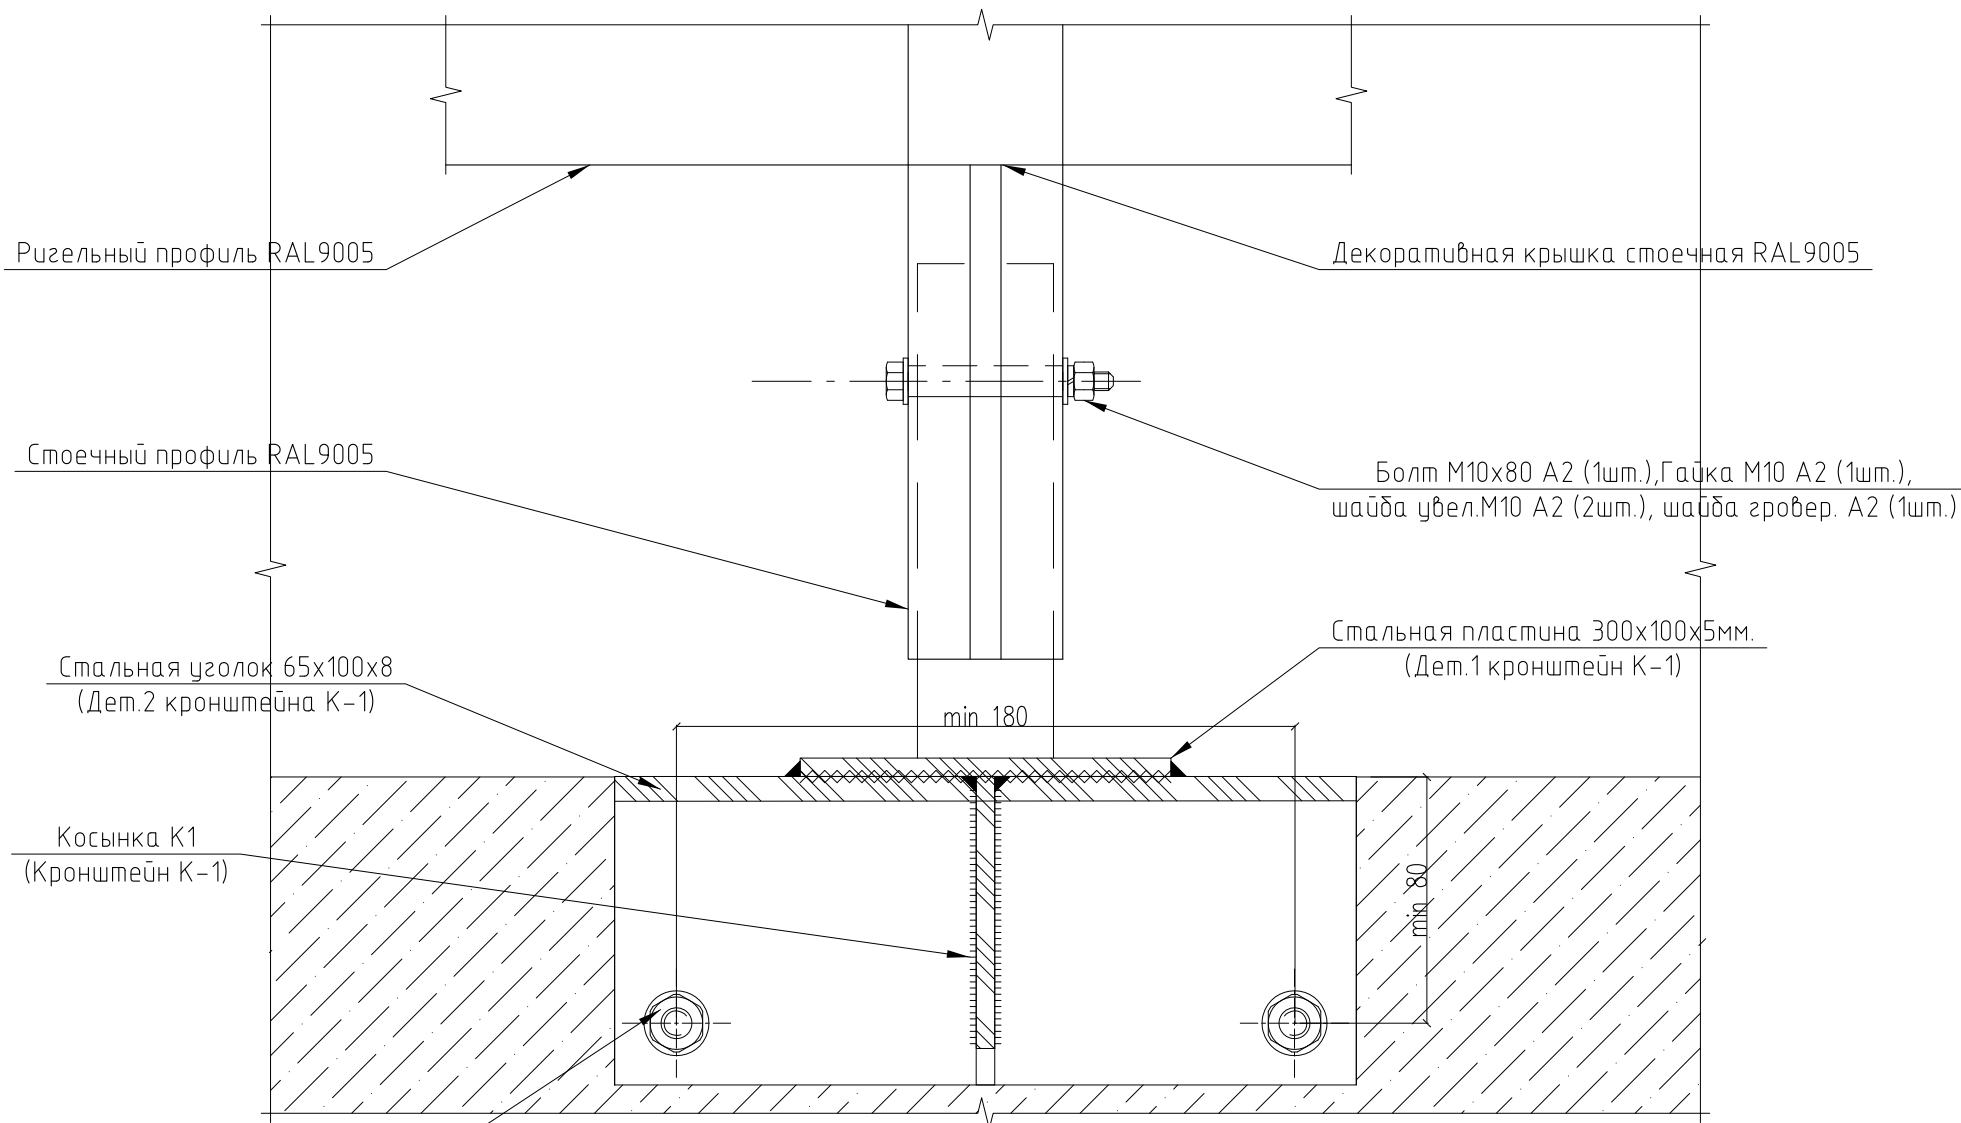

20022020

Московская обл., Одинцовский р-н, д. Жуковка, ДП "Жуковка-2"

Светопрозрачные алюминиевые конструкции

Стадия	Лист	Листов
Р	20	25


Узел 5

ООО "Гармония"


Инв. № подл.	Подп. и дата	Взам. инв. №

Изм.	Кол. уч.	Лист	№ док.	Подп.	Дата
Разраб.		Ланцева Н.А.			20.02.2020
Провер.		Кириянов А.М.			
Утвердил		Коноплич С.В.			
ГИП					


Узел 7

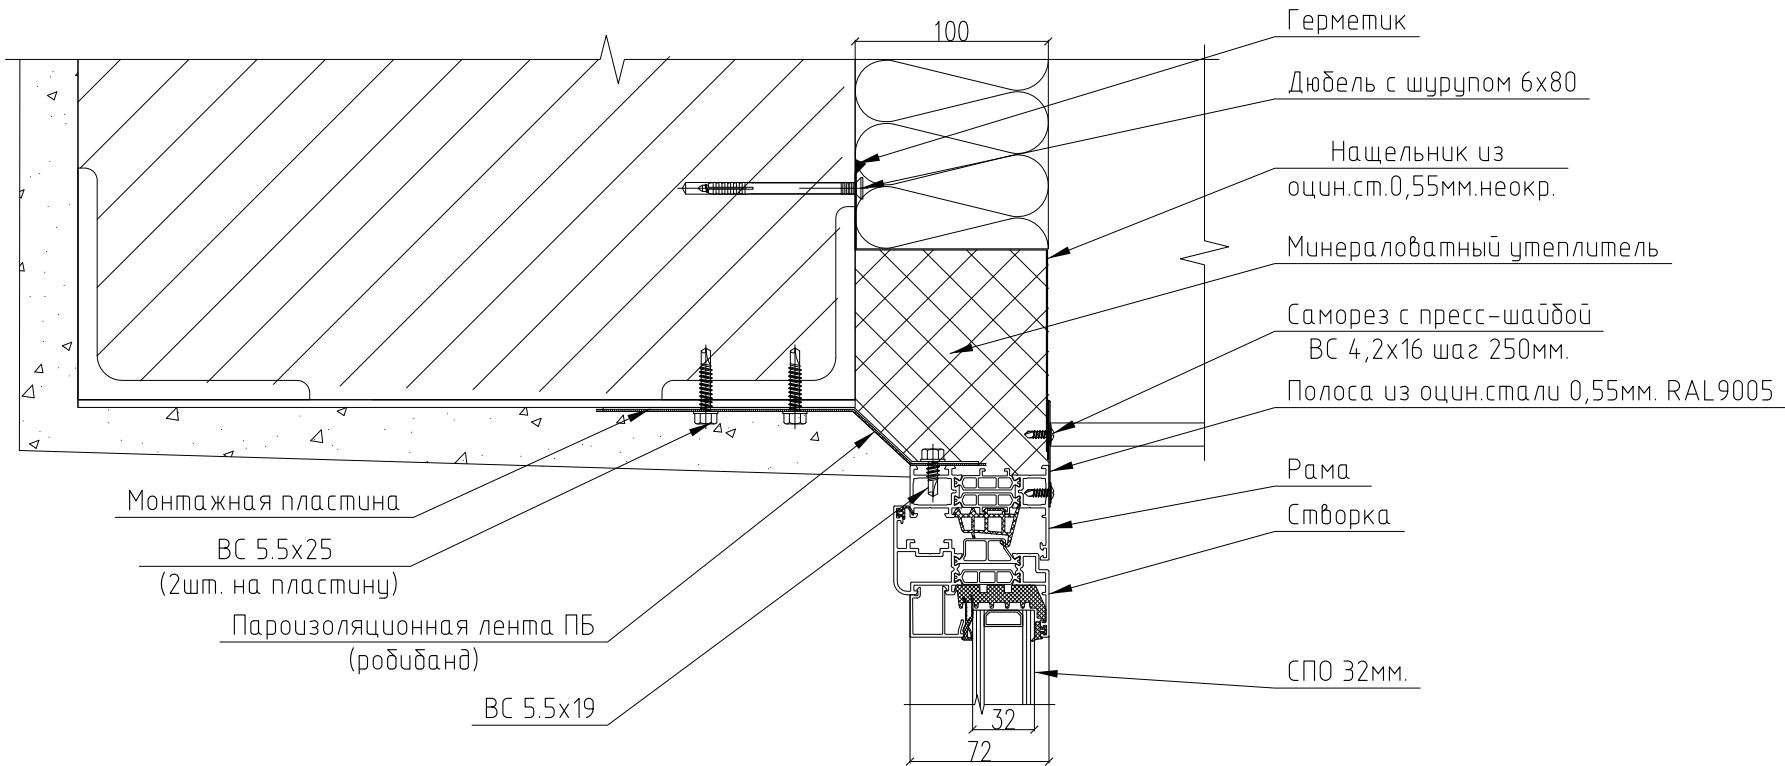

Узел 6

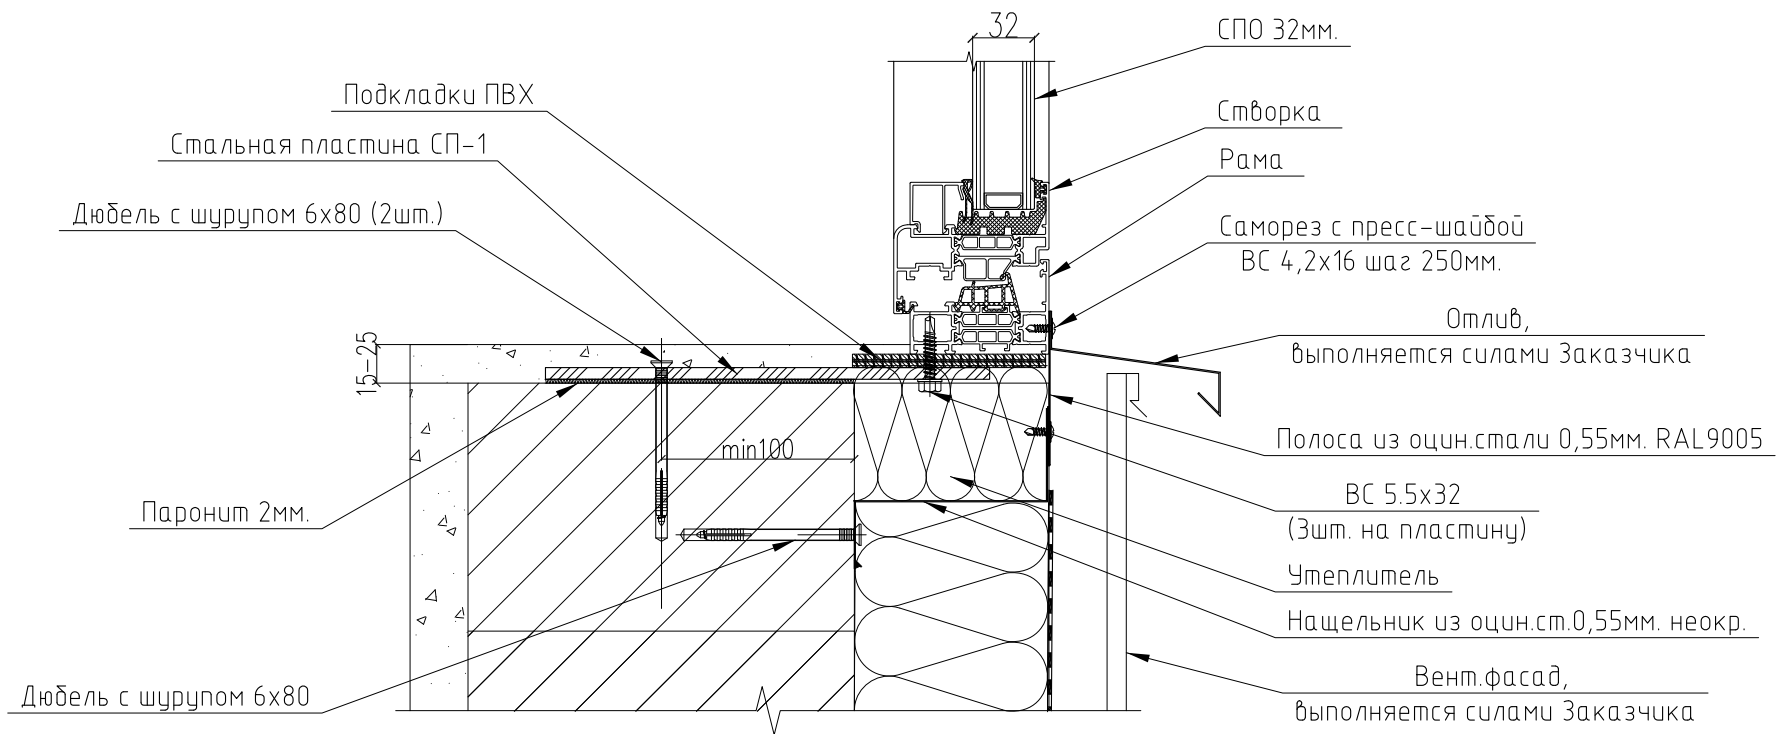


Узел 8

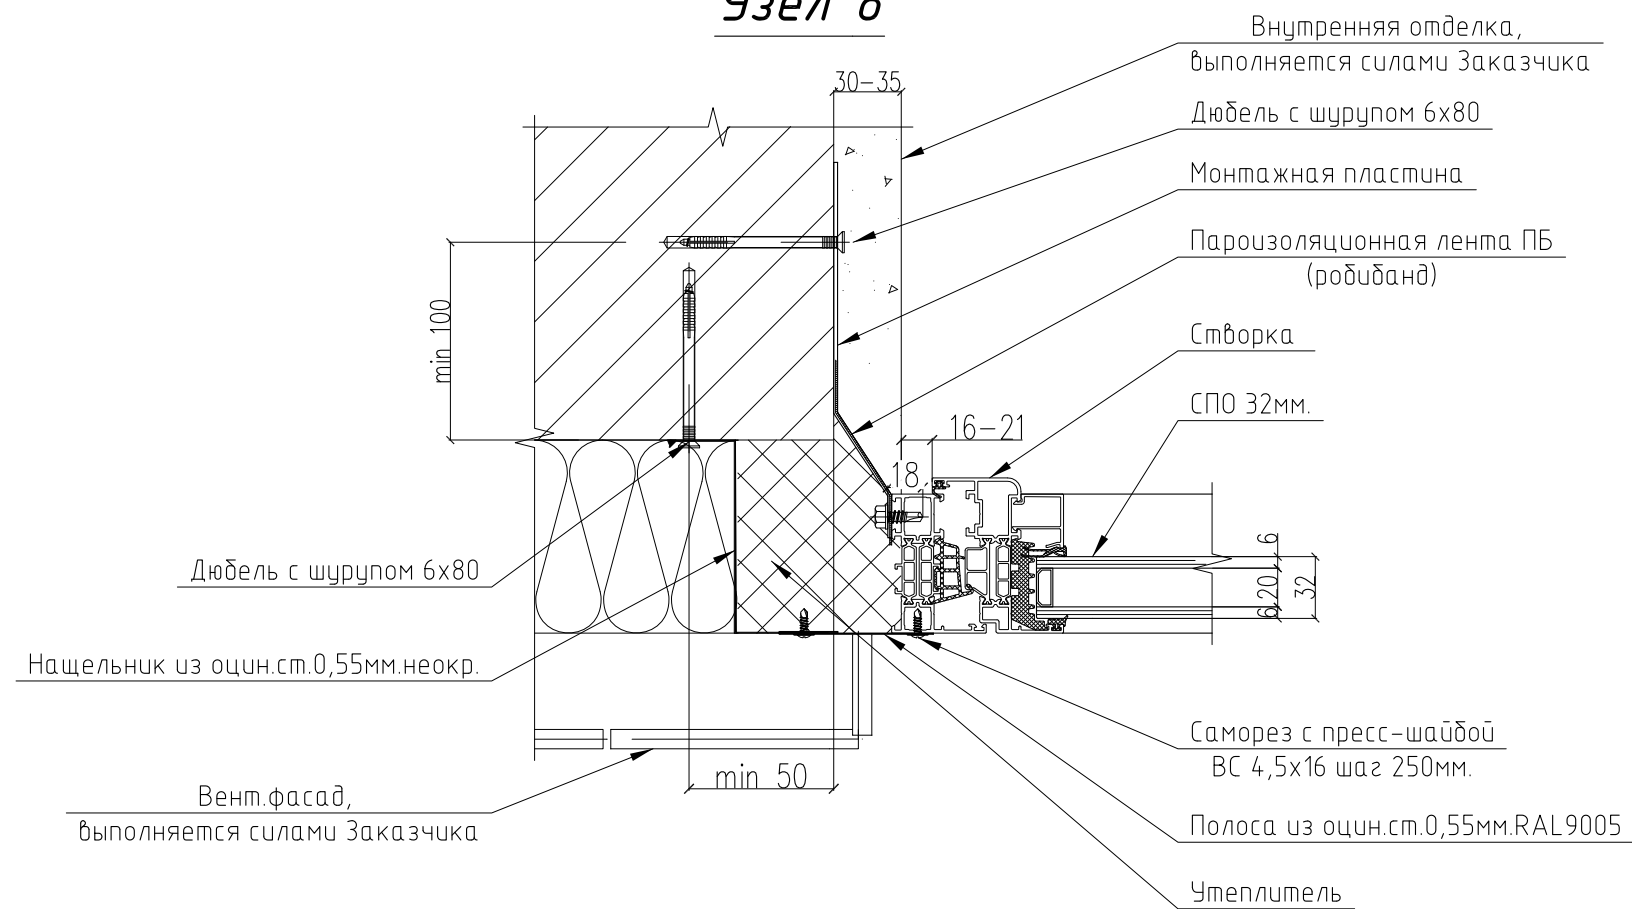


Инв. № подл.	Подп. и дата	Взам. инв. №	

						20022020			
						Московская обл., Одинцовский р-н, д.Жуковка, ДП "Жуковка-2"			
Изм.	Кол.уч.	Лист	№ док.	Подп.	Дата	Светопрозрачные алюминиевые конструкции	Стадия	Лист	Листов
Разраб.		Ланцева Н.А.			20.02.2020г.		Р	21	25
Провер.		Кириянов А.М.							
Утвердил		Коноплич С.В.				Узел 6, 7	ООО "Гармония"		
ГИП									

Узел 11

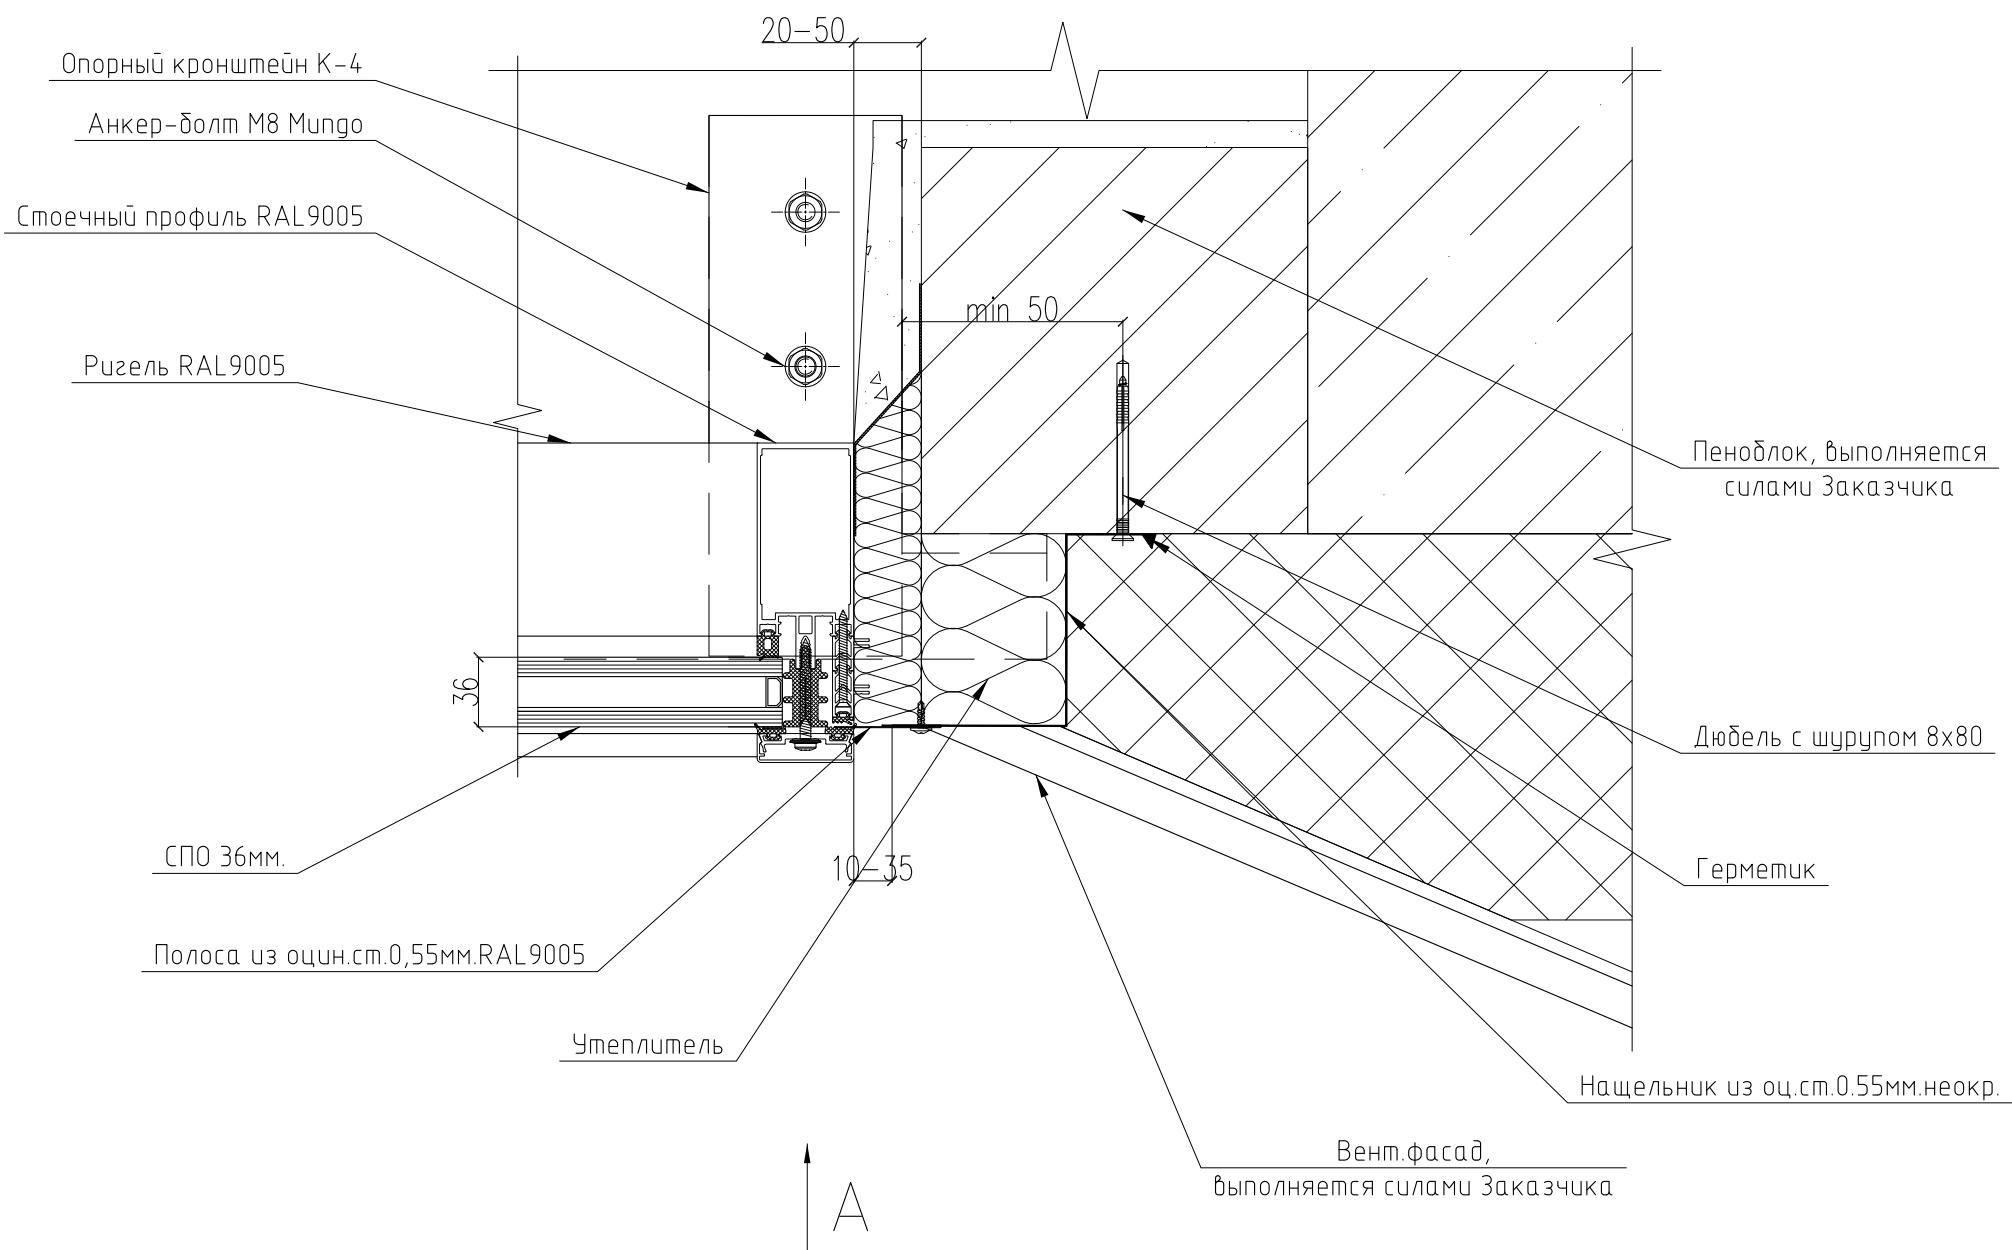


Вид А

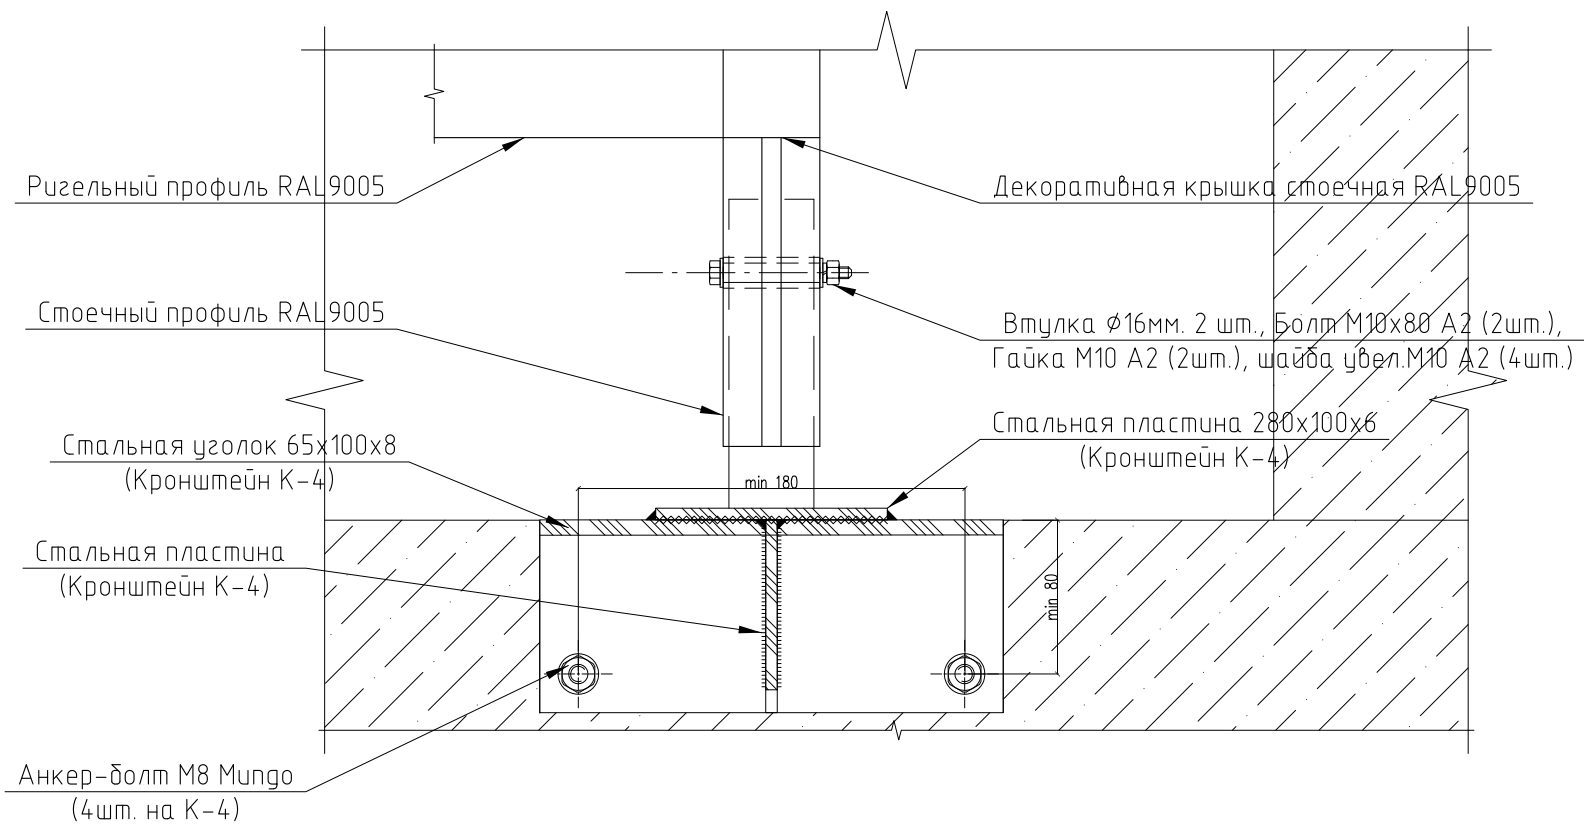

Инв. № подл.	Подп. и дата	Взам. инв. №	


						17022020			
						Московская обл., Одинцовский р-н, д. Жуковка, ДП "Жуковка-2"			
Изм.	Кол. уч.	Лист	№ док.	Подп.	Дата	Свето ­ прозрачные алюминиевые конструкции	Стадия	Лист	Листов
Разраб.		Ланцева Н.А.			20.02.202г.		Р	22	25
Провер.		Кириянов А.М.							
Утвердил		Коноплич С.В.				Узел 11	ООО "Гармония"		
ГИП									

Узел 13

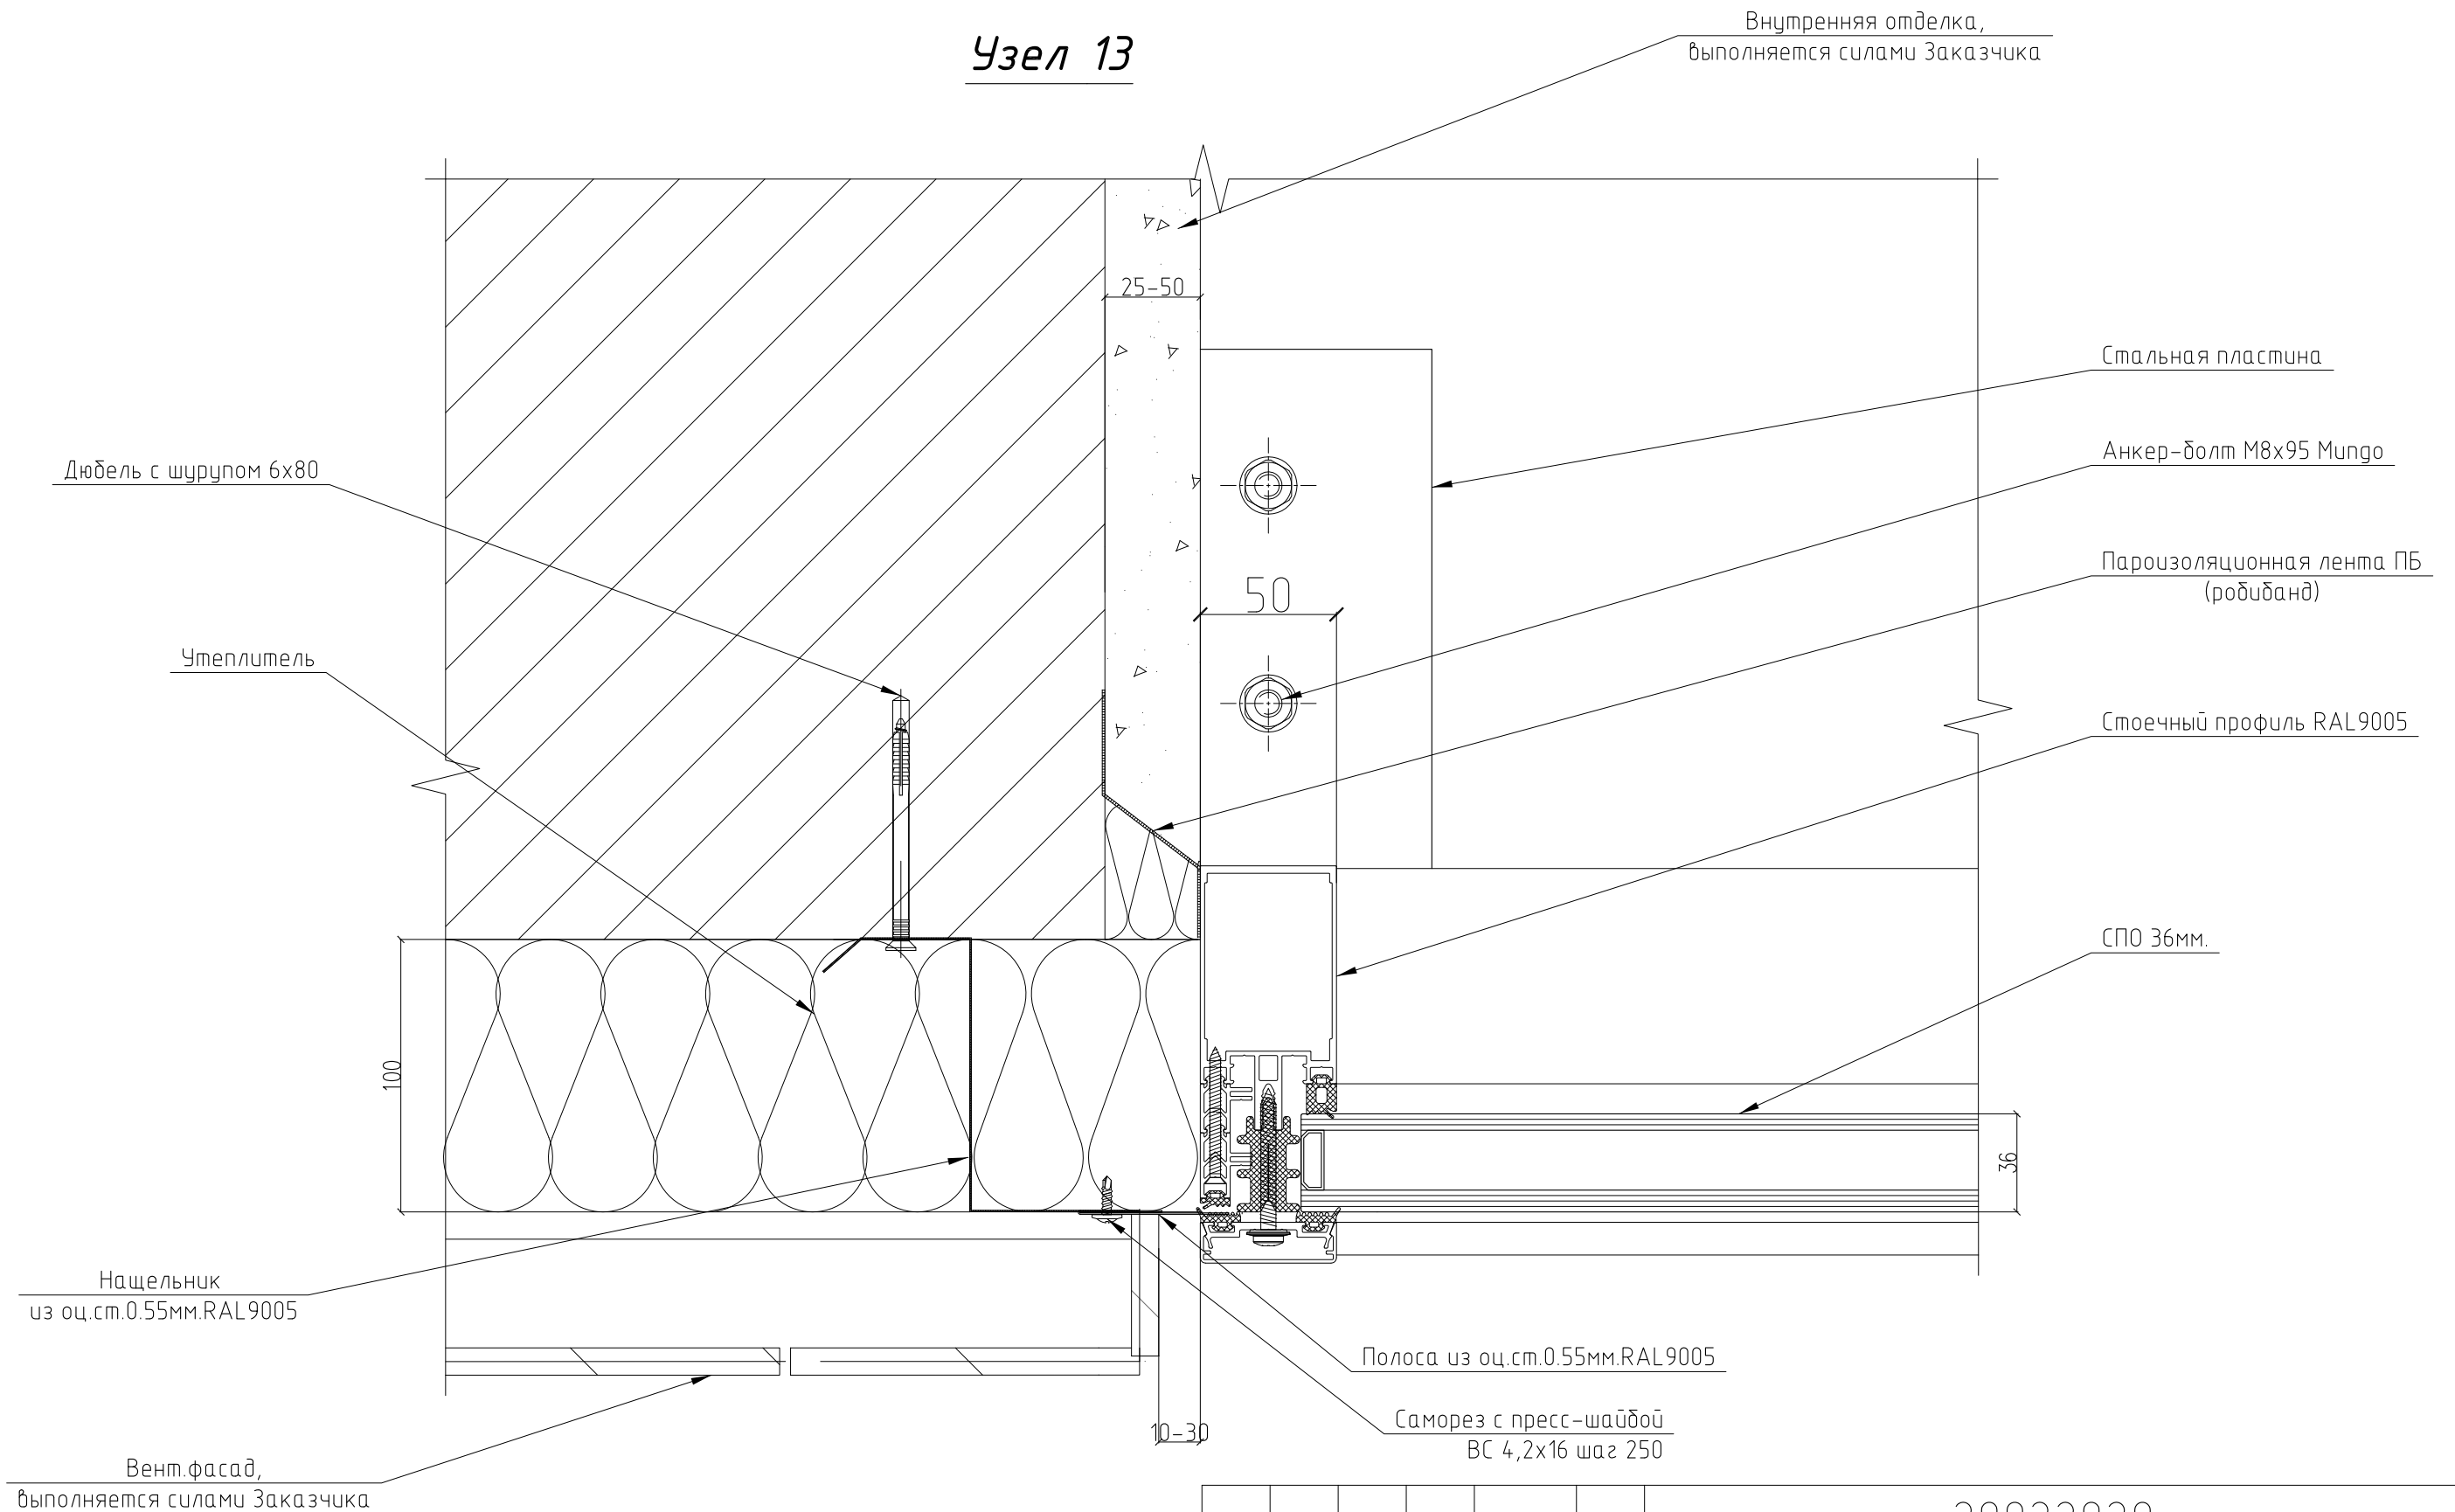


						20022020			
						Московская обл., Одинцовский р-н, д.Жуковка, ДП "Жуковка-2"			
Изм.	Кол.уч.	Лист	№ док.	Подп.	Дата	Светопрозрачные алюминиевые конструкции	Стадия	Лист	Листов
Разраб.		Ланцева Н.А.			20.02.20г.		Р	23	25
Провер.		Кириянов А.М.							
Утвердил		Коноплич С.В.				Узел 13	ООО "Гармония"		
ГИП									

Узел 14

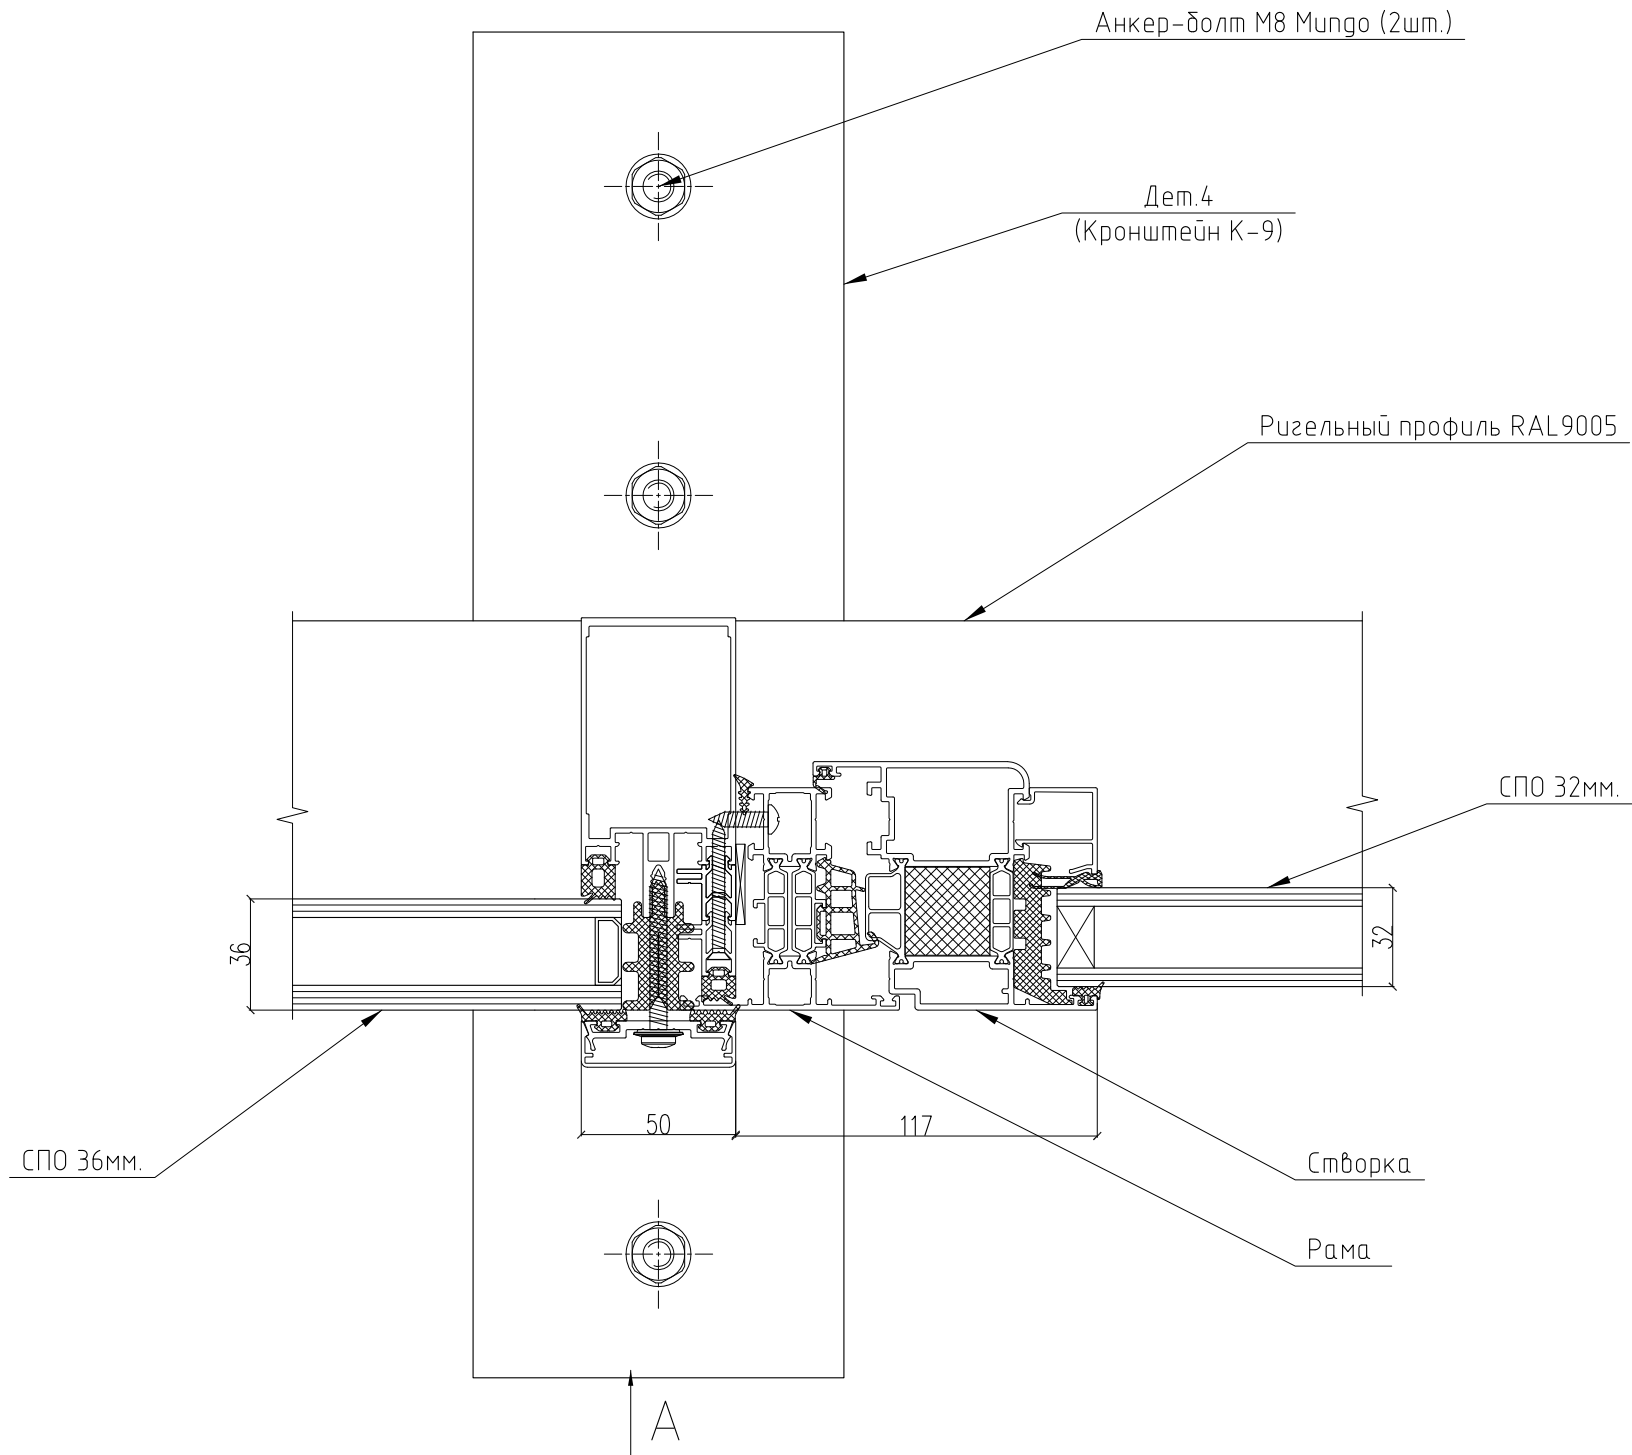


Вид А

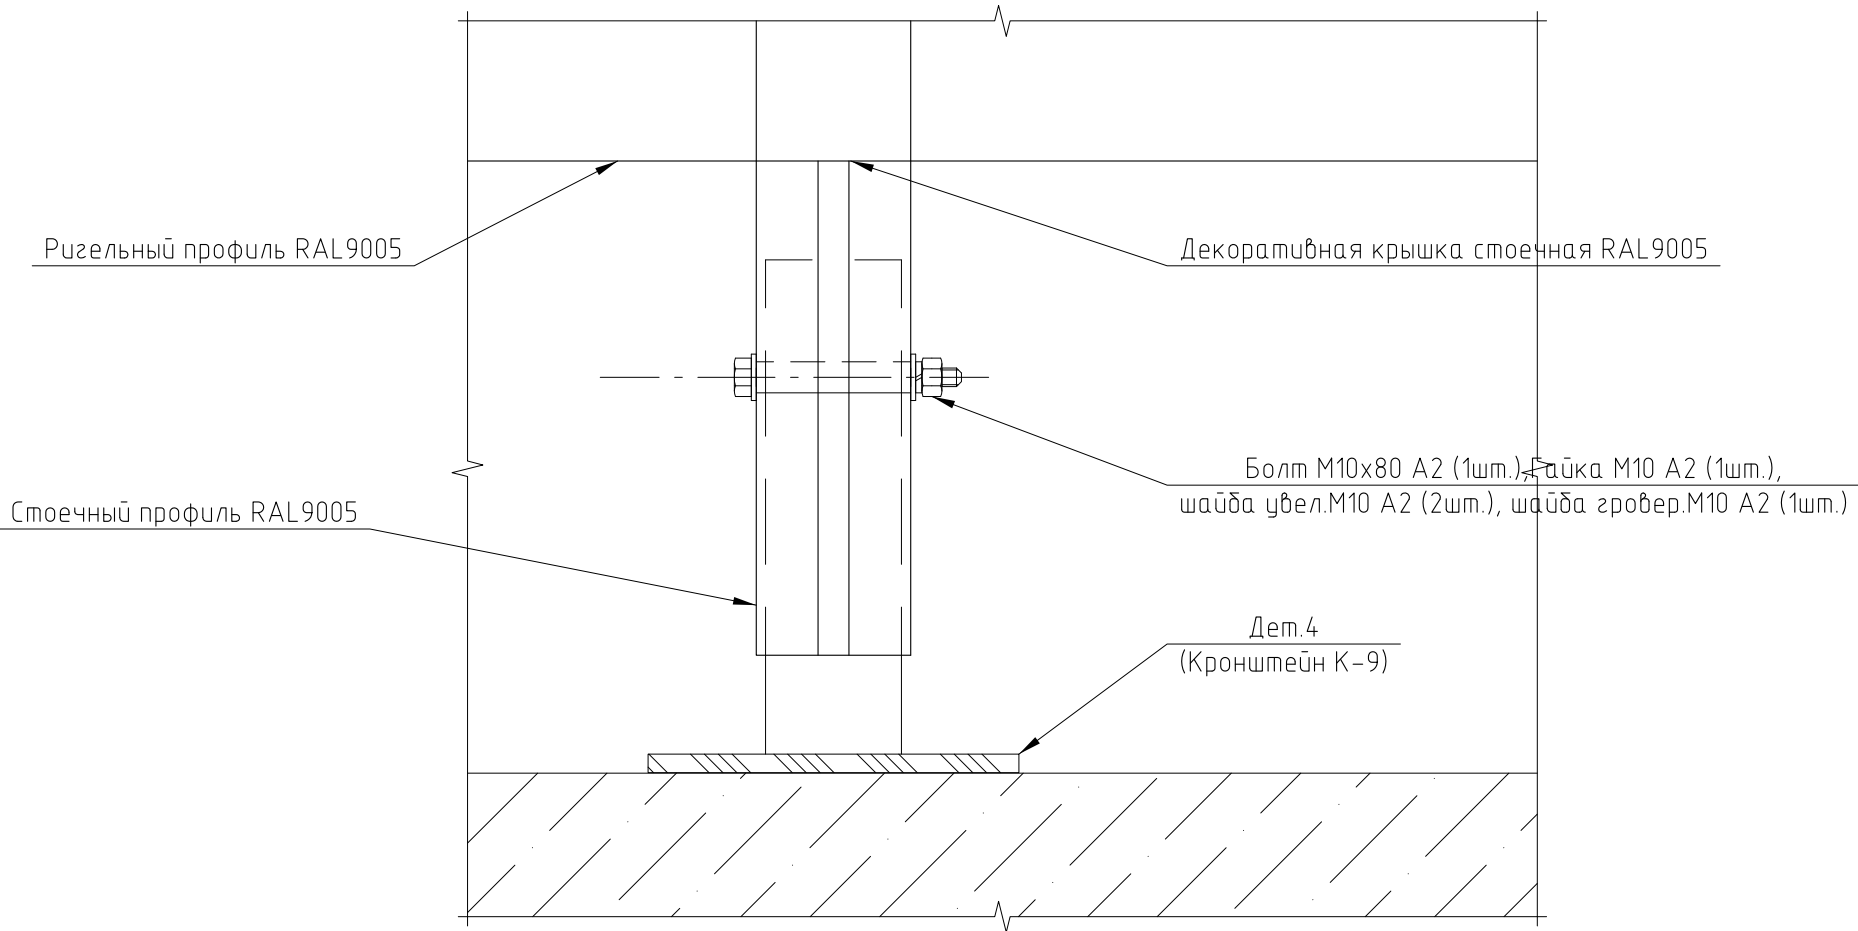


						20022020			
						Московская обл., Одинцовский р-н, д.Жуковка, ДП "Жуковка-2"			
Изм.	Кол.уч.	Лист	№ док.	Подп.	Дата	Светопрозрачные алюминиевые конструкции	Стадия	Лист	Листов
Разраб.		Ланцева Н.А.			20.02.2020		Р	24	25
Провер.		Кириянов А.М.							
Утвердил		Коноплич С.В.				Узел 14.	ООО "Гармония"		
ГИП									

Инв. № подл.	Подп. и дата	Взам. инв. №

Узел 16

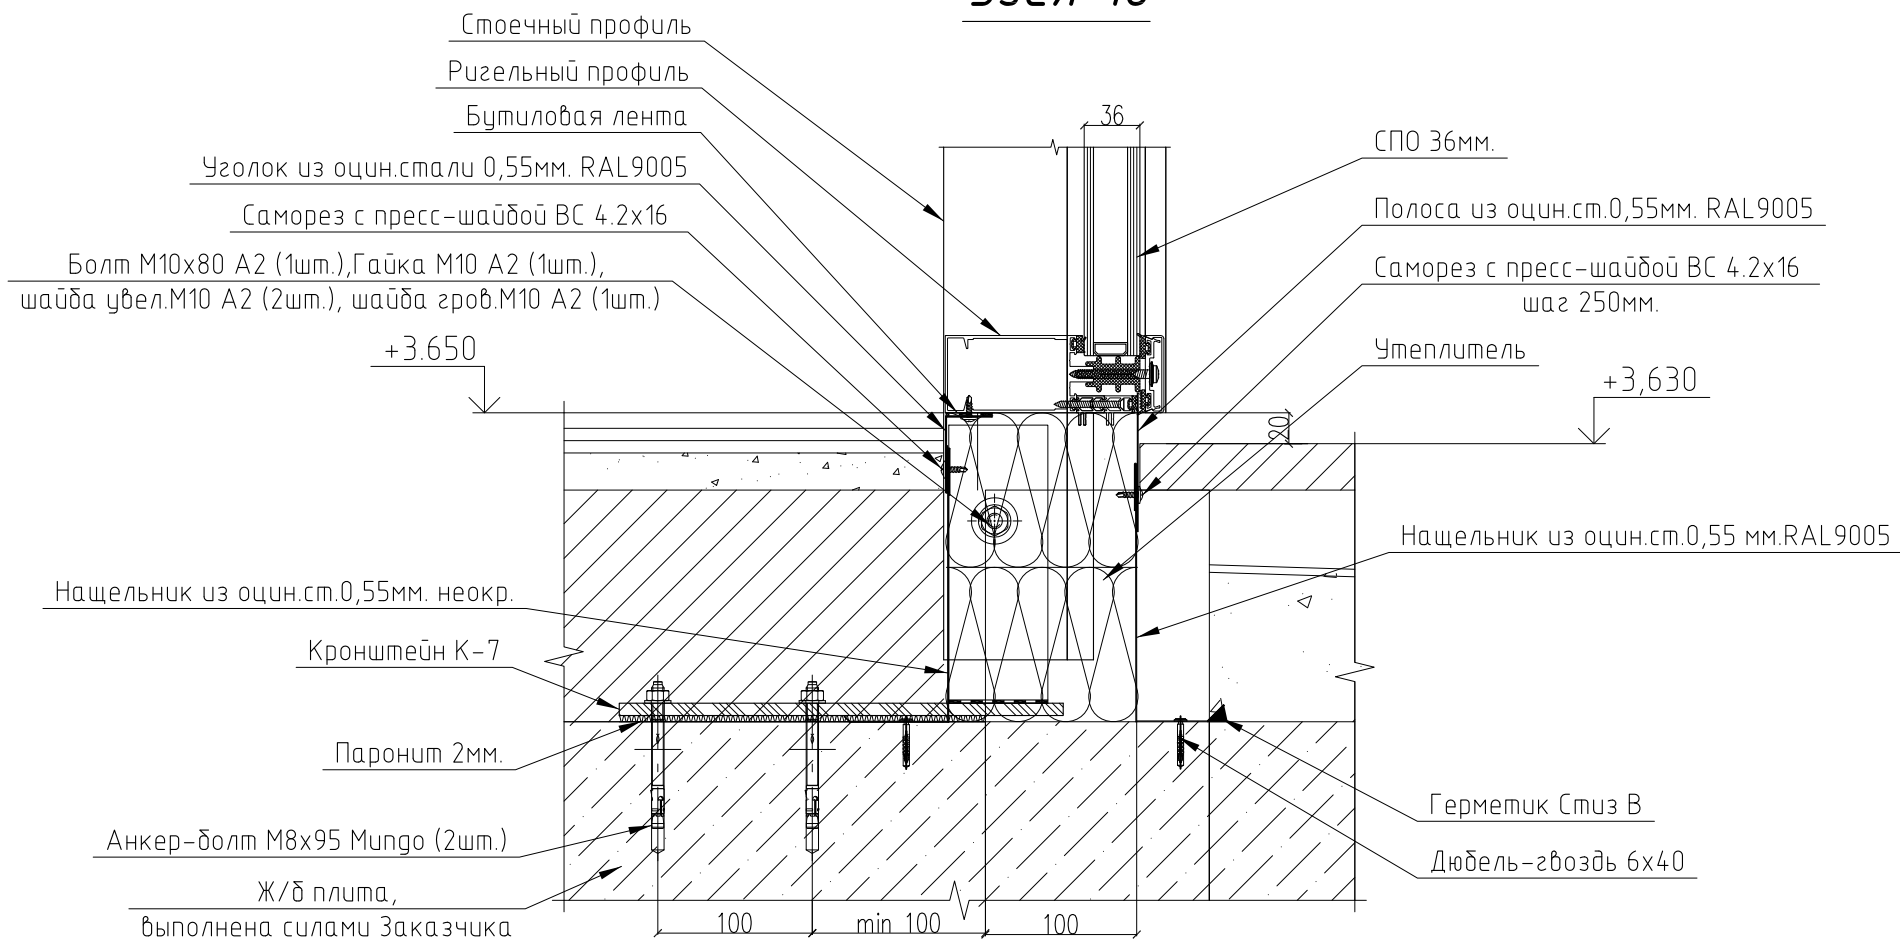

Узел 17

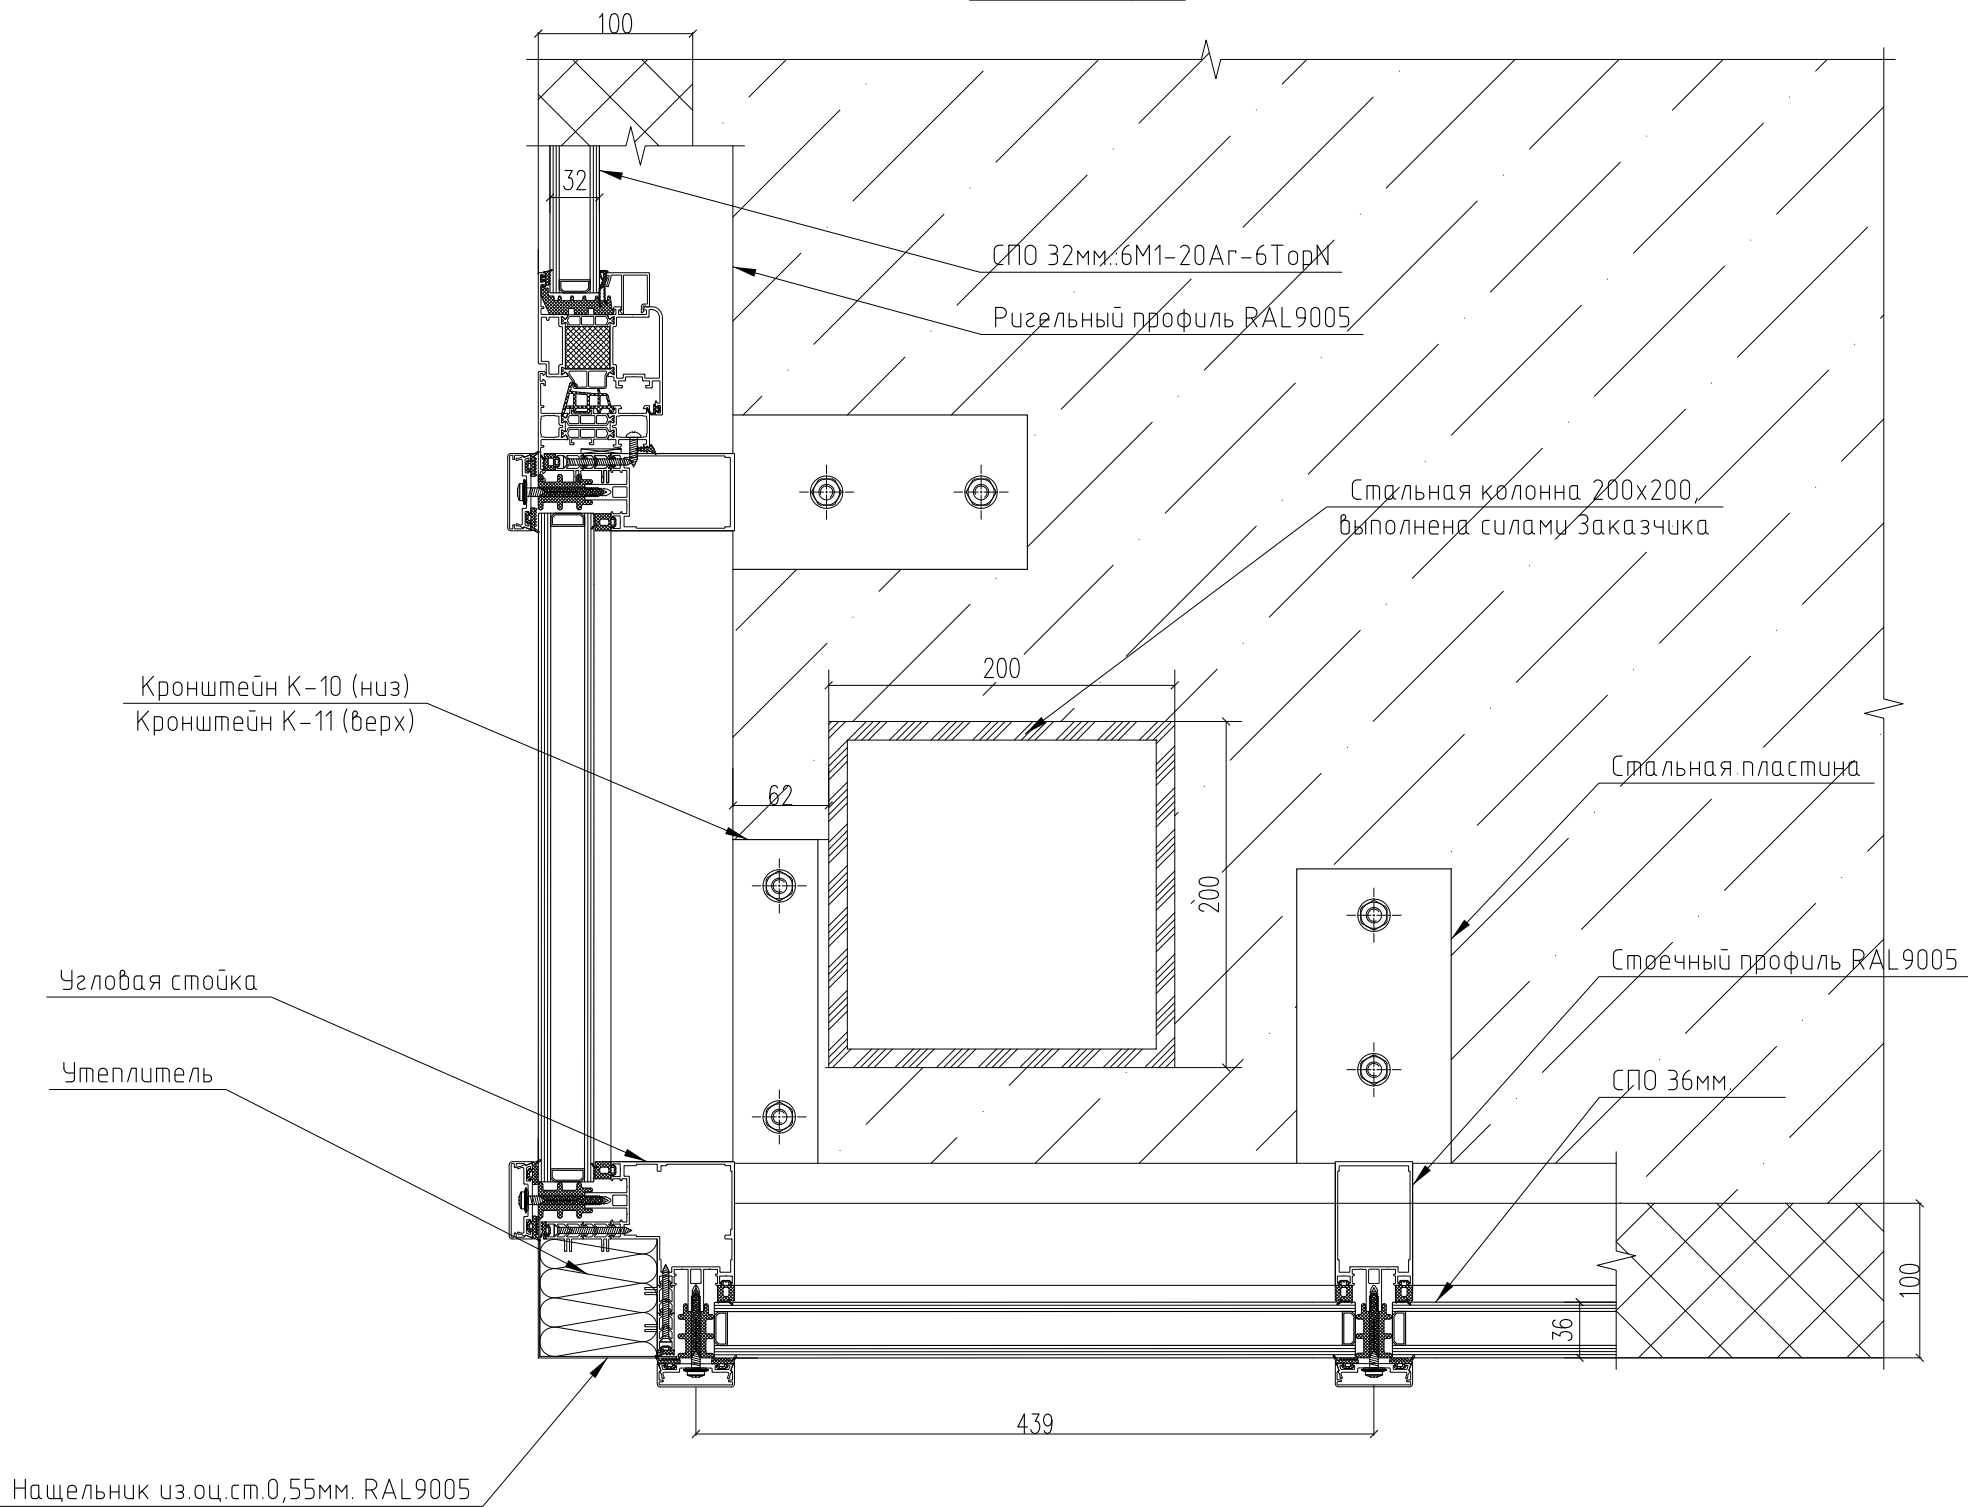

						20022020			
						Московская обл., Одинцовский р-н, д. Жуковка, ДП "Жуковка-2"			
Изм.	Кол. уч.	Лист	№ док.	Подп.	Дата	Светопрозрачные алюминиевые конструкции	Стадия	Лист	Листов
Разраб.		Ланцева Н.А.			20.02.20г.		Р	25	25
Провер.		Кириянов А.М.							
Утвердил		Коноплич С.В.				Узел 16, 17.	ООО "Гармония"		
ГИП									