

Лист согласования проекта.

Согласовано _____ / _____ /
" _____ " _____ /2020./

Согласовано _____ / _____ /
" _____ " _____ /2020./

Согласовано _____ / _____ /
" _____ " _____ /2020./

Согласовано _____ / _____ /
" _____ " _____ /2020./

Согласовано _____ / _____ /
" _____ " _____ /2020./

Согласовано _____ / _____ /
" _____ " _____ /2020./

Общие данные

1. Данный комплект чертежей стадии КМ включает основные технические решения по изготовлению и монтажу алюминиевых конструкций (витражных окон общественных помещений первого этажа) по объекту: "Жилой дом по адресу: Московская область, Ленинский муниципальный район, с/п Булатниковское, п. Битца, корпус 4." Разработан на основании ТЗ ООО "ДСК-1 Проект" и проекта шифр Бз-4-АР2.

Размеры для изготовления алюминиевых конструкций, уточняются индивидуально, путем проведения геодезической съемки подготовленных проемов на объекте.

Проектирование ведется в соответствии с требованиями ГОСТ и СП (актуализированная редакция):

СП 20.13330.2016 "Нагрузки и воздействия"

СП 70.13330.2012 "Несущие и ограждающие конструкции"

СП 1238.13330.2016 "Алюминиевые конструкции"

СП 16.13330.2011 "Стальные конструкции"

СП 28.13330.2012 "Защита строительных конструкций от коррозии"

2. Алюминиевые конструкции выполнять согласно СП 128.13330.2012 "Алюминиевые конструкции."

Актуализированная редакция СНиП 2.03.06–85*, ГОСТ Р 56926–2016 "Конструкции оконные и балконные различного функционального назначения для жилых зданий"

3. Витражные окна в проекте выполнены с применением системы профилей "Алютех" серии ALT W62 и исполняются в соответствии с нормами и технологией фирмы производителя.

4. Изготовление и монтаж конструкций вести в соответствии с требованиями СП 70.13330.2012, технологиями и рекомендациями фирмы "Алютех" и правилами по технике безопасности.

5. Обработка профилей и комплектация изделий резиной, саморезами и прочей фурнитурой необходимо выполнять в строгом соответствии с рекомендациями производителя профильной системы

6. Согласно техническому заданию Заказчика и ГОСТ 23166-99 "Блоки оконные. Общие технические условия", показатель приведенного сопротивления теплопередачи витражных окон не ниже $0,65 \text{ м}^2 \text{°C/Вт}$.

Приведенное сопротивление теплопередачи заполнения (см.ниже пункт 7) не ниже $0,8 \text{ м}^2 \cdot \text{°C} / \text{Вт}$. Класс звукоизоляции не ниже Д (25–27 дБА).

7. Заполнения:

Стеклопакет 40мм.:4-14-4-14-4И Символ (1).

Стеклопакет 40мм.:4зак.-14-4-14-4Изак Символ (2).

Пояснение:

- "4зак." - стекло 4мм. закаленное;
- "4Изак." - стекло 4мм. энергосберегающие (низкоэмиссионное) закаленное;
- "4" - стекло 4мм. марки М1
- "4И" - стекло 4мм. энергосберегающие (низкоэмиссионное)

Спецификация на заполнения (габариты, количество стеклопактов и панелей) формируются на стадии кмд.

8. Видимые алюминиевые профили покрыты защитно-декоративными эмалями способом порошковой окраски. Толщина покрытия – не менее 60мкм. Цвет покрытия профилей выполнить в соответствии с колористическим решением внутри и снаружи RAL7016 (согласно таблице RAL classic).

9. Фурнитура оконная:

на окна устанавливается комплекты поворотного открывания. Цвет оконной фурнитуры RAL7016.

10. По периметру примыкания к строительным конструкциям зазоры утепляются монтажной пеной. На монтажную пену наносится герметик снаружи Стиз А, изнутри Стиз В.

11. Сборка алюминиевых конструкций выполняется по чертежам КМД, разрабатываемых организацией – производителем работ, в соответствии с системными решениями.

12. До начала установки витражей генеральной подрядной организации необходимо подготовить проемы. Проемы должны быть ровные, без выбоин, без пыли и песка.

13. При погрузке, перевозке и монтаже конструкций должна быть соблюдена их геометрическая неизменяемость и исключено нарушение покрытия.

14. Крепление монтажных элементов осуществлять последовательно, стеклить рамы допустимо только после полной фиксации монтажного элемента.

15. До начала производства работ произвести геодезическую съемку, уточняющие габариты привязок и размеры, указанные в чертежах. Все несоответствия отражаются в чертежах КМД и согласовываются с авторами проекта и Главным архитектором проекта.

16. Технические решения, принятые в проекте, соответствуют требованиям экологических, санитарно-гигиенических, противопожарных и других норм, действующих на территории РФ и обеспечивают безопасную для жизни и здоровья людей эксплуатацию объекта при соблюдении предусмотренных проектом мероприятий.










Ведомость рабочих чертежей основного комплекта		
Лист	Наименование	Примечание
б/н	Титульный лист ООО "ГАРМОНИЯ"	
б/н	Лист согласования	
1	Общие данные. Ведомость рабочих чертежей основного комплекта. Спецификация витражных окон.	
2	Витражные окна: Ву-2.1, Ву-2.2, Ву-2.3, Ву-2.4, Ву-2.5, Ву-2.6, Ву-2.7, Ву-2.8.	
3	Витражные окна: Ву-2.9, Ву-2.10.1, Ву-2.10.2, Ву-2.11, Ву-2.12, Ву-2.13, Ву-2.14.	
4	Витражные окна: Ву-3.1, Ву-3.2, Ву-3.3, Ву-3.4, Ву-3.5, Ву-3.6, Ву-3.7, Ву-3.8.	
5	Витражные окна: Ву-3.9, Ву-3.10, Ву-3.11, Ву-3.12.1, Ву-3.12.2, Ву-3.12.3, Ву-3.12.4, Ву-3.13.1, Ву-3.13.2, Ву-3.14, Ву-3.15, Ву-3.16.	
6	Узлы 1, 2. Разрезы 2-2, 3-3, 4-4, 5-5, 6-6.	

Спецификация витражных окон 1 этажа.		
Марка	Размер изделий	Всего на корпус, шт.
Vu-2.1	2360x2390h	7
Vu-2.2	2360x2690h	12
Vu-2.3	2360x2990h	10
Vu-2.4	2360x3290h	2
Vu-2.5	2360x3590h	7
Vu-2.6	2360x3890h	2
Vu-2.7	2360x4240h	3
Vu-2.8	2360x4390h	6
Vu-2.9	1460x2390h	1
Vu-2.10.1	1160x2690h	1
Vu-2.10.2	1560x2690h	2
Vu-2.11	1460x2990h	2
Vu-2.12	1160x3590h	1
Vu-2.13	1460x3890h	1
Vu-2.14	1460x4490h	2
Vu-3.1	2360x2690h	7
Vu-3.2	2360x2990h	10
Vu-3.3	2360x3290h	9
Vu-3.4	2360x3590h	6
Vu-3.5	2360x3890h	4
Vu-3.6	2360x4190h	4
Vu-3.7	2360x4540h	7
Vu-3.8	2360x4690h	8
Vu-3.9	1280x2690h	1
Vu-3.10	1460x2690h	1
Vu-3.11	1460x2990h	4
Vu-3.12.1	1460x3290h	5
Vu-3.12.2	1560x3290h	2
Vu-3.12.3	760x3290h	2
Vu-3.12.4	1460x3290h	1
Vu-3.13.1	1460x3590h	2
Vu-3.13.2	1340x3590h	1
Vu-3.14	1440x3890h	2
Vu-3.15	1560x4540h	1
Vu-3.16	1560x4690h	1

						30072020			
						"Первый пусковой комплекс второго этапа строительства многоэтажной жилой застройки по адресу: Московская область, Ленинский муниципальный район, с/п Булатниковское, пос Битца, корпус 4"			
Изм.	Код. уч.	Лист?	док.	Погн.	Дата		Стадия	Лист	Листов
Разраб.	Ланцева Н.А.			07.2020		Светопрзрачные алюминиевые конструкции. Витражные окна 1 этажа	Р	1	6
ГИП	Кириянов А.М.			07.2020					
Провер.	Сафонов С.В.			07.2020		Общие данные. Ведомость рабочих чертежей основного комплекта. Спецификация витражных окон.	ООО ГАРМОНИЯ		

Согласовано

Инв. ? подл. Подп. и дата Взам. инв. ?

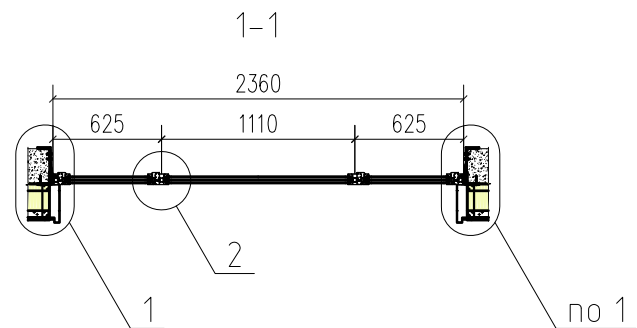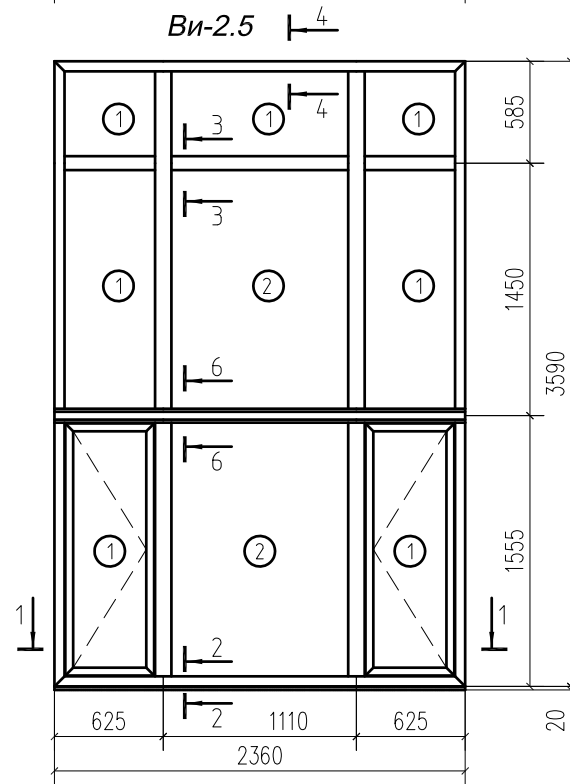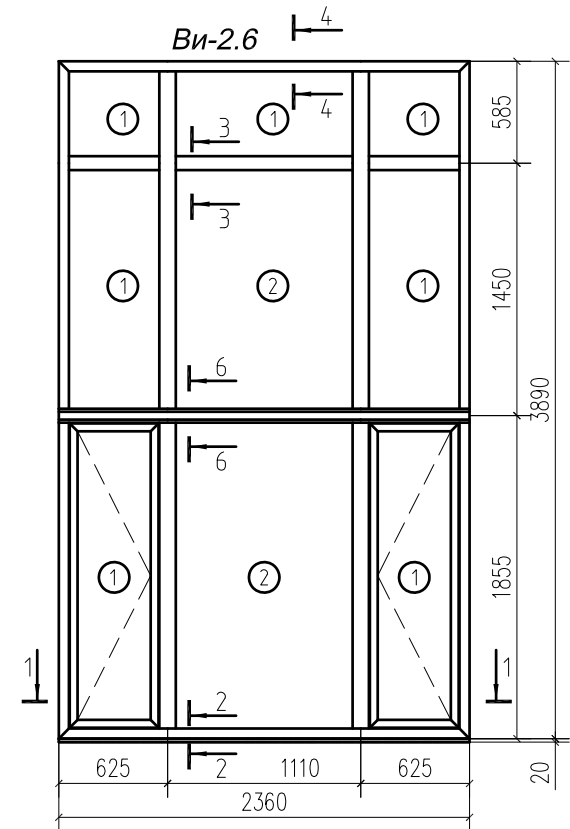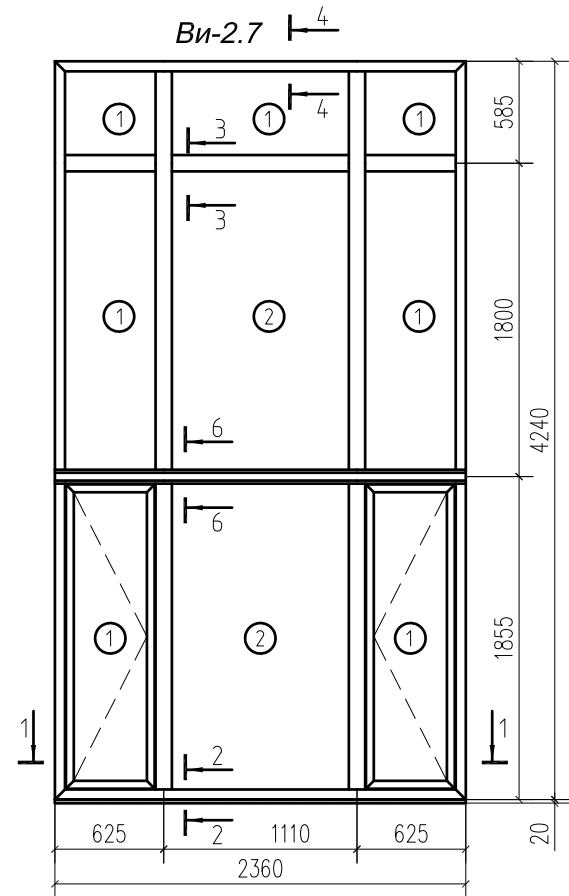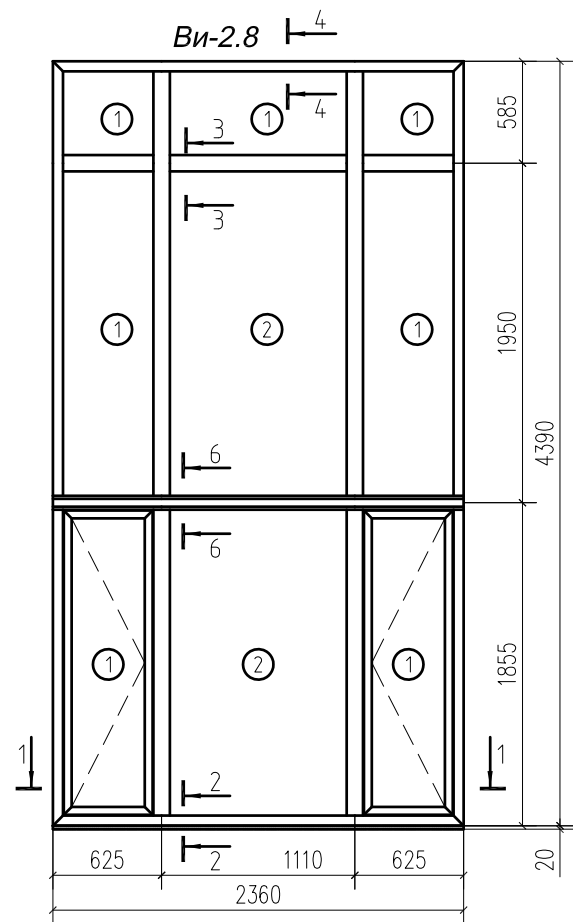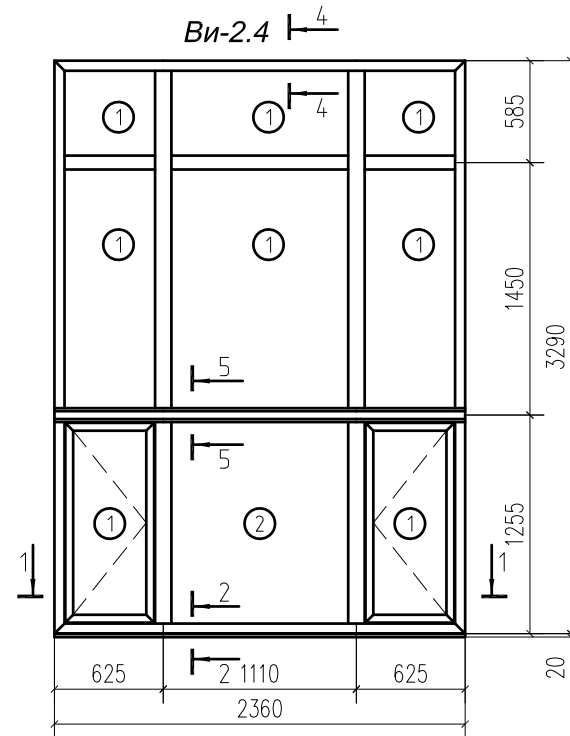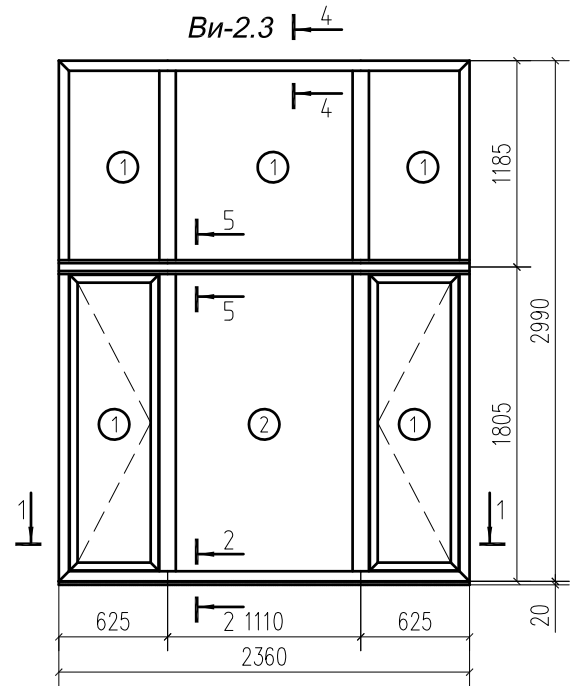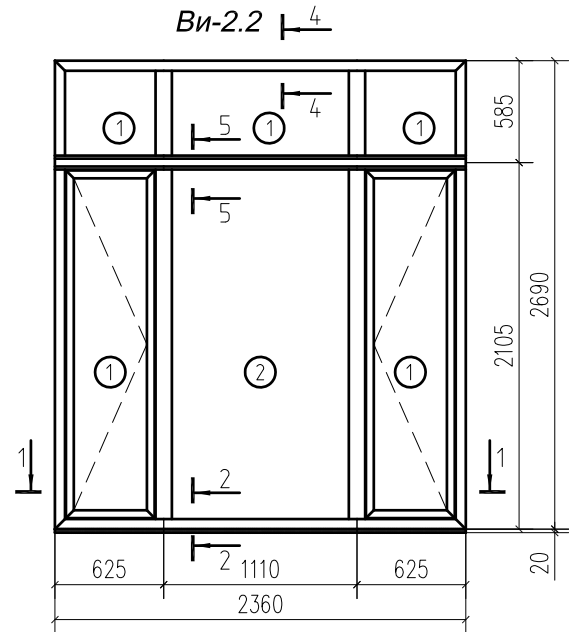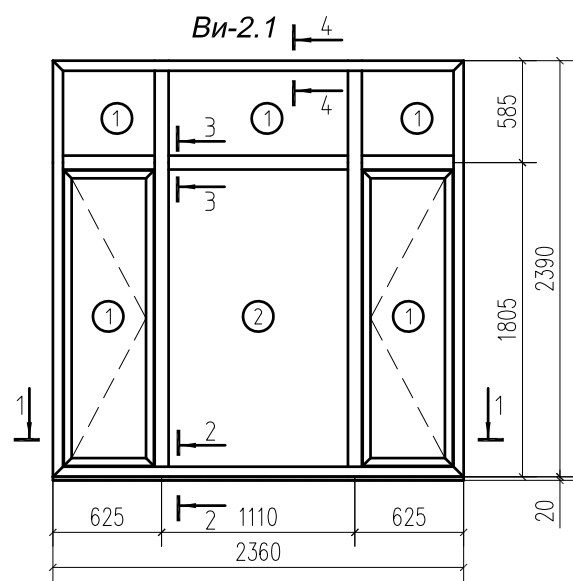

Примечание:









1 - стеклопакет 40мм: 4-14-4-14-4И

2 - стеклопакет 40мм: 4зак-14-4-14-4Изак

						30072020
						"Первый пусковой комплекс второго этапа строительства многоэтажной жилой застройки по адресу: Московская область, Ленинский муниципальный район, с/п Булатниковское, пос Битца, корпус 4"
Изм.	Кол. уч.	Лист?	док	Подп.	Дата	Стация
Разраб.	Ланцева Н.А.				07.2020	Р
ГИП	Кириянов А.М.				07.2020	2
Провер.	Сафонов С.В.				07.2020	6
						Витражные окна: Ви-1, Ви-2.2, Ви-2.3, Ви-2.4, Ви-2.5, Ви-2.6, Ви-2.7, Ви-2.8.
						ООО ГАРМОНИЯ

Формат

А3






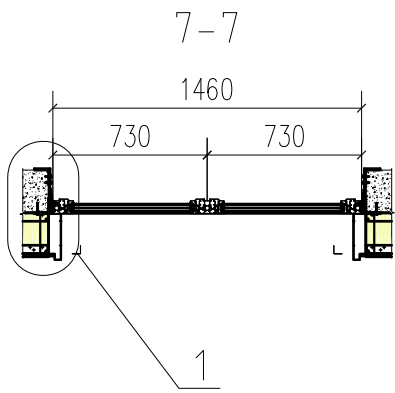
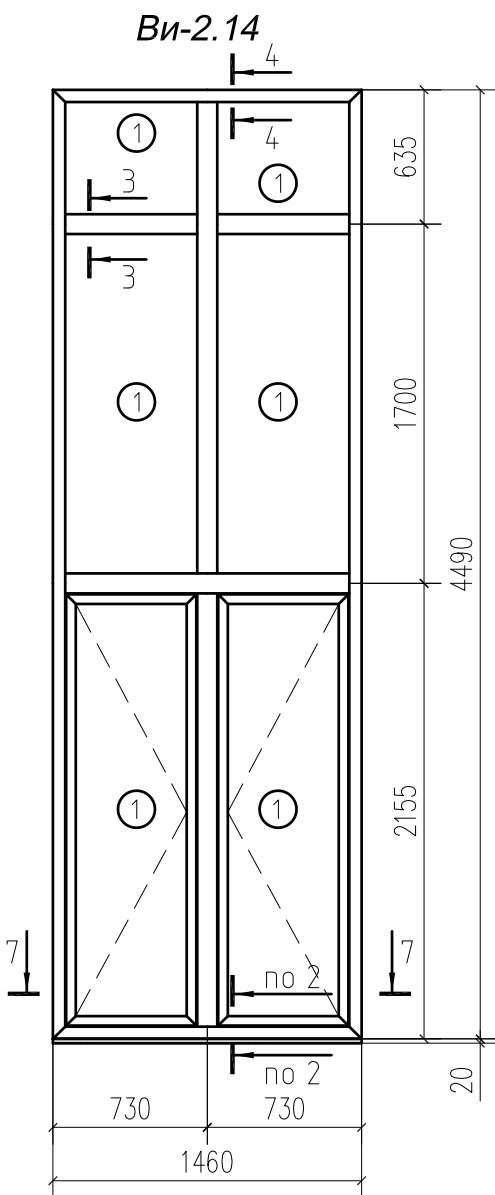
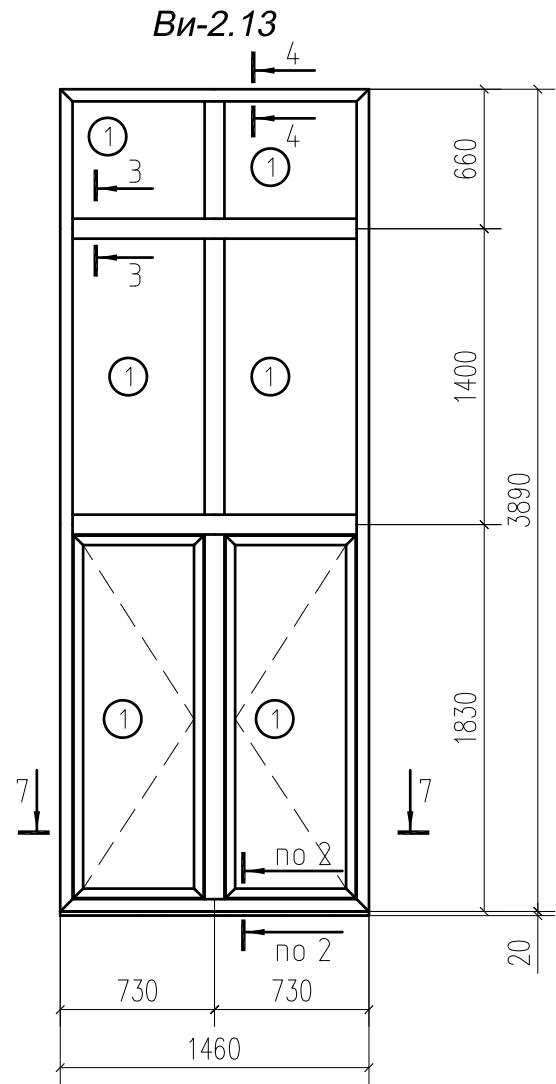
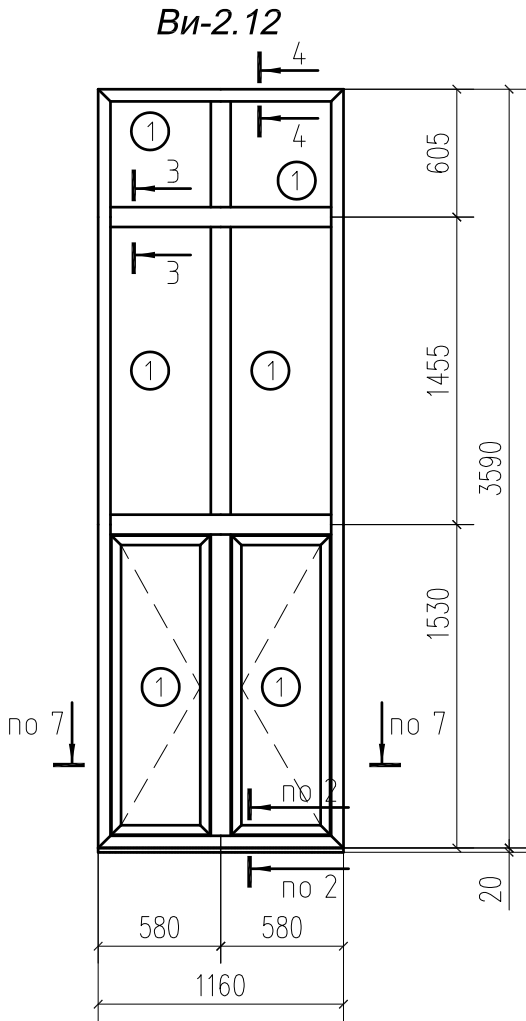
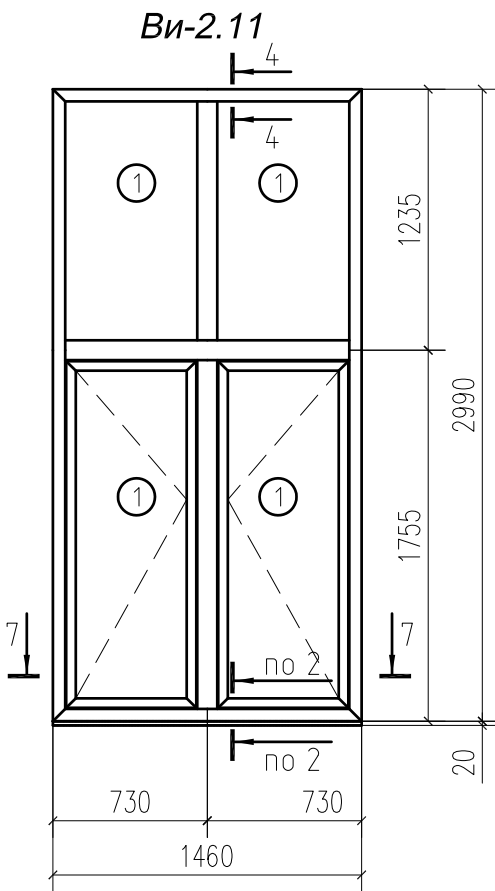
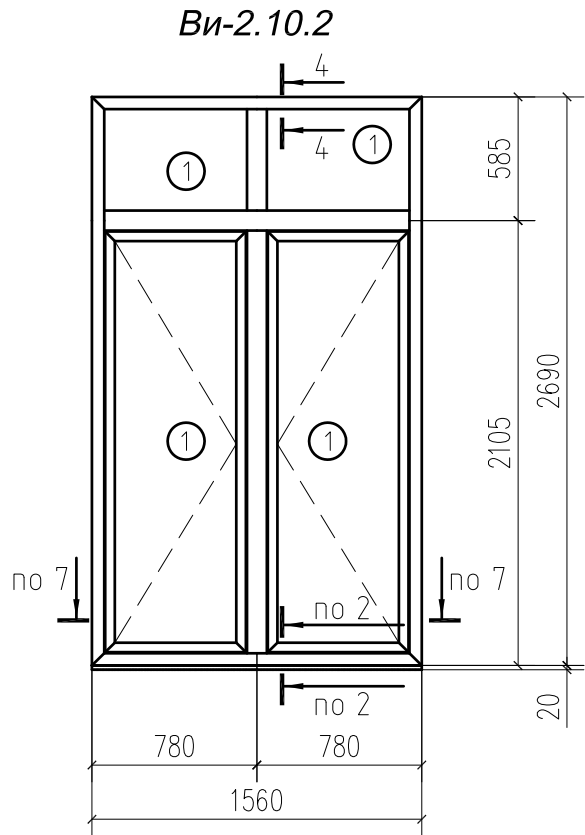
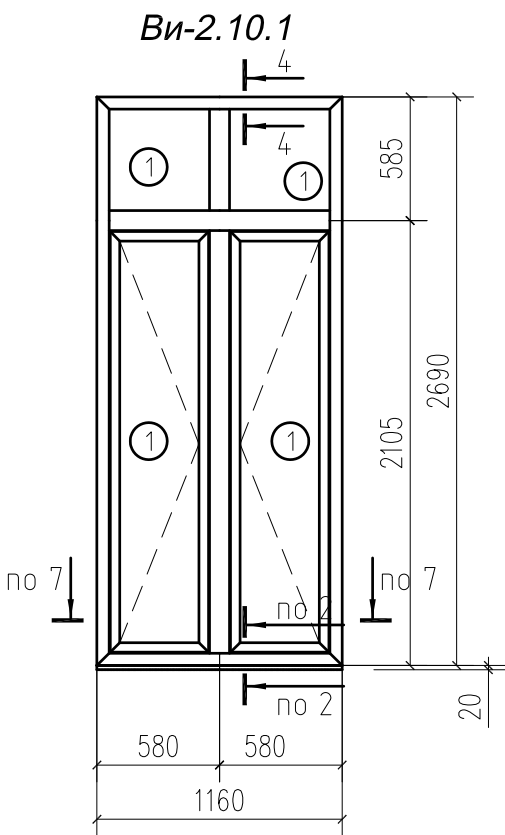
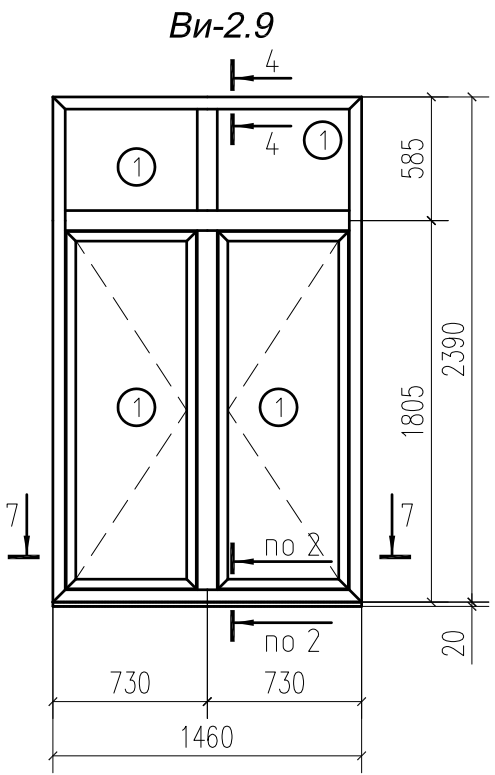


Примечание:
1 – стеклопакет 40мм.: 4-14-4-14-4И
2 – стеклопакет 40мм.: 4зак-14-4-14-4Изак

						30072020		
						"Первый пусковой комплекс второго этапа строительства многоэтажной жилой застройки по адресу: Московская область, Ленинский муниципальный район, с/п Булатниковское, пос Битца, корпус 4"		
Изм.	Кол. уч.	Лист?	док.	Погн.	Дата			
							Стадия	Лист
Разраб.	Ланцева Н.А.			07.2020	Светопрозрачные алюминиевые конструкции. Витражные окна 1 этажа		Р	3
ГИП	Кириянов А.М.			07.2020				6
Провер.	Сафонов С.В.			07.2020	Витражные окна: Ви-2.9, Ви-2.10.1, Ви-2.10.2, Ви-2.11, Ви-2.12, Ви-2.13, Ви-2.14.	ООО ГАРМОНИЯ		

Согласовано

Инв. ? подл. Подп. и дата Взам. инв. ?

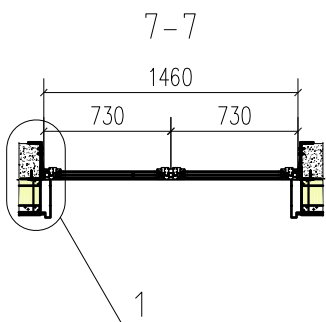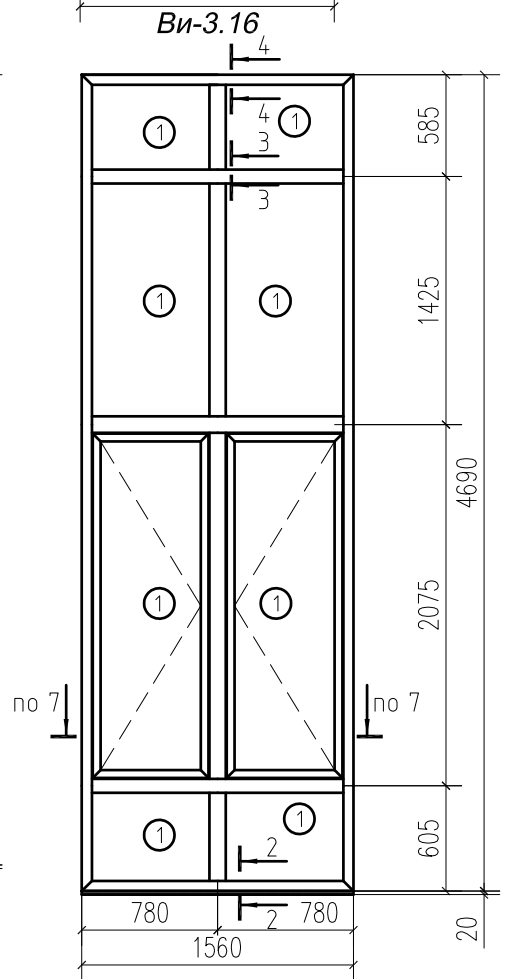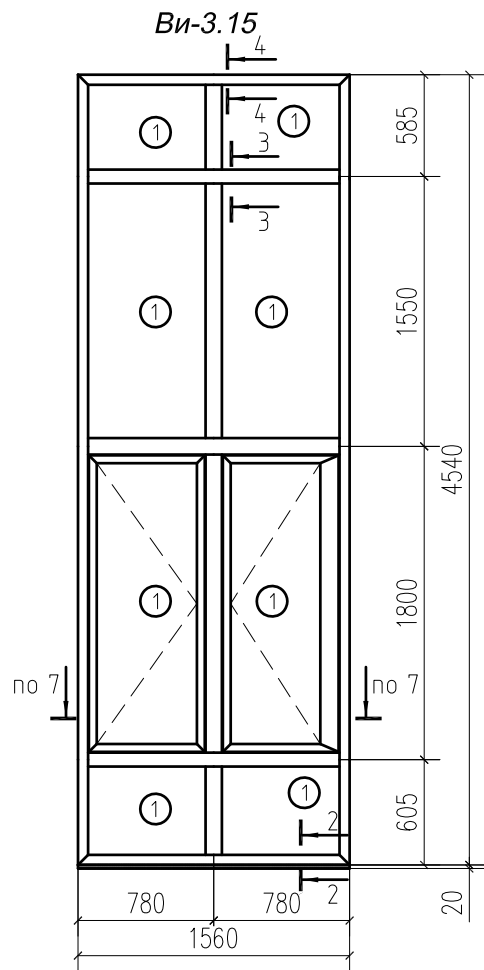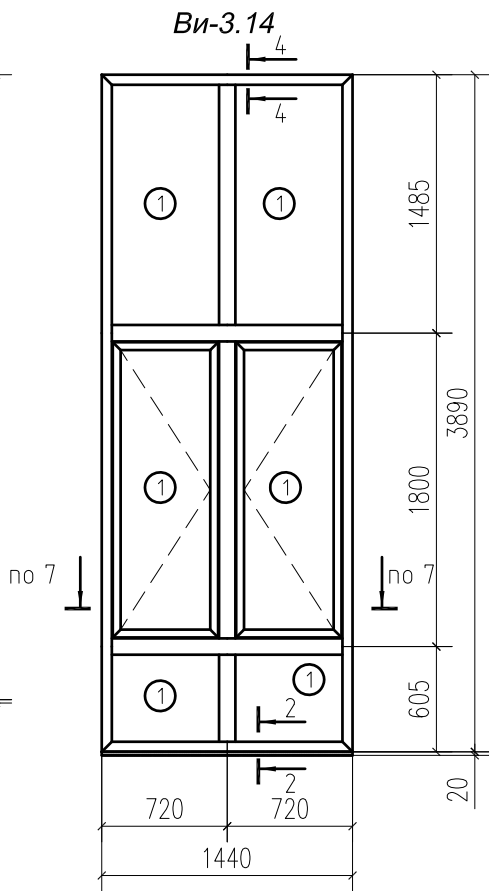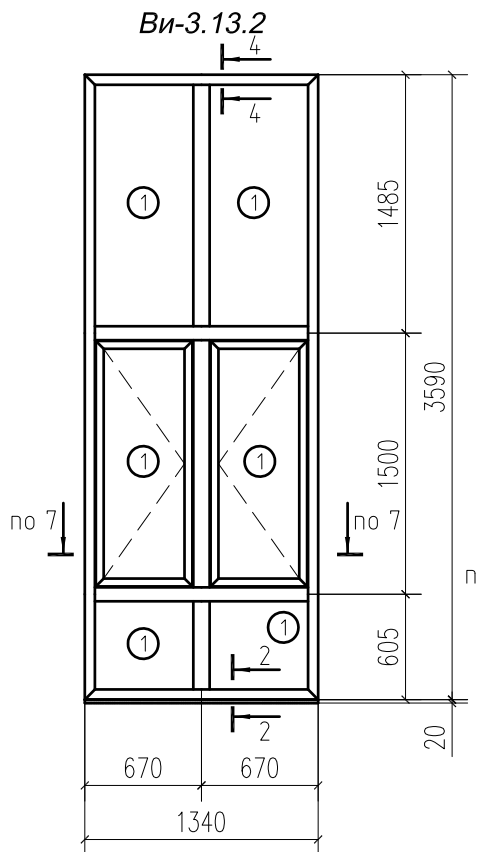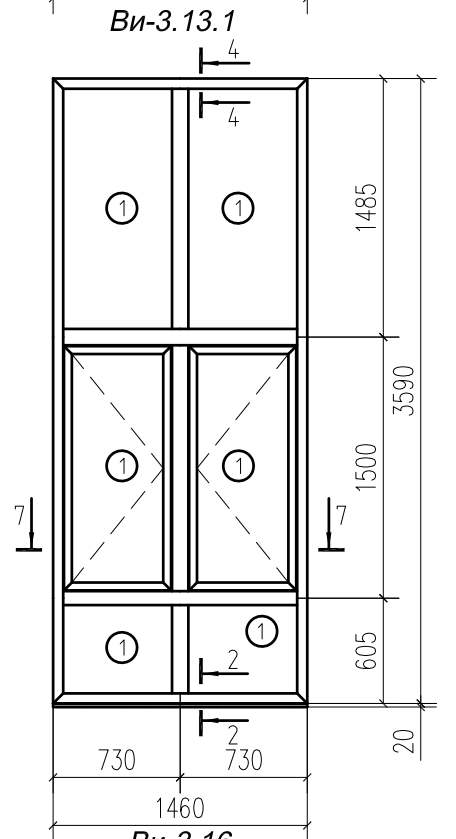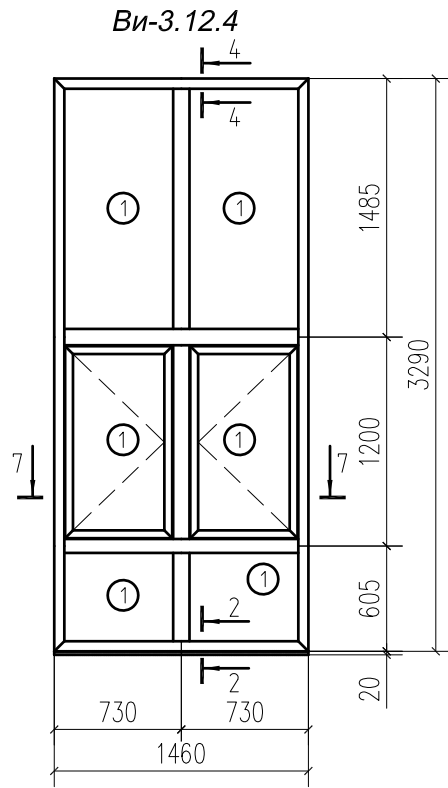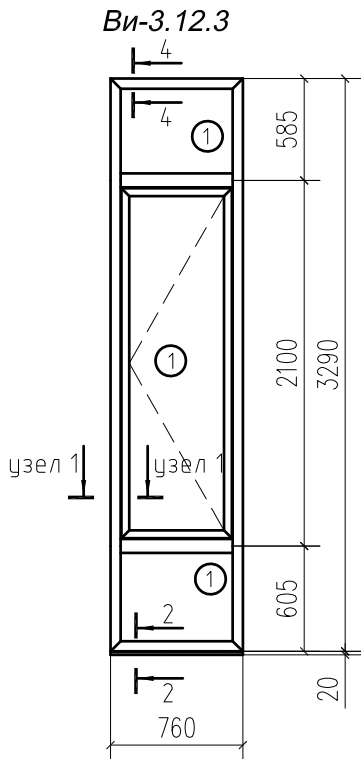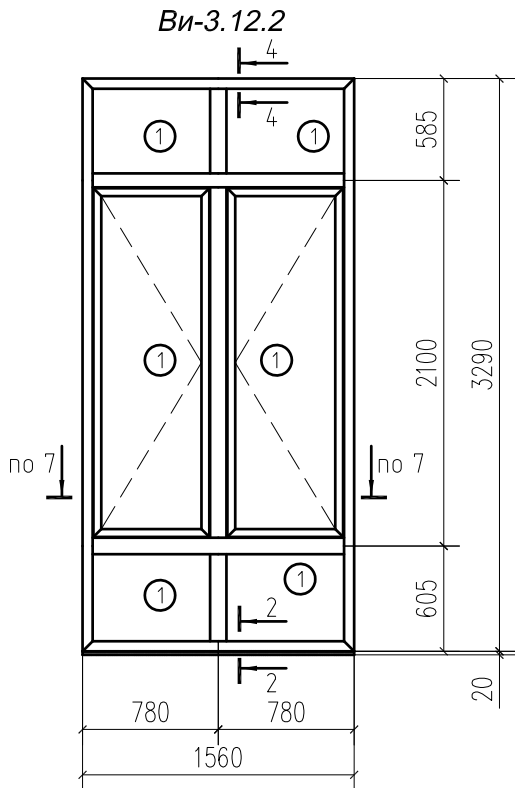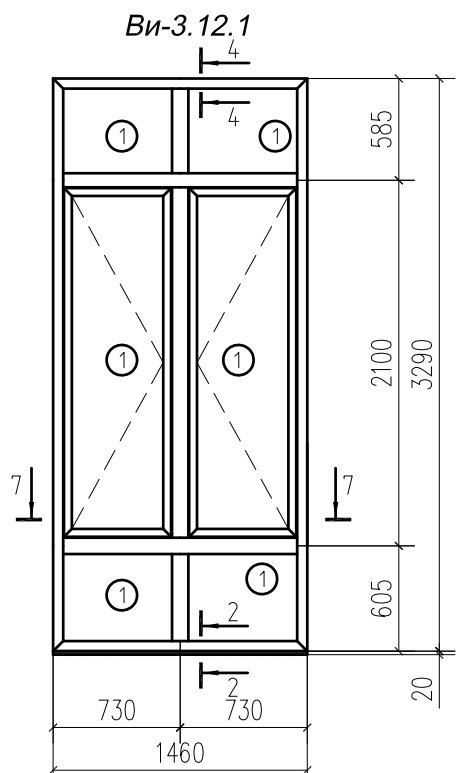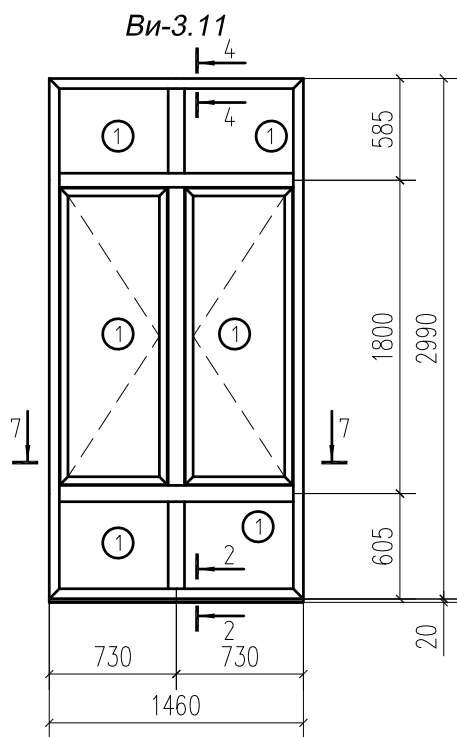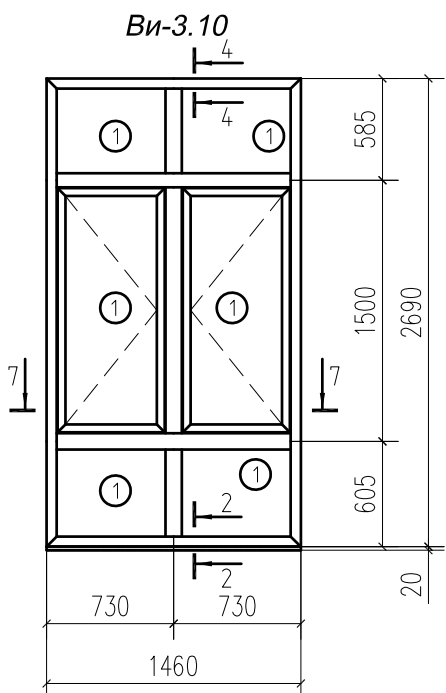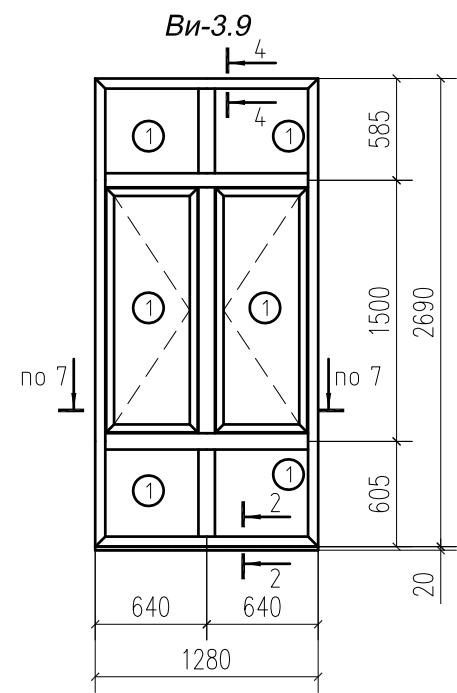


Примечание:
1 - стеклопакет 40мм: 4-14-4-14-4И
2 - стеклопакет 40мм: 4зак-14-4-14-4Изак

Изм.	Кол. уч.	Лист?	док.	Погн.	Дата
Разраб.	Ланцева Н.А.				07.2020
ГИП	Кириянов А.М.				07.2020
Провер.	Сафонов С.В.				07.2020

30072020			
"Первый пусковой комплекс второго этапа строительства многоэтажной жилой застройки по адресу: Московская область, Ленинский муниципальный район, с/п Булатниковское, пос. Битца, корпус 4"			
Светопрзрачные алюминиевые конструкции. Витражные окна 1 этажа	Стадия	Лист	Листов
	Р	5	6
Витражные окна: Ви-3.9, Ви-3.10, Ви-3.11, Ви-3.12.1, Ви-3.12.2, Ви-3.12.3, Ви-3.12.4, Ви-3.13.1, Ви-3.13.2, Ви-3.14, Ви-3.15, Ви-3.16		ООО ГАРМОНИЯ	

Согласовано

Инв. ? подл. Подп. и дата Взам. инв. ?

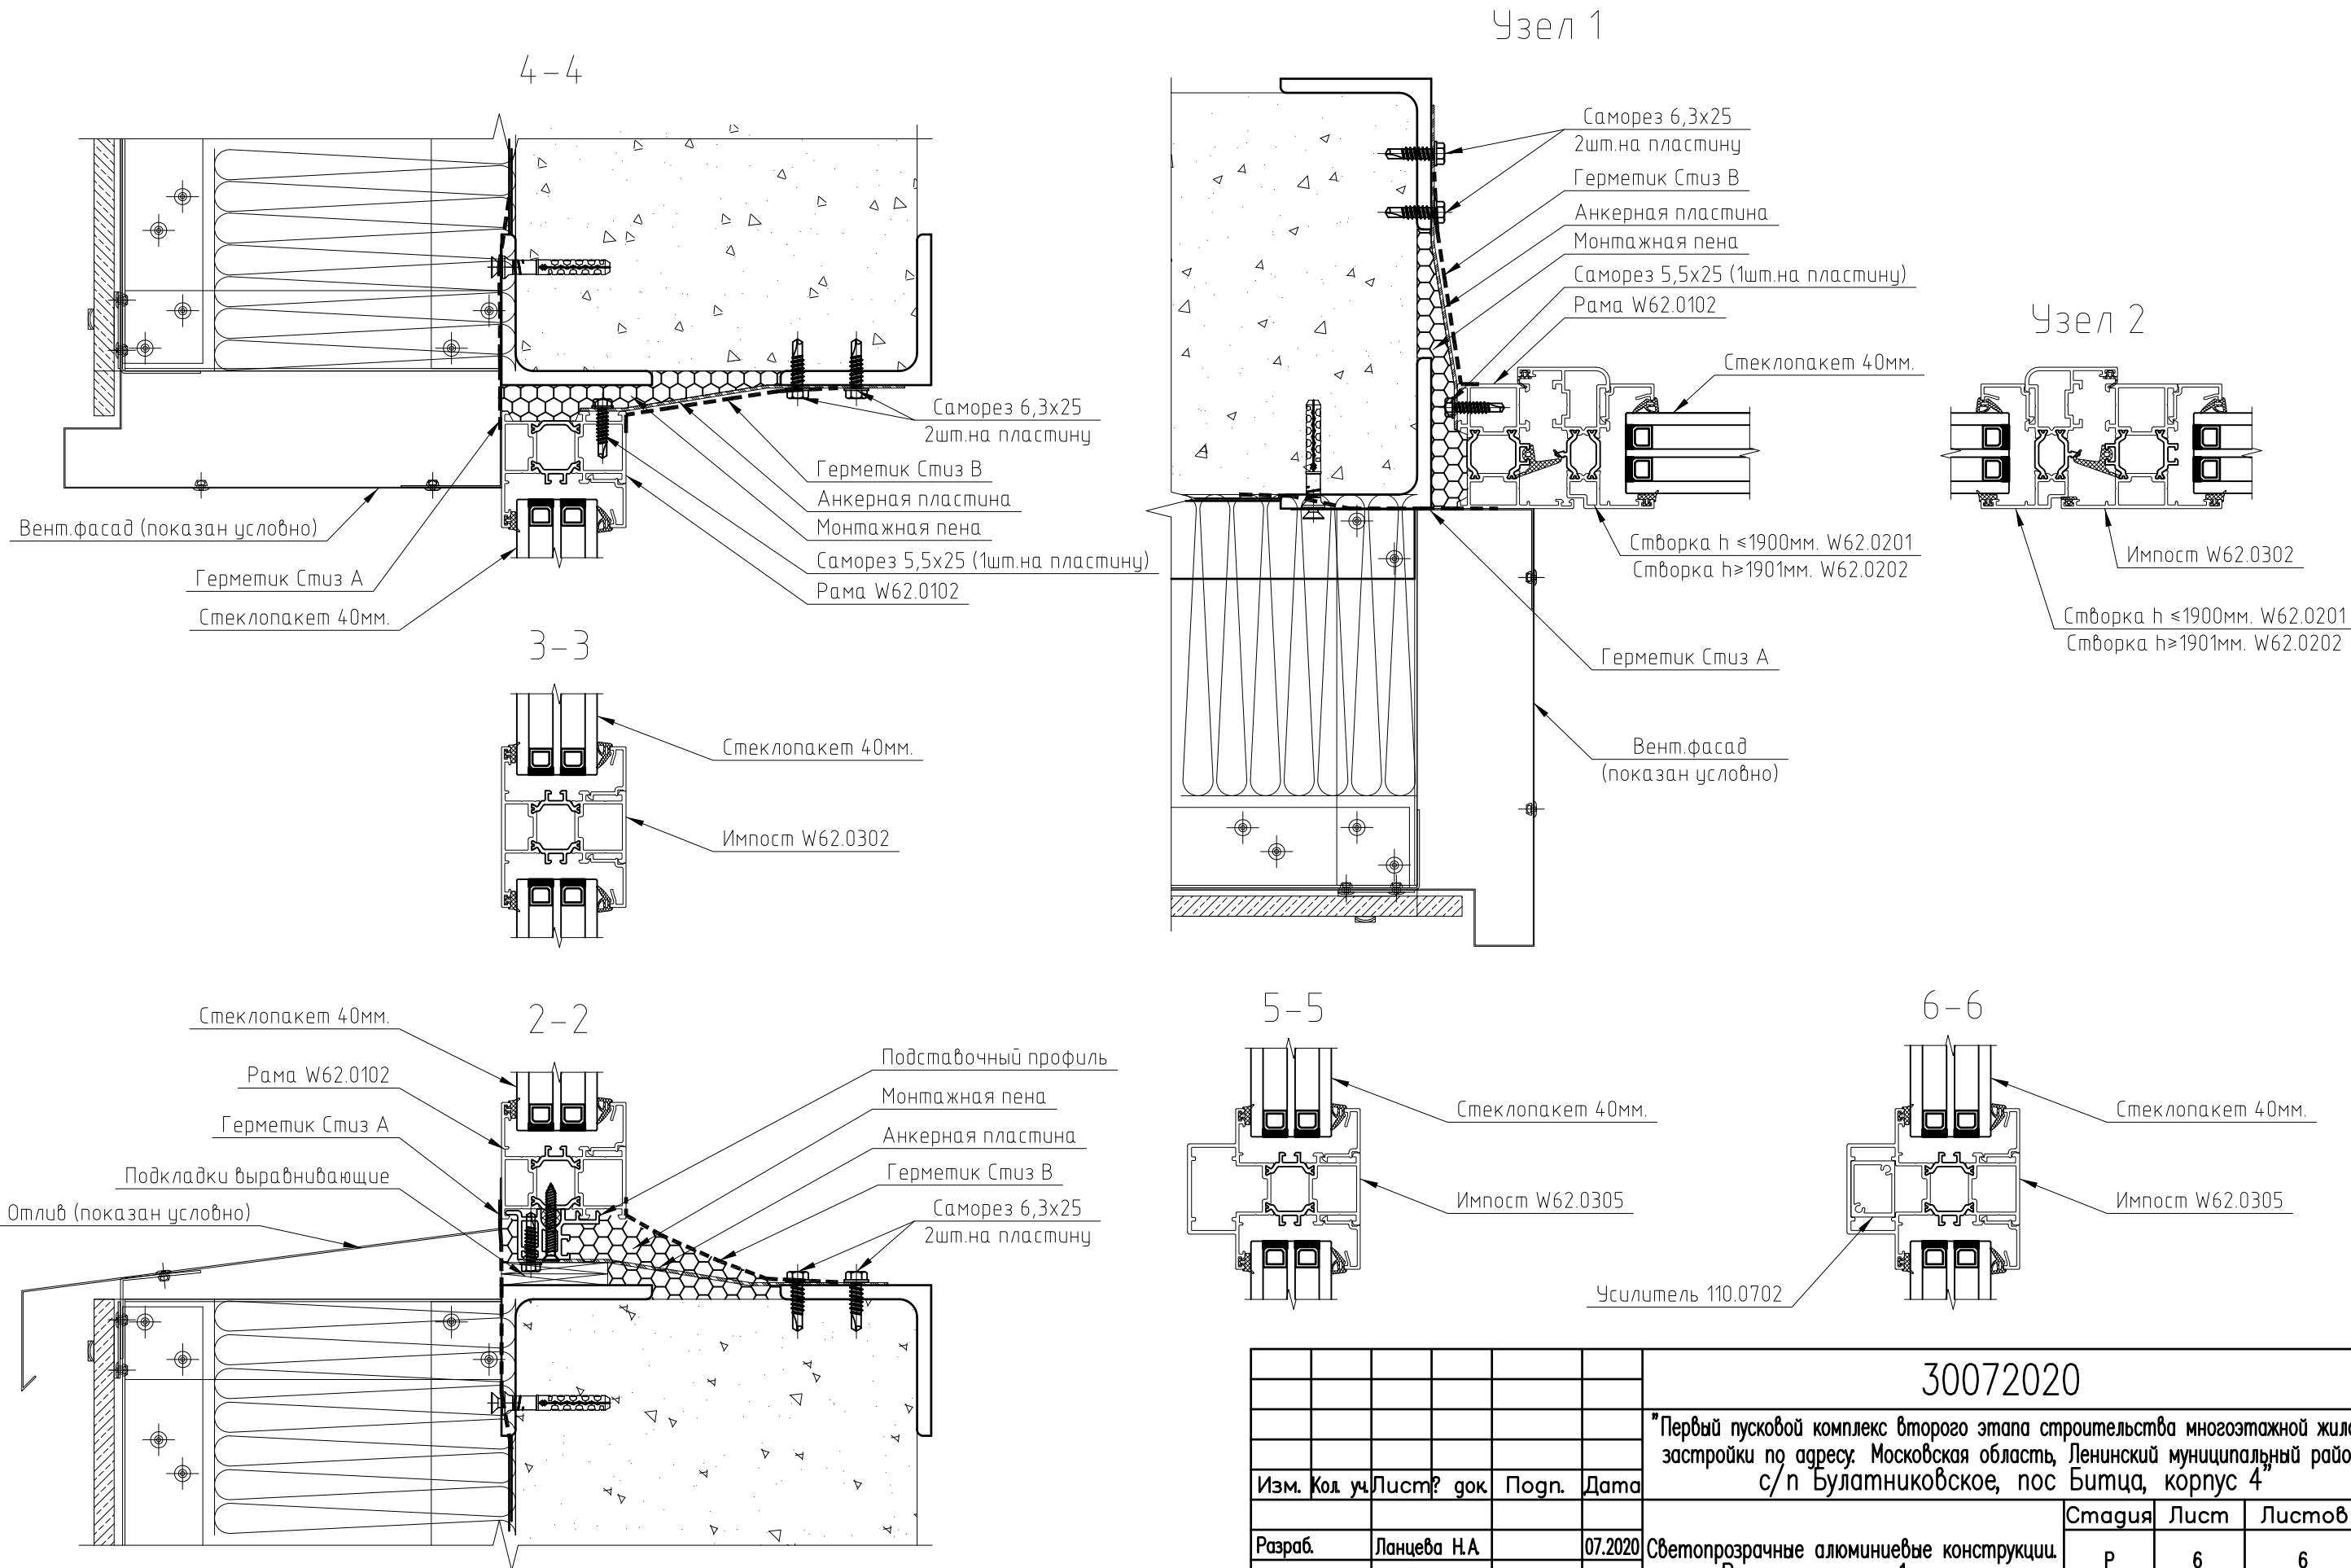

						30072020		
						"Первый пусковой комплекс второго этапа строительства многоэтажной жилой застройки по адресу: Московская область, Ленинский муниципальный район, с/п Булатниковское, пос Битца, корпус 4"		
Изм.	Кол. уч.	Лист?	док	Подп.	Дата	Светопрозрачные алюминиевые конструкции. Витражные окна 1 этажа	Стадия	Лист
Разраб.	Ланцева Н.А.			07.2020			Р	6
ГИП	Кириянов А.М.			07.2020				6
Провер.	Сафонов С.В.			07.2020				
						Узлы 1,2. Разрезы 2-2, 3-3, 4-4, 5-5, 6-6.	ООО ГАРМОНИЯ	