

ООО «МАРКА ПОЛА»
ИНН 7702762718 ОГРН 1117746402355

Договор оказания услуг № 23-11 КМД от 01.10.2022г.

Заказчик – АО «Ал Д Мега Лаб»

«Многофункциональная комплексная жилая застройка, Квартал 2, корпус
1,2,3,4,5,6 по адресу: Москва, СЗАО, внутригородская территория
муниципальный округ Хорошево-Мневники, ул. Нижние Мневники»

КОНСТРУКТОРСКАЯ ДОКУМЕНТАЦИЯ

Чертежи КМД Алюминиевых светопрозрачных конструкций. Витражи.

Генеральный директор



Бирюкова Т. С.

2022

Пояснительная записка

В соответствии с заданием заказчика была разработана рабочая документация по чертежам КМД для алюминиевых балконных дверей.


В состав рабочей документации входят:

1. КМД - Общий вид и сечения алюминиевых витражей.
2. КМД - Узлы сборки и обработки.

При монтаже необходимо пользоваться указаниями соответствующего тома конструкторской документации.


Наименование услуг	Сроки выполнения работ	Кол-во	Ед. изм
Разработка чертежей раздела КМД (Витражи CW50) для объекта " Многофункциональная комплексная жилая застройка, Квартал 2, корпус 1,2,3,4,5,6 по адресу: Москва, СЗАО, внутригородская территория муниципальный округ Хорошево-Мневники, ул. Нижние Мневники "	06.03.2023	4450,00	кв.м.

Угловой витраж В-1 (развертка).
Кол-во: 19 шт.
S=10,97 м.кв.

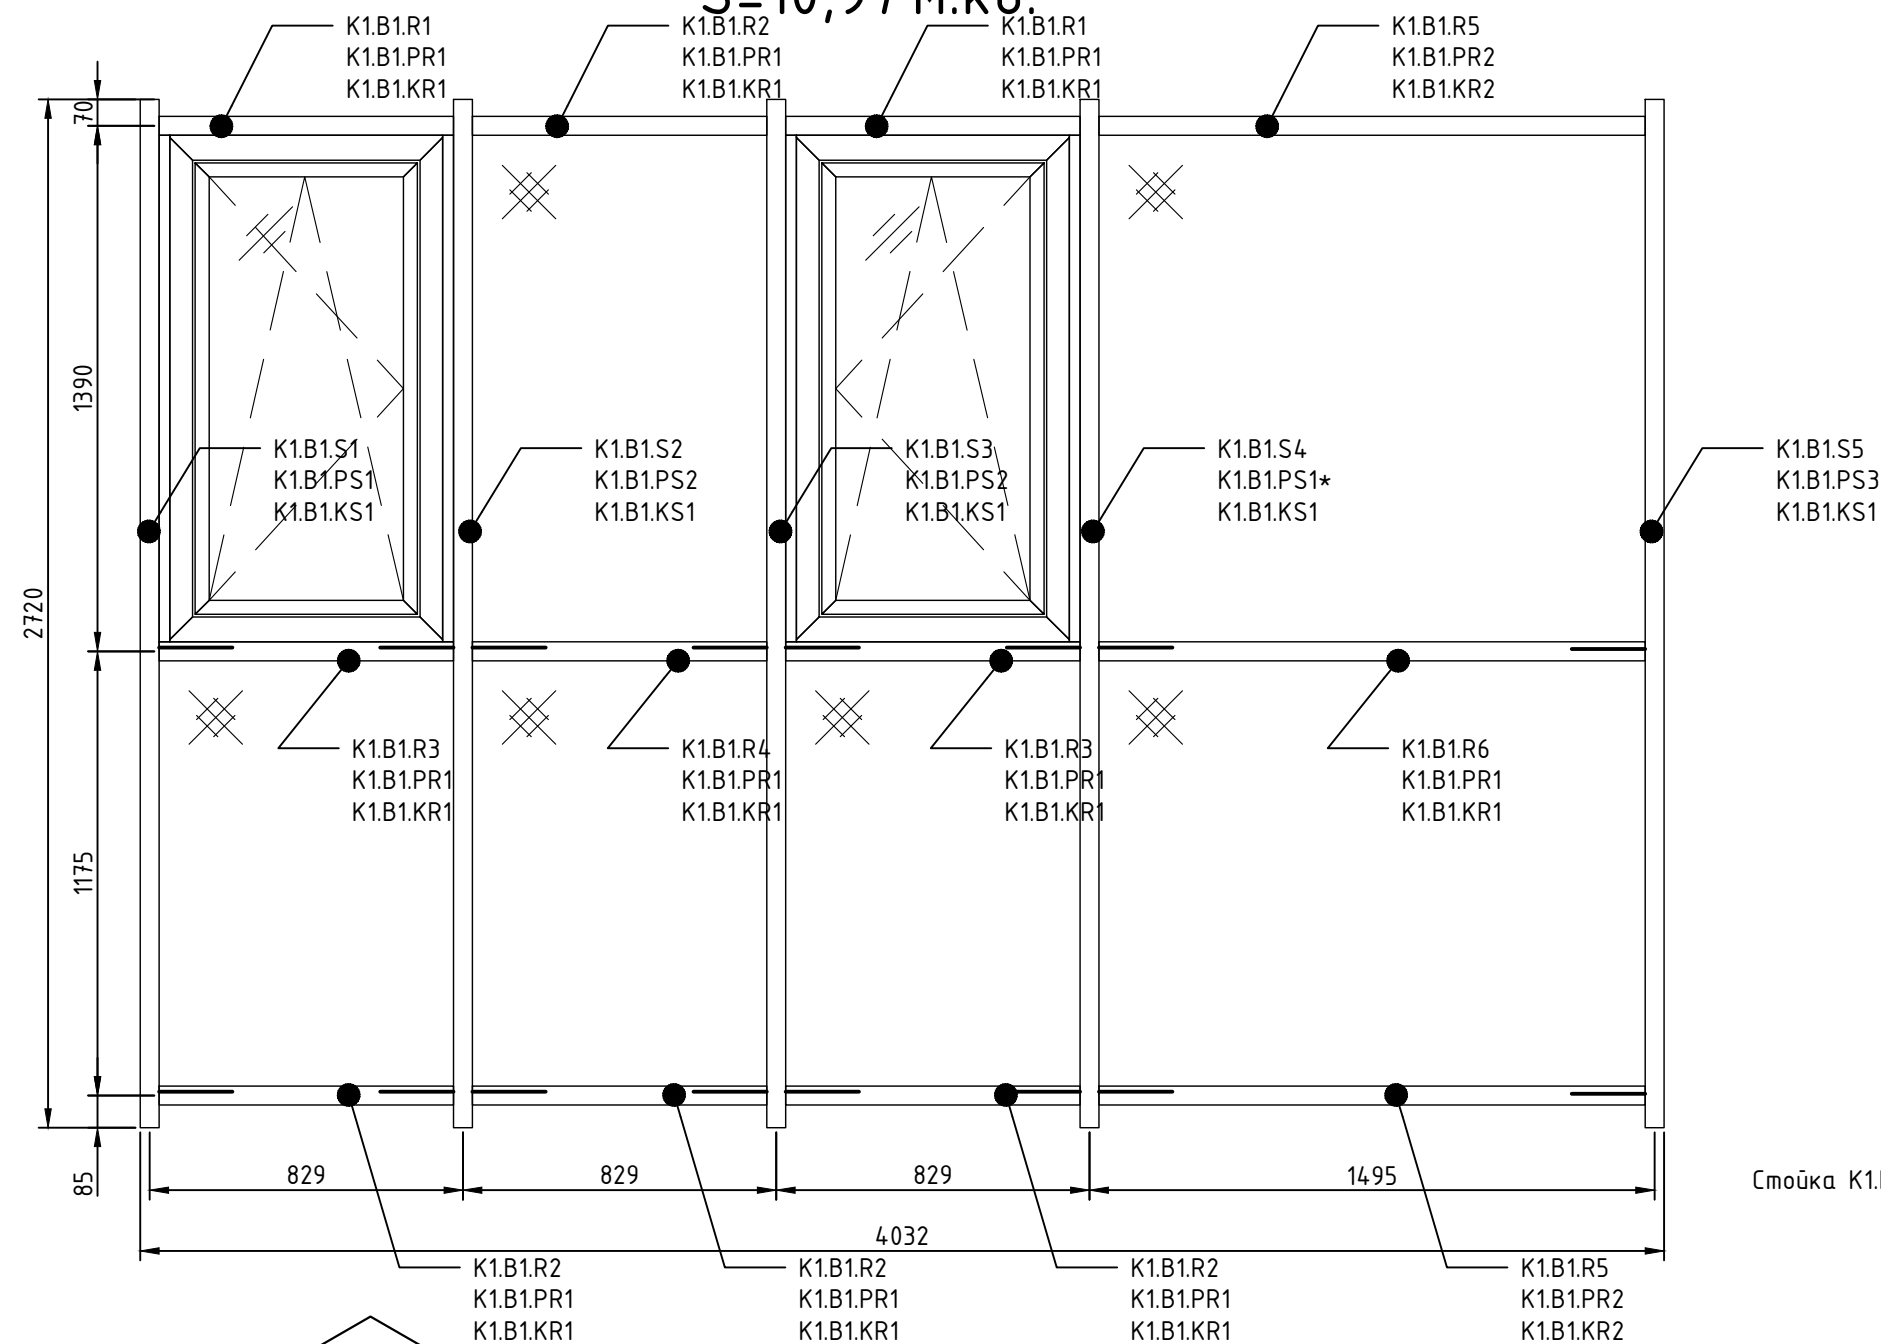


Заполнение термовставки - 0809892 + 0809893.
Под прижимы битуловая лента - 0849711.
Прижимной саморез:
- прижимы PS1, PS2, PS1* - Ø6,3x67мм - 0535476
- прижимы PS3, PR1, PR2 - Ø6,3x64мм - 0535475

Ригеля крепить саморезом Ø4,2x12,7мм - 0525317

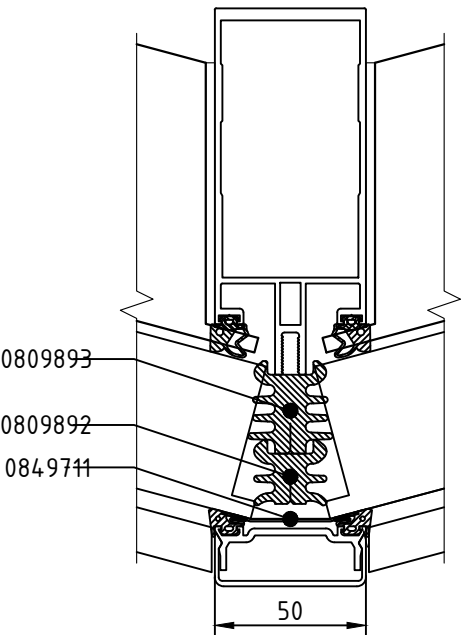

Стойка K1.B1.S4 устанавливается со стоечным сухарем 0345593 во всю длину.

Согласовано	ГАП	ГИП
	Взам. инв. N	Подп. и дата
Инв. N подл.	Взам. инв. N	Подп. и дата

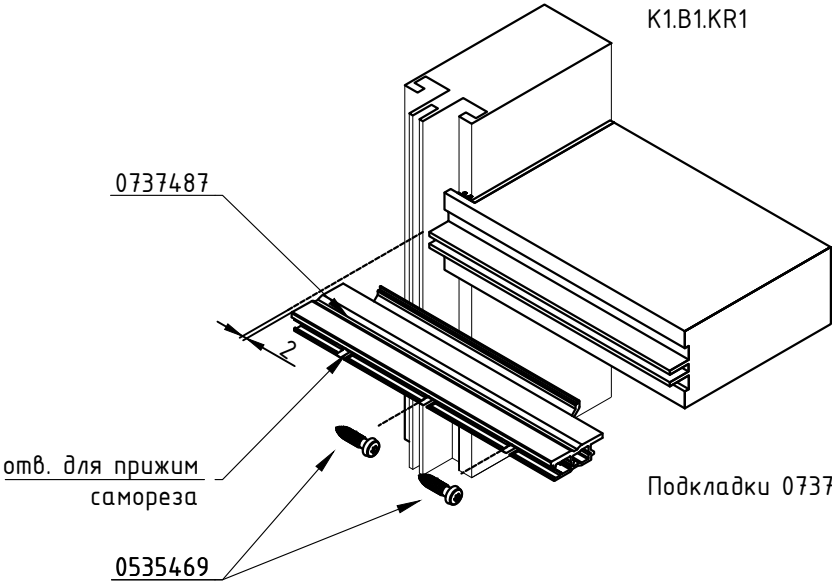


Подкладки 0737487 напилить из профиля 0340385.

						Остров 2 К1			
						" Многофункциональная комплексная жилая застройка , квартал 2, корпус 1, 2, 3, 4, 5, 6 по адресу : г . Москва , внутригородская территория муниципальный округ Хорошёво -Мнёвники."			
Изм.	Кол.уч.	Лист	№ док.	Подп.	Дата	Светопрозрачные конструкции	Стадия	Лист	Листов
Разраб.	Бирюкова				06.23		Р	1	120
Проверил									
Н.контр.						Угловой витраж В-1	ООО "МАРКА ПОЛА"		
Т.контр.									
Утв.									

Угловой витраж В-2 (развертка).

Кол-во: 1 шт.

S=11,77 м.кв.

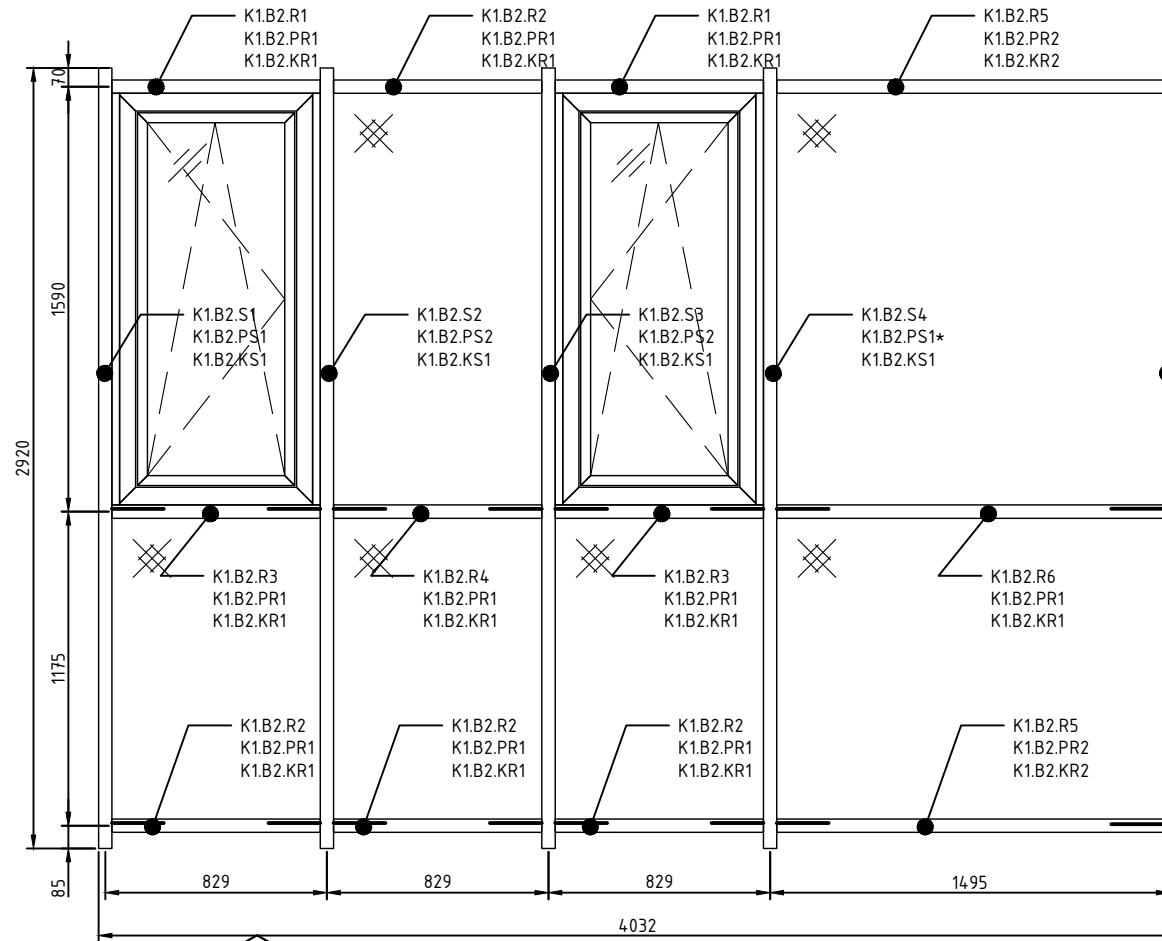


Заполнение термовставки - 0809892 + 0809893.

Под прижимы бутиловая лента - 0849711.


Прижимной саморез:

- прижимы PS1, PS2, PS1* - Ø6,3x67мм - 0535476
- прижимы PS3, PR1, PR2 - Ø6,3x64мм - 0535475

Ригеля крепить саморезом Ø4,2x12,7мм - 0525317

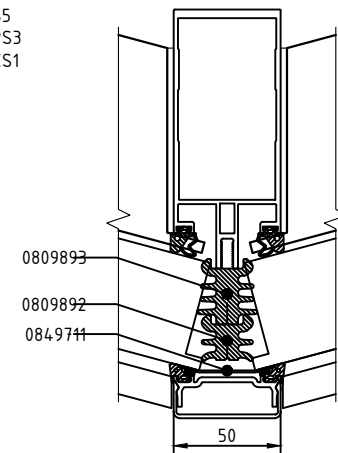

Стойка K1.B2.S4 устанавливается со стоечным сухарем 0345593 во всю длину.

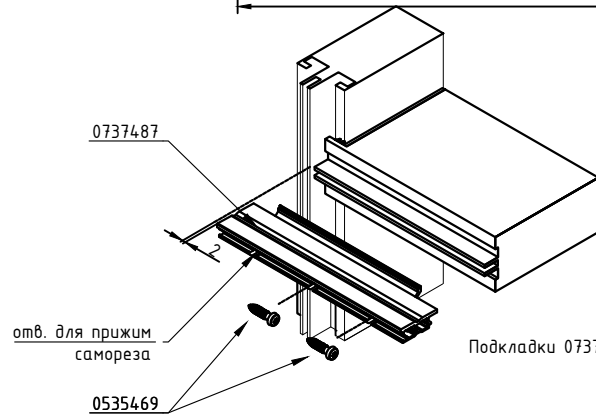

Подкладка 0737487

Подкладки 0737487 напилить из профиля 0340385.

						Остров 2 К1			
						" Многофункциональная комплексная жилая застройка , квартал 2, корпус 1, 2, 3, 4, 5, 6 по адресу : г . Москва , внутригородская территория муниципальный округ Хорошёво - Мнёвники."			
Изм.	Кол.уч.	Лист	№ док.	Подп.	Дата	Светопрозрачные конструкции	Стадия	Лист	Листов
Разраб.	Бирюкова				06.23		Р	2	
Проверил									
Н. контр.						Угловой витраж В-2		ООО "МАРКА ПОЛА"	
Т. контр.									
Утв.									


Копировал

Согласовано	ГАП	Взам. инв. №
	ГИП	
Инв. № подл.	Подп. и дата	Взам. инв. №

Угловой витраж В-3 (развертка).


Кол-во: 19 шт.

S=10,05 м.кв.

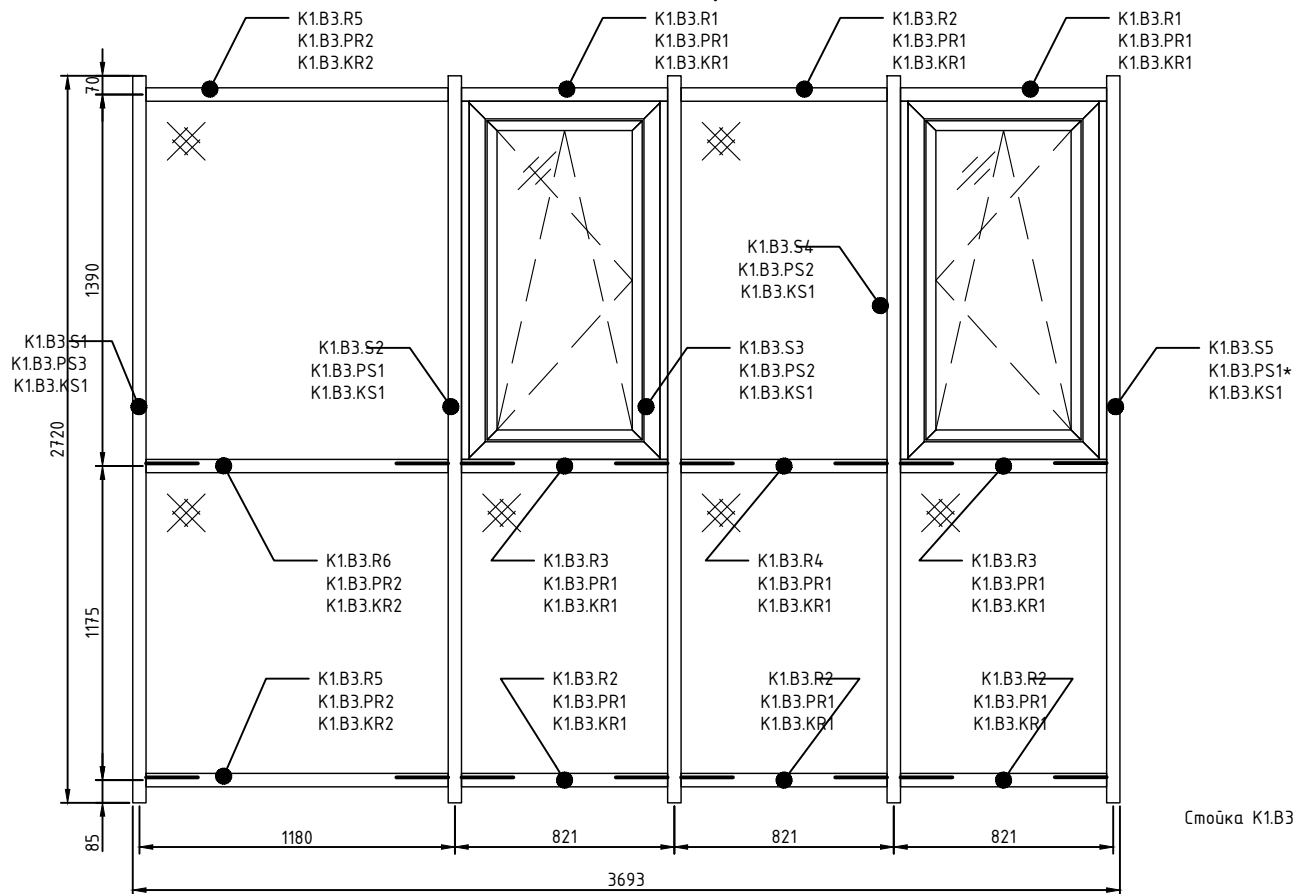


Заполнение термовставки - 0809892 + 0809893.
Под прижимы бутиловая лента - 0849711.
Прижимной саморез:
- прижимы PS1, PS2, PS1* - Ø6,3х67мм - 0535476
- прижимы PS3, PR1, PR2 - Ø6,3х64мм - 0535475

Ригеля крепить саморезом Ø4,2х12,7мм - 0525317

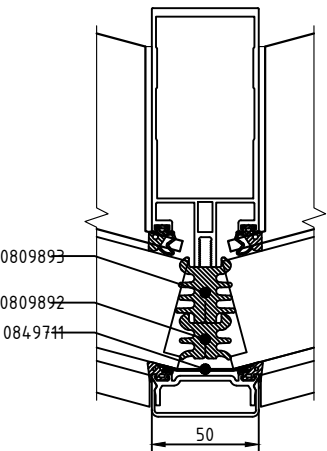

Стойка K1.B3.S2 устанавливается со стоечным сухарем 0345593 во всю длину.

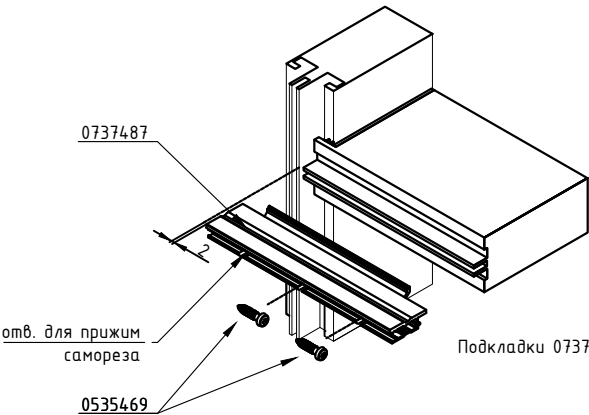

Подкладки 0737487 напилить из профиля 0340385.

Подкладка 0737487

						Остров 2 К1			
						" Многофункциональная комплексная жилая застройка , квартал 2, корпус 1, 2, 3, 4, 5, 6 по адресу : г . Москва , внутригородская территория муниципальный округ Хорошево –Мнёвники."			
Изм.	Кол.уч.	Лист	№ док	Подп.	Дата	Светопрозрачные конструкции	Стадия	Лист	Листов
Разраб.	Бирюкова				06.23		Р	3	
Проверил									
Н.контр.						Угловой витраж В-3	ООО "МАРКА ПОЛА"		
Т.контр.									
Утв.									


Копировал

Согласовано					
ГАП					
ГИП					
Инв. N подл.	Подп. и дата	Взам. инв. N			

Угловой витраж В-4 (развертка).

Кол-во : 1 шт.

S=10,97 м.кв.

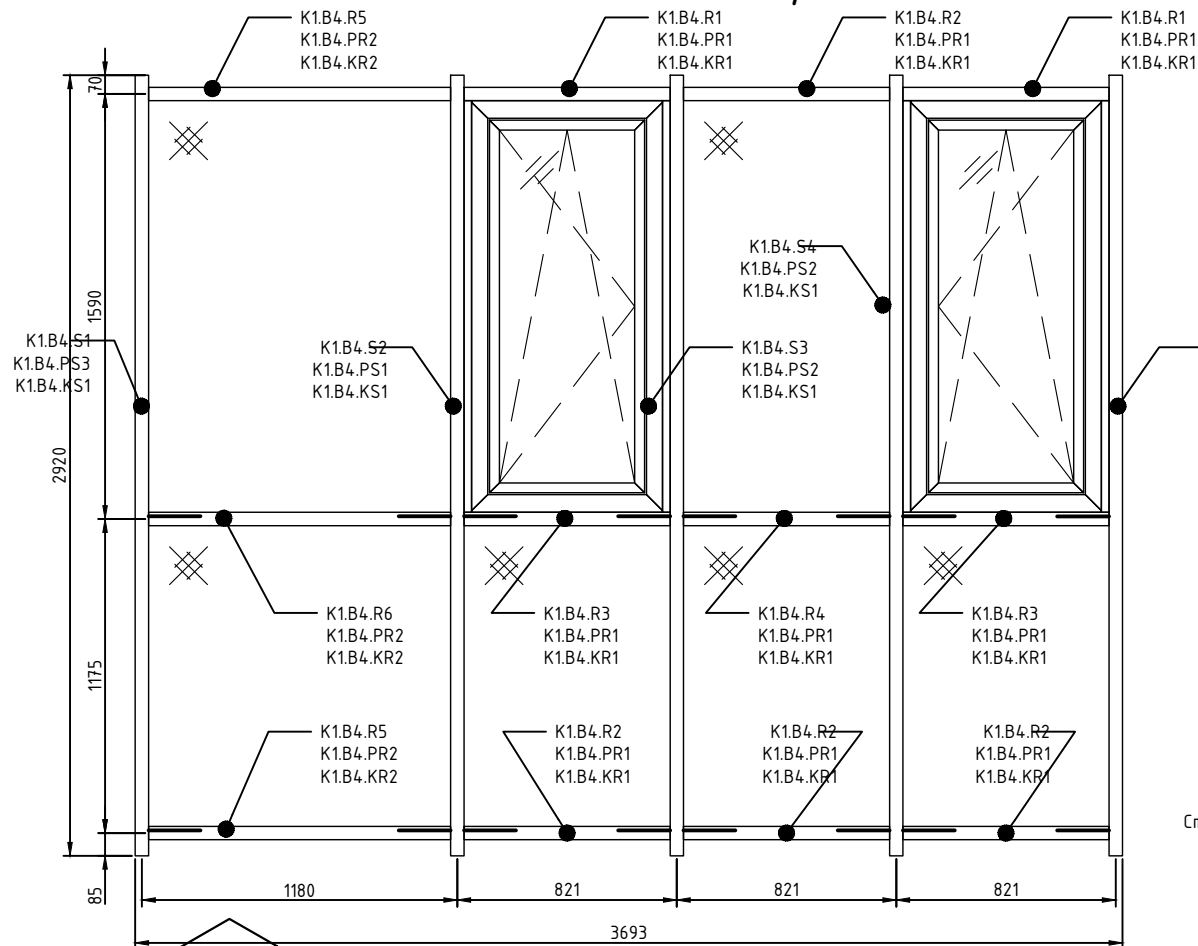


Заполнение термовставки - 0809892 + 0809893.

Под прижимы дупиловая лента - 0849711.


Прижимной саморез:

- прижимы PS1, PS2, PS1* - Ø6,3x67мм - 0535476
- прижимы PS3, PR1, PR2 - Ø6,3x64мм - 0535475

Резиля крепить саморезом Ø4,2x12,7мм - 0525317

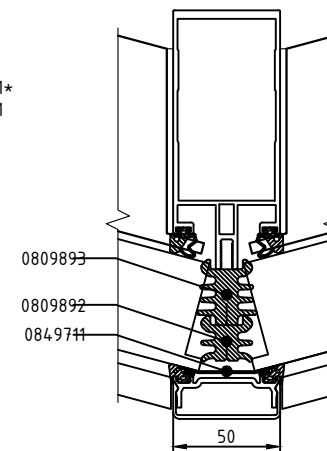

Стойка K1.B4.S2 устанавливается со стоечным сухарем 0345593 во всю длину.

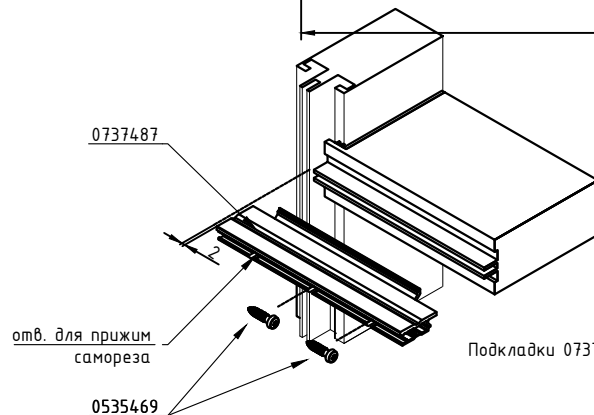

Подкладка 0737487

Подкладки 0737487 напилить из профиля 0340385.

						Остров 2 К1			
						" Многофункциональная комплексная жилая застройка , квартал 2, корпус 1, 2, 3, 4, 5, 6 по адресу : г . Москва , внутригородская территория муниципальный округ Хорошёво -Мнёвники."			
Изм.	Кол.уч.	Лист	№ док.	Подп.	Дата	Светопрзрачные конструкции	Стадия	Лист	Листов
Разраб.	Бирюкова				06.23		Р	4	
Проверил									
Н. контр.									
Т. контр.						Угловой витраж В-4		ООО "МАРКА ПОЛА"	
Утв.									


Копировал

Согласовано	ГАП	ГИП
Инв. N подл.	Подп. и дата	Взам. инв. N

Угловой витраж В-5 (развертка).

Кол-во: 19 шт.

S=10,90 м.кв.

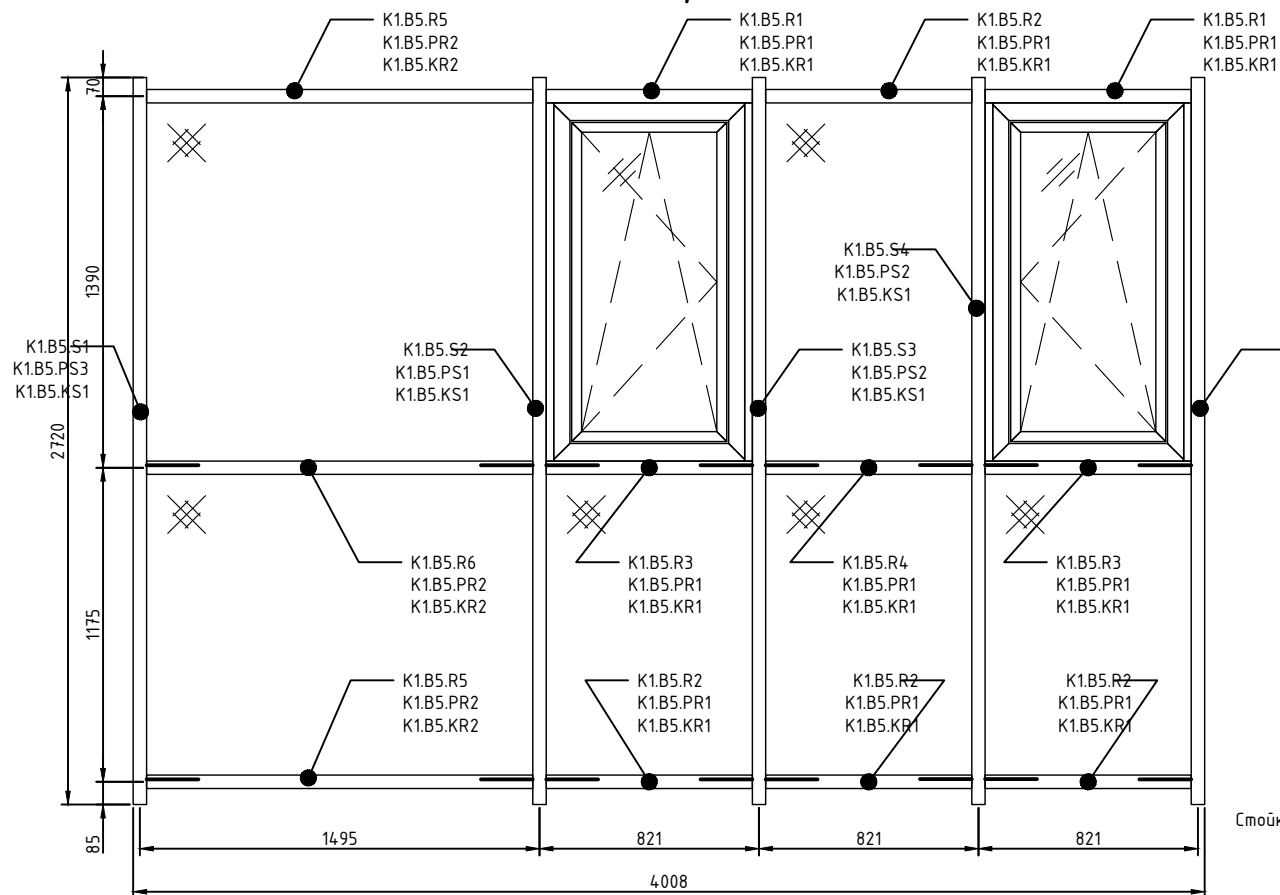


Заполнение термовставки - 0809892 + 0809893.

Под прижимы бутиловая лента - 0849711.


Прижимной саморез:

- прижимы PS1, PS2, PS1* - Ø6,3x67мм - 0535476
- прижимы PS3, PR1, PR2 - Ø6,3x64мм - 0535475

Ригеля крепить саморезом Ø4,2x12,7мм - 0525317

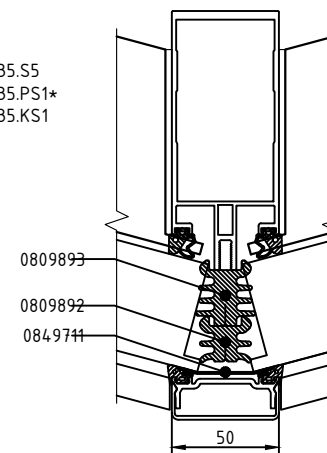

Стойка K1.B5.S2 устанавливается со стоечным сухарем 0345593 во всю длину.

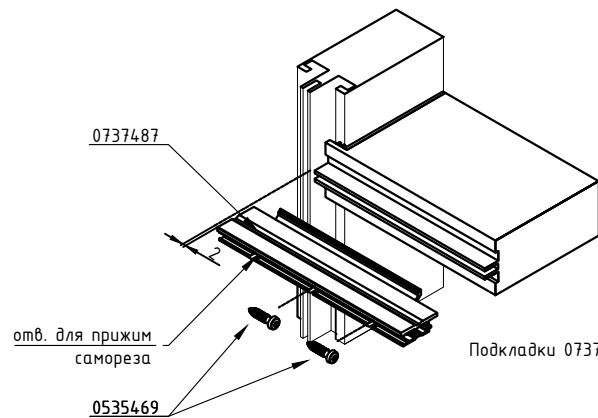

Подкладка 0737487

Подкладки 0737487 напилить из профиля 0340385.

						Остров 2 К1			
						" Многофункциональная комплексная жилая застройка , квартал 2, корпус 1, 2, 3, 4, 5, 6 по адресу : г . Москва , внутригородская территория муниципальный округ Хорошёво -Мнёвники."			
Изм.	Кол.уч.	Лист	№ док.	Подп.	Дата	Светопрозрачные конструкции	Стадия	Лист	Листов
Разраб.	Бирюкова				06.23		Р	5	
Проверил									
Н.контр.									
Т.контр.						Угловой витраж В-5		ООО "МАРКА ПОЛА"	
Утв.									

Копировал

Согласовано

Взам. инв. №

Подп. и дата

Инв. № подл.


ГАП

ГИП

Угловой витраж В-8 (развертка).

Кол-во : 19 шт.

S=8,41м.кв.

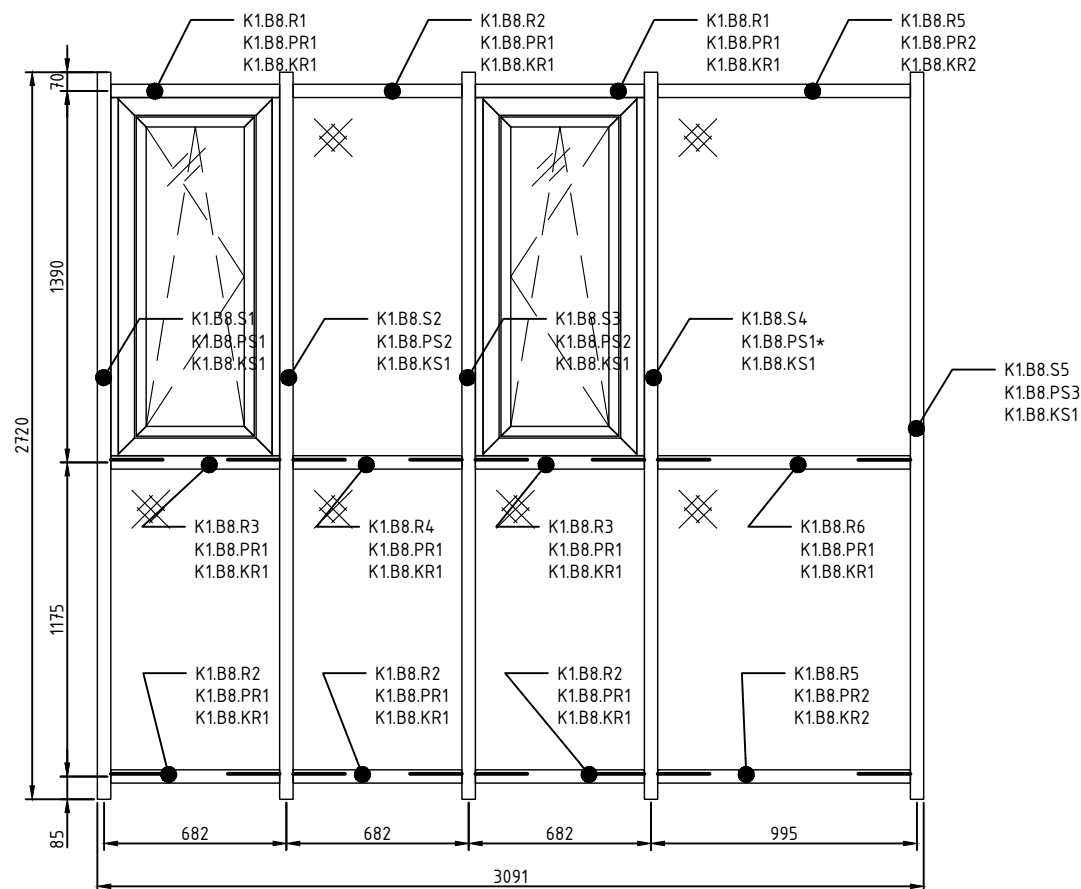


Заполнение термовставки - 0809892 + 0809893.

Под прижимы дублированная лента - 0849711.


Прижимной саморез:

- прижимы PS1, PS2, PS1* - Ø6,3x67мм - 0535476
- прижимы PS3, PR1, PR2 - Ø6,3x64мм - 0535475

Резиля крепить саморезом Ø4,2x12,7мм - 0525317

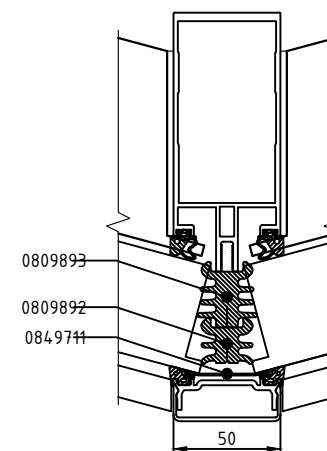

Стойка K1.B8.S4 устанавливается со стоечным сухарем 0345593 во всю длину.

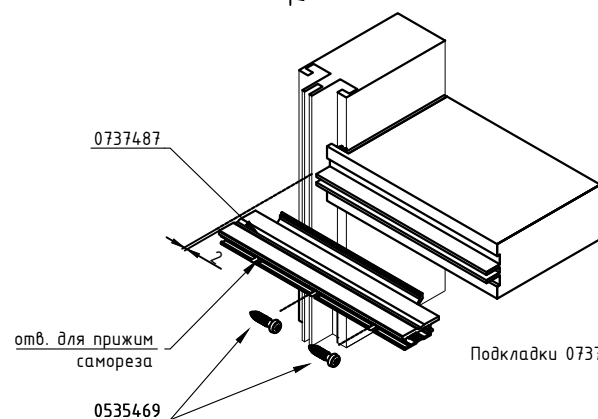

Подкладка 0737487

Подкладки 0737487 напилить из профиля 0340385.

						Остров 2 К1		
						" Многофункциональная комплексная жилая застройка , квартал 2, корпус 1, 2, 3, 4, 5, 6 по адресу : г . Москва , внутригородская территория муниципальный округ Хорошёво -Мнёвники."		
Изм.	Кол.уч.	Лист	№ док.	Подп.	Дата	Светопрозрачные конструкции	Стадия	Лист
Разраб.	Бирюкова				06.23		Р	7
Проверил								
Н.контр.						Угловой витраж В-8	ООО "МАРКА ПОЛА"	
Т.контр.								
Утв.								


Копировал

Согласовано	ГАП	ГИП
Инв. N подл.	Подп. и дата	Взам. инв. N

Угловой витраж В-9 (развертка).

Кол-во : 2 шт.

S=9,03 м.кв.

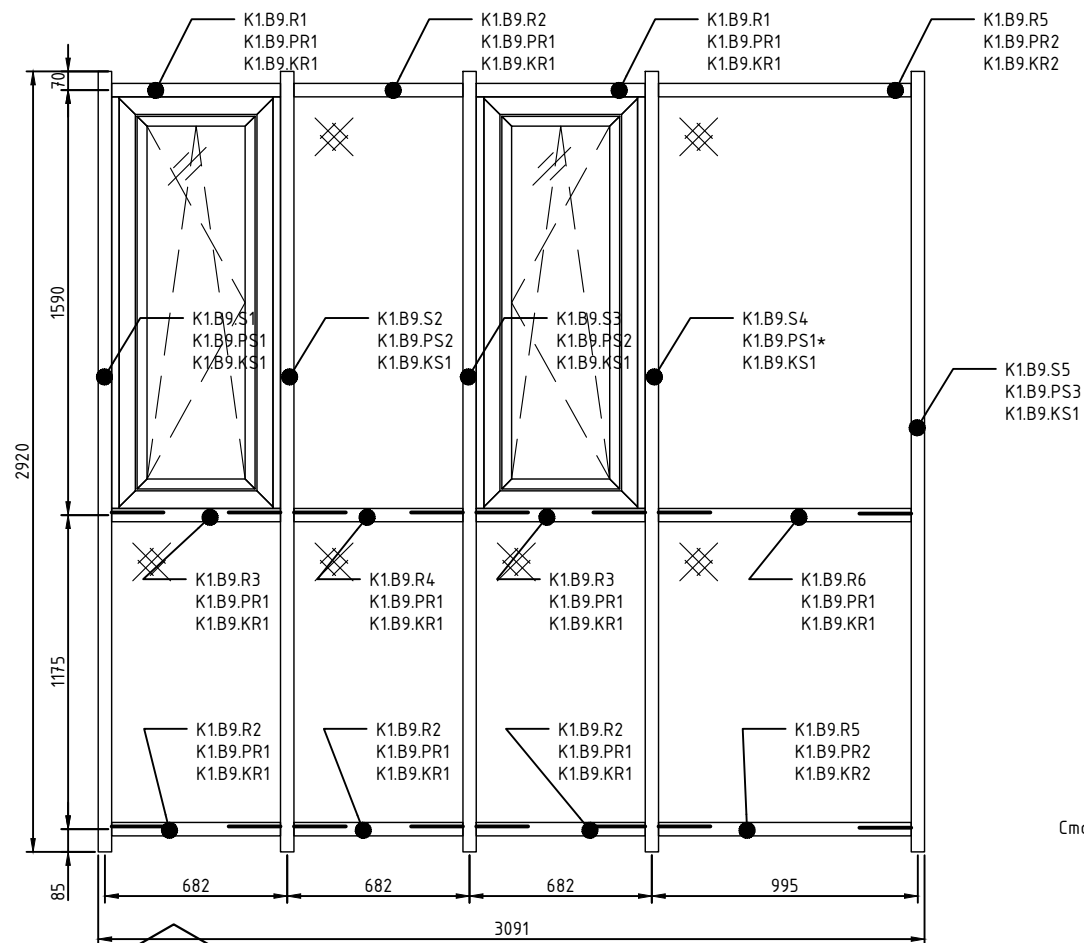


Заполнение термовставки - 0809892 + 0809893.

Под прижимы бутиловая лента - 0849711.


Прижимной саморез:

- прижимы PS1, PS2, PS1* - Ø6,3x67мм - 0535476
- прижимы PS3, PR1, PR2 - Ø6,3x64мм - 0535475

Ригеля крепить саморезом Ø4,2x12,7мм - 0525317

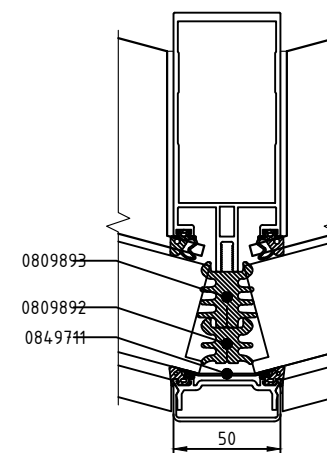

Стойка K1.B9.S4 устанавливается со стоечным сухарем 0345593 во всю длину.

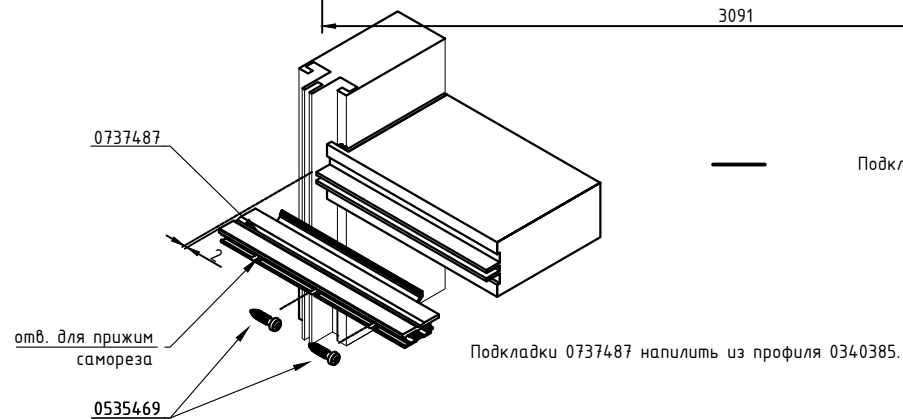

Подкладка 0737487

Подкладки 0737487 напилить из профиля 0340385.

						Остров 2 К1			
						" Многофункциональная комплексная жилая застройка , квартал 2, корпус 1, 2, 3, 4, 5, 6 по адресу : г . Москва , внутригородская территория муниципальный округ Хорошёво -Мнёвники."			
Изм.	Кол.уч.	Лист	№ док.	Подп.	Дата	Светопрозрачные конструкции	Стадия	Лист	Листов
Разраб.	Бирюкова				06.23		Р	8	
Проверил									
Н.контр.									
Т.контр.						Угловой витраж В-9		ООО "МАРКА ПОЛА"	
Утв.									

Копировал



Согласовано	ГАП	Взам. инв. №	Подп. и дата	Инв. № подл.
	ГИП			

Инв. N подл.	Подп. и дата	Взам. инв. N	Согласовано	
			ГАП	
			ГИП	

Technical drawing of a window frame assembly. The drawing shows a cross-section of the frame with dimensions in millimeters (mm). The total height of the frame is 2615 mm, calculated as 0340610 + 0340581. The frame is divided into three vertical sections: a top section of 45 mm, a middle section of 1390 mm, and a bottom section of 70 mm. The frame is supported by a base of 85 mm. The drawing also shows the distribution of loads (1 and 2) on the frame and the resulting internal forces (G and H).







Цвем: 79 7M15

1. Каждую стойку перед производством работ оклеить защитной пленкой, замаркировать номером стойки и укомплектовать уплотнителями и филлистрами
2. Стойки укомплектовать подпятниками из 034.5593 L=150 мм и дренажным лотком 073.8263.04 на винт 050.5029.--
3. Манжету 080.9885 и сухарь РС-2 установить на производстве по шаблону. Манжету подрезать по торцу ригеля.
4. Ригельные сухари РС-1 и РС-2 устанавливать на саморез Ø4,8x13 - 0525330.

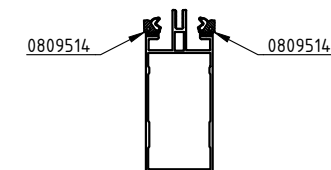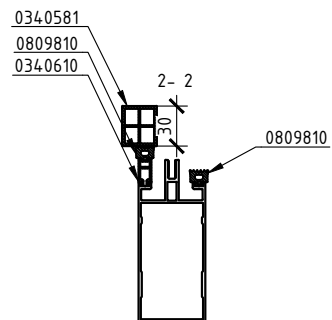


						Остров 2 К1			
						“ Многофункциональная комплексная жилая застройка , квартал 2, корпус 1, 2, 3, 4, 5, 6 по адресу : г . Москва , внутригородская территория муниципальный округ Хорошёво -Мнёвники.”			
Изм.	Кол.уч.	Лист	№ док.	Подп.	Дата	Светопрозрачные конструкции	Стадия	Лист	Листов
Разраб.	Бирюкова				06.23		Р	9	
Проверил									
Н.контр.									
						Стойки	ООО “МАРКА ПОЛА”		
Т.контр.									
Утв.									

Копировал

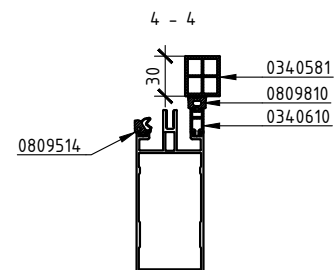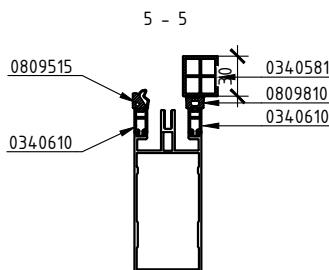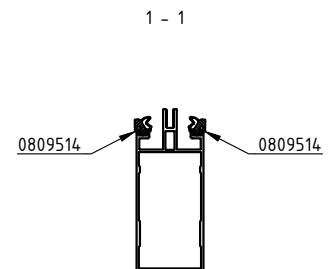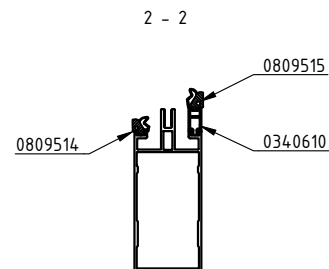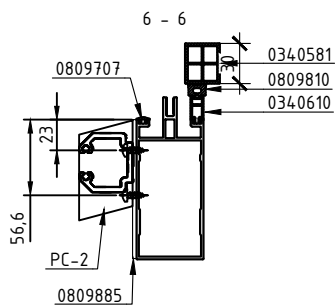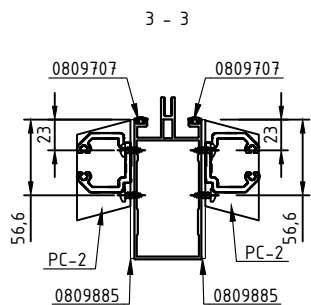


Маркировка:
 K1.B1.S3 - 19 шт.
 K1.B1.S2 - 19шт (зеркально)
 K1.B3.S4 - 19 шт.
 K1.B3.S3 - 19шт (зеркально)
 K1.B5.S4 - 19 шт.
 K1.B5.S3 - 19шт (зеркально)
 K1.B8.S3 - 19 шт.
 K1.B8.S2 - 19шт (зеркально)

Цвет: 79 7M15

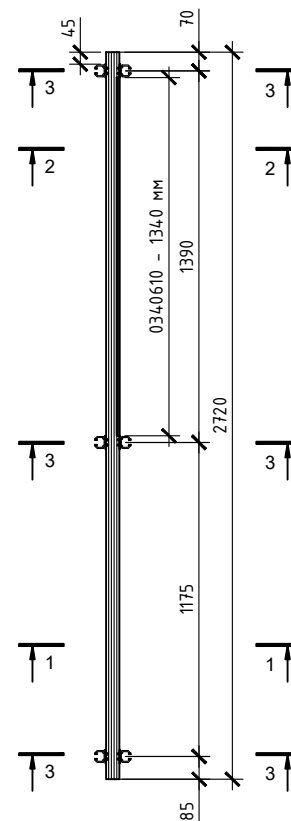

Маркировка:
 K1.B1.S1 - 19 шт. (зеркально)
 K1.B3.S5 - 19 шт
 K1.B5.S5 - 19 шт.
 K1.B8.S1 - 19 шт. (зеркально)

Цвет: 79 7M15

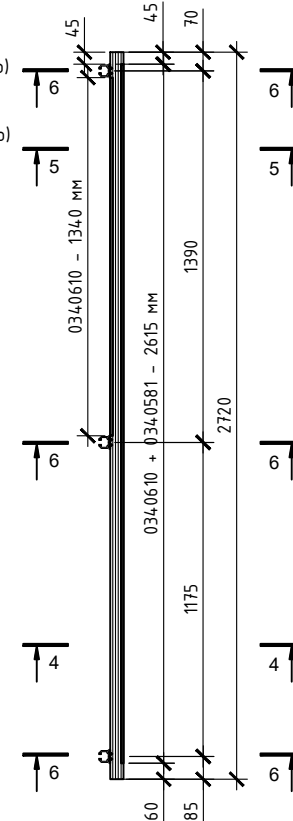

Примечание.

1. Каждую стойку перед производством работ оклеить защитной пленкой, замаркировать номером стойки и укомплектовать уплотнителями и филлистрами
2. Стойки укомплектовать подпятниками из 034.5593 L=150 мм и дренажным лотком 073.8263.04 на винт 050.5029.--
3. Манжету 080.9885 и сухарь PC-2 установить на производстве по шаблону. Манжету подрезать по торцу ригеля.
4. Ригельные сухари PC-1 и PC-2 устанавливать на саморез Ø4,8x13 - 0525330.


Согласовано	ГАП	ГИП
Инв. N подл.	Подп. и дата	Взам. инв. N

						Остров 2 К1			
						" Многофункциональная комплексная жилая застройка , квартал 2, корпус 1, 2, 3, 4, 5, 6 по адресу : г . Москва , внутригородская территория муниципальный округ Хорошёво -Мнёвники."			
Изм.	Кол.уч.	Лист	№ док.	Подп.	Дата	Светопрозрачные конструкции	Стадия	Лист	Листов
Разраб.	Бирюкова				06.23		Р	10	
Проверил									
Н.контр.						Стойки	ООО "МАРКА ПОЛА"		
Т.контр.									
Утв.									


Копировал

Согласовано			Взам. инв. №		Подп. и дата		Инв. № подл.	
	ГАП	ГИП						






Маркировка:
 K1.B2.S5 – 1 шт. (зеркально)
 K1.B4.S1 – 1 шт
 K1.B6.S1 – 2 шт.
 K1.B9.S5 – 2 шт. (зеркально)

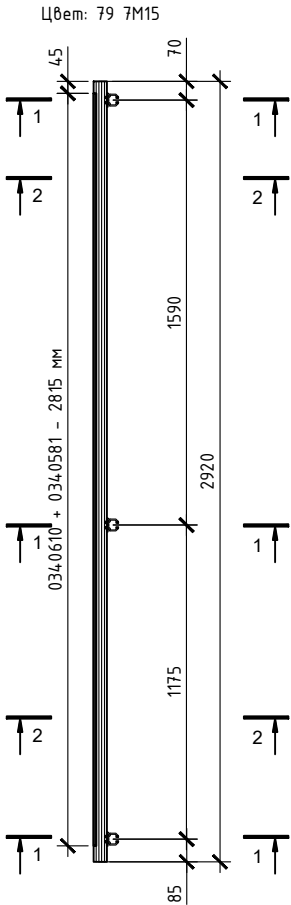

Маркировка:
 K1.B2.S4 – 1 шт. (зеркально)
 K1.B4.S2 – 1 шт
 K1.B6.S2 – 2 шт.
 K1.B9.S4 – 2 шт. (зеркально)






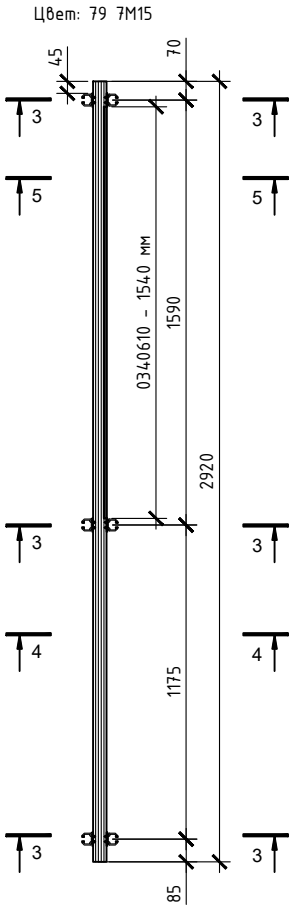


- Примечание.
1. Каждую стойку перед производством работ оклеить защитной пленкой, замаркировать номером стойки и укомплектовать уплотнителями и флистрами
 2. Стойки укомплектовать подпятниками из 034.5593 L=150 мм и дренажным лотком 073.8263.04 на винт 050.5029.--
 3. Манжету 080.9885 и сухарь РС-2 установить на производстве по шаблону. Манжету подрезать по торцу ригеля.
 4. Ригельные сухари РС-1 и РС-2 устанавливать на саморез Ø4,8x13 – 0525330.

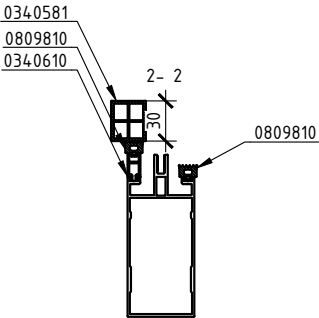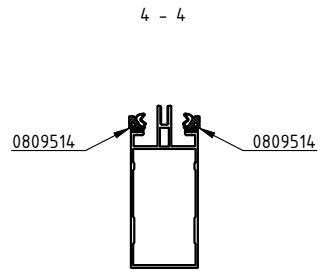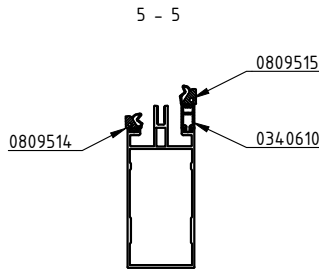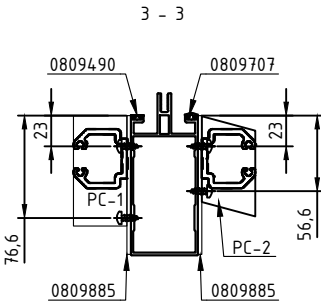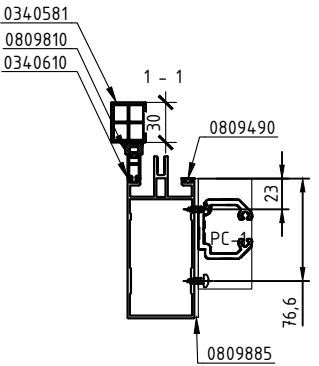


						Остров 2 К1			
						“ Многофункциональная комплексная жилая застройка , квартал 2, корпус 1, 2, 3, 4, 5, 6 по адресу : г . Москва , внутригородская территория муниципальный округ Хорошёво –Мнёвники.”			
Изм.	Кол.уч.	Лист	№ док.	Подп.	Дата	Светопрозрачные конструкции	Стадия	Лист	Листов
Разраб.	Бирюкова				06.23		Р	11	
Проверил									
Н.контр.									
						Стойки	ООО “МАРКА ПОЛА”		
Т.контр.									
Утв.									

Согласовано	ГАП	
	ГИП	
Инв. № подл.	Подп. и дата	
	Взам. инв. №	

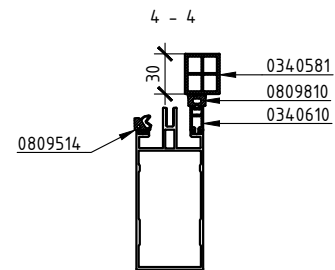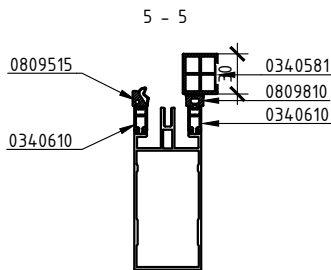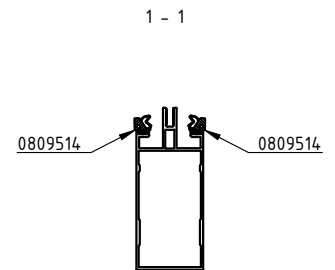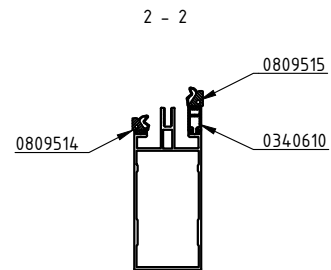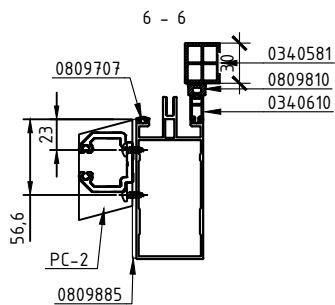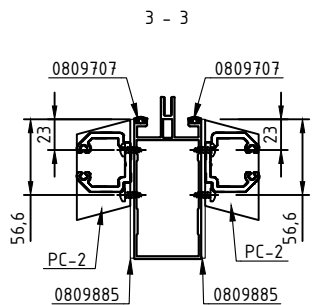


Маркировка:
K1.B2.S3 - 1 шт.
K1.B2.S2 - 1шт (зеркально)
K1.B4.S4 - 1 шт.
K1.B4.S3 - 1шт (зеркально)
K1.B6.S4 - 2 шт.
K1.B6.S3 - 2шт (зеркально)
K1.B9.S3 - 2 шт.
K1.B9.S2 - 2шт (зеркально)

Цвет: 79 7M15

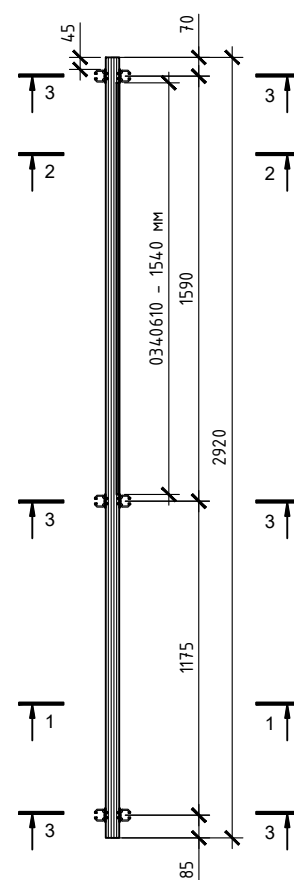

Маркировка:
K1.B2.S1 - 1 шт. (зеркально)
K1.B4.S5 - 1 шт.
K1.B6.S5 - 2 шт.
K1.B9.S1 - 2 шт. (зеркально)
Цвет: 79 7M15

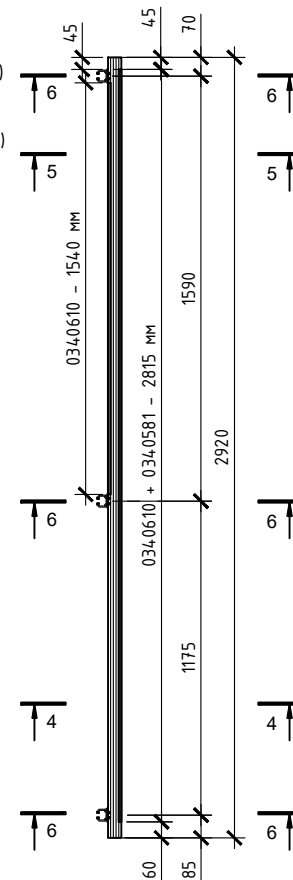


Примечание.

1. Каждую стойку перед производством работ оклеить защитной пленкой, замаркировать номером стойки и укомплектовать уплотнителями и филлистрами
2. Стойки укомплектовать подпятниками из 034.5593 L=150 мм и дренажным лотком 073.8263.04 на винт 050.5029.--
3. Манжету 080.9885 и сухарь PC-2 установить на производстве по шаблону. Манжету подрезать по торцу ригеля.
4. Ригельные сухари PC-1 и PC-2 устанавливать на саморез Ø4,8x13 - 0525330.


						Остров 2 К1			
						" Многофункциональная комплексная жилая застройка , квартал 2, корпус 1, 2, 3, 4, 5, 6 по адресу : г . Москва , внутригородская территория муниципальный округ Хорошёво -Мнёвники."			
Изм.	Кол.уч.	Лист	№ док.	Подп.	Дата	Светопрозрачные конструкции	Стадия	Лист	Листов
Разраб.	Бирюкова				06.23		Р	12	
Проверил									
Н.контр.						Стойки	ООО "МАРКА ПОЛА"		
Т.контр.									
Утв.									

Копировал


Профиль ригеля 0343524
Цвет: 79 7M15

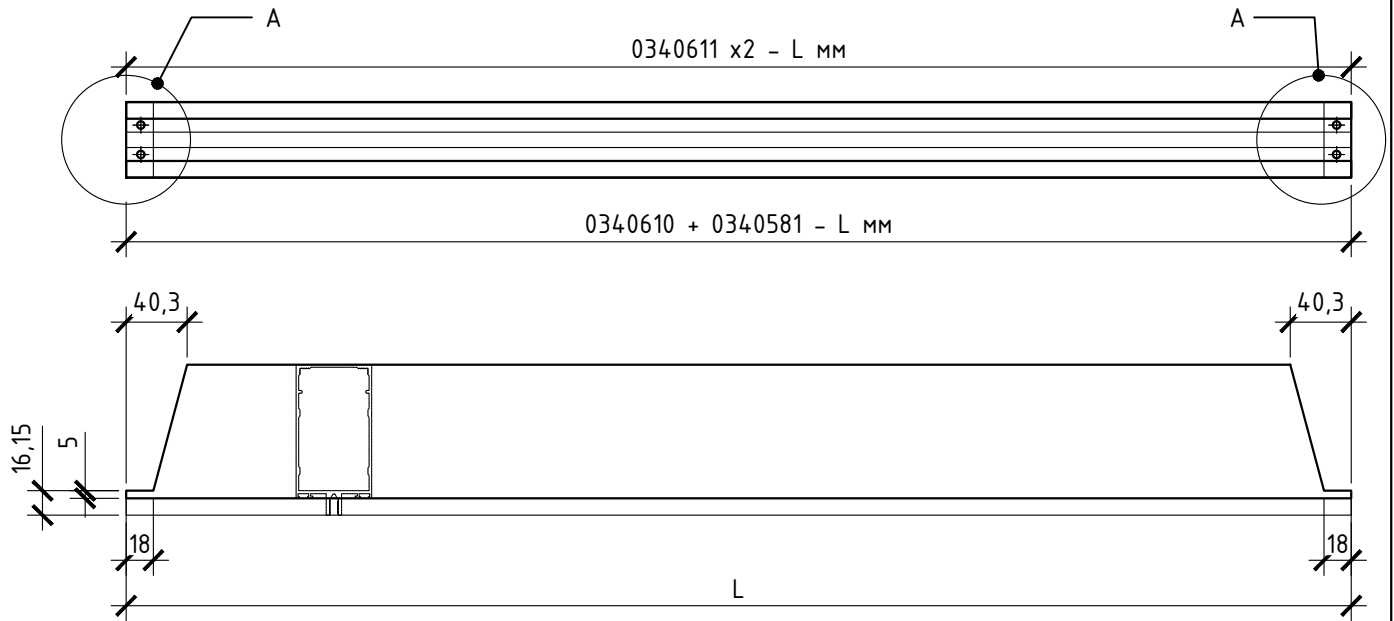

Маркировка	L, мм	Кол-во
K1.B1.R1	766,2	38
K1.B2.R1	766,2	2
K1.B3.R1	758,2	38
K1.B4.R1	758,2	2
K1.B5.R1	758,2	38
K1.B6.R1	758,2	4
K1.B8.R1	619,2	38
K1.B9.R1	619,2	4

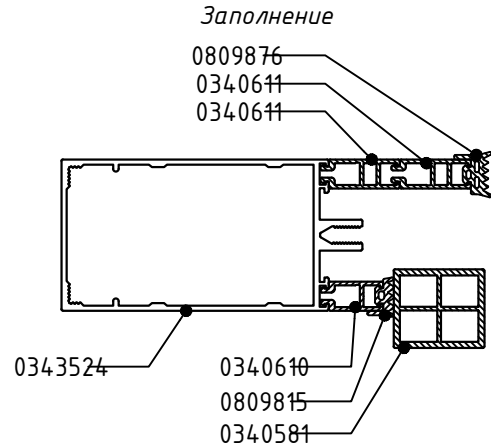

Одр. А (2:1)

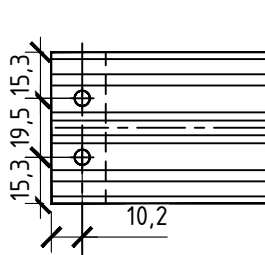


Примечание.

1. Каждый ригель перед производством работ оклеить защитной пленкой, замаркировать номером стойки и укомплектовать уплотнителями и филлистрами


Согласовано	ГАП	ГИП								
	Взам. инв. №	Подп. и дата								
Инв. № подл.	Изм.	Кол.уч.	Лист	№ док.	Подп.	Дата	Остров 2 К1			
	Разраб.	Бирюкова				06.23	" Многофункциональная комплексная жилая застройка , квартал 2, корпус 1, 2, 3, 4, 5, 6 по адресу : г . Москва , внутригородская территория муниципального округа Хорошёво –Мнёвники."			
Инв. № подл.	Проверил						Светопрозрачные конструкции	Стадия	Лист	Листов
	Н.контр.							Р	13	
	Т.контр.							Ригели		
Утв.							ООО "МАРКА ПОЛА"			

Копировал


Профиль ригеля 0343524
Цвет: 79 7M15

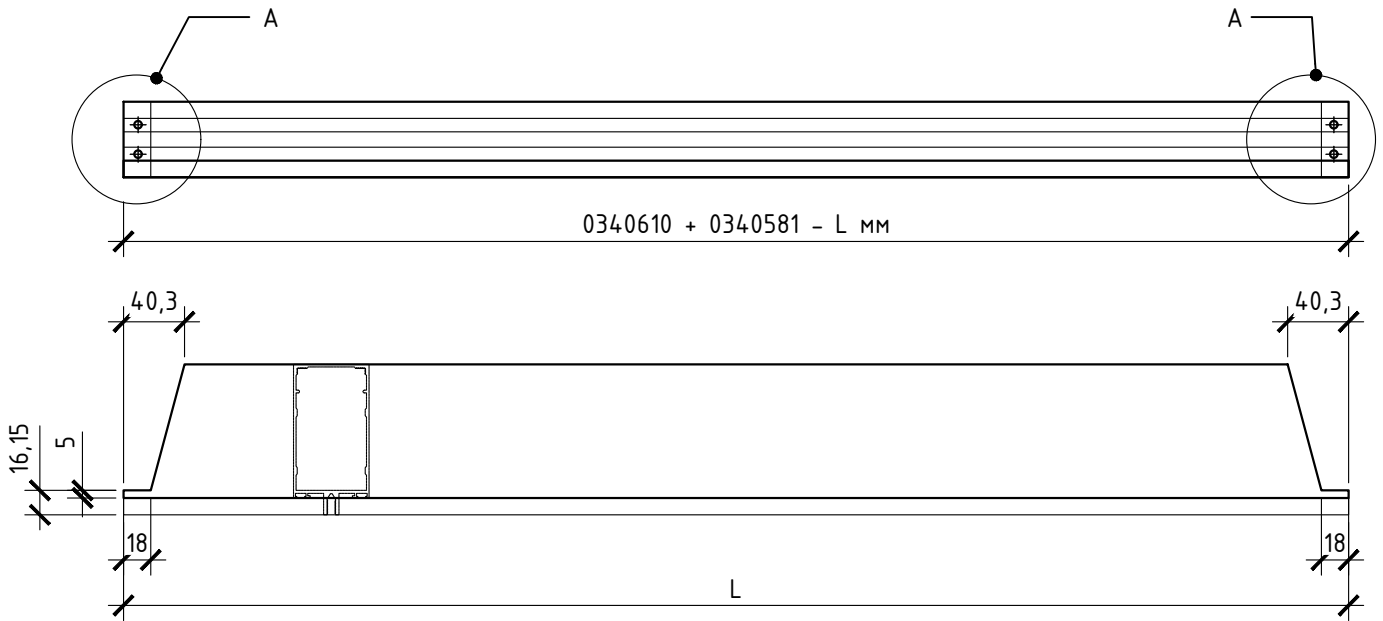

Маркировка		L, мм	Кол-во
K1.B1.R2		766,2	76
K1.B2.R2		766,2	4
K1.B3.R2		758,2	76
K1.B4.R2		758,2	4
K1.B5.R2		758,2	76
K1.B6.R2		758,2	8
K1.B8.R2		619,2	76
K1.B9.R2		619,2	8

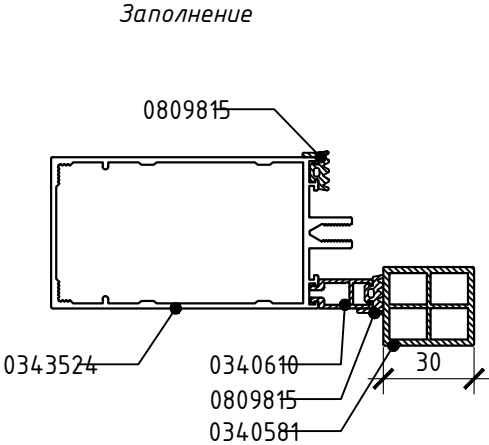

Обр. А (2:1)

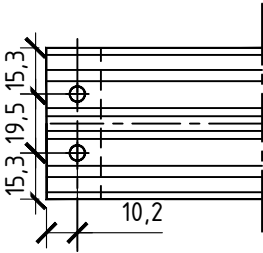


Примечание.
1. Каждый ригель перед производством работ оклеить защитной пленкой, замаркировать номером стойки и укомплектовать уплотнителями и филлистрами


Согласовано	ГАП	ГИП				
	Взам. инв. Н					
Подп. и дата	Изм.	Кол.уч.	Лист	№ док.	Подп.	Дата
	Разраб.	Бирюкова				06.23
Инв. Н подл.	Проверил					
	Н.контр.					
	Т.контр.					
	Утв.					

Остров 2 К1				
" Многофункциональная комплексная жилая застройка , квартал 2, корпус 1, 2, 3, 4, 5, 6 по адресу : г . Москва , внутригородская территория муниципальный округ Хорошёво –Мнёвники."				
Светопрозрачные конструкции		Стадия	Лист	Листов
		Р	14	
Ригели		ООО "МАРКА ПОЛА"		


Профиль ригеля 0343524
Цвет: 79 7M15

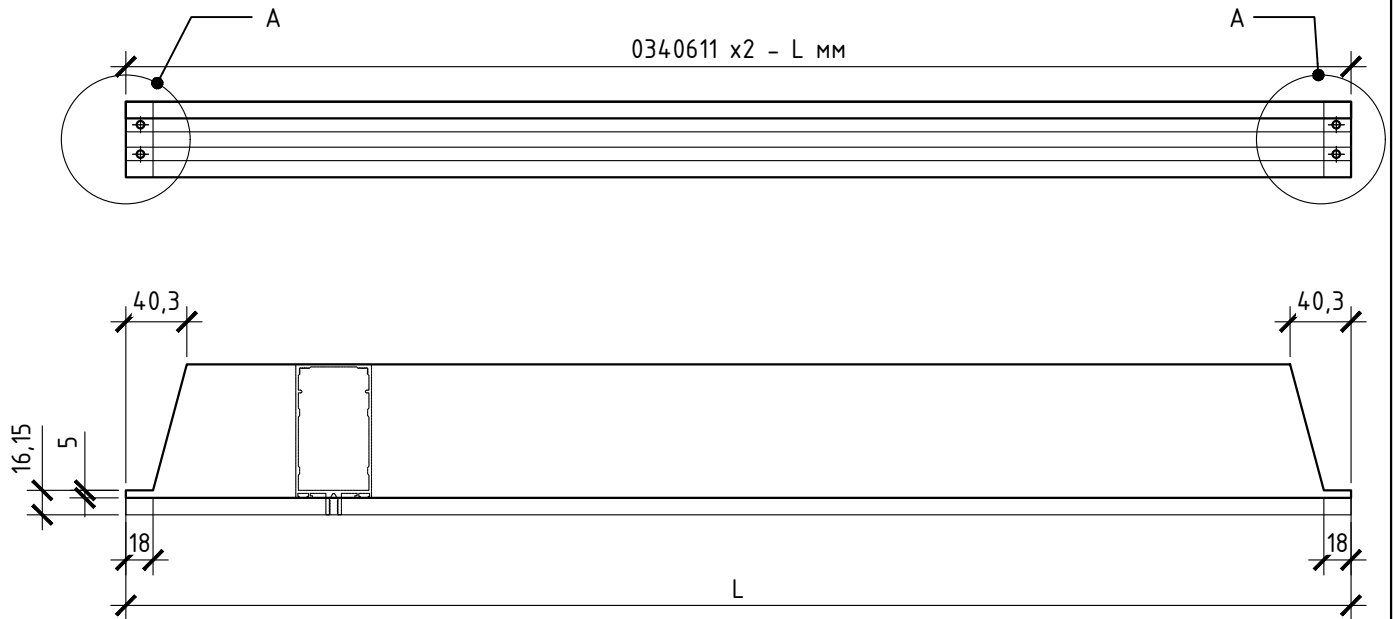

Маркировка		L, мм	Кол-во
K1.B1.R3		766,2	38
K1.B2.R3		766,2	2
K1.B3.R3		758,2	38
K1.B4.R3		758,2	2
K1.B5.R3		758,2	38
K1.B6.R3		758,2	4
K1.B8.R3		619,2	38
K1.B9.R3		619,2	4

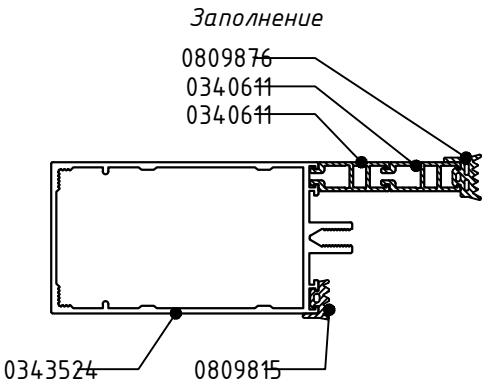



Одр. А (2:1)

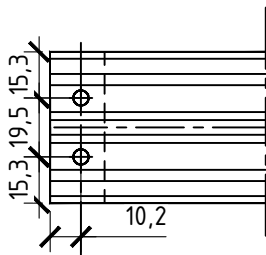

Примечание.
1. Каждый ригель перед производством работ оклеить защитной пленкой, замаркировать номером стойки и укомплектовать уплотнителями и флистрами


Согласовано	ГАП									
	ГИП									
	Взам. инв. Н									
	Подп. и дата									
Инв. Н подл.	Изм.	Кол.уч.	Лист	№ док.	Подп.	Дата	Остров 2 К1			
	Разраб.	Бирюкова				06.23	" Многофункциональная комплексная жилая застройка , квартал 2, корпус 1, 2, 3, 4, 5, 6 по адресу : г . Москва , внутригородская территория муниципальный округ Хорошёво –Мнёвники."			
	Проверил						Светопрозрачные конструкции	Стадия	Лист	Листов
	Н.контр.							Р	15	
	Т.контр.						Ригели	ООО "МАРКА ПОЛА"		
	Утв.									

Профиль ригеля 0343524
Цвет: 79 7M15

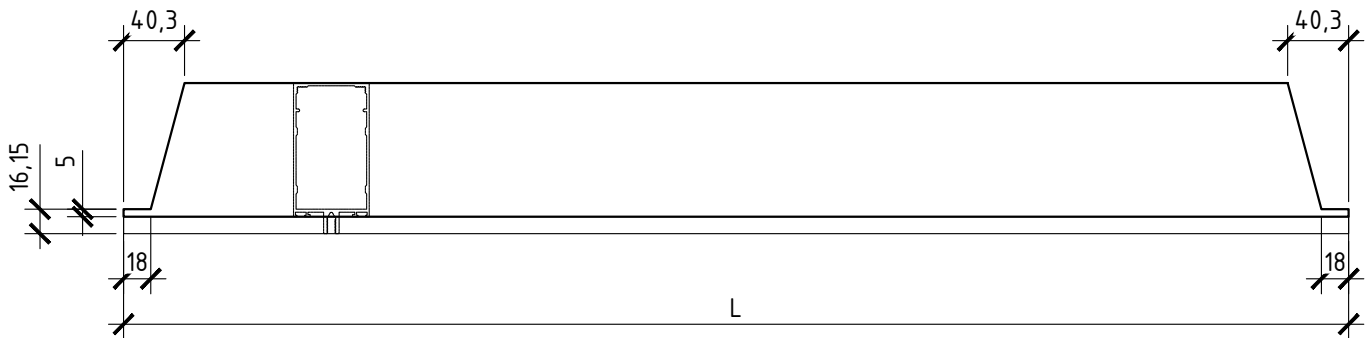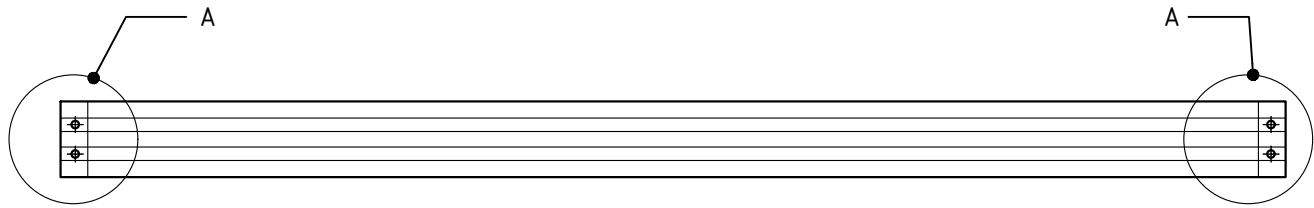


Заполнение

Маркировка		L, мм	Кол-во
K1.B1.R4		766,2	19
K1.B2.R4		766,2	1
K1.B3.R4		758,2	19
K1.B4.R4		758,2	1
K1.B5.R4		758,2	19
K1.B6.R4		758,2	2
K1.B8.R4		619,2	19
K1.B9.R4		619,2	2

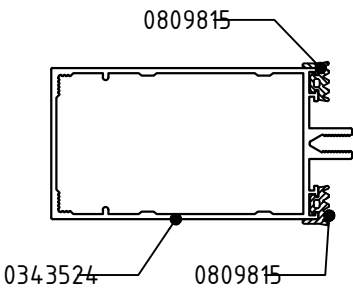

Обр. А (2:1)

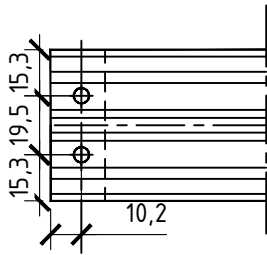


Примечание.
1. Каждый ригель перед производством работ оклеить защитной пленкой, замаркировать номером стойки и укомплектовать уплотнителями и флистрами

Согласовано		
	ГАП	
	ГИП	
Инв. № подл.	Подп. и дата	Взам. инв. №


						Остров 2 К1				
						" Многофункциональная комплексная жилая застройка , квартал 2, корпус 1, 2, 3, 4, 5, 6 по адресу : г . Москва , внутригородская территория муниципальный округ Хорошёво –Мнёвники."				
Изм.	Кол.уч.	Лист	№ док.	Подп.	Дата	Светопрозрачные конструкции		Стадия	Лист	Листов
Разраб.		Бирюкова			06.23			Р	16	
Проверил										
Н.контр.						Ригели		ООО "МАРКА ПОЛА"		
Т.контр.										
Утв.										

Профиль ригеля 0343525
Цвет: 79 7M15

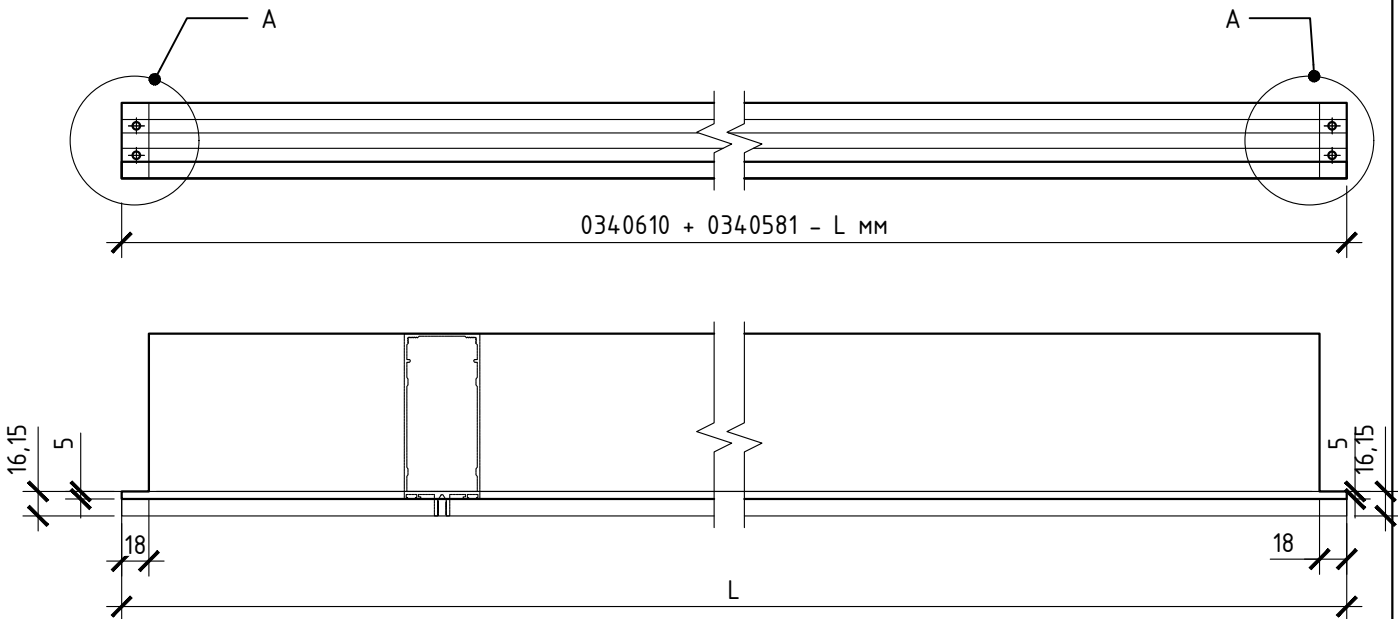


Заполнение

Маркировка	L, мм	Кол-во
K1.B1.R5	1475,0	38
K1.B2.R5	1475,0	2
K1.B3.R5	1160,0	38
K1.B4.R5	1160,0	2
K1.B5.R5	1475,0	38
K1.B6.R5	1475,0	4
K1.B8.R5	975,0	38
K1.B9.R5	975,0	4

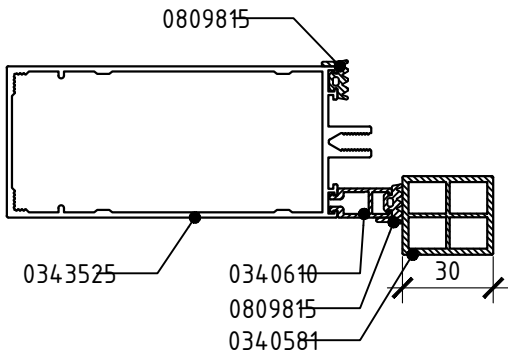



Обр. А (2:1)

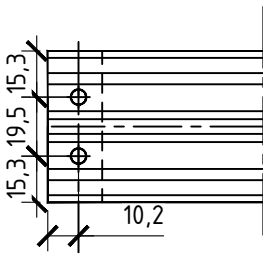

Примечание.
1. Каждый ригель перед производством работ оклеить защитной пленкой, замаркировать номером стойки и укомплектовать уплотнителями и филлистрами


Согласовано	ГАП	ГИП	Взам. инв. N	Подп. и дата	Изм.	Кол.уч.	Лист	№ док.	Подп.	Дата	Остров 2 К1			
											" Многофункциональная комплексная жилая застройка , квартал 2, корпус 1, 2, 3, 4, 5, 6 по адресу : г . Москва , внутригородская территория муниципальный округ Хорошёво -Мнёвники."			
	Инв. N подл.	Разраб.	Бирюкова		06.23	Светопрозрачные конструкции	Стадия	Лист	Листов					
		Проверил					P	17						
		Н.контр.					000 "МАРКА ПОЛА"							
		Т.контр.												
		Утв.												
		Ригели												

Профиль рузеля 0343525
Цвем: 79 7M15

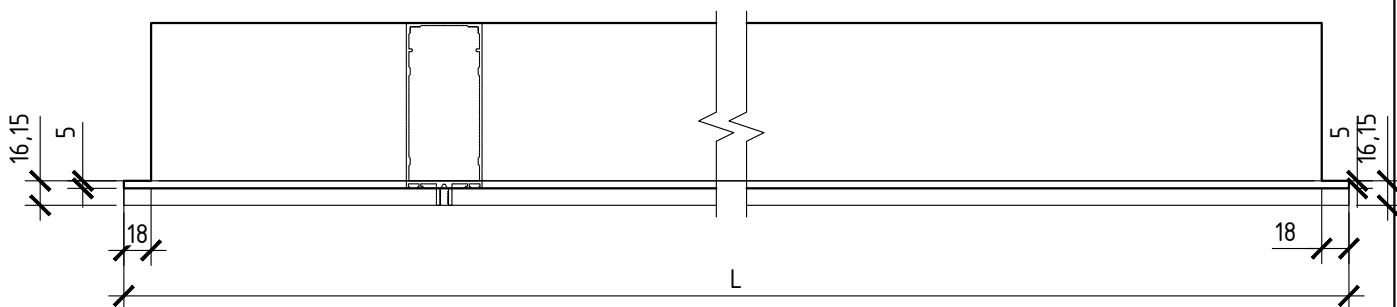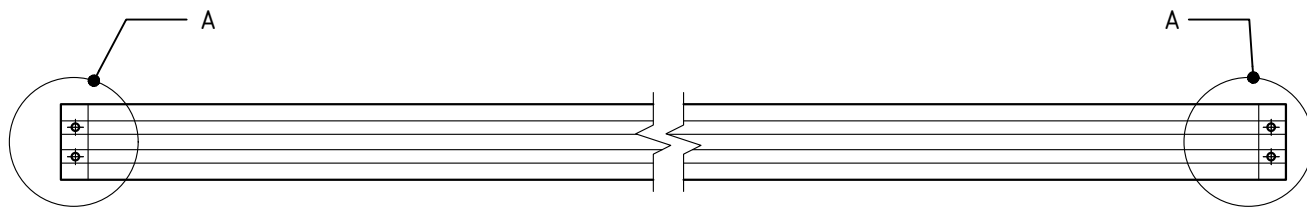


Заполнение

Маркировка		L, мм	Кол-во
K1.B1.R6		1475,0	19
K1.B2.R6		1475,0	1
K1.B3.R6		1160,0	19
K1.B4.R6		1160,0	1
K1.B5.R6		1475,0	19
K1.B6.R6		1475,0	2
K1.B8.R6		975,0	19
K1.B9.R6		975,0	2

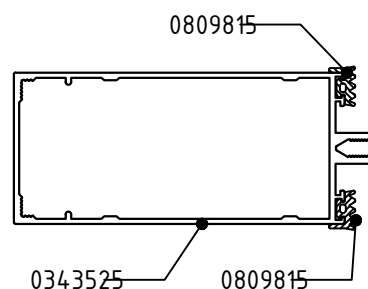

Οδρ. Α (2:1)

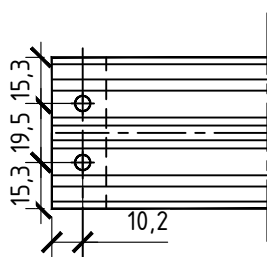





Примечание.

1. Каждый рулель перед производством работ оклеить защитной пленкой, замаркировать номером стойки и укомплектовать уплотнителями и флистами

						Остров 2 К1			
						" Многофункциональная комплексная жилая застройка , квартал 2, корпус 1, 2, 3, 4, 5, 6 по адресу : г . Москва , внутригородская территория муниципальный округ Хорошёво –Мнёвники."			
Изм.	Кол.уч.	Лист	№ док.	Подп.	Дата				
Разраб.		Бирюкова			06.23	Светопрозрачные конструкции	Стадия	Лист	Листов
Проверил							Р	18	
Н.контр.									
						Ризели	ООО "МАРКА ПОЛА"		
Т.контр.									
Утв.									



Копировал

Прижимная планка стойки
Цвет: без покраски

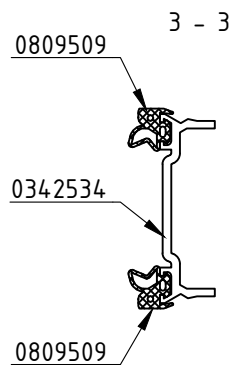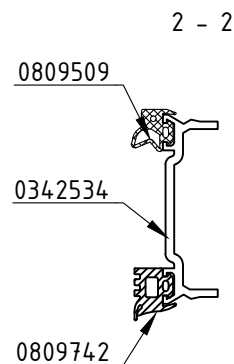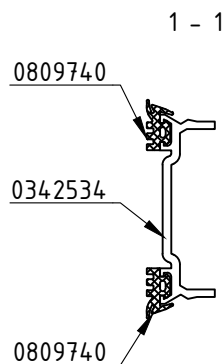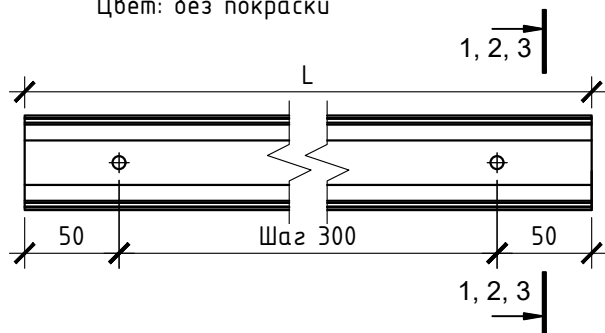

Маркировка	№ Сечения	L, мм	Кол-во
K1.B1.PS1	2 - 2	2615,0	38
K1.B1.PS2	3 - 3	2615,0	38
K1.B1.PS3	1 - 1	2615,0	19
K1.B2.PS1	2 - 2	2815,0	2
K1.B2.PS2	3 - 3	2815,0	2
K1.B2.PS3	1 - 1	2815,0	1
K1.B3.PS1	2 - 2	2615,0	38
K1.B3.PS2	3 - 3	2615,0	38
K1.B3.PS3	1 - 1	2615,0	19
K1.B4.PS1	2 - 2	2815,0	2
K1.B4.PS2	3 - 3	2815,0	2
K1.B4.PS3	1 - 1	2815,0	1
K1.B5.PS1	2 - 2	2615,0	38
K1.B5.PS2	3 - 3	2615,0	38
K1.B5.PS3	1 - 1	2615,0	19
K1.B6.PS1	2 - 2	2815,0	4
K1.B6.PS2	3 - 3	2815,0	4
K1.B6.PS3	1 - 1	2815,0	2

Маркировка	№ Сечения	L, мм	Кол-во
K1.B8.PS1	2 - 2	2615,0	38
K1.B8.PS2	3 - 3	2615,0	38
K1.B8.PS3	1 - 1	2615,0	19
K1.B9.PS1	2 - 2	2815,0	4
K1.B9.PS2	3 - 3	2815,0	4
K1.B9.PS3	1 - 1	2815,0	2

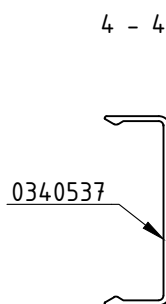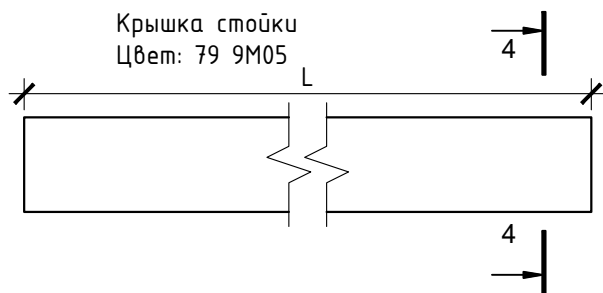


Маркировка	L, мм	Кол-во
K1.B1.KS1	2615,0	95
K1.B2.KS1	2815,0	5
K1.B3.KS1	2615,0	95
K1.B4.KS1	2815,0	5
K1.B5.KS1	2615,0	95
K1.B6.KS1	2815,0	10
K1.B8.KS1	2615,0	95
K1.B9.KS1	2815,0	10


Согласовано	ГАП	Взам. инв. №	Подп. и дата	Инв. № подл.
	ГИП			

						Остров 2 К1				
						" Многофункциональная комплексная жилая застройка , квартал 2, корпус 1, 2, 3, 4, 5, 6 по адресу : г . Москва , внутригородская территория муниципальный округ Хорошёво -Мнёвники."				
Изм.	Кол.уч.	Лист	№ док.	Подп.	Дата	Светопрозрачные конструкции		Стадия	Лист	Листов
Разраб.		Бирюкова			06.23			Р	19	
Проверил										
Н.контр.										
						Прижим и крышка стойки		ООО "МАРКА ПОЛА"		
Т.контр.										
Утв.										

Прижимная планка ригеля
Цвет: без покраски

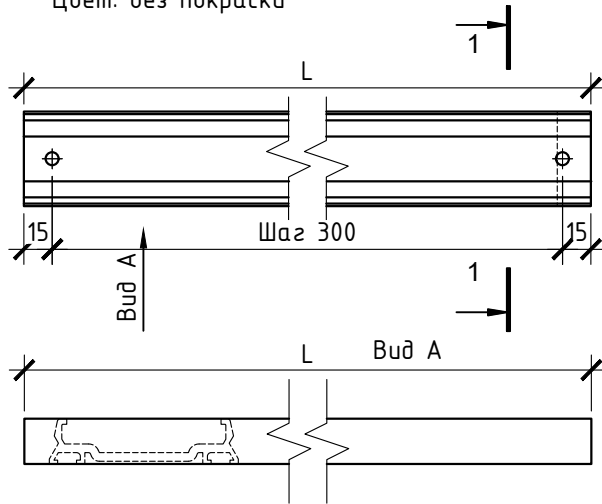


Крышка ригеля
Цвет: 79 9M05

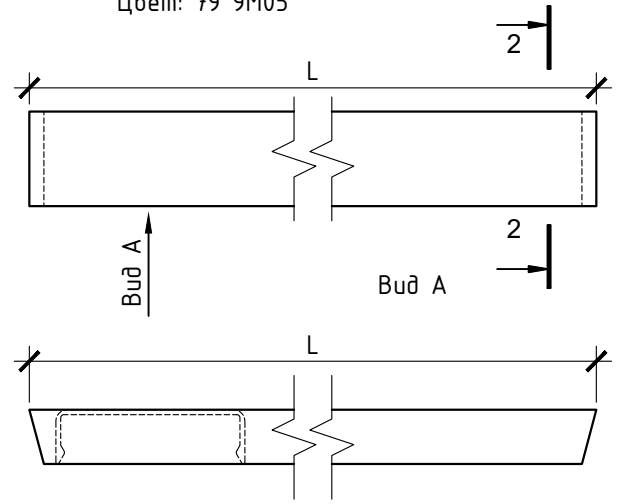

Маркировка а		L, мм	Кол-во
K1.B1.PR1		766,0	171
K1.B1.PR2		1441,0	57
K1.B2.PR1		766,0	9
K1.B2.PR2		1441,0	3
K1.B3.PR1		758,0	171
K1.B3.PR2		1126,0	57
K1.B4.PR1		758,0	9
K1.B4.PR2		1126,0	3
K1.B5.PR1		758,0	171
K1.B5.PR2		1441,0	57
K1.B6.PR1		758,0	18
K1.B6.PR2		1441,0	6
K1.B8.PR1		619,0	171
K1.B8.PR2		941,0	57
K1.B9.PR1		619,0	18
K1.B9.PR2		941,0	6

Маркировка		L, мм	Кол-во
K1.B1.KR1		776,5	171
K1.B1.KR2	ПРЯМАЯ	1443,0	57
K1.B2.KR1		776,5	9
K1.B2.KR2	ПРЯМАЯ	1443,0	3
K1.B3.KR1		768,5	171
K1.B3.KR2	ПРЯМАЯ	1128,0	57
K1.B4.KR1		768,5	9
K1.B4.KR2	ПРЯМАЯ	1128,0	3
K1.B5.KR1		768,5	171
K1.B5.KR2	ПРЯМАЯ	1443,0	57
K1.B6.KR1		768,5	18
K1.B6.KR2	ПРЯМАЯ	1443,0	6
K1.B8.KR1		629,5	171
K1.B8.KR2	ПРЯМАЯ	943,0	57
K1.B9.KR1		629,5	18
K1.B9.KR2	ПРЯМАЯ	943,0	6

! ---.---.KR2 прямые, без углов запила

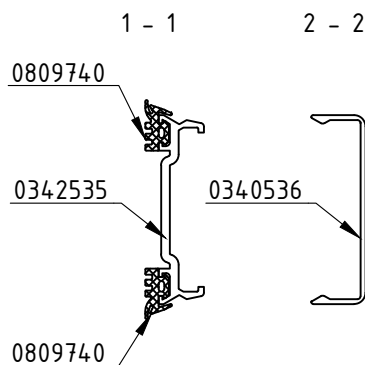


Согласовано	ГАП	ГИП	Взам. инв. №	Подп. и дата	Инв. № подл.	Изм.	Кол.уч.	Лист	№ док.	Подп.	Дата	Остров 2 К1								
	" Многофункциональная комплексная жилая застройка , квартал 2, корпус 1, 2, 3, 4, 5, 6 по адресу : г . Москва , внутригородская территория муниципальный округ Хорошёво -Мнёвники."																			
	Разраб.	Бирюкова											06.23	Светопрозрачные конструкции	Стадия	Лист	Листов			
	Проверил														Р	20				
	Н.контр.											Прижим и крышка ригеля	ООО "МАРКА ПОЛА"							
	Т.контр.																			
	Утв.																			

Угловой витраж В-1.1 (развертка).

Кол-во : 18 шт.

S=11,64 м.кв.

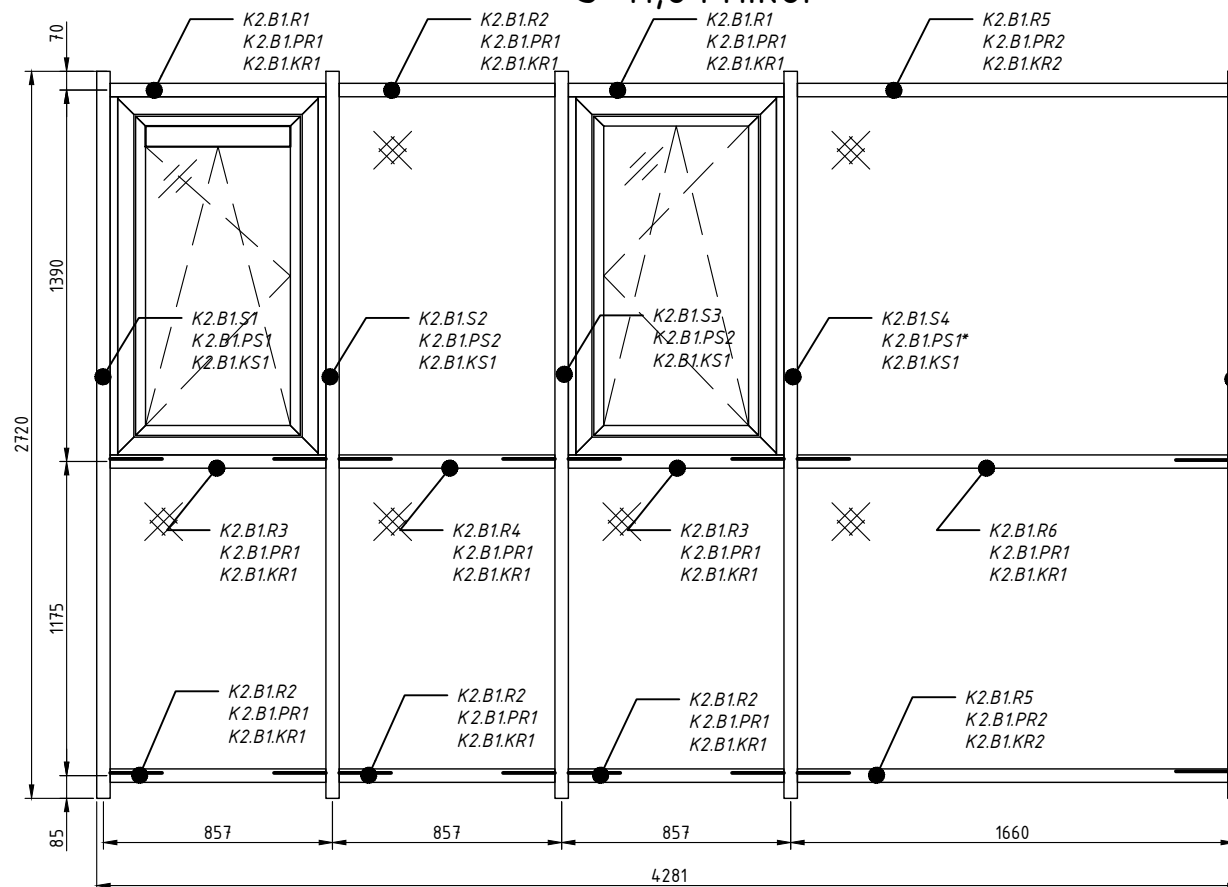


Заполнение термовставки - 0809892 + 0809893.

Под прижимы бутиловая лента - 0849711.


Прижимной саморез:

- прижимы PS1, PS2, PS1* - Ø6,3x67мм - 0535476
- прижимы PS3, PR1, PR2 - Ø6,3x64мм - 0535475

Ригеля крепить саморезом Ø4,2x12,7мм - 0525317

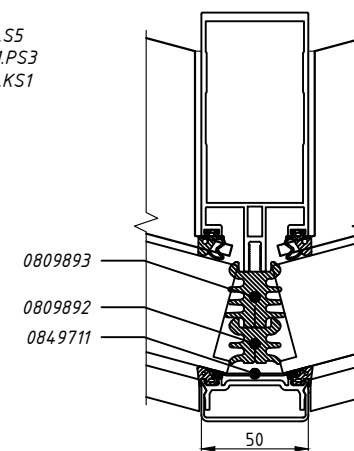

Стойка K2.B1.S4 устанавливается со стоечным сухарем 0345593 во всю длину.

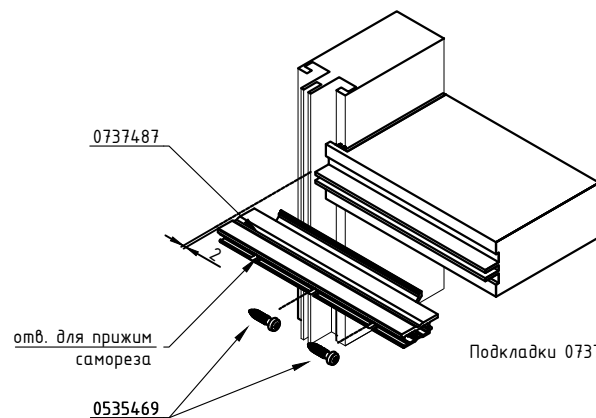

Подкладка 0737487

Подкладки 0737487 напилить из профиля 0340385.

						Остров 2 К1			
						" Многофункциональная комплексная жилая застройка , квартал 2, корпус 1, 2, 3, 4, 5, 6 по адресу : г . Москва , внутригородская территория муниципальный округ Хорошёво -Мнёвники."			
Изм.	Кол.уч.	Лист	№ док.	Подп.	Дата	Светопрозрачные конструкции	Стадия	Лист	Листов
Разраб.	Бирюкова				06.23		Р	21	
Проверил									
Н.контр.									
Т.контр.						Угловой витраж В-1.1			
Утв.						ООО "МАРКА ПОЛА"			


Копировал

Инв. N подл.	Подп. и дата	Взам. инв. N	Согласовано	
			ГАП	ГИП

Угловой витраж В-3.1 (развертка).


Кол-во : 17 шт.

S=11,83 м.кв.

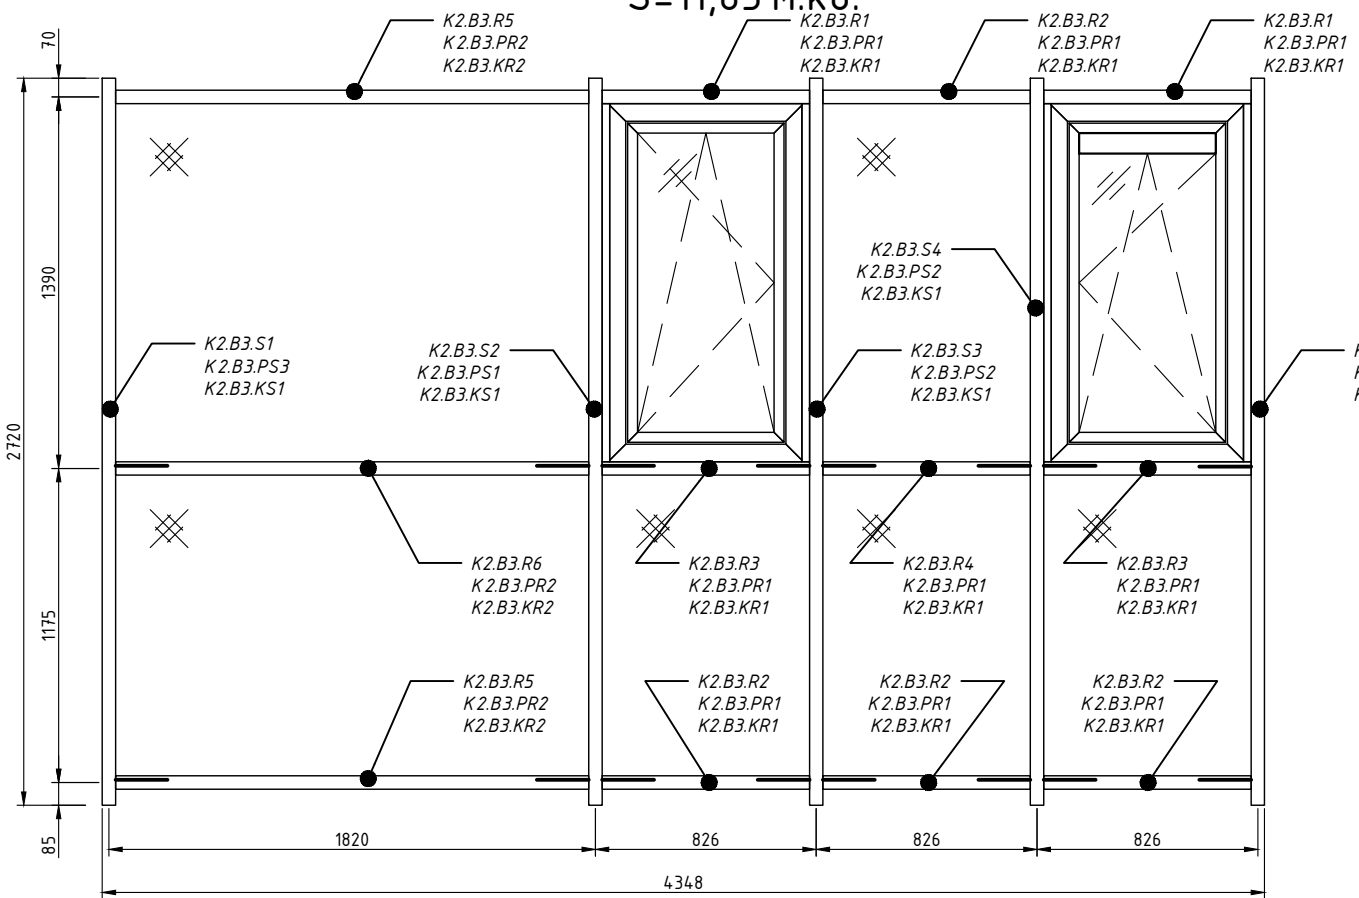


Заполнение термовставки - 0809892 + 0809893.
Под прижимы бутиловая лента - 0849711.
Прижимной саморез:
- прижимы PS1, PS2, PS1* - Ø6,3x67мм - 0535476
- прижимы PS3, PR1, PR2 - Ø6,3x64мм - 0535475

Ригеля крепить саморезом Ø4,2x12,7мм - 0525317

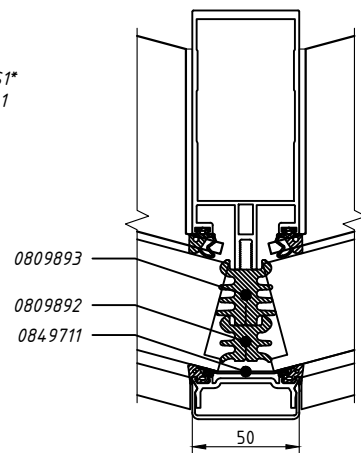

Стойка K2.B3.S2 устанавливается со стоечным сухарем 0345593 во всю длину.

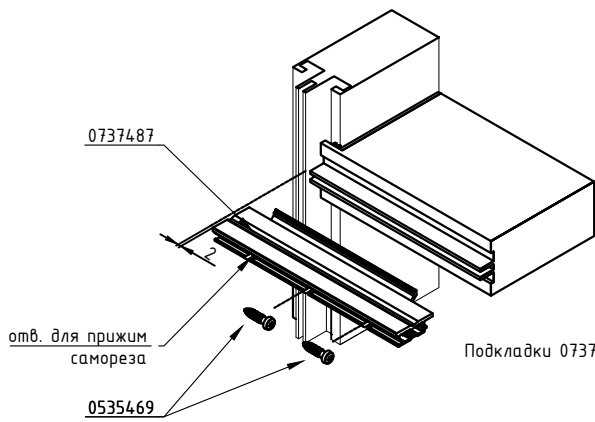

Подкладка 0737487

Подкладки 0737487 напилить из профиля 0340385.

						Остров 2 К1			
						" Многофункциональная комплексная жилая застройка , квартал 2, корпус 1, 2, 3, 4, 5, 6 по адресу : г . Москва , внутригородская территория муниципальный округ Хорошёво –Мнёвники."			
Изм.	Кол.уч.	Лист	№ док	Подп.	Дата	Стеклопрозрачные конструкции		Стация	Лист
Разраб.	Бирюкова				06.23			Р	23
Проверил									
Н. контр.						Угловой витраж В-3.1		ООО "МАРКА ПОЛА"	
Т. контр.									
Утв.									


Копировал

Согласовано
ГАП
ГИП
Инв. и подл.
Подп. и дата
Взам. инв. и
Инв. и подл.

Угловой витраж В-4.1 (развертка).


Кол-во : 20 шт.

S=11,86 м.кв.

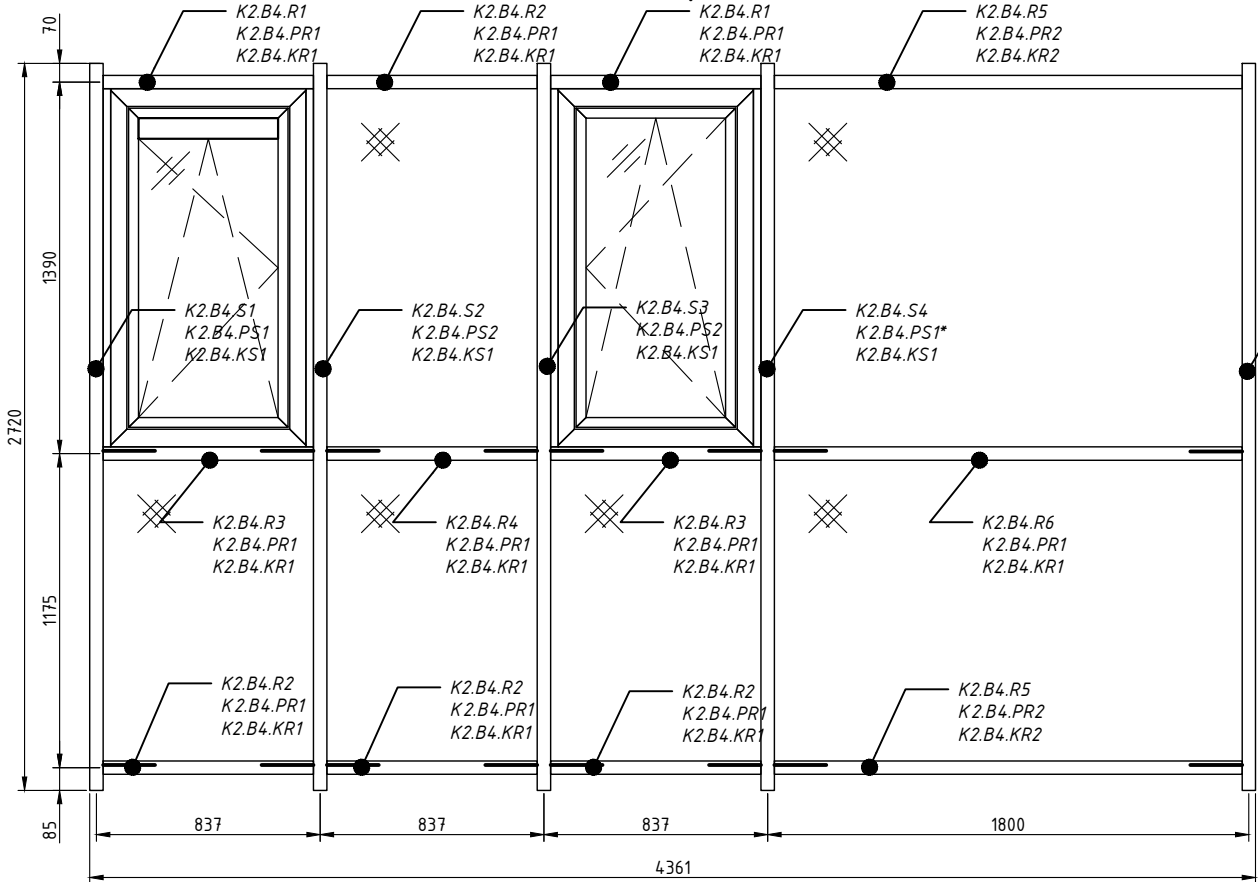


Заполнение термовставки - 0809892 + 0809893.
Под прижимы бутиловая лента - 0849711.
Прижимной саморез:
- прижимы PS1, PS2, PS1* - Ø6,3x67мм - 0535476
- прижимы PS3, PR1, PR2 - Ø6,3x64мм - 0535475

Ригеля крепить саморезом Ø4,2x12,7мм - 0525317

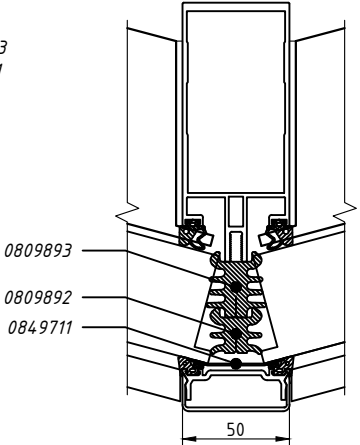

Стойка K2.B2.S2 устанавливается со стоечным сухарем 0345593 во всю длину.

Согласовано	
ГАП	
ГИП	
Инв. № подл.	
Подп. и дата	
Взам. инв. №	

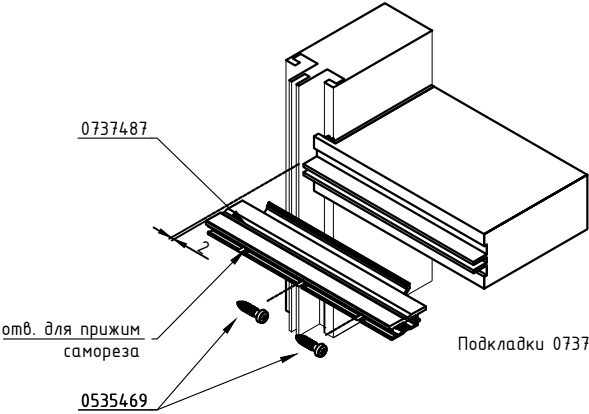

Подкладки 0737487 напилить из профиля 0340385.


						Остров 2 К1			
						" Многофункциональная комплексная жилая застройка , квартал 2, корпус 1, 2, 3, 4, 5, 6 по адресу : г . Москва , внутригородская территория муниципальный округ Хорошёво -Мнёвники."			
Изм.	Кол.уч.	Лист	№ док.	Подп.	Дата	Светопрзрачные конструкции	Стадия	Лист	Листов
Разраб.	Бирюкова				06.23		Р	24	
Проверил									
Н.контр.						Угловой витраж В-4.1	ООО "МАРКА ПОЛА"		
Т.контр.									
Утв.									

Копировал

Угловой витраж В-5.1 (развертка).



Кол-во : 2 шт.

S=8,69 м.кв.

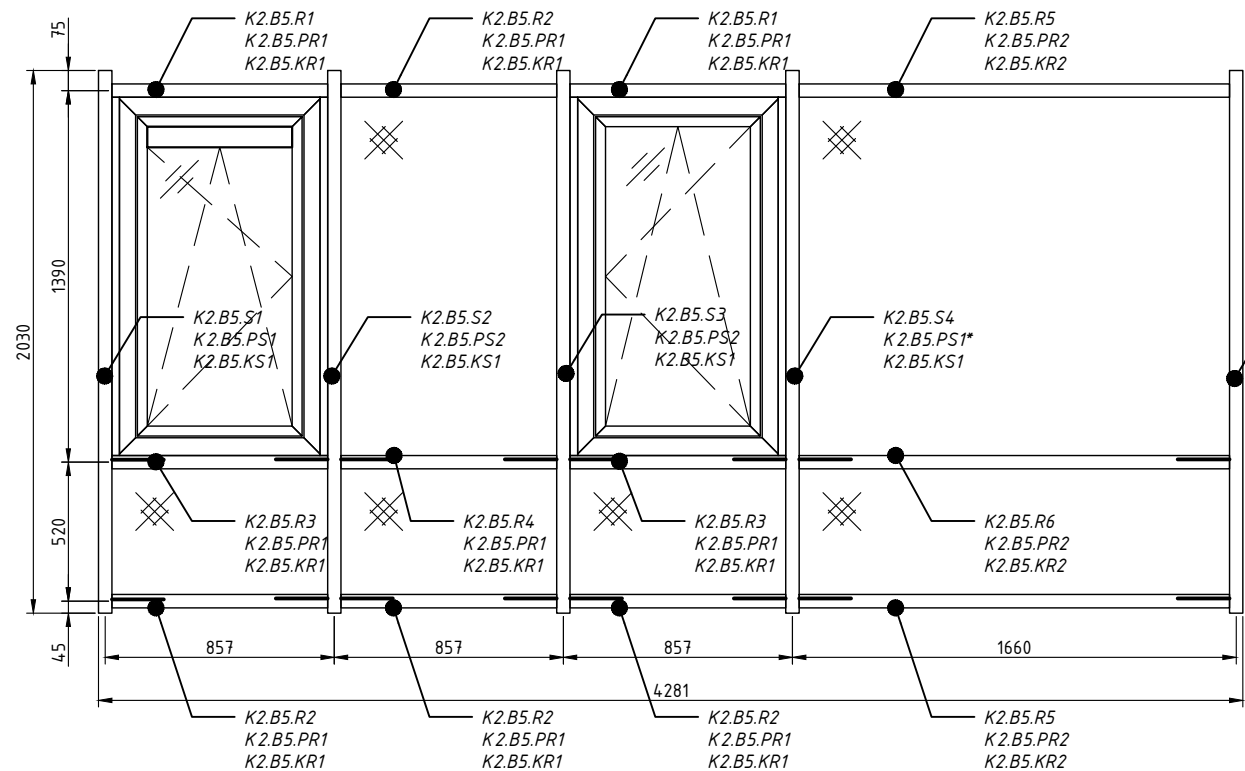

Заполнение термовставки - 0809892 + 0809893.
Под прижимы бутиловая лента - 0849711.
Прижимной саморез:
- прижимы PS1, PS2, PS1* - Ø6,3x67мм - 0535476
- прижимы PS3, PR1, PR2 - Ø6,3x64мм - 0535475

Резеля крепить саморезом Ø4,2x12,7мм - 0525317

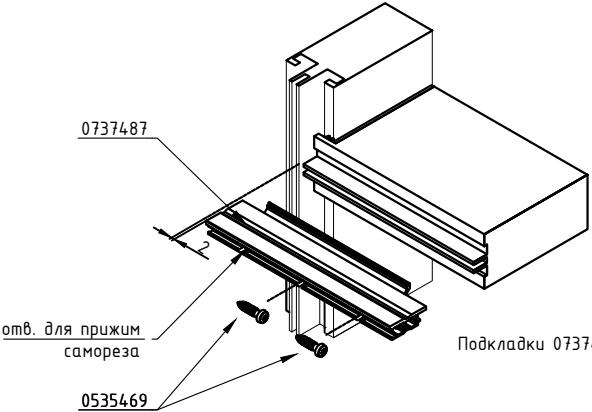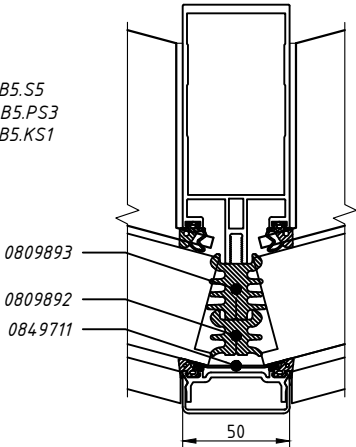

Подкладки 0737487 напилить из профиля 0340385.

Подкладка 0737487

						Остров 2 К1			
						" Многофункциональная комплексная жилая застройка , квартал 2, корпус 1, 2, 3, 4, 5, 6 по адресу : г . Москва , внутригородская территория муниципальный округ Хорошёво -Мнёвники."			
Изм.	Кол.уч.	Лист	№ док.	Подп.	Дата	Светопрозрачные конструкции	Стадия	Лист	Листов
Разраб.	Бирюкова				06.23		Р	25	
Проверил									
Н.контр.						Угловой витраж В-5.1	ООО "МАРКА ПОЛА"		
Т.контр.									
Утв.									

Копировал

Согласовано

ГАП

ГИП

Взам. инв. №


Подп. и дата

Инв. № подл.

Угловой витраж В-6.1 (развертка).



Кол-во : 3 шт.

S=8,83 м.кв.

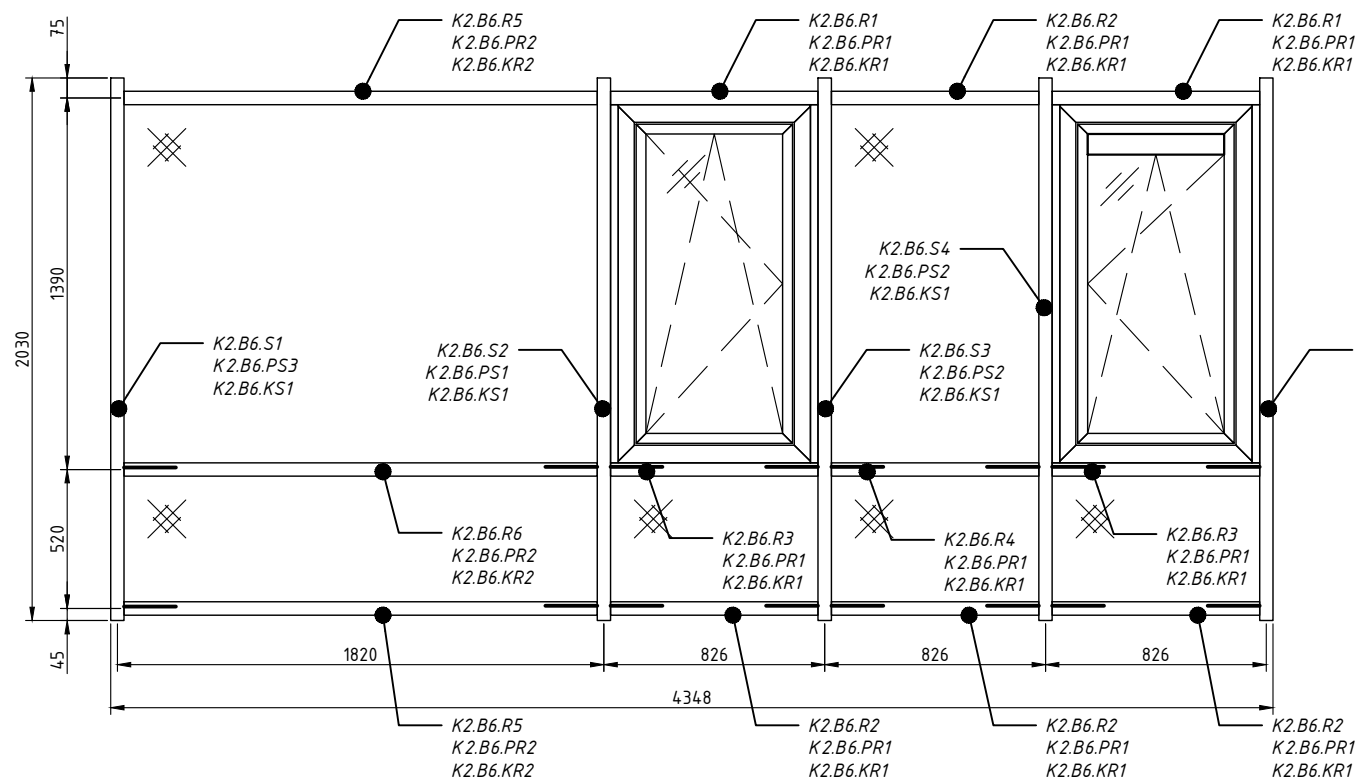

Заполнение термовставки - 0809892 + 0809893.
Под прижимы бутиловая лента - 0849711.
Прижимной саморез:
- прижимы PS1, PS2, PS1* - Ø6,3x67мм - 0535476
- прижимы PS3, PR1, PR2 - Ø6,3x64мм - 0535475

Ригеля крепить саморезом Ø4,2x12,7мм - 0525317

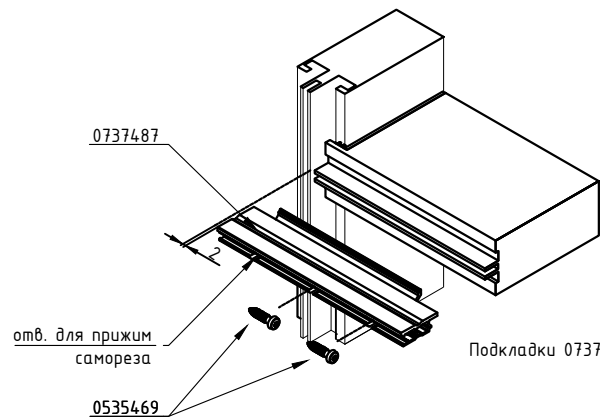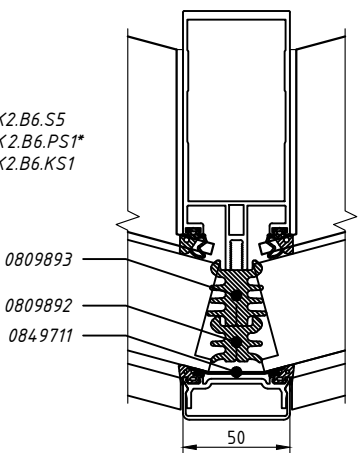

Подкладки 0737487 напилить из профиля 0340385.

Подкладка 0737487


						Остров 2 К1			
						" Многофункциональная комплексная жилая застройка , квартал 2, корпус 1, 2, 3, 4, 5, 6 по адресу : г . Москва , внутригородская территория муниципальный округ Хорошево -Мнёвники."			
Изм.	Кол.уч.	Лист	№ док.	Подп.	Дата	Светопрозрачные конструкции	Стадия	Лист	Листов
Разраб.	Бирюкова				06.23		Р	26	
Проверил									
Н.контр.						Угловой витраж В-6.1	ООО "МАРКА ПОЛА"		
Т.контр.									
Утв.									

Копировал

Угловой витраж В-7 (развертка).

Кол-во: 1 шт.

S=12,5 м.кв.

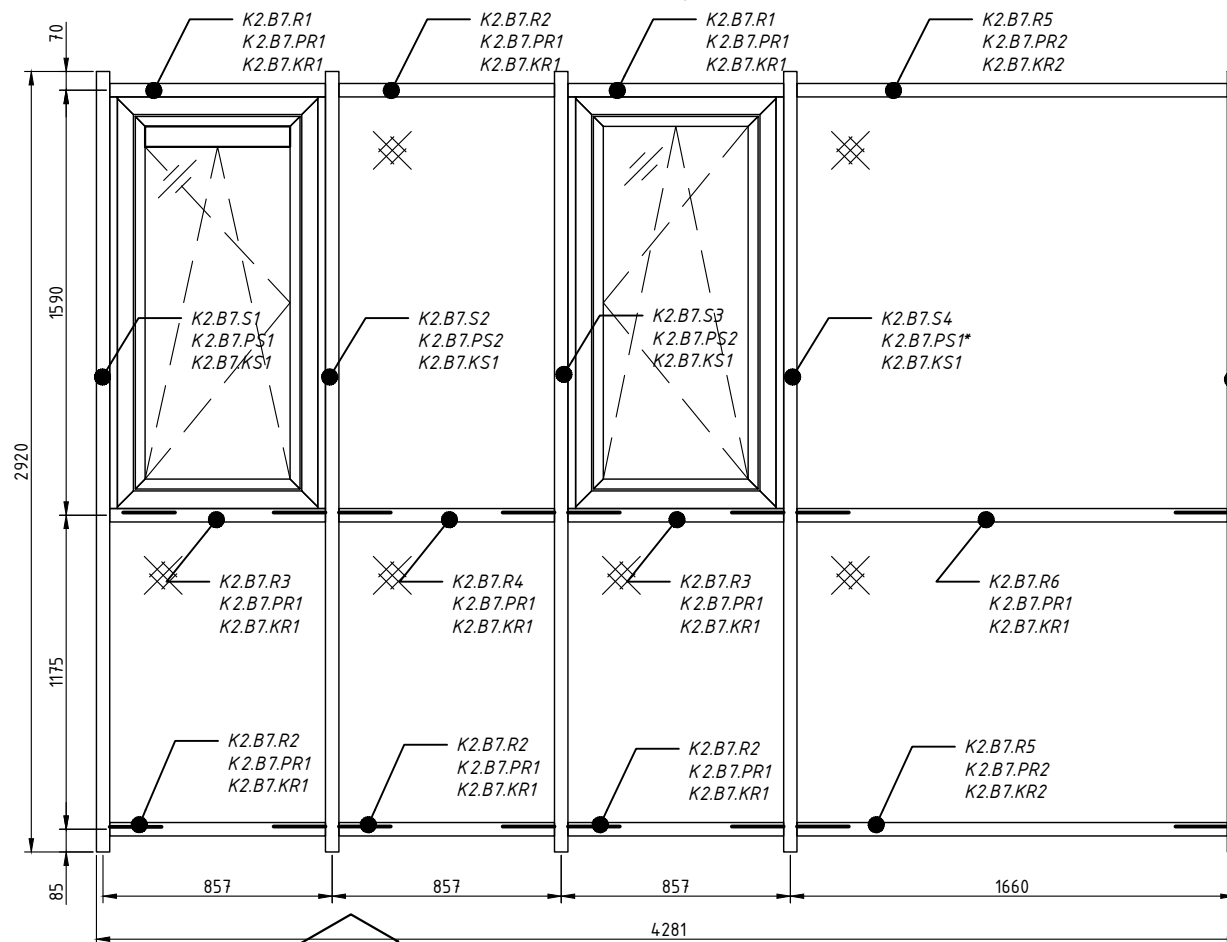


Заполнение термовставки - 0809892 + 0809893.

Под прижимы бутиловая лента - 0849711.


Прижимной саморез:

- прижимы PS1, PS2, PS1* - Ø6,3x67мм - 0535476
- прижимы PS3, PR1, PR2 - Ø6,3x64мм - 0535475

Резеля крепить саморезом Ø4,2x12,7мм - 0525317

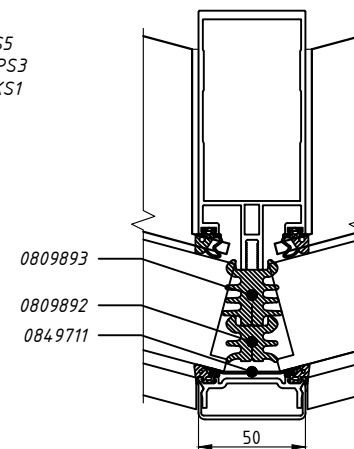

Стойка K2.B7.S4 устанавливается со стоечным сухарем 0345593 во всю длину.

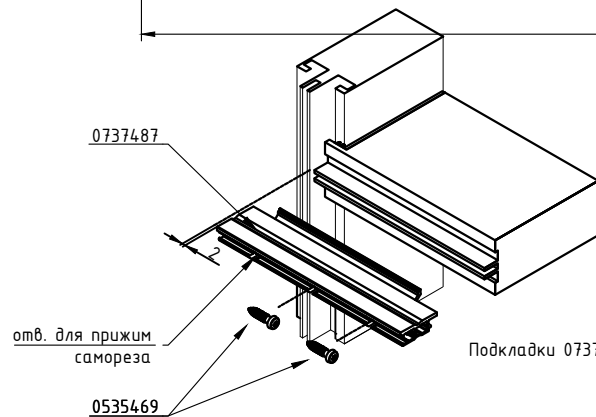

Подкладка 0737487

Подкладки 0737487 напилить из профиля 0340385.

						Остров 2 К1			
						" Многофункциональная комплексная жилая застройка , квартал 2, корпус 1, 2, 3, 4, 5, 6 по адресу : г . Москва , внутригородская территория муниципальный округ Хорошёво -Мнёвники."			
Изм.	Кол.уч.	Лист	№ док.	Подп.	Дата	Светопрозрачные конструкции	Стадия	Лист	Листов
Разраб.	Бирюкова				06.23		Р	27	
Проверил									
Н.контр.									
Т.контр.						Угловой витраж В-7		ООО "МАРКА ПОЛА"	
Утв.									


Копировал

Согласовано					
ГАП					
ГИП					
Инв. N подл.	Подп. и дата	Взам. инв. N			

Угловой витраж В-8.1 (развертка).


Кол-во: 1 шт.

S=12,44 м.кв.

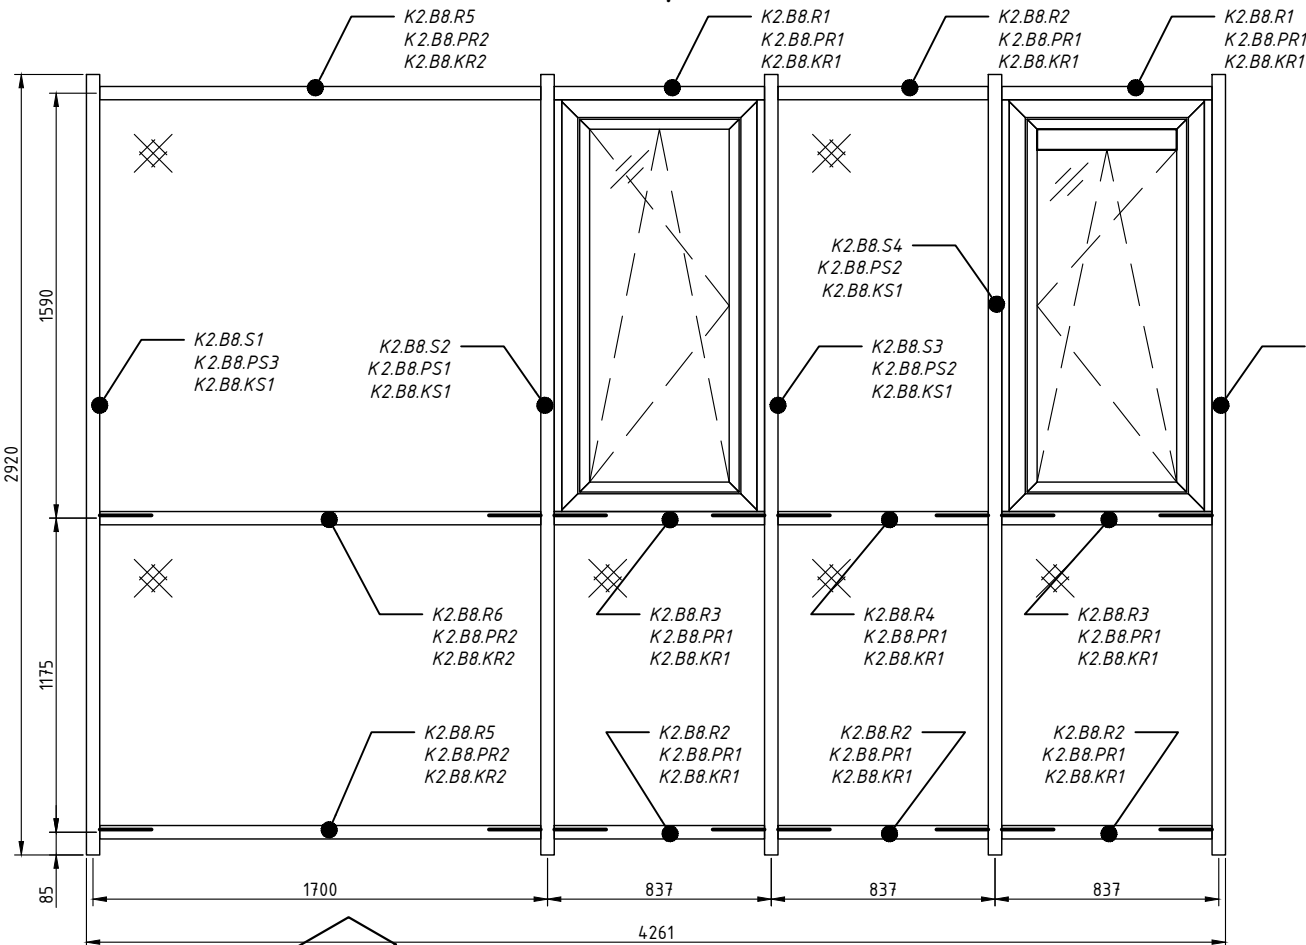


Заполнение термовставки - 0809892 + 0809893.
Под прижимы бутиловая лента - 0849711.
Прижимной саморез:
- прижимы PS1, PS2, PS1* - Ø6,3x67мм - 0535476
- прижимы PS3, PR1, PR2 - Ø6,3x64мм - 0535475

Резеля крепить саморезом Ø4,2x12,7мм - 0525317

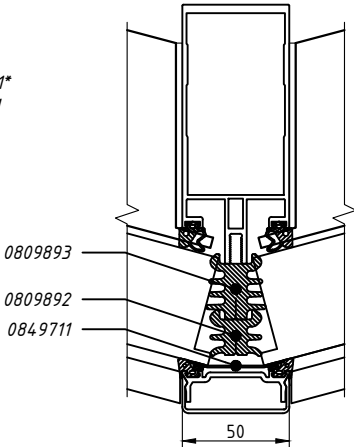

Стойка K2.B8.S2 устанавливается со стоечным сухарем 0345593 во всю длину.

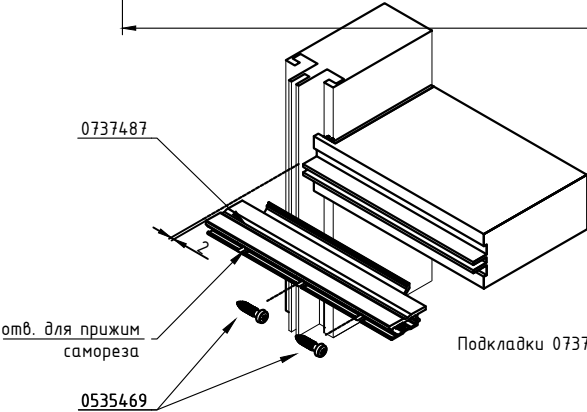

Подкладка 0737487

Подкладки 0737487 напилить из профиля 0340385.

						Остров 2 К1			
						“ Многофункциональная комплексная жилая застройка , квартал 2, корпус 1, 2, 3, 4, 5, 6 по адресу : г . Москва , внутригородская территория муниципальный округ Хорошёво -Мнёвники.”			
Изм.	Кол.уч.	Лист	№ док.	Подп.	Дата	Светопрозрачные конструкции	Стадия	Лист	Листов
Разраб.	Бирюкова				06.23		Р	28	
Проверил									
Н.контр.									
Т.контр.						Угловой витраж В-8.1	ООО “МАРКА ПОЛА”		
Утв.									


Копировал

Согласовано					
ГАП					
ГИП					
Инв. N подл.	Подп. и дата	Взам. инв. N			

Угловой витраж В-9.1 (развертка).


Кол-во: 1 шт.

S=12,70 м.кв.

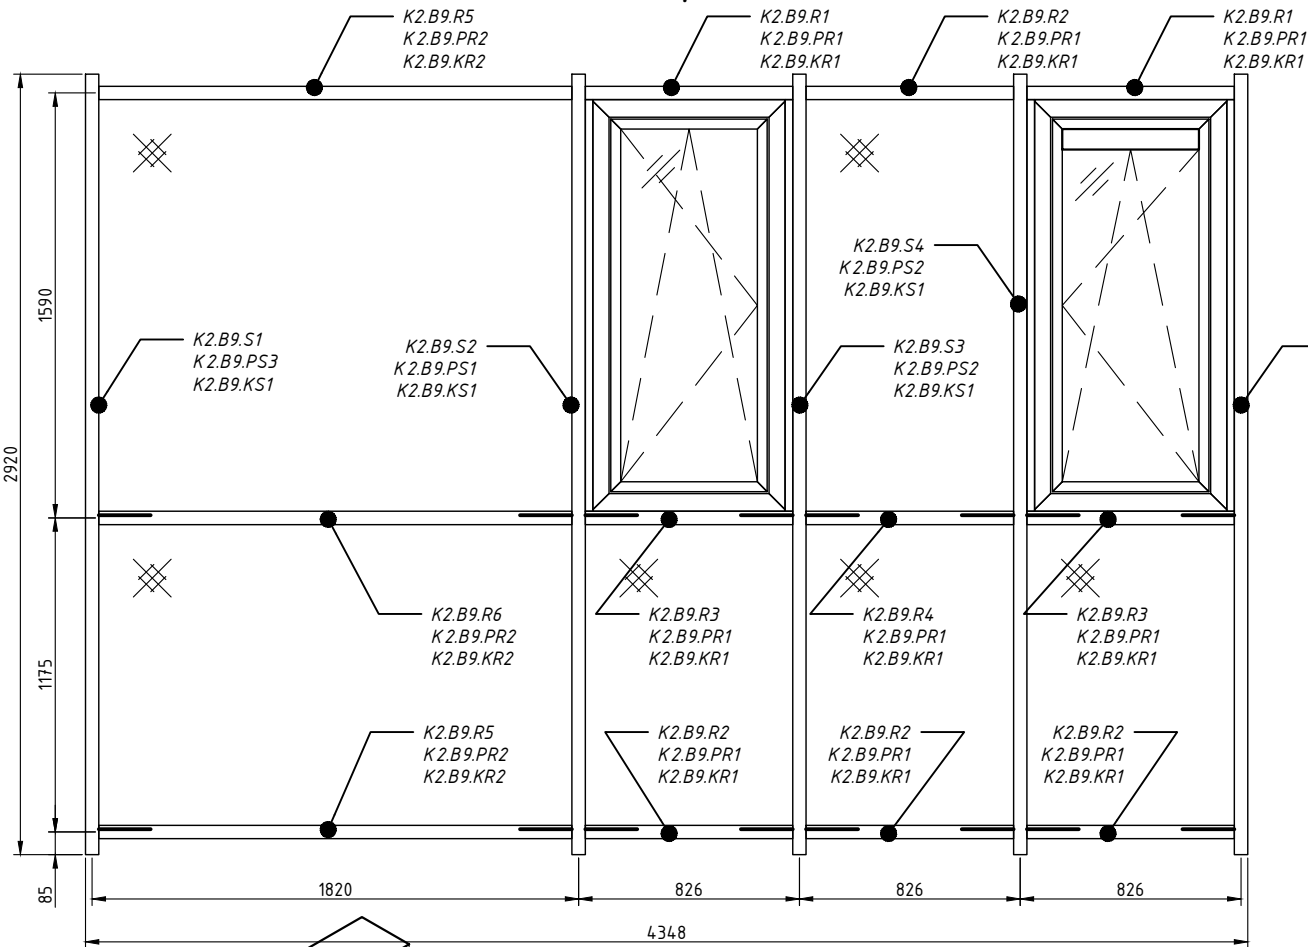


Заполнение термовставки - 0809892 + 0809893.
Под прижимы бутиловая лента - 0849711.
Прижимной саморез:
- прижимы PS1, PS2, PS1* - Ø6,3x67мм - 0535476
- прижимы PS3, PR1, PR2 - Ø6,3x64мм - 0535475

Ригеля крепить саморезом Ø4,2x12,7мм - 0525317

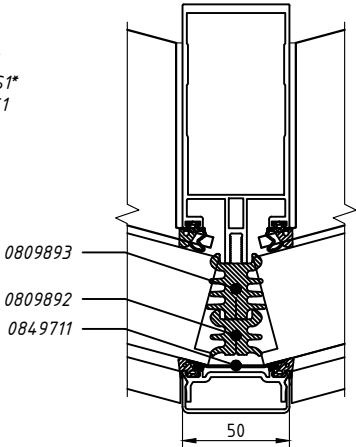

Стойка K2.B9.S2 устанавливается со стоечным сухарем 0345593 во всю длину.

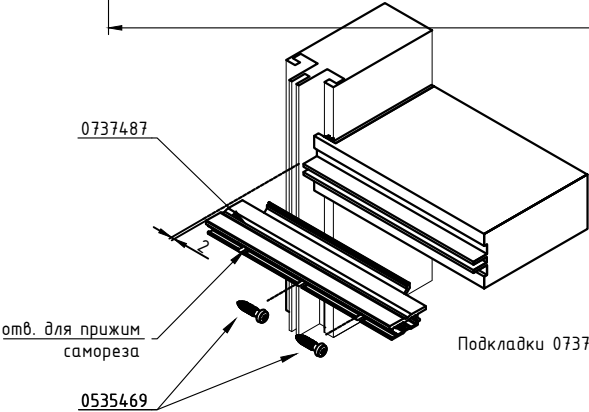

Подкладка 0737487

Подкладки 0737487 напилить из профиля 0340385.

						Остров 2 К1			
						“ Многофункциональная комплексная жилая застройка , квартал 2, корпус 1, 2, 3, 4, 5, 6 по адресу : г . Москва , внутригородская территория муниципальный округ Хорошёво -Мнёвники.”			
Изм.	Кол.уч.	Лист	№ док.	Подп.	Дата	Светопрозрачные конструкции	Стадия	Лист	Листов
Разраб.	Бирюкова				06.23		Р	29	
Проверил									
Н.контр.						Угловой витраж В-9.1	ООО “МАРКА ПОЛА”		
Т.контр.									
Утв.									

Копировал

Согласовано

ГАП

ГИП

Взам. инв. №


Подп. и дата

Инв. № подл.

Угловой витраж В-10 (развертка).

Кол-во: 1 шт.

S=12,73 м.кв.

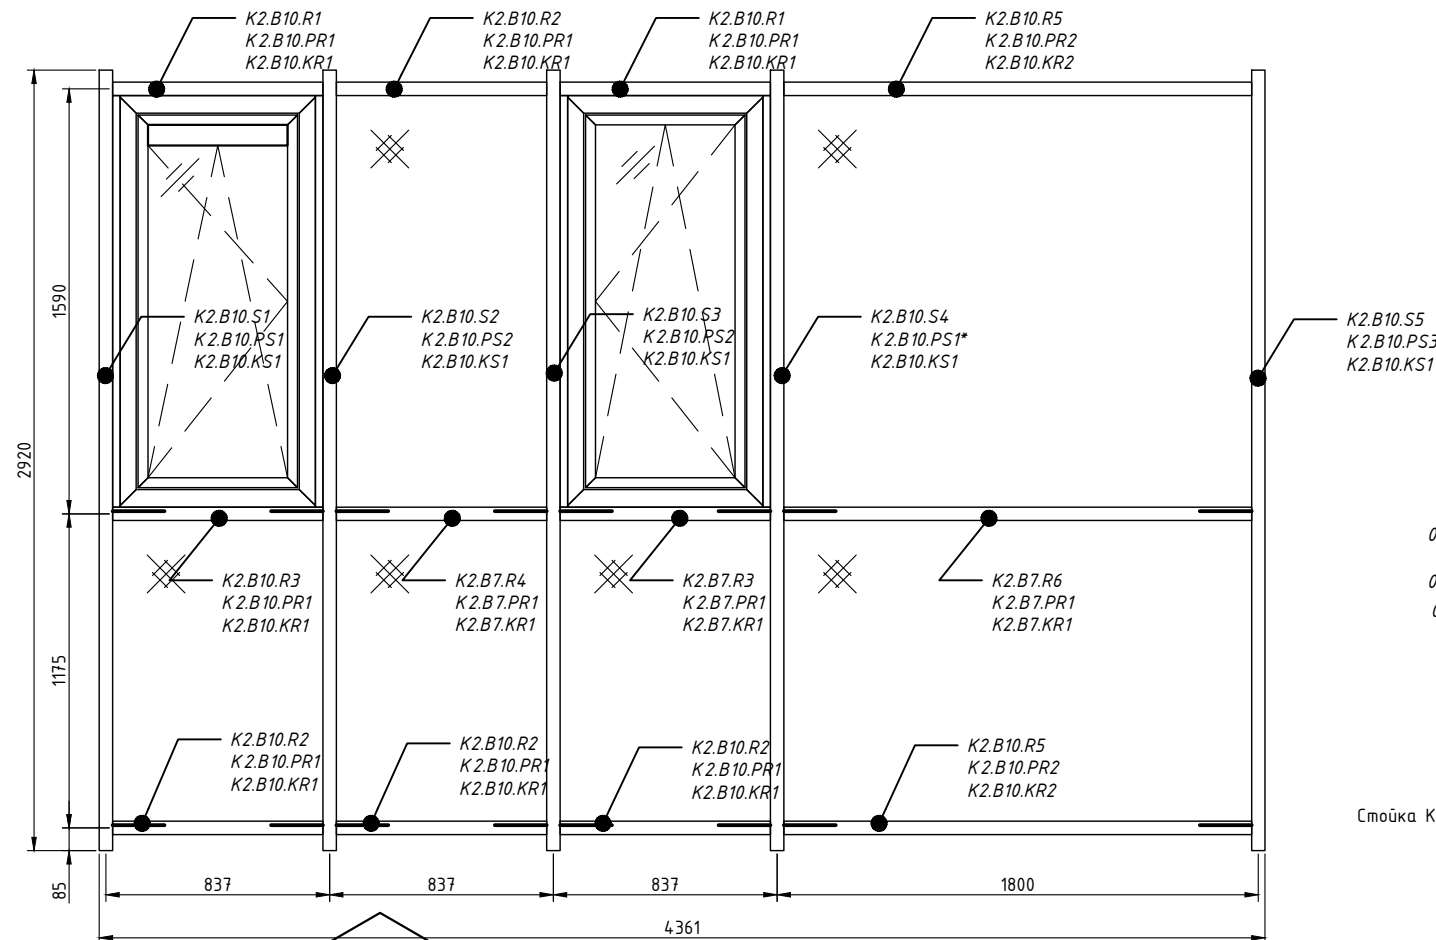


Заполнение термовставки - 0809892 + 0809893.

Под прижимы бутиловая лента - 0849711.


Прижимной саморез:

- прижимы PS1, PS2, PS1* - Ø6,3x67мм - 0535476
- прижимы PS3, PR1, PR2 - Ø6,3x64мм - 0535475

Ригеля крепить саморезом Ø4,2x12,7мм - 0525317

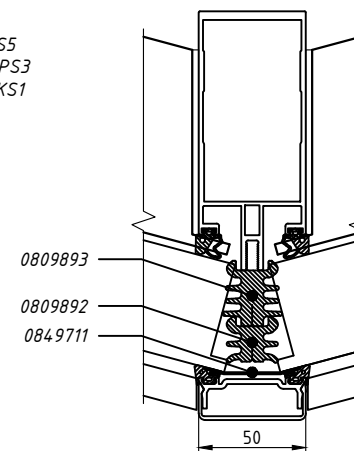

Стойка K2.B10.S4 устанавливается со стоечным сухарем 0345593 во всю длину.

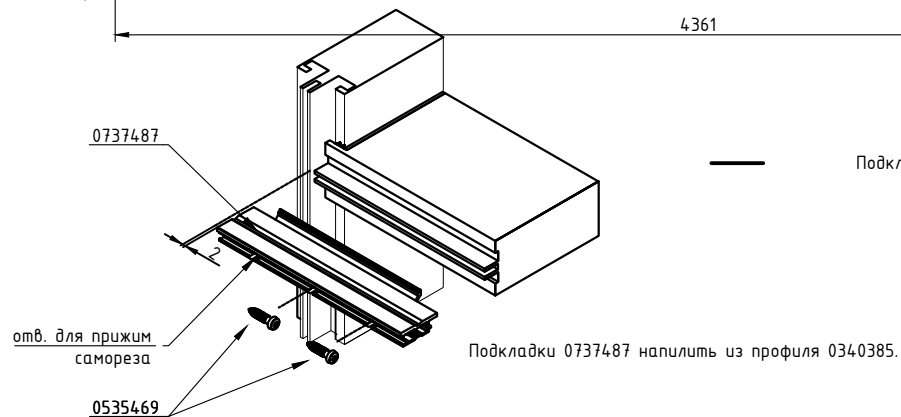

Подкладка 0737487

Подкладки 0737487 напилить из профиля 0340385.

						Остров 2 К1			
						" Многофункциональная комплексная жилая застройка , квартал 2, корпус 1, 2, 3, 4, 5, 6 по адресу : г . Москва , внутригородская территория муниципальный округ Хорошёво -Мнёвники."			
Изм.	Кол.уч.	Лист	№ док.	Подп.	Дата	Светопрозрачные конструкции	Стадия	Лист	Листов
Разраб.	Бирюкова				06.23		Р	30	
Проверил									
Н.контр.						Угловой витраж В-10	ООО "МАРКА ПОЛА"		
Т.контр.									
Утв.									


Копировал

Согласовано					
ГАП					
ГИП					
Инв. N подл.	Подп. и дата	Взам. инв. N			

Согласовано			Взам. инв. №		Подп. и дата		Инв. № подл.	
	ГАП	ГИП						


Маркировка:
K2.B1.S5 – 18 шт. (зеркально)
K2.B2.S1 – 20 шт
K2.B3.S1 – 17 шт.
K2.B4.S5 – 20 шт. (зеркально)

Цвет: 79 7M15

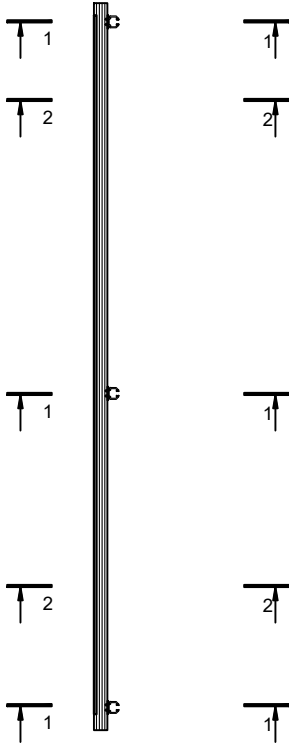



Маркировка:
K2.B1.S4 – 18 шт. (зеркально)
K2.B2.S2 – 20 шт
K2.B3.S2 – 17 шт.
K2.B4.S4 – 20 шт. (зеркально)

Цвет: 79 7M15

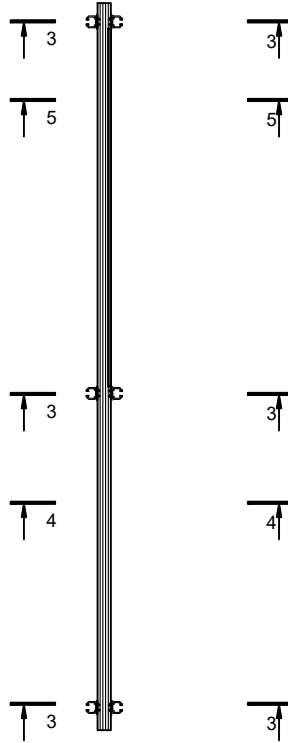







Примечание.

1. Каждую стойку перед производством работ оклеить защитной пленкой,замаркировать номером стойки и укомплектовать уплотнителями и филлистрами
2. Стойки укомплектовать подпятниками из 034.5593 L=200 мм и дренажным лотком 073.8263.04 на винт 050.5029.--
3. Манжету 080.9885 и сухарь РС-2 установить на производсве по шаблону. Манжету подрезать по торцу ригеля.
4. Ригельные сухари РС-1 и РС-2 устанавливать на саморез Ø4,8x13 – 0525330.

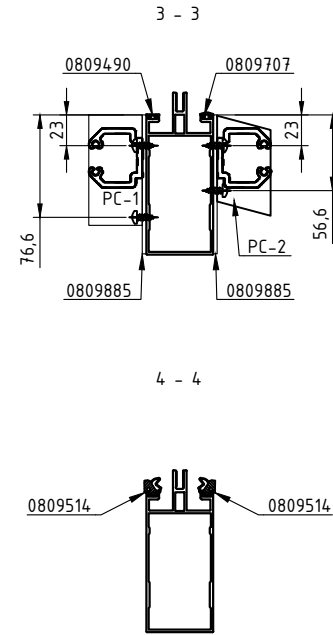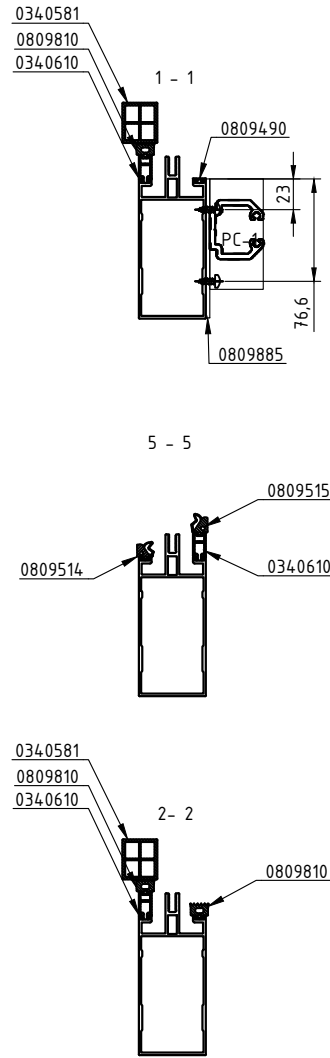

							Остров 2 К1			
							" Многофункциональная комплексная жилая застройка , квартал 2, корпус 1, 2, 3, 4, 5, 6 по адресу : г . Москва , внутригородская территория муниципальный округ Хорошёво –Мнёвники."			
Изм.	Кол.уч.	Лист	№ док.	Подп.	Дата		Светопрзрачные конструкции	Стадия	Лист	Листов
Разраб.	Бирюкова				06.23			Р	31	
Проверил										
Н. контр.							Стойки В1.1, В2.1, В3.1, В4.1	ООО "МАРКА ПОЛА"		
Т. контр.										
Утв.										

Копировал

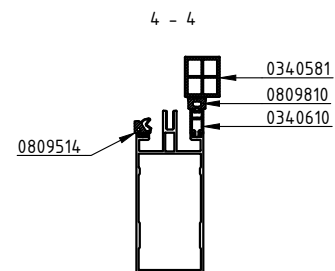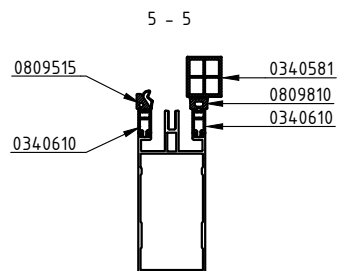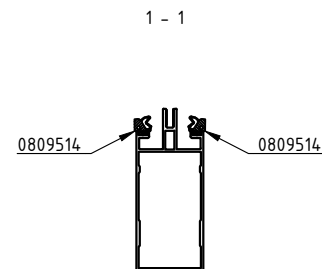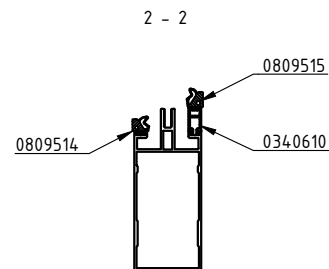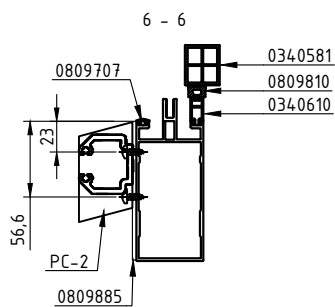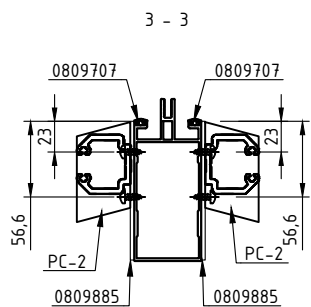


Маркировка:
K2.B1.S3 - 18 шт.
K2.B1.S2 - 18шт (зеркально)
K2.B2.S4 - 20 шт.
K2.B2.S3 - 20шт (зеркально)
K2.B3.S4 - 17 шт.
K2.B3.S3 - 17шт (зеркально)
K2.B4.S3 - 20 шт.
K2.B4.S2 - 20шт (зеркально)

Цвет: 79 7M15

Маркировка:
K2.B1.S1 - 18 шт. (зеркально)
K2.B2.S5 - 20 шт
K2.B3.S5 - 17 шт.
K2.B4.S1 - 20 шт. (зеркально)

Цвет: 79 7M15

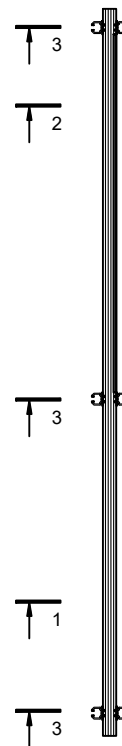

Примечание.

1. Каждую стойку перед производством работ оклеить защитной пленкой, замаркировать номером стойки и укомплектовать уплотнителями и филлистрами
2. Стойки укомплектовать подпятниками из 034.5593 L=200 мм и дренажным лотком 073.8263.04 на винт 050.5029.--
3. Манжету 080.9885 и сухарь PC-2 установить на производстве по шаблону. Манжету подрезать по торцу ригеля.
4. Ригельные сухари PC-1 и PC-2 устанавливать на саморез Ø4,8x13 - 0525330.


						Остров 2 К1			
						" Многофункциональная комплексная жилая застройка , квартал 2, корпус 1, 2, 3, 4, 5, 6 по адресу : г . Москва , внутригородская территория муниципальный округ Хорошёво -Мнёвники."			
Изм.	Кол.уч.	Лист	№ док.	Подп.	Дата	Светопрзрачные конструкции	Стадия	Лист	Листов
Разраб.	Бирюкова				06.23		Р	32	
Проверил									
Н.контр.						Стойки В1.1, В2.1, В3.1, В4.1	ООО "МАРКА ПОЛА"		
Т.контр.									
Утв.									

Копировал

Согласовано	ГАП	
	ГИП	
Взам. инв. №		
Подп. и дата		
Инв. № подл.		


Маркировка:
K2.B5.S5 – 2 шт. (зеркально)
K2.B6.S1 – 3 шт

Цвет: 79 7M15

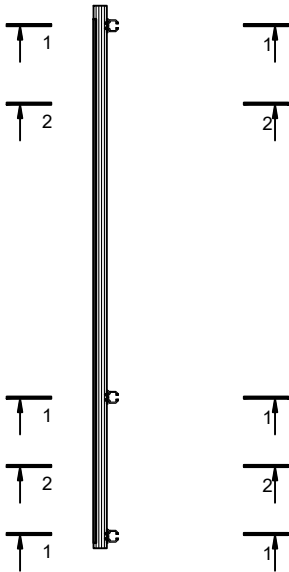


Маркировка:
K2.B5.S4 – 2 шт. (зеркально)
K2.B6.S2 – 3 шт



Цвет: 79 7M15

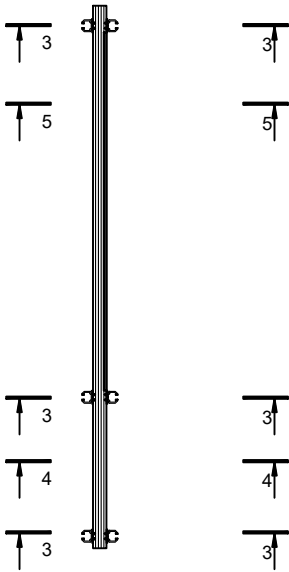


- Примечание.
1. Каждую стойку перед производством работ оклеить защитной пленкой,замаркировать номером стойки и укомплектовать уплотнителями и филлистрами
 2. Стойки укомплектовать подпятниками из 034.5593 L=200 мм и дренажным лотком 073.8263.04 на винт 050.5029.--
 3. Манжету 080.9885 и сухарь РС-2 установить на производстве по шаблону. Манжету подрезать по торцу ригеля.
 4. Ригельные сухари РС-1 и РС-2 устанавливать на саморез Ø4,8x13 – 0525330.

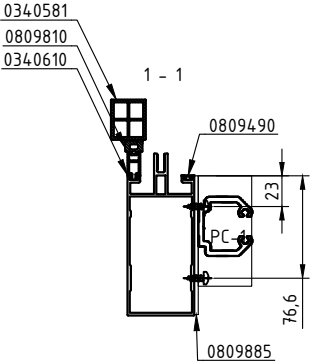


5 - 5

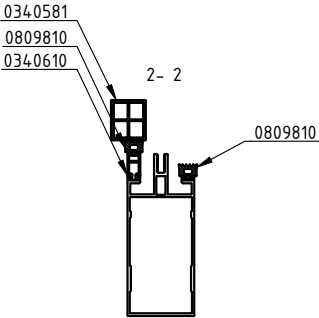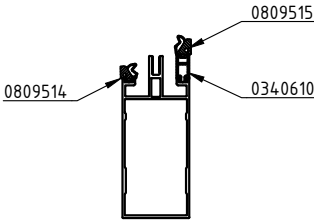







3 - 3

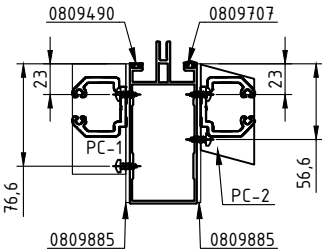

4 - 4

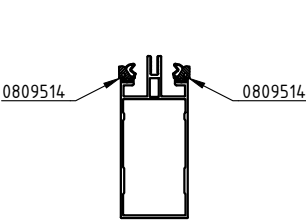


Остров 2 К1						
" Многофункциональная комплексная жилая застройка , квартал 2, корпус 1, 2, 3, 4, 5, 6 по адресу : г . Москва , внутригородская территория муниципальный округ Хорошёво –Мнёвники."						
Изм.	Кол.уч.	Лист	№ док.	Подп.	Дата	
Разраб.	Бирюкова				06.23	
Проверил						
Н.контр.						
Стойки B5.1, B6.1						000 "МАРКА ПОЛА"
Т.контр.						
Утв.						

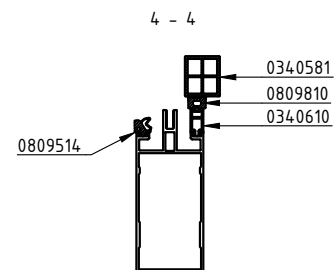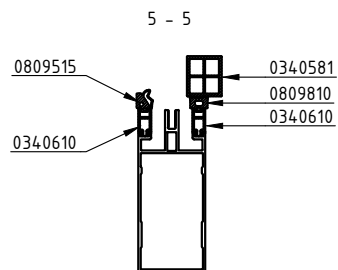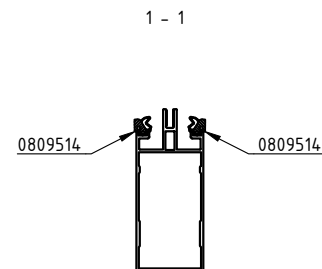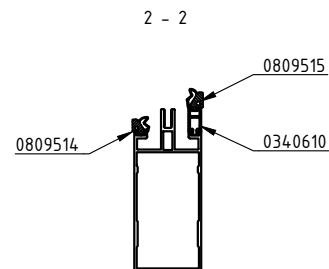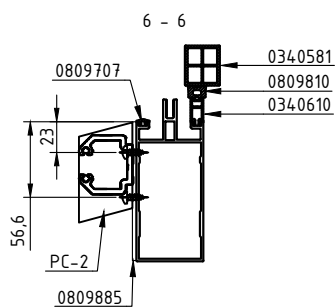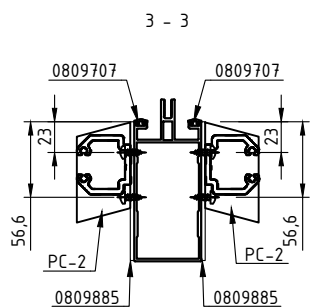

Маркировка:
K2.B5.S3 – 2 шт.
K2.B5.S2 – 2шт (зеркально)
K2.B6.S4 – 3 шт.
K2.B6.S3 – 3шт (зеркально)

Цвет: 79 7M15

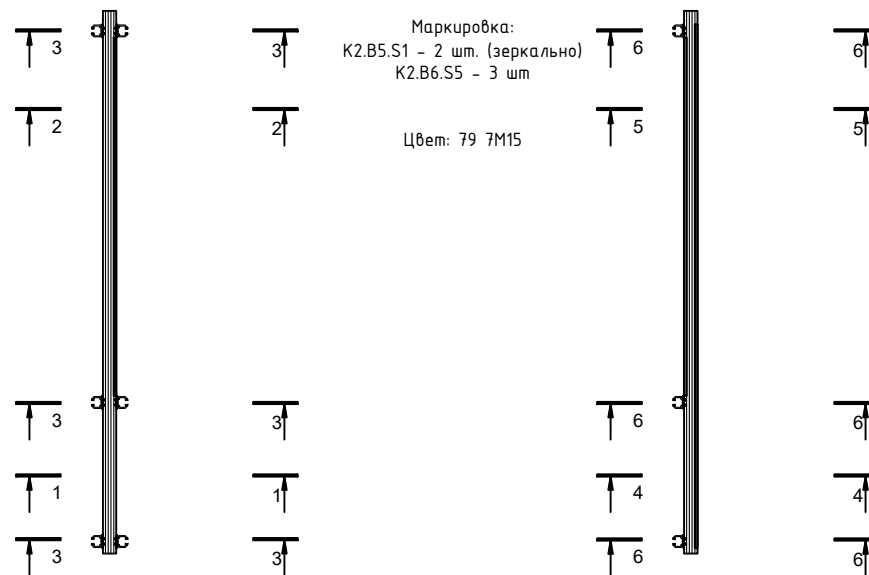

Маркировка:
K2.B5.S1 – 2 шт. (зеркально)
K2.B6.S5 – 3 шт

Цвет: 79 7M15

Примечание.

1. Каждую стойку перед производством работ оклеить защитной пленкой, замаркировать номером стойки и укомплектовать уплотнителями и филлистрами
2. Стойки укомплектовать подпятниками из 034.5593 L=200 мм и дренажным лотком 073.8263.04 на винт 050.5029.--
3. Манжету 080.9885 и сухарь PC-2 установить на производстве по шаблону. Манжету подрезать по торцу ригеля.
4. Ригельные сухари PC-1 и PC-2 устанавливать на саморез Ø4,8x13 – 0525330.

						Остров 2 К1			
						" Многофункциональная комплексная жилая застройка , квартал 2, корпус 1, 2, 3, 4, 5, 6 по адресу : г . Москва , внутригородская территория муниципальный округ Хорошёво –Мнёвники."			
Изм.	Кол.уч.	Лист	№ док.	Подп.	Дата	Светопрозрачные конструкции	Стадия	Лист	Листов
Разраб.	Бирюкова				06.23		Р	34	
Проверил									
Н.контр.						Стойки B5.1, B6.1	ООО "МАРКА ПОЛА"		
Т.контр.									
Утв.									


Копировал

Согласовано					
ГАП					
ГИП					
Взам. инв. Н					
Подп. и дата					
Инв. Н подл.					

Согласовано				
	ГАП			
	ГИП			
Инв. N подл.	Подп. и дата	Взам. инв. N		


Маркировка:
K2.B7.S5 – 1 шт. (зеркально)
K2.B8.S1 – 1 шт
K2.B9.S1 – 1 шт.
K2.B10.S5 – 1 шт. (зеркально)

Цвет: 79 7M15





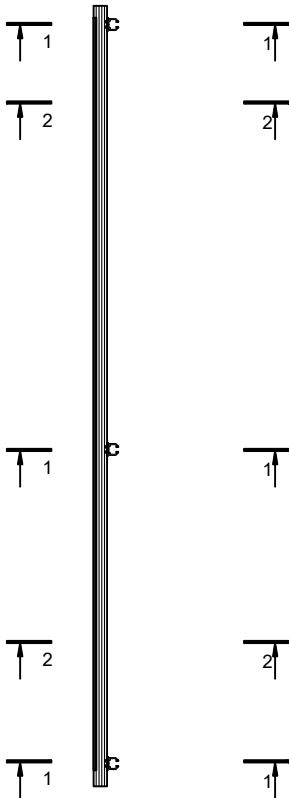


Маркировка:
K2.B7.S4 – 1 шт. (зеркально)
K2.B8.S2 – 1 шт
K2.B9.S2 – 1 шт.
K2.B10.S4 – 1 шт. (зеркально)

Цвет: 79 7M15

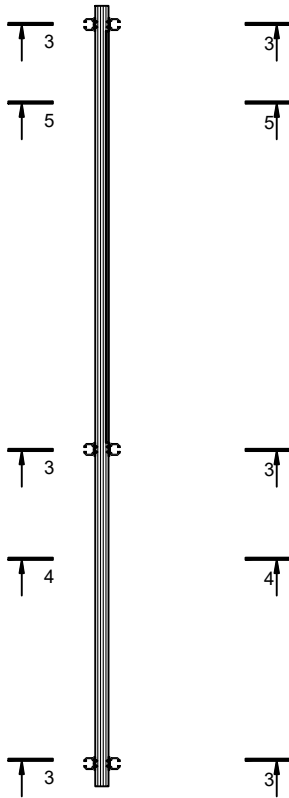







- Примечание.
1. Каждую стойку перед производством работ оклеить защитной пленкой, замаркировать номером стойки и укомплектовать уплотнителями и флистрами
 2. Стойки укомплектовать подпятниками из 034.5593 L=200 мм и дренажным лотком 073.8263.04 на винт 050.5029.--
 3. Манжету 080.9885 и сухарь РС-2 установить на производстве по шаблону. Манжету подрезать по торцу ригеля.
 4. Ригельные сухари РС-1 и РС-2 устанавливать на саморез Ø4,8x13 – 0525330.

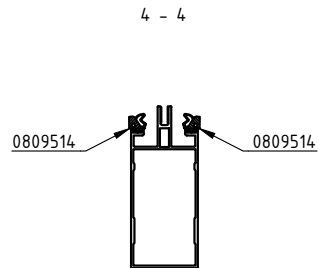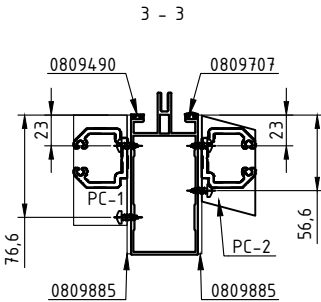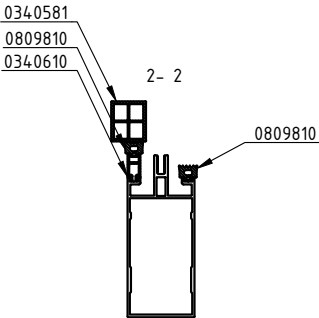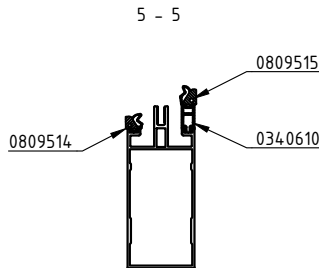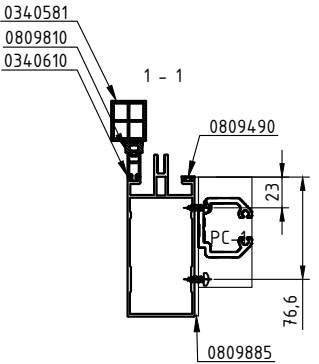

						Остров 2 К1			
						" Многофункциональная комплексная жилая застройка , квартал 2, корпус 1, 2, 3, 4, 5, 6 по адресу : г . Москва , внутригородская территория муниципальный округ Хорошёво –Мнёвники."			
Изм.	Кол.уч.	Лист	№ док.	Подп.	Дата	Светопрозрачные конструкции	Стадия	Лист	Листов
Разраб.	Бирюкова				06.23		Р	35	
Проверил									
Н. контр.						Стойки В7, В8.1, В9.1, В10	ООО "МАРКА ПОЛА"		
Т. контр.									
Утв.									

Копировал


Инв. N подл.	Подп. и дата	Взам. инв. N	Согласовано	
			ГАП	ГИП

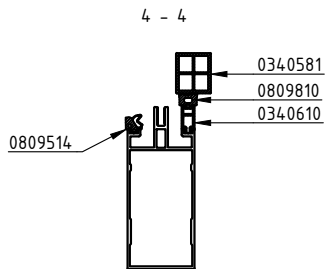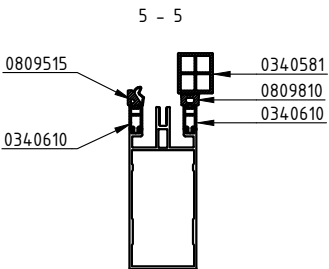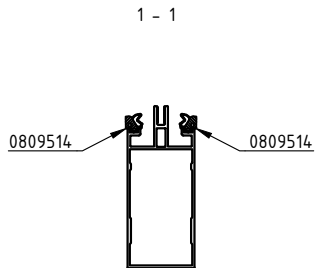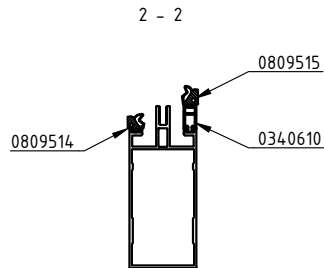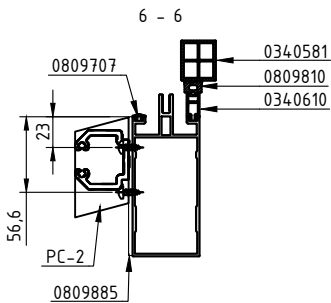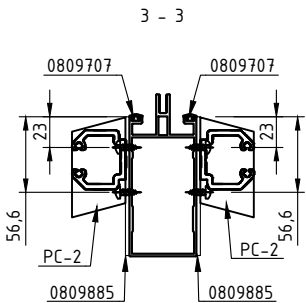

Маркировка:
 K2.B7.S3 - 1 шт.
 K2.B7.S2 - 1шт (зеркально)
 K2.B8.S4 - 1 шт.
 K2.B8.S3 - 1шт (зеркально)
 K2.B9.S4 - 1 шт.
 K2.B9.S3 - 1шт (зеркально)
 K2.B10.S3 - 1 шт.
 K2.B10.S2 - 1шт (зеркально)

Цвет: 79 7M15

Маркировка:
 K2.B7.S1 - 1 шт. (зеркально)
 K2.B8.S5 - 1 шт
 K2.B9.S5 - 1 шт.
 K2.B10.S1 - 1 шт. (зеркально)
 Цвет: 79 7M15


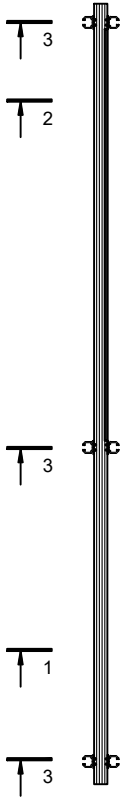


Примечание.
 1. Каждую стойку перед производством работ оклеить защитной пленкой,замаркировать номером стойки и укомплектовать уплотнителями и филлистрами
 2. Стойки укомплектовать подпятниками из 034.5593 L=200 мм и дренажным лотком 073.8263.04 на винт 050.5029.--
 3. Манжету 080.9885 и сухарь PC-2 установить на производстве по шаблону. Манжету подрезать по торцу ригеля.
 4. Ригельные сухари PC-1 и PC-2 устанавливать на саморез Ø4,8x13 - 0525330.


						Остров 2 К1			
						" Многофункциональная комплексная жилая застройка , квартал 2, корпус 1, 2, 3, 4, 5, 6 по адресу : г . Москва , внутригородская территория муниципальный округ Хорошёво –Мнёвники."			
Изм.	Кол.уч.	Лист	№ док.	Подп.	Дата	Светопрзрачные конструкции	Стадия	Лист	Листов
Разраб.	Бирюкова				06.23		Р	36	
Проверил									
Н.контр.						Стойки В7, В8.1, В9.1, В10	ООО "МАРКА ПОЛА"		
Т.контр.									
Утв.									

Копировал


Профиль ригеля 0343524
Цвет: 79 7M15

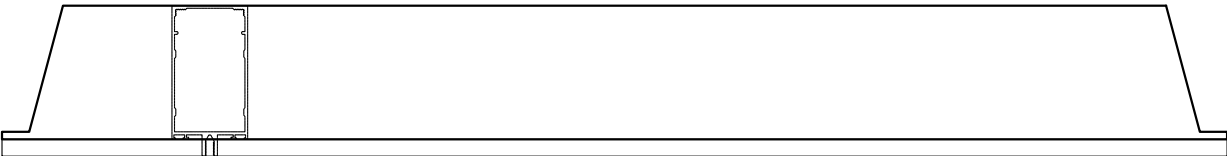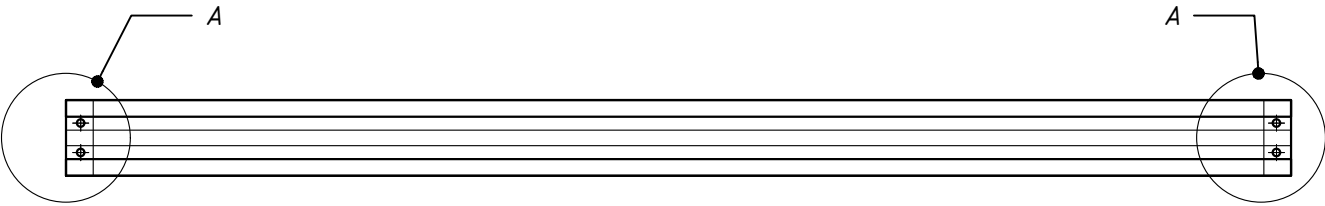

Маркировка		L, мм	Кол-во
K2.B1.R1		794,2	36
K2.B2.R1		774,2	40
K2.B3.R1		763,2	34
K2.B4.R1		774,2	40
K2.B5.R1		794,2	4
K2.B6.R1		763,2	6
K2.B7.R1		794,2	2
K2.B8.R1		774,2	2
K2.B9.R1		763,2	2
K2.B10.R1		774,2	2

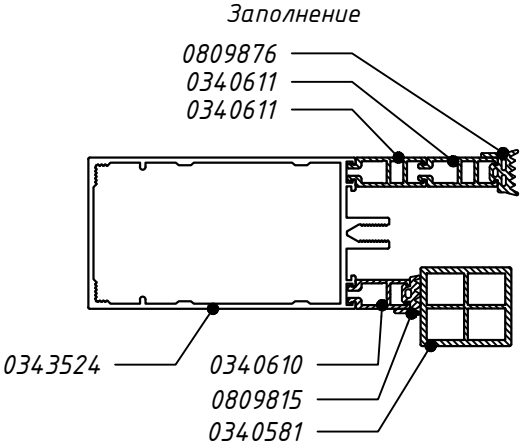

Одп. А (2:1)

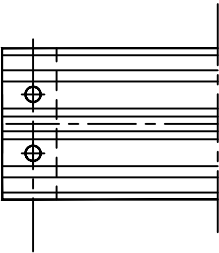

Примечание.
1. Каждый ригель перед производством работ оклеить защитной пленкой, замаркировать номером стойки и укомплектовать уплотнителями и флистрами

Согласовано

ГАП
ГИП



Взам. инв. №

Подп. и дата

Инв. № подл.


Изм.	Кол.уч.	Лист	№ док.	Подп.	Дата	Остров 2 К1			
Разраб.	Бирюкова				06.23	" Многофункциональная комплексная жилая застройка , квартал 2, корпус 1, 2, 3, 4, 5, 6 по адресу : г . Москва , внутригородская территория муниципальный округ Хорошёво –Мнёвники."			
Проверил						Светопрозрачные конструкции	Стадия	Лист	Листов
Н.контр.							Р	37	
Т.контр.						Ригели	ООО "МАРКА ПОЛА"		
Утв.									

Профиль ригеля 0343524
Цвет: 79 7M15

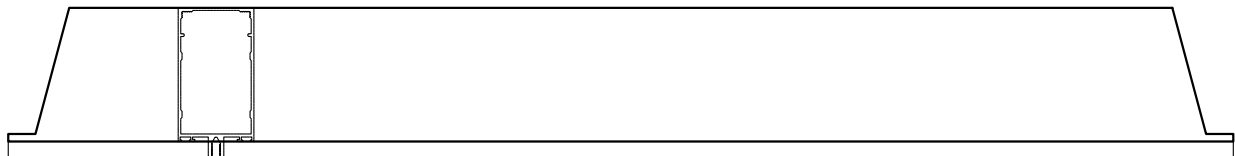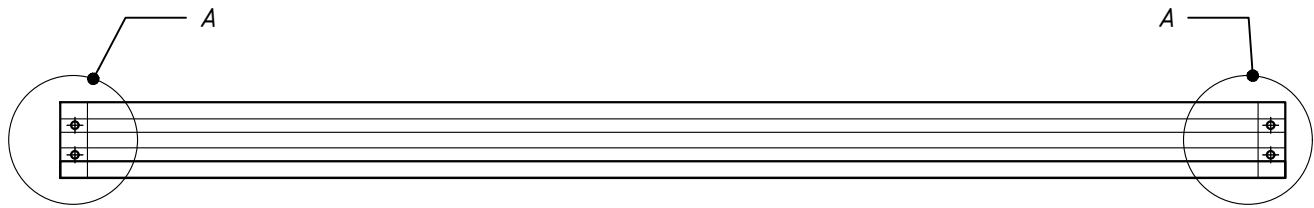


Маркировка		L, мм	Кол-во
K2.B1.R2		794,2	72
K2.B2.R2		774,2	80
K2.B3.R2		763,2	68
K2.B4.R2		774,2	80
K2.B5.R2		794,2	8
K2.B6.R2		763,2	12
K2.B7.R2		794,2	4
K2.B8.R2		774,2	4
K2.B9.R2		763,2	4
K2.B10.R2		774,2	4

Обр. А (2:1)

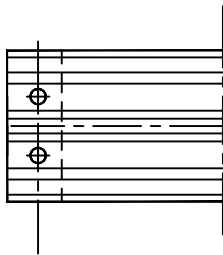

Заполнение

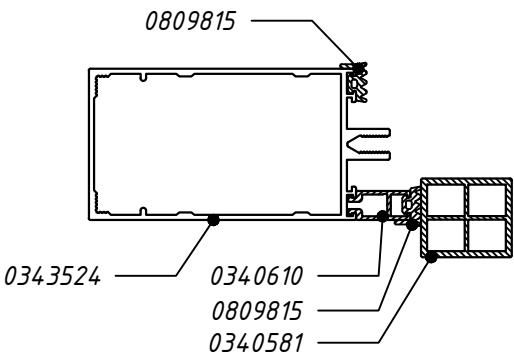


Примечание.
1. Каждый ригель перед производством работ оклеить защитной пленкой, замаркировать номером стойки и укомплектовать уплотнителями и флистурами


Согласовано	ГАП	ГИП
Взам. инв. №		
Подп. и дата		
Инв. № подл.		

						Остров 2 К1		
						" Многофункциональная комплексная жилая застройка , квартал 2, корпус 1, 2, 3, 4, 5, 6 по адресу : г . Москва , внутригородская территория муниципальный округ Хорошёво –Мнёвники."		
Изм.	Кол.уч.	Лист	№ док.	Подп.	Дата	Светопрзрачные конструкции	Стадия	Лист
Разраб.	Бирюкова				06.23		Р	38
Проверил						Ригели	ООО "МАРКА ПОЛА"	
Н.контр.								
Т.контр.								
Утв.								


Профиль рузеля 0343524
Цвем: 79 7M15

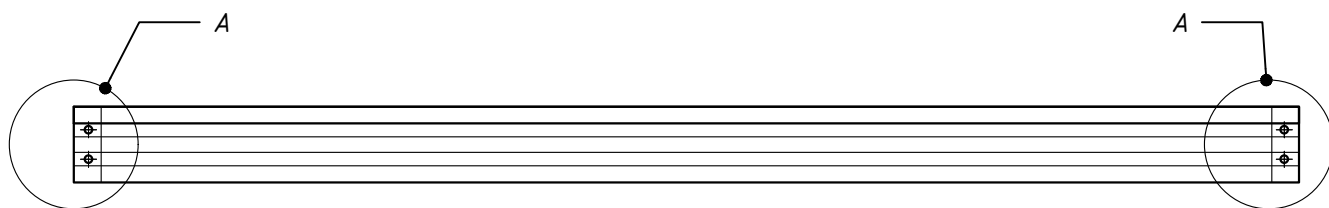

Маркировка	L, мм	Кол-во
K2.B1.R3	794,2	36
K2.B2.R3	774,2	40
K2.B3.R3	763,2	34
K2.B4.R3	774,2	40
K2.B5.R3	794,2	4
K2.B6.R3	763,2	6
K2.B7.R3	794,2	2
K2.B8.R3	774,2	2
K2.B9.R3	763,2	2
K2.B10.R3	774,2	2

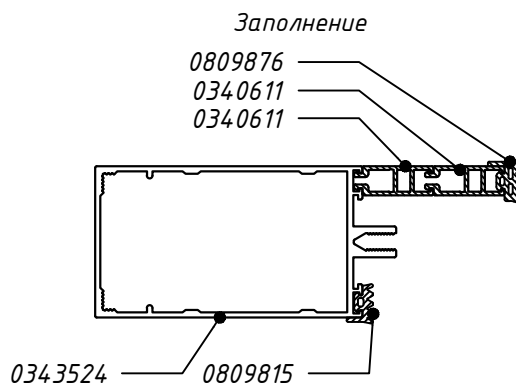

0δρ. A (2:1)

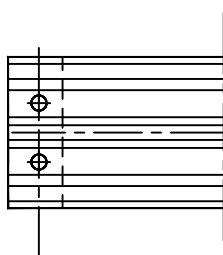

Примечание.

1. Каждый рулель перед производством работ оклеить защитной пленкой, замаркировать номером стойки и комплектовать уплотнителями и флистрами

						Остров 2 К1			
						" Многофункциональная комплексная жилая застройка , квартал 2, корпус 1, 2, 3, 4, 5, 6 по адресу : г . Москва , внутригородская территория муниципальный округ Хорошёво –Мнёвники."			
Изм.	Кол.уч.	Лист	№ док.	Подп.	Дата				
Разраб.		Бирюкова			06.23	Светопрозрачные конструкции	Стадия	Лист	Листов
Проверил							Р	39	
Н.контр.									
						Ризели	ООО "МАРКА ПОЛА"		
Т.контр.									
Утв.									

Копировал

оголасовано

ГЛД



Г И П

Взам. инв. №

Подн. и дата


Инв. N подл.

Профиль ригеля 0343524
Цвет: 79 7M15

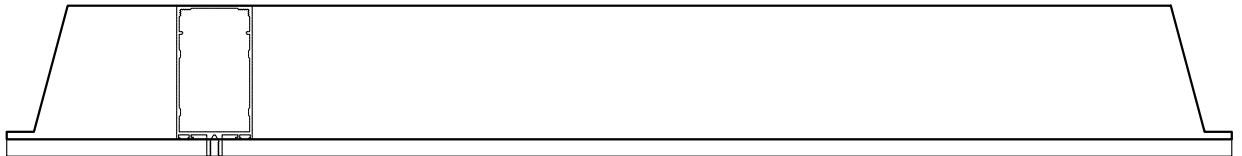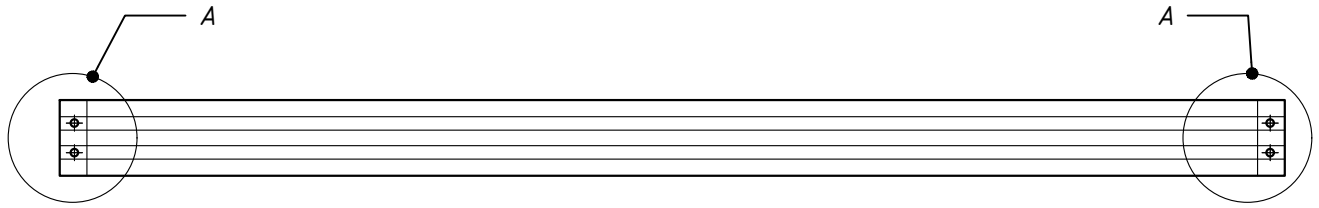


Заполнение

Маркировка	L, мм	Кол-во
K2.B1.R4	794,2	18
K2.B2.R4	774,2	20
K2.B3.R4	763,2	17
K2.B4.R4	774,2	20
K2.B5.R4	794,2	2
K2.B6.R4	763,2	3
K2.B7.R4	794,2	1
K2.B8.R4	774,2	1
K2.B9.R4	763,2	1
K2.B10.R4	774,2	1

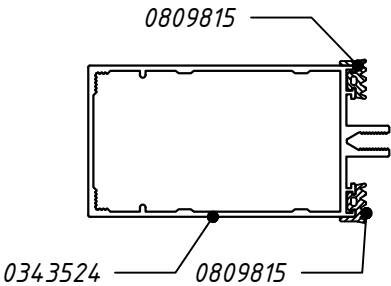

Обр. А (2:1)

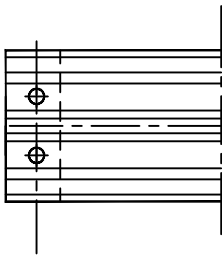

Примечание.
1. Каждый ригель перед производством работ оклеить защитной пленкой,замаркировать номером стойки и укомплектовать уплотнителями и флистурами

Согласовано

ГАП
ГИП


Взам. инв. №

Подп. и дата

Инв. № подл.


Изм.	Кол.уч.	Лист	№ док.	Подп.	Дата	Остров 2 К1			
Разраб.	Бирюкова				06.23	" Многофункциональная комплексная жилая застройка , квартал 2, корпус 1, 2, 3, 4, 5, 6 по адресу : г . Москва , внутригородская территория муниципальный округ Хорошёво –Мнёвники."			
Проверил						Светопрозрачные конструкции	Стадия	Лист	Листов
Н.контр.							Р	40	
Т.контр.						Ригели	ООО "МАРКА ПОЛА"		
Утв.									

Профиль ригеля 0343525
Цвет: 79 7M15

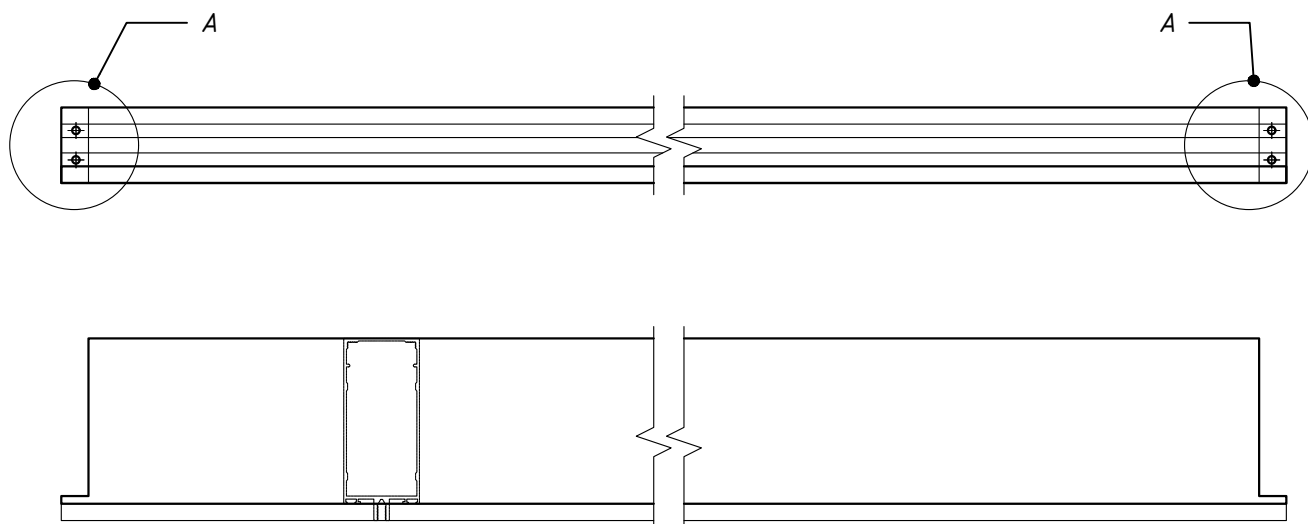


Заполнение

Маркировка	L, мм	Кол-во
K2.B1.R5	1640,0	36
K2.B2.R5	1680,0	40
K2.B3.R5	1800,0	34
K2.B4.R5	1780,0	40
K2.B5.R5	1640,0	4
K2.B6.R5	1800,0	6
K2.B7.R5	1640,0	2
K2.B8.R5	1680,0	2
K2.B9.R5	1800,0	2
K2.B10.R5	1780,0	2

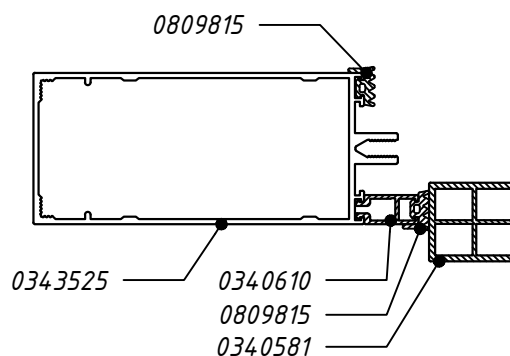

Обр. А (2:1)

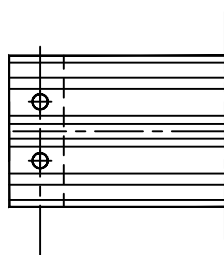


Примечание.

1. Каждый ригель перед производством работ оклеить защитной пленкой, замаркировать номером стойки и укомплектовать уплотнителями и филлистрами


Согласовано	ГАП	Взам. инв. №	Подп. и дата	Изм.	Кол.уч.	Лист	№ док.	Подп.	Дата	Остров 2 К1			
	ГИП									" Многофункциональная комплексная жилая застройка , квартал 2, корпус 1, 2, 3, 4, 5, 6 по адресу : г . Москва , внутригородская территория муниципальный округ Хорошёво –Мнёвники."			
Инв. № подл.	Разраб.	Бирюкова		06.23	Светопрозрачные конструкции					Стадия	Лист	Листов	
	Проверил									Р	41		
	Н.контр.					Ригели					ООО "МАРКА ПОЛА"		
	Т.контр.												
	Утв.												

Профиль ригеля 0343525
Цвет: 79 7M15

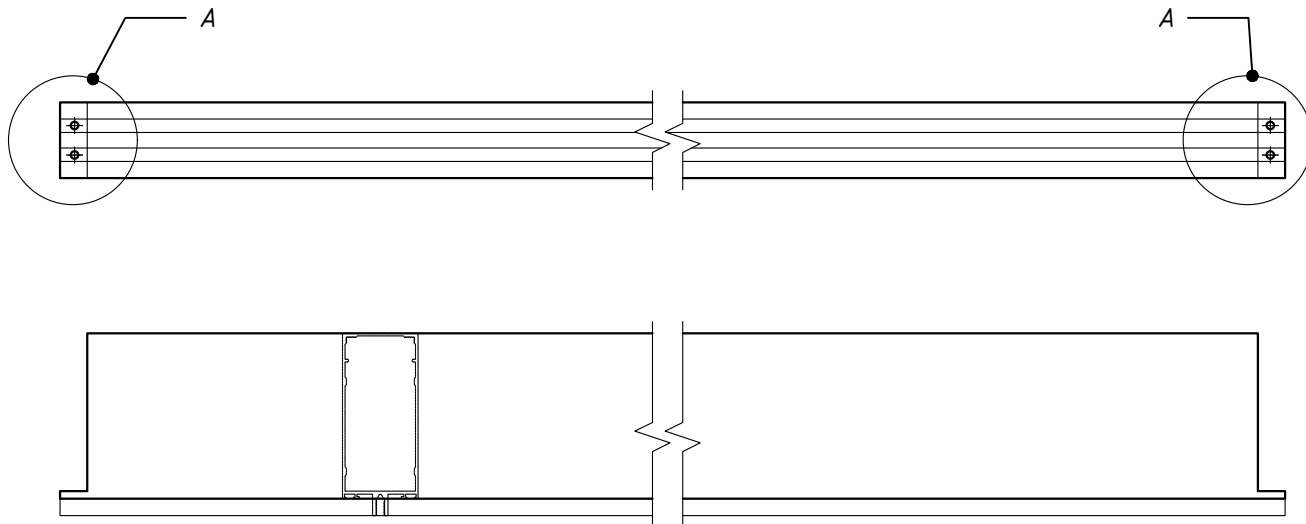


Заполнение

Маркировка		L, мм	Кол-во
K2.B1.R6		1640,0	18
K2.B2.R6		1680,0	20
K2.B3.R6		1800,0	17
K2.B4.R6		1780,0	20
K2.B5.R6		1640,0	2
K2.B6.R6		1800,0	3
K2.B7.R6		1640,0	1
K2.B8.R6		1680,0	1
K2.B9.R6		1800,0	1
K2.B10.R6		1780,0	1

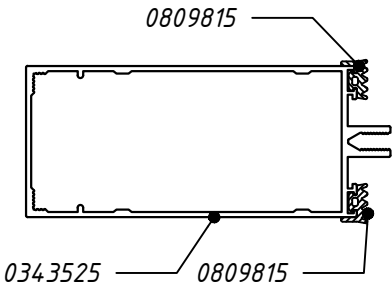



Обр. А (2:1)

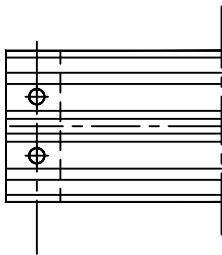

Примечание.
1. Каждый ригель перед производством работ оклеить защитной пленкой, замаркировать номером стойки и укомплектовать уплотнителями и филистрами

Согласовано	ГАП	ГИП								
	Взам. инв. N									
Подп. и дата	Изм.	Кол.уч.	Лист	№ док.	Подп.	Дата	Остров 2 К1			
	Разраб.	Бирюкова				06.23	" Многофункциональная комплексная жилая застройка , квартал 2, корпус 1, 2, 3, 4, 5, 6 по адресу : г . Москва , внутригородская территория муниципальный округ Хорошёво -Мнёвники."			
Инв. N подл.	Проверил						Светопрозрачные конструкции	Стадия	Лист	Листов
	Н.контр.							Р	42	
	Т.контр.						Ригели	ООО "МАРКА ПОЛА"		
	Утв.									


Прижимная планка стойки
Цвет: без покраски

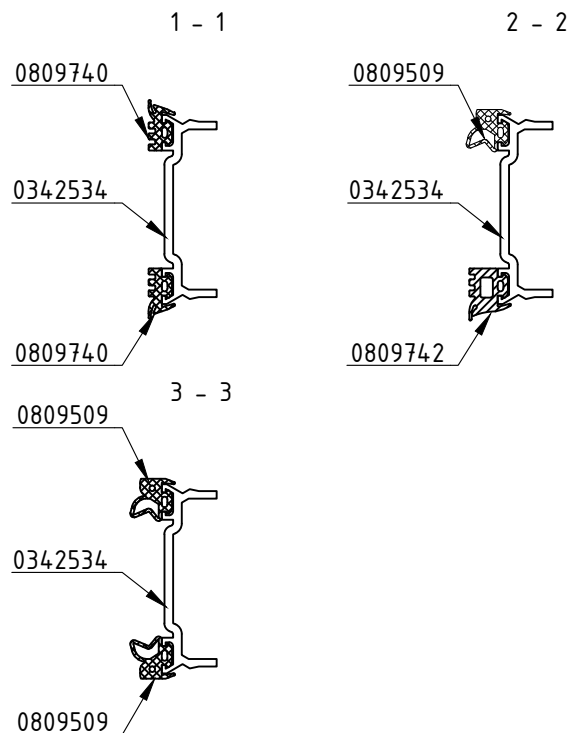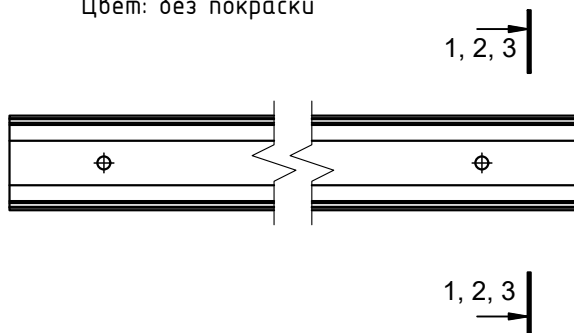

Маркировка	№ Сечения	L, мм	Кол-во
K2.B1.PS1	2 - 2	2615,0	36
K2.B1.PS2	3 - 3	2615,0	36
K2.B1.PS3	1 - 1	2615,0	18
K2.B2.PS1	2 - 2	2615,0	40
K2.B2.PS2	3 - 3	2615,0	40
K2.B2.PS3	1 - 1	2615,0	20
K2.B3.PS1	2 - 2	2615,0	34
K2.B3.PS2	3 - 3	2615,0	34
K2.B3.PS3	1 - 1	2615,0	17
K2.B4.PS1	2 - 2	2615,0	40
K2.B4.PS2	3 - 3	2615,0	40
K2.B4.PS3	1 - 1	2615,0	20
K2.B5.PS1	2 - 2	1960,0	4
K2.B5.PS2	3 - 3	1960,0	4
K2.B5.PS3	1 - 1	1960,0	2
K2.B6.PS1	2 - 2	1960,0	6
K2.B6.PS2	3 - 3	1960,0	6
K2.B6.PS3	1 - 1	1960,0	3
K2.B7.PS1	2 - 2	2815,0	2
K2.B7.PS2	3 - 3	2815,0	2
K2.B7.PS3	1 - 1	2815,0	1

Маркировка	№ Сечения	L, мм	Кол-во
K2.B8.PS1	2 - 2	2815,0	2
K2.B8.PS2	3 - 3	2815,0	2
K2.B8.PS3	1 - 1	2815,0	1
K2.B9.PS1	2 - 2	2815,0	2
K2.B9.PS2	3 - 3	2815,0	2
K2.B9.PS3	1 - 1	2815,0	1
K2.B10.PS1	2 - 2	2815,0	2
K2.B10.PS2	3 - 3	2815,0	2
K2.B10.PS3	1 - 1	2815,0	1

Крышка стойки
Цвет: 79 9M05

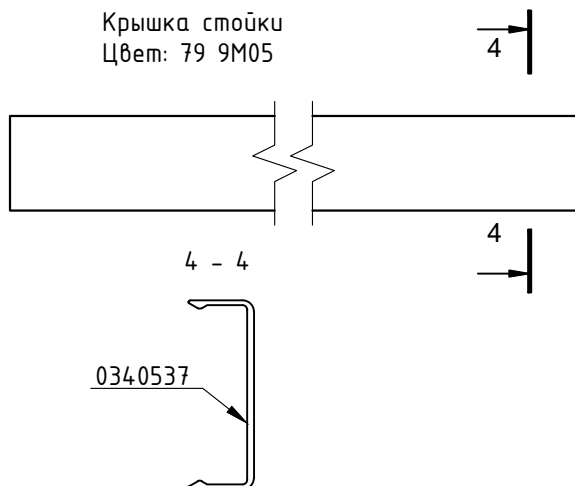


Маркировка	L, мм	Кол-во
K2.B1.KS1	2615,0	90
K2.B2.KS1	2615,0	100
K2.B3.KS1	2615,0	85
K2.B4.KS1	2615,0	100
K2.B5.KS1	1960,0	10
K2.B6.KS1	1960,0	15
K2.B7.KS1	2815,0	5
K2.B8.KS1	2815,0	5
K2.B9.KS1	2815,0	5
K2.B10.KS1	2815,0	5


Согласовано	ГАП	ГИП
	Взам. инв. Н	Подп. и дата
Инв. Н подл.	Изм.	Кол.уч.
	Разраб.	Бирюкова
	Проверил	
	Н.контр.	
	Т.контр.	
	Утв.	

						Остров 2 К1			
						" Многофункциональная комплексная жилая застройка , квартал 2, корпус 1, 2, 3, 4, 5, 6 по адресу : г . Москва , внутригородская территория муниципальный округ Хорошёво –Мнёвники."			
Изм.	Кол.уч.	Лист	№ док.	Подп.	Дата	Светопрозрачные конструкции	Стадия	Лист	Листов
Разраб.		Бирюкова			06.23		Р	43	
Проверил									
Н.контр.									
						Прижим и крышка стойки	ООО "МАРКА ПОЛА"		
Т.контр.									
Утв.									

Прижимная планка ригеля
Цвет: без покраски

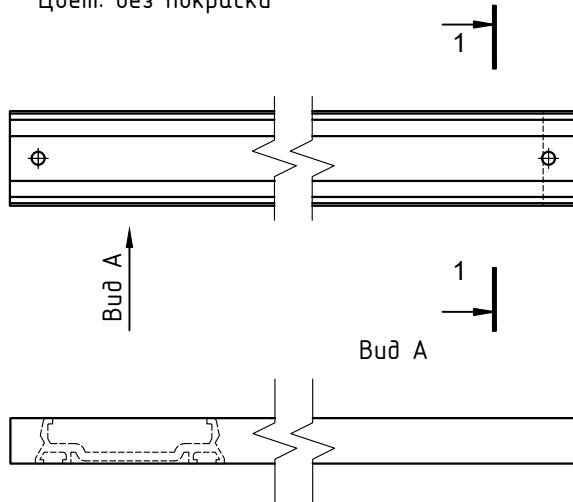


Крышка ригеля
Цвет: 79 9M05

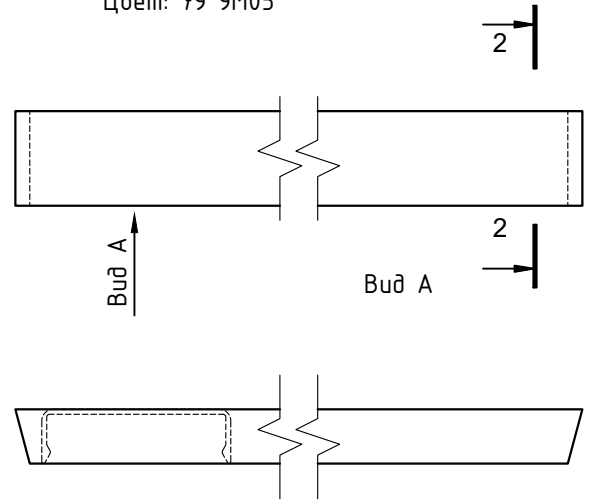

Маркировка		L, мм	Кол-во
K2.B1.PR1		794,0	162
K2.B1.PR2		1606,0	54
K2.B2.PR1		774,0	180
K2.B2.PR2		1646,0	60
K2.B3.PR1		763,0	153
K2.B3.PR2		1766,0	51
K2.B4.PR1		774,0	180
K2.B4.PR2		1746,0	60
K2.B5.PR1		794,0	18
K2.B5.PR2		1606,0	6
K2.B6.PR1		763,0	27
K2.B6.PR2		1766,0	9
K2.B7.PR1		794,0	9
K2.B7.PR2		1606,0	3
K2.B8.PR1		774,0	9
K2.B8.PR2		1646,0	3
K2.B9.PR1		763,0	9
K2.B9.PR2		1766,0	3
K2.B10.PR1		774,0	9
K2.B10.PR2		1746,0	3

Маркировка		L, мм	Кол-во
K2.B1.KR1		804,6	162
K2.B1.KR2	ПРЯМАЯ	1608,0	54
K2.B2.KR1		784,6	180
K2.B2.KR2	ПРЯМАЯ	1648,0	60
K2.B3.KR1		773,6	153
K2.B3.KR2	ПРЯМАЯ	1768,0	51
K2.B4.KR1		784,6	180
K2.B4.KR2	ПРЯМАЯ	1748,0	60
K2.B5.KR1		804,6	18
K2.B5.KR2	ПРЯМАЯ	1608,0	6
K2.B6.KR1		773,6	27
K2.B6.KR2	ПРЯМАЯ	1768,0	9
K2.B7.KR1		804,6	9
K2.B7.KR2	ПРЯМАЯ	1608,0	3
K2.B8.KR1		784,6	9
K2.B8.KR2	ПРЯМАЯ	1648,0	3
K2.B9.KR1		773,6	9
K2.B9.KR2	ПРЯМАЯ	1768,0	3
K2.B10.KR1		784,6	9
K2.B10.KR2	ПРЯМАЯ	1748,0	3

1 - 1 2 - 2

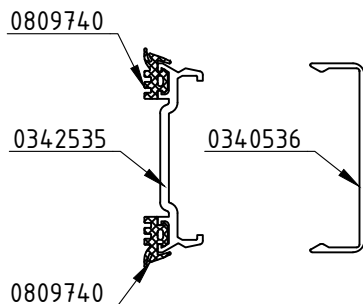

! ---.---.KR2 прямые, без углов запила


Согласовано	ГАП	Взам. инв. №	Подп. и дата	Инв. № подл.
	ГИП			

						Остров 2 К1			
						" Многофункциональная комплексная жилая застройка , квартал 2, корпус 1, 2, 3, 4, 5, 6 по адресу : г . Москва , внутригородская территория муниципальный округ Хорошёво –Мнёвники."			
Изм.	Кол.уч.	Лист	№ док.	Подп.	Дата	Светопрозрачные конструкции	Стадия	Лист	Листов
Разраб.		Бирюкова			06.23		Р	44	
Проверил									
Н.контр.									
						Прижим и крышка ригеля	ООО "МАРКА ПОЛА"		
Т.контр.									
Утв.									

Угловой витраж В-1.2 (развертка)

Кол-во: 17 шт.

S=9,26 м.кв.

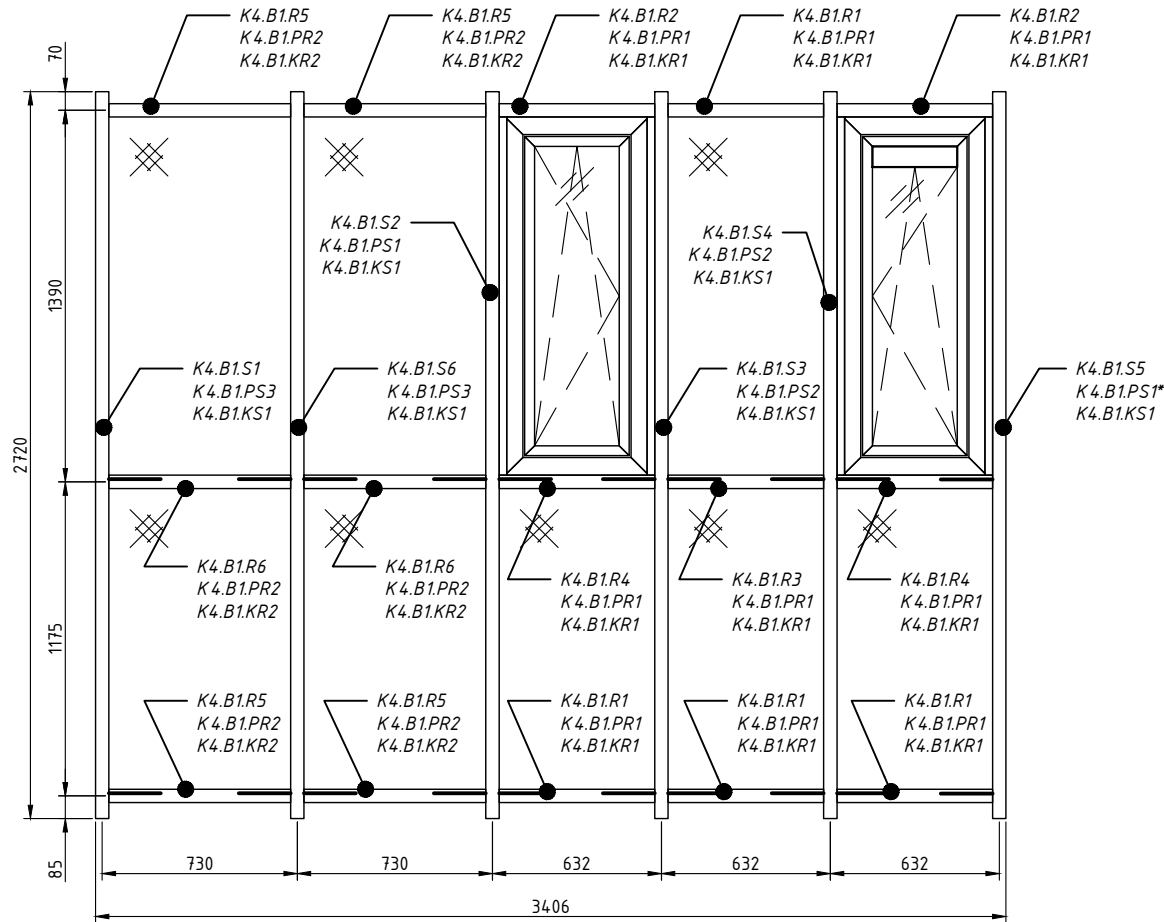


Заполнение термовставки - 0809892 + 0809893.
Под прижимы бутиловая лента - 0849711.


Прижимной саморез:

- прижимы PS1, PS2, PS1* - Ø6,3x67мм - 0535476
- прижимы PS3, PR1, PR2 - Ø6,3x64мм - 0535475

Ригеля крепить саморезом Ø4,2x12,7мм - 0525317

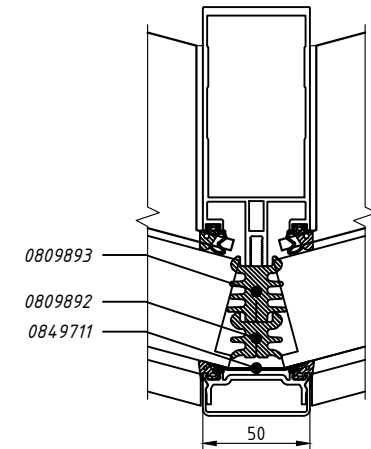

Заполнение под встраиваемые окна (компенсаторы и уплотнители) устанавливаются подрядной организацией, после монтажа витражей.

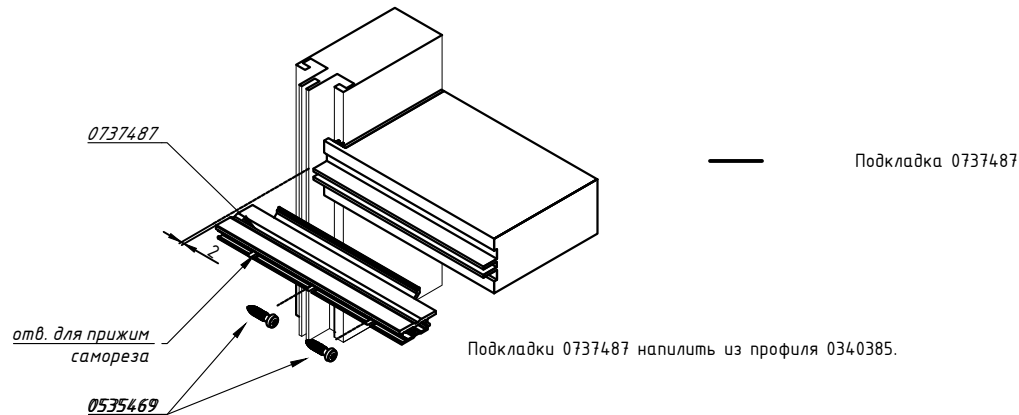

Подкладка 0737487

Подкладки 0737487 напилить из профиля 0340385.

						Остров 2 К1			
						" Многофункциональная комплексная жилая застройка , квартал 2, корпус 1, 2, 3, 4, 5, 6 по адресу : г . Москва , внутригородская территория муниципального округа Хорошёво –Мнёвники."			
Изм.	Кол.уч.	Лист	№ док.	Подп.	Дата	Светопрозрачные конструкции	Стадия	Лист	Листов
Разраб.	Бирякова				06.23		Р	45	
Проверил									
Н.контр.									
Т.контр.						Угловой витраж В-1.2		ООО "МАРКА ПОЛА"	
Утв.									


Копировал

Согласовано					
ГАП					
ГИП					
Взам. инв. Н					
Подп. и дата					
Инв. Н подл.					


Угловой витраж В-8.2 (развертка)

Кол-во: 17 шт.


S=9,45 м.кв.

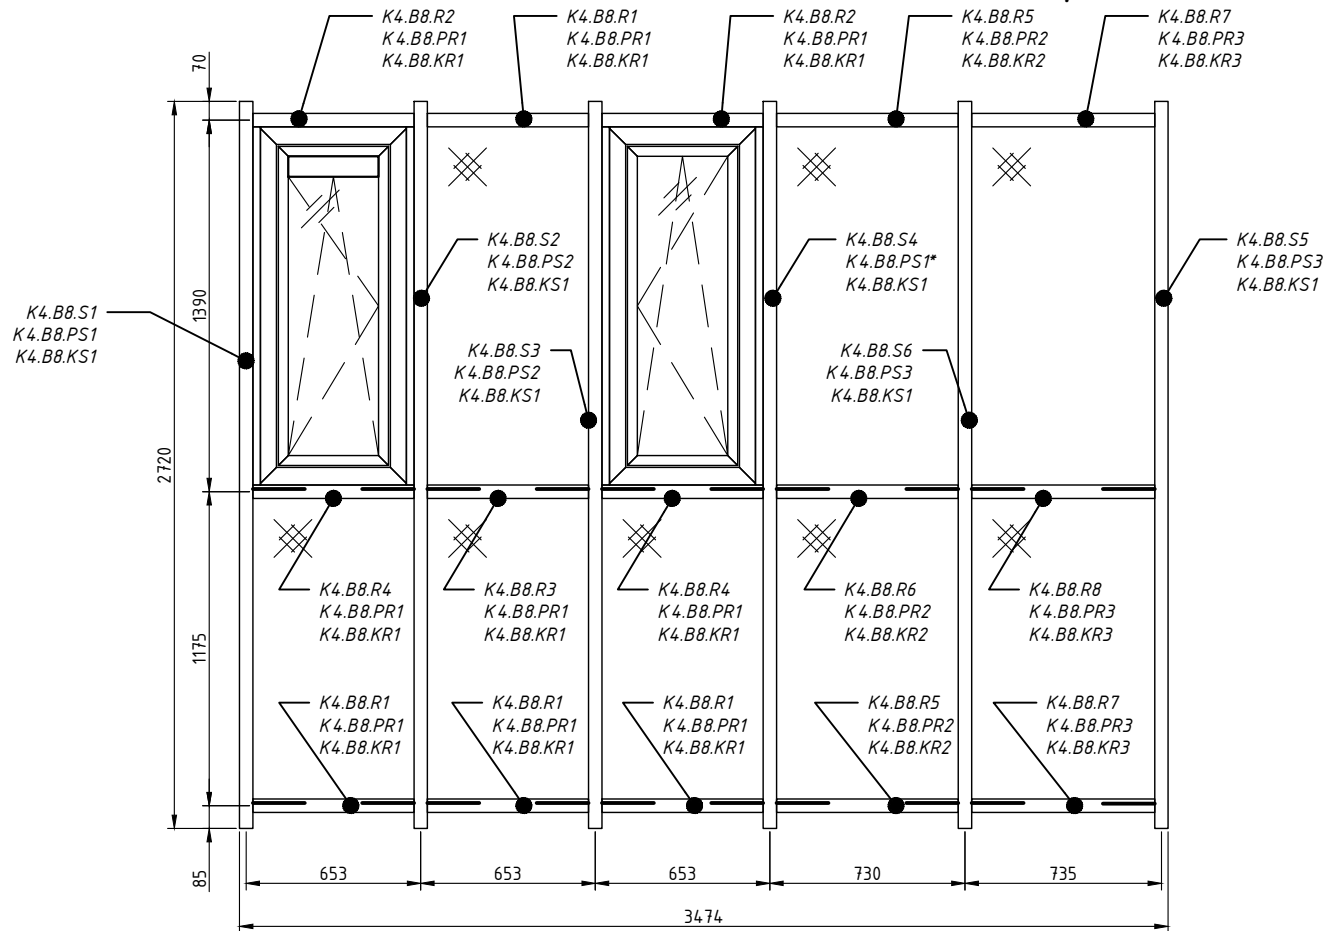

Заполнение термовставки - 0809892 + 0809893.
Под прижимы бутиловая лента - 0849711.
Прижимной саморез:
- прижимы PS1, PS2, PS1* - Ø6,3x67мм - 0535476
- прижимы PS3, PR1, PR2 - Ø6,3x64мм - 0535475
Ригеля крепить саморезом Ø4,2x12,7мм - 0525317

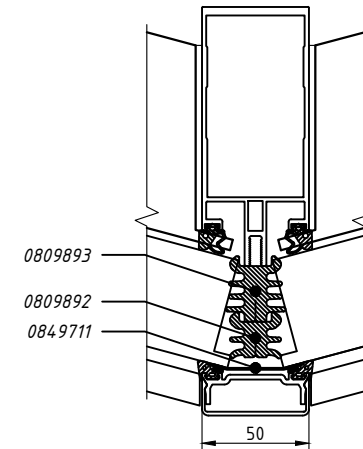

Заполнение под встраиваемые окна (компенсаторы и уплотнители) устанавливаются подрядной организацией, после монтажа витражей.

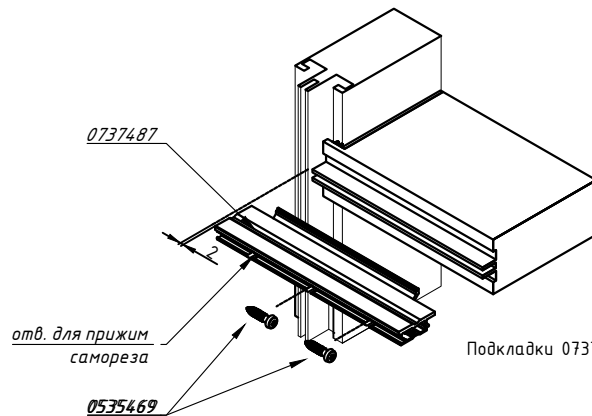

Подкладки 0737487 напилить из профиля 0340385.

Подкладка 0737487

						Остров 2 К1			
						" Многофункциональная комплексная жилая застройка , квартал 2, корпус 1, 2, 3, 4, 5, 6 по адресу : г . Москва , внутригородская территория муниципальный округ Хорошёво -Мнёвники."			
Изм.	Кол.уч.	Лист	№ док.	Подп.	Дата	Светопрозрачные конструкции	Стадия	Лист	Листов
Разраб.	Бирюкова				06.23		Р	46	
Проверил									
Н.контр.									
Т.контр.						Угловой витраж В-8.2		ООО "МАРКА ПОЛА"	
Утв.									


Копировал

Согласовано					
ГАП					
ГИП					
Инв. N подл.	Подп. и дата	Взам. инв. N			


Угловой витраж В-22 (развертка).

Кол-во: 15 шт.


S=8,81м.кв.

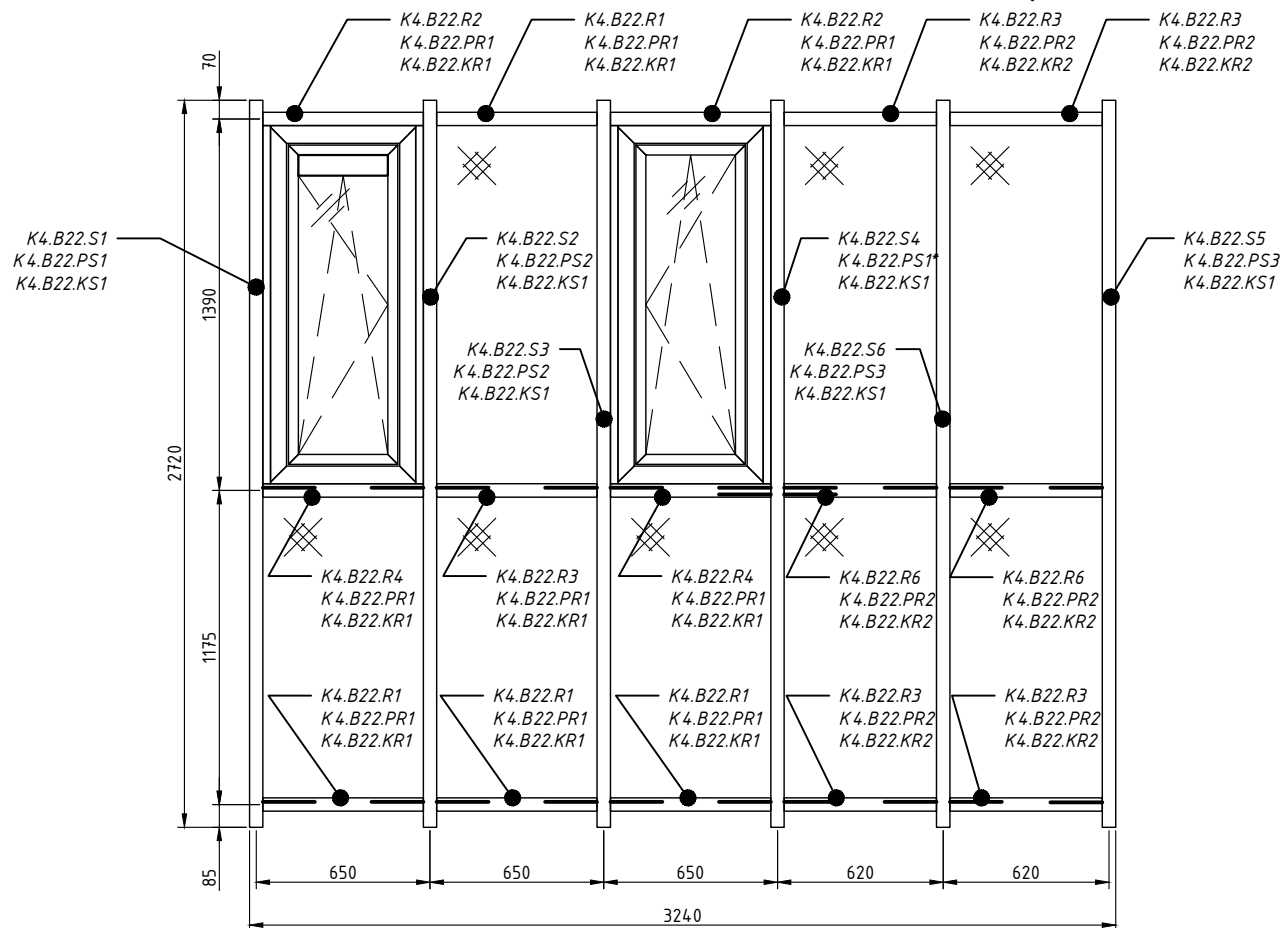

Заполнение термовставки - 0809892 + 0809893.
Под прижимы бутиловая лента - 0849711.
Прижимной саморез:
- прижимы PS1, PS2, PS1* - Ø6,3x67мм - 0535476
- прижимы PS3, PR1, PR2 - Ø6,3x64мм - 0535475
Резеля крепить саморезом Ø4,2x12,7мм - 0525317

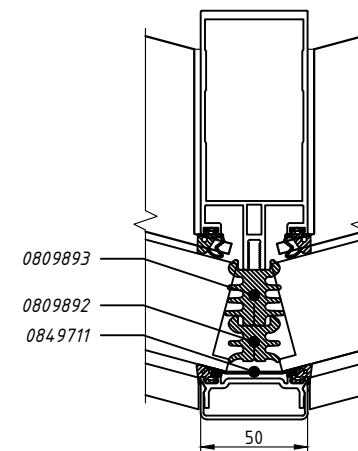

Заполнение под встраиваемые окна (компенсаторы и уплотнители) устанавливаются подрядной организацией, после монтажа витражей.

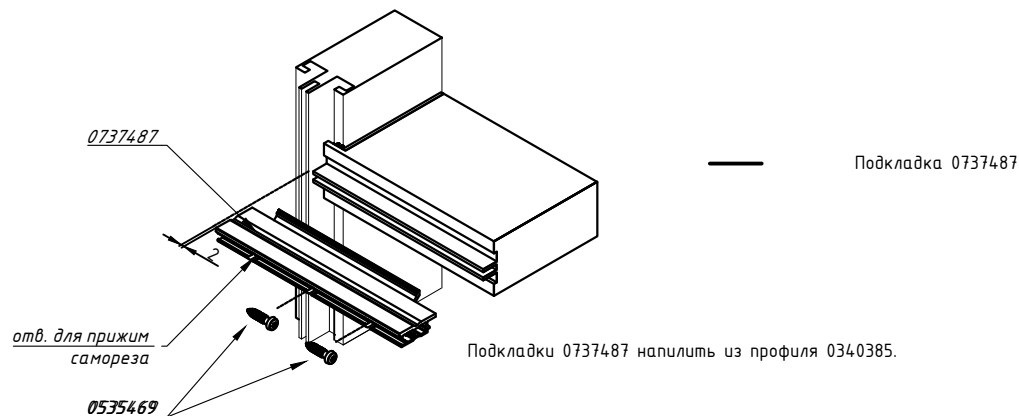

						Остров 2 К1			
						" Многофункциональная комплексная жилая застройка , квартал 2, корпус 1, 2, 3, 4, 5, 6 по адресу : г . Москва , внутригородская территория муниципальный округ Хорошёво -Мнёвники."			
Изм.	Кол.уч.	Лист	№ док.	Подп.	Дата	Светопрозрачные конструкции	Стадия	Лист	Листов
Разраб.	Бирюкова				06.23		Р	47	
Проверил									
Н.контр.									
Т.контр.						Угловой витраж В-22	ООО "МАРКА ПОЛА"		
Утв.									


Копировал

Согласовано	ГАП	ГИП	Взам. инв. №	Подп. и дата	Инв. № подл.

Угловой витраж В-39 (развертка).


Кол-во: 9 шт.

S=8,94 м.кв.

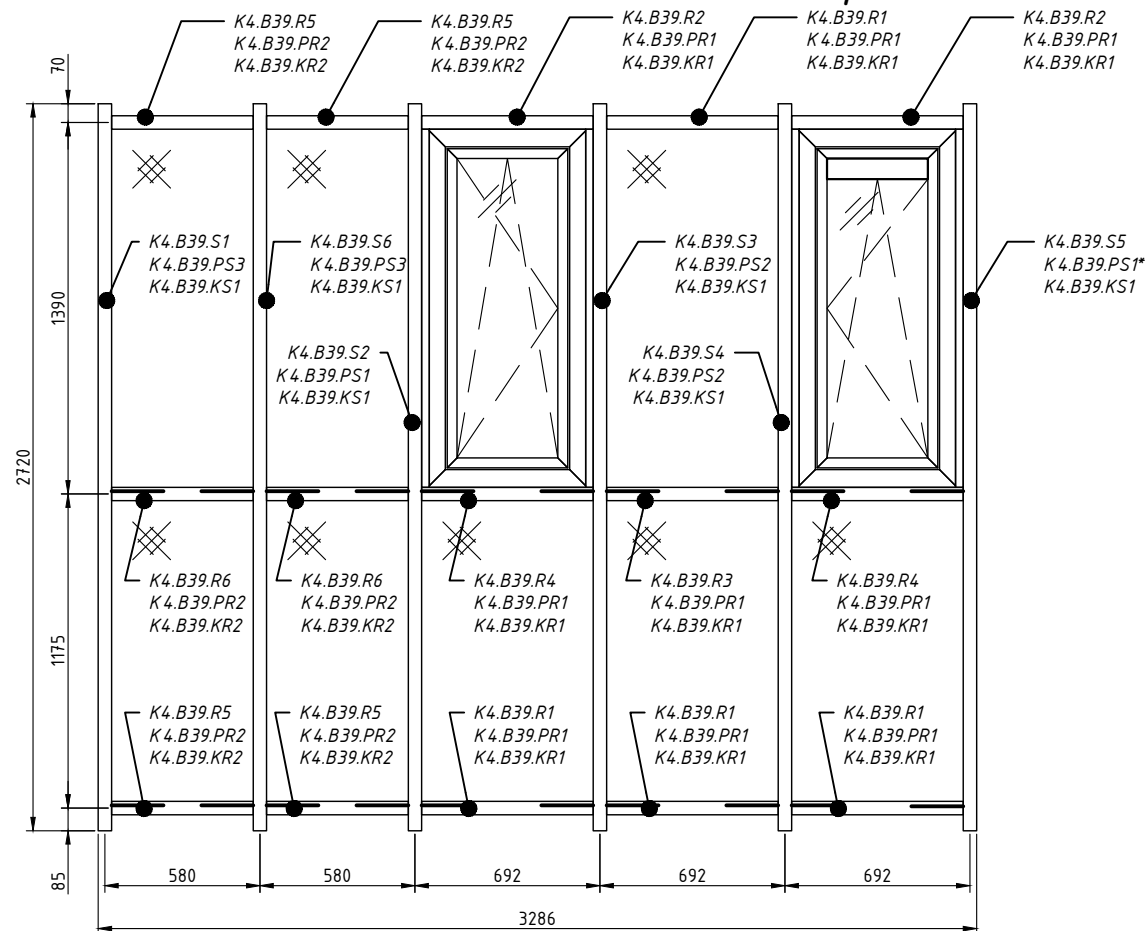


Заполнение термовставки - 0809892 + 0809893.
Под прижимы бутиловая лента - 0849711.
Прижимной саморез:
- прижимы PS1, PS2, PS1* - Ø6,3x67мм - 0535476
- прижимы PS3, PR1, PR2 - Ø6,3x64мм - 0535475

Ригель крепить саморезом Ø4,2x12,7мм - 0525317

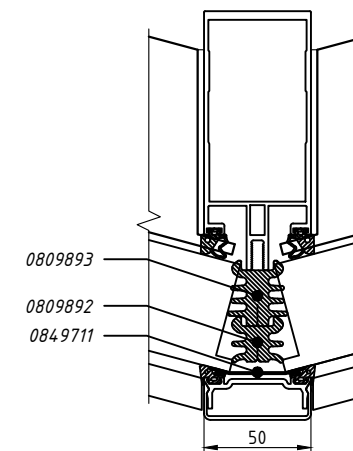

Заполнение под встраиваемые окна (компенсаторы и уплотнители) устанавливаются подрядной организацией, после монтажа витражей.

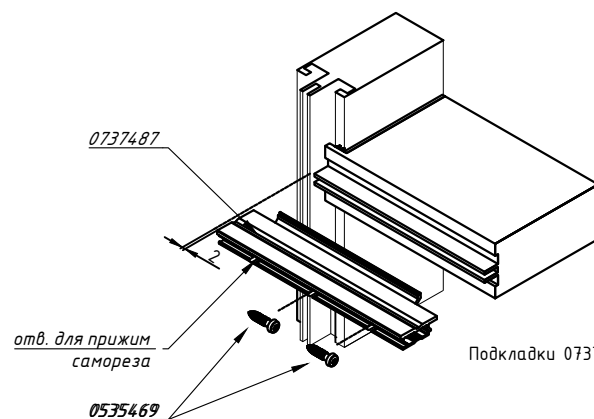

Подкладки 0737487 напилить из профиля 0340385.

Подкладка 0737487

						Остров 2 К1			
						" Многофункциональная комплексная жилая застройка , квартал 2, корпус 1, 2, 3, 4, 5, 6 по адресу : г . Москва , внутригородская территория муниципальный округ Хорошёво -Мнёвники."			
Изм.	Кол.уч.	Лист	№ док.	Подп.	Дата	Светопрозрачные конструкции	Стадия	Лист	Листов
Разраб.	Бирюкова				06.23		Р	48	
Проверил									
Н.контр.						Угловой витраж В-39	ООО "МАРКА ПОЛА"		
Т.контр.									
Утв.									


Копировал

Согласовано	ГАП	ГИП
Инв. № подл.	Подп. и дата	Взам. инв. №


Угловой витраж В-27 (развертка).

Кол-во: 1 шт.


S=10,19 м.кв.

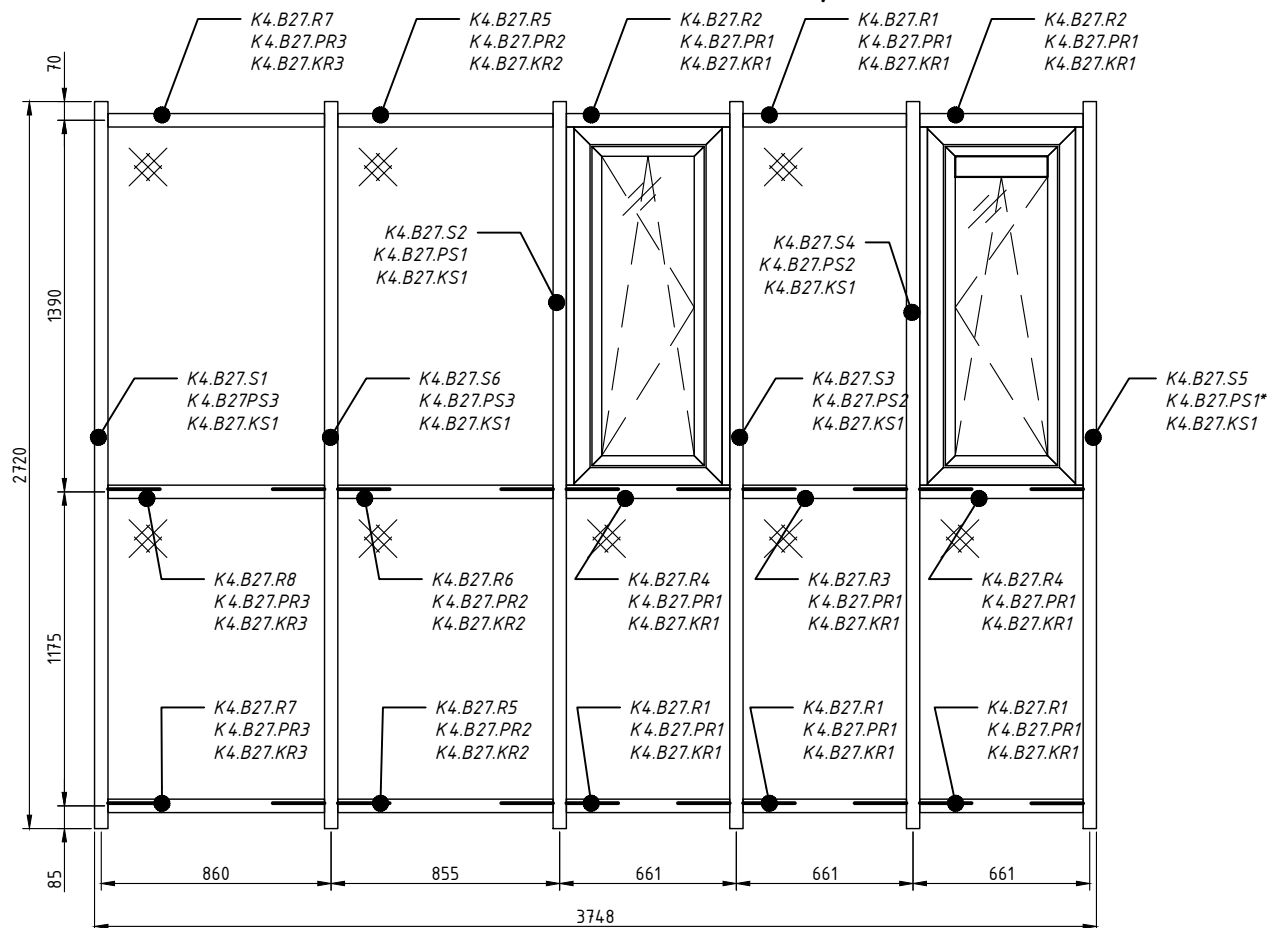

Заполнение термовставки - 0809892 + 0809893.
Под прижимы бутиловая лента - 0849711.
Прижимной саморез:
- прижимы PS1, PS2, PS1* - Ø6,3x67мм - 0535476
- прижимы PS3, PR1, PR2 - Ø6,3x64мм - 0535475
Ригель крепить саморезом Ø4,2x12,7мм - 0525317

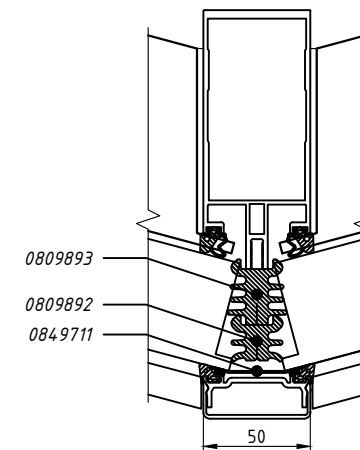

Заполнение под встраиваемые окна (компенсаторы и уплотнители) устанавливаются подрядной организацией, после монтажа витражей.

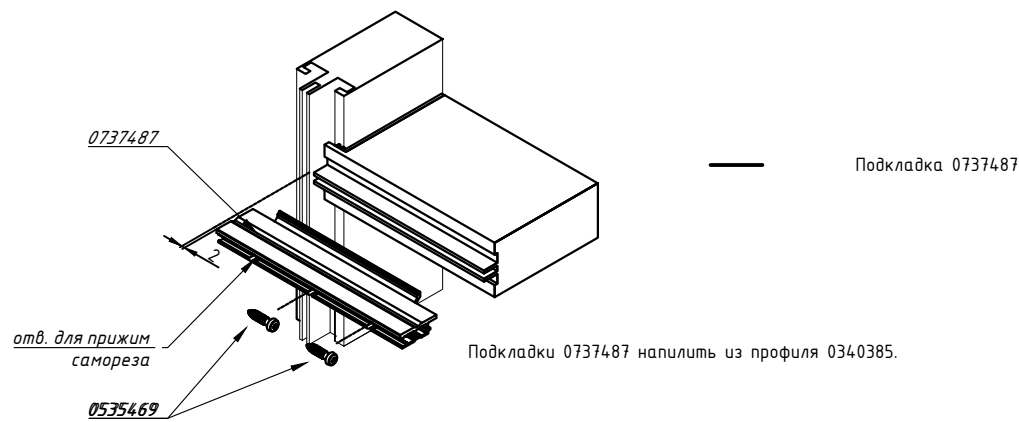

						Остров 2 К1			
						" Многофункциональная комплексная жилая застройка , квартал 2, корпус 1, 2, 3, 4, 5, 6 по адресу : г . Москва , внутригородская территория муниципальный округ Хорошёво -Мнёвники."			
Изм.	Кол.уч.	Лист	№ док.	Подп.	Дата	Светопрозрачные конструкции	Стадия	Лист	Листов
Разраб.	Бирюкова				06.23		Р	49	
Проверил									
Н.контр.						Угловой витраж В-27		ООО "МАРКА ПОЛА"	
Т.контр.									
Утв.									


Копировал

Согласовано	ГАП	ГИП
Инв. и дата	Взам. инв. и дата	Подп. и дата
Инв. и подл.		


Угловой витраж В-29 (развертка).

Кол-во: 1 шт.


S=10,19 м.кв.

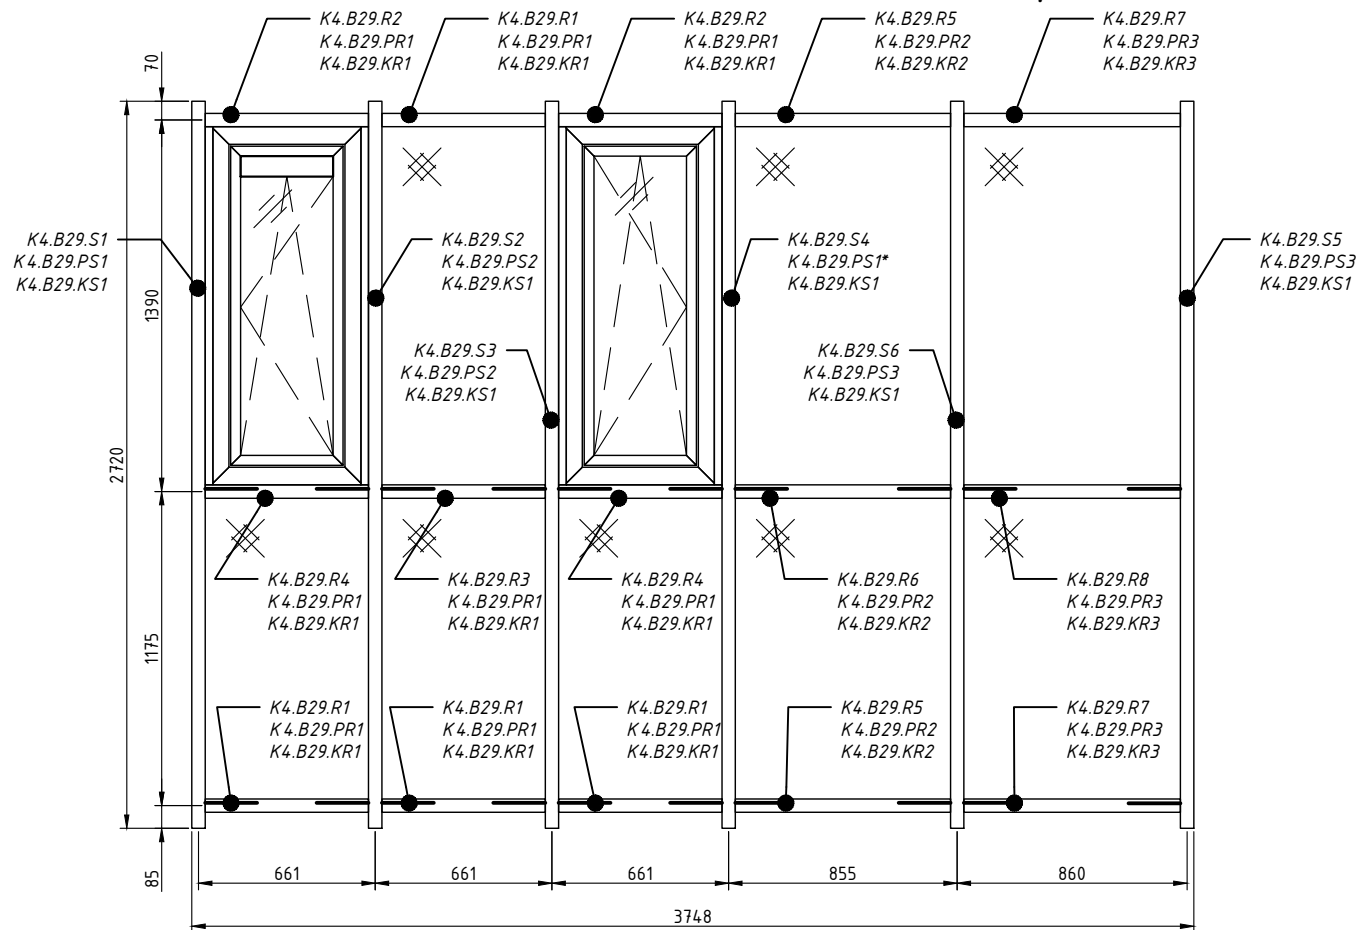

Заполнение термовставки - 0809892 + 0809893.
Под прижимы бутиловая лента - 0849711.
Прижимной саморез:
- прижимы PS1, PS2, PS1* - Ø6,3x67мм - 0535476
- прижимы PS3, PR1, PR2 - Ø6,3x64мм - 0535475
Резеля крепить саморезом Ø4,2x12,7мм - 0525317

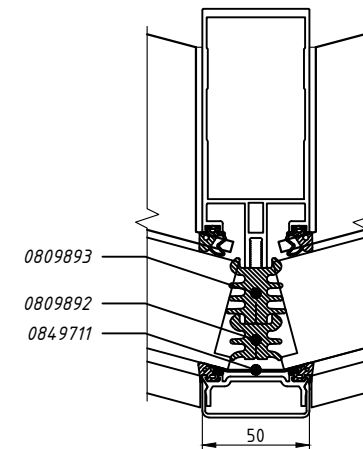

Заполнение под встраиваемые окна (компенсаторы и уплотнители) устанавливаются подрядной организацией, после монтажа витражей.

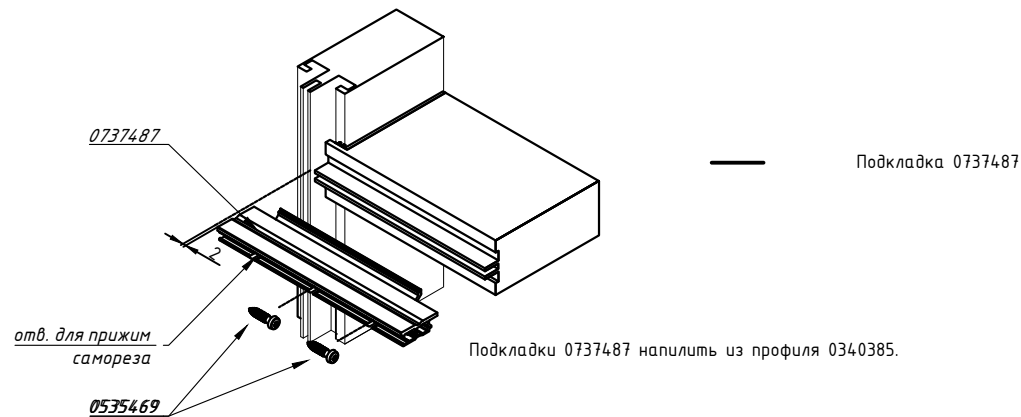


						Остров 2 К1			
						" Многофункциональная комплексная жилая застройка , квартал 2, корпус 1, 2, 3, 4, 5, 6 по адресу : г . Москва , внутригородская территория муниципальный округ Хорошёво –Мнёвники."			
Изм.	Кол.уч.	Лист	№ док.	Подп.	Дата	Светопрозрачные конструкции	Стадия	Лист	Листов
Разраб.	Бирюкова				06.23		Р	50	
Проверил									
Н. контр.									
Т. контр.						Угловой витраж В-29		ООО "МАРКА ПОЛА"	
Утв.									

Копировал

Инв. № подл.	Подп. и дата	Взам. инв. №	Согласовано	
			ГАП	
			ГИП	


Маркировка:
 К4.В1.С1 – 17 шт.
 К4.В8.С5 – 17 шт. (зеркально)
 К4.В22.С5 – 15 шт. (зеркально)
 К4.В39.С1 – 9 шт.
 К4.В27.С1 – 9 шт.
 К4.В29.С5 – 1 шт. (зеркально)

Цвет: 79 7М15

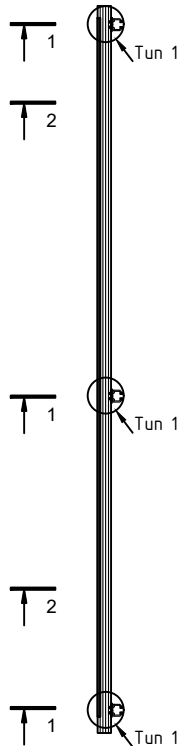


Маркировка:
 К4.В1.С6 – 17 шт.
 К4.В8.С6 – 17 шт.
 К4.В22.С6 – 15 шт.
 К4.В39.С6 – 9 шт.
 К4.В27.С6 – 9 шт.
 К4.В29.С6 – 1 шт.

Цвет: 79 7М15

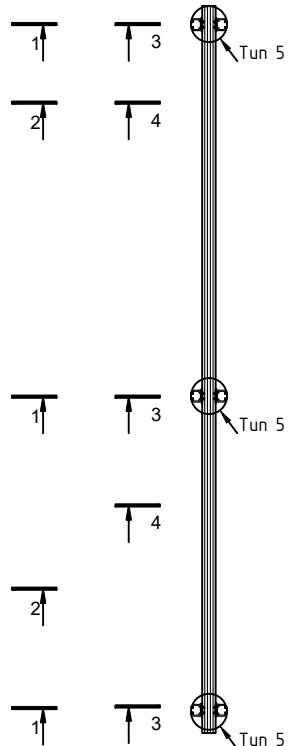

Маркировка:
 К4.В1.С2 – 17 шт.
 К4.В8.С4 – 17 шт. (зеркально)
 К4.В22.С4 – 15 шт. (зеркально)
 К4.В39.С2 – 9 шт.
 К4.В27.С2 – 9 шт.
 К4.В29.С4 – 1 шт. (зеркально)


Цвет: 79 7М15

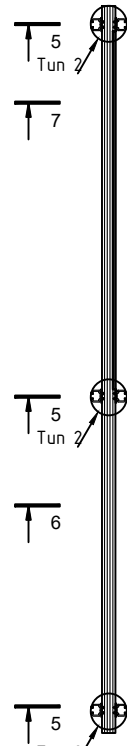

Тип крепления ригельного сухаря см. лист 3.

Примечание.

- Каждую стойку перед производством работ оклеить защитной пленкой, замаркировать номером стойки и укомплектовать уплотнителями и флистрами
- Стойки укомплектовать подпятниками из 034.5593 L=200 мм
- Манжету 080.9885 и сухарь РС-2 установить на производстве по шаблону. Манжету подрезать по торцу ригеля.
- Ригельные сухари РС-1 и РС-2 устанавливать на саморез Ø4,8x13 – 0525330.

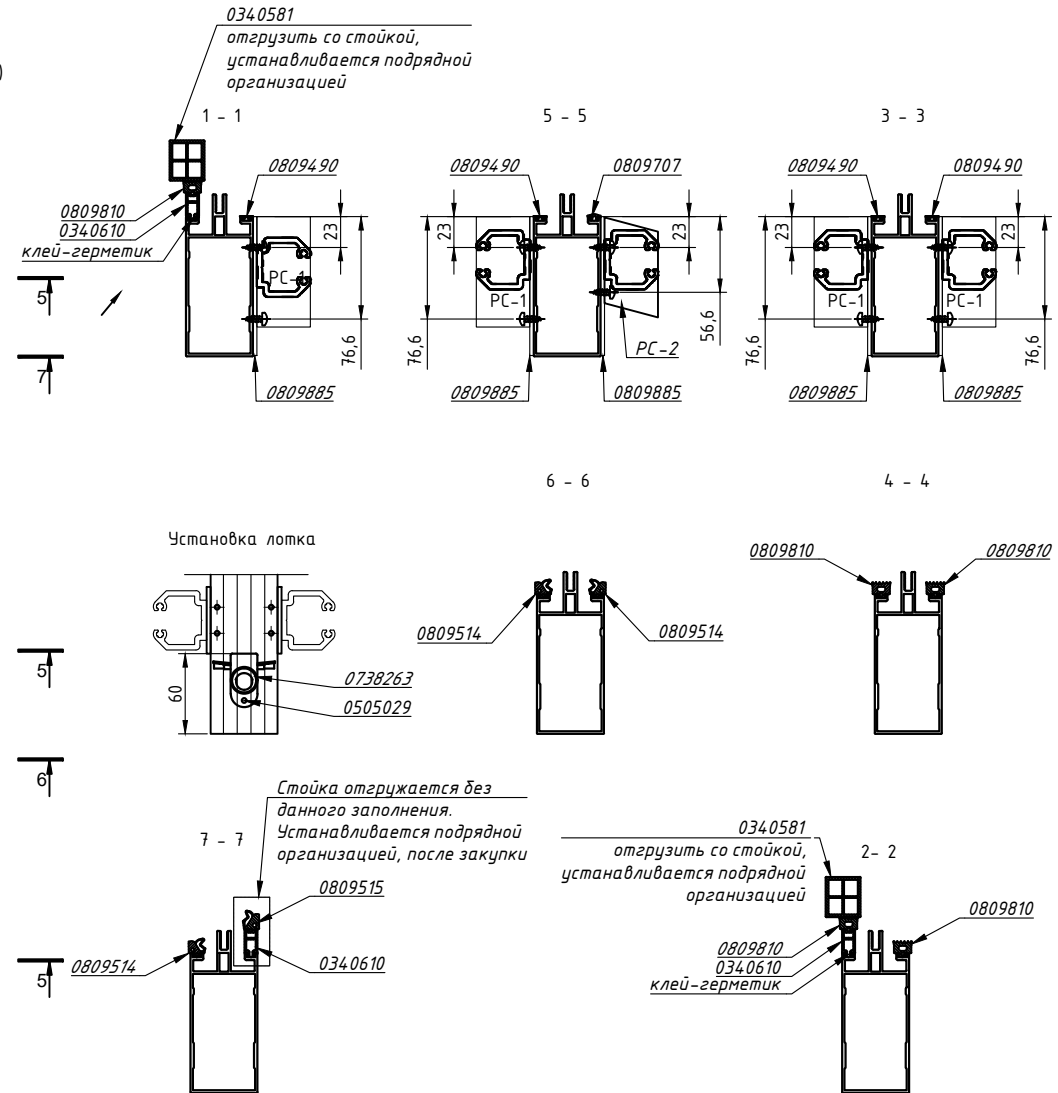

						Остров 2 К1			
						" Многофункциональная комплексная жилая застройка , квартал 2, корпус 1, 2, 3, 4, 5, 6 по адресу : г . Москва , внутригородская территория муниципальный округ Хорошёво – Мнёвники."			
Изм.	Кол.уч.	Лист	№ док.	Подп.	Дата	Светопрозрачные конструкции	Стадия	Лист	Листов
Разраб.	Бирюкова				06.23		Р	51	
Проверил									
Н.контр.						Стойки В1, В8, В22, В39, В27, В29	ООО "МАРКА ПОЛА"		
Т.контр.									
Утв.									



Копировал

Согласовано	ГАП	ГИП
Инв. N подл.	Взам. инв. N	Подп. и дата

Инв. N подл.	Подп. и дата	Взам. инв. N	Согласовано
		ГАП	ГИП





Маркировка:
 К4.В1.С4 – 17 шт.
 К4.В1.С3 – 17шт (зеркально)
 К4.В8.С3 – 17 шт.
 К4.В8.С2 – 17шт (зеркально)
 К4.В22.С3 – 15 шт.
 К4.В22.С2 – 15шт (зеркально)
 К4.В39.С4 – 9 шт.
 К4.В39.С3 – 9шт (зеркально)
 К4.В27.С4 – 1 шт.
 К4.В27.С3 – 1шт (зеркально)
 К4.В29.С3 – 1 шт.
 К4.В29.С2 – 1шт (зеркально)

Цвет: 79 7М15

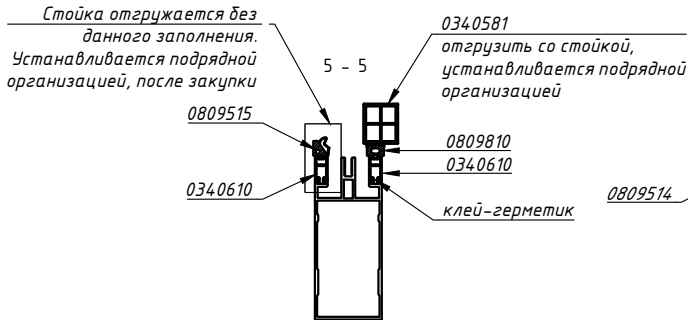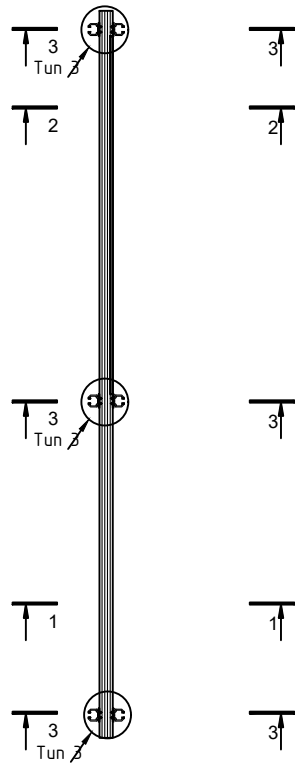

Маркировка:
 К4.В1.С5 – 17 шт.
 К4.В8.С1 – 17 шт. (зеркально)
 К4.В22.С1 – 15 шт. (зеркально)
 К4.В39.С5 – 9 шт.
 К4.В27.С5 – 9 шт.
 К4.В29.С1 – 1 шт. (зеркально)

Цвет: 79 7М15

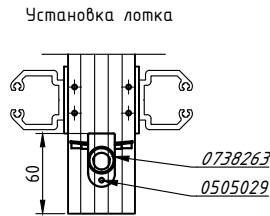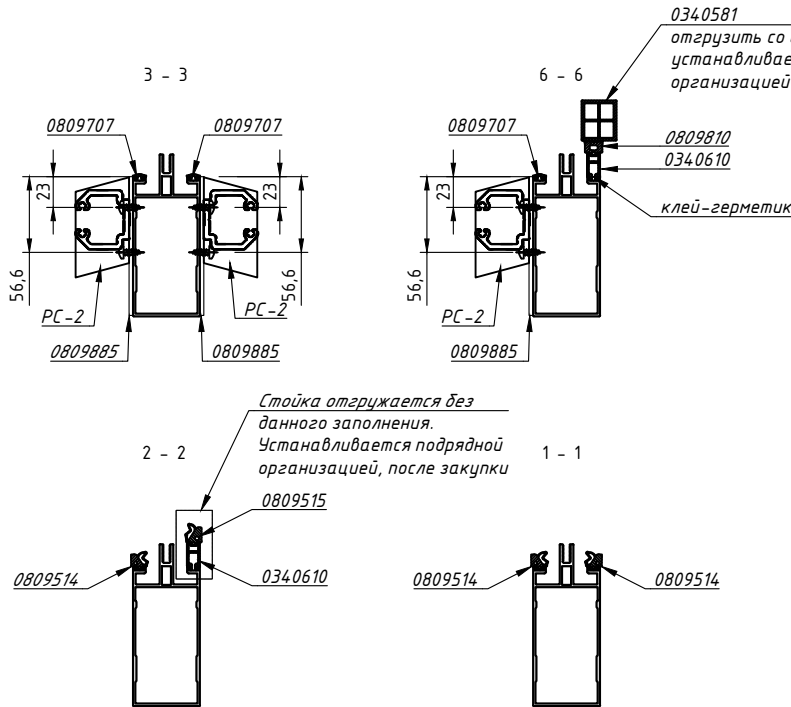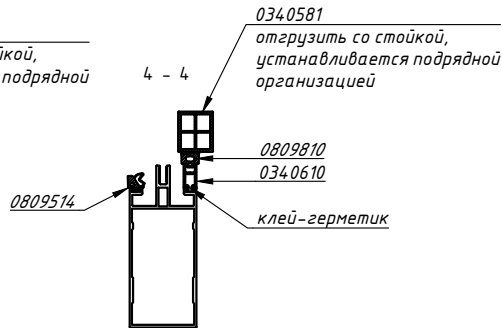
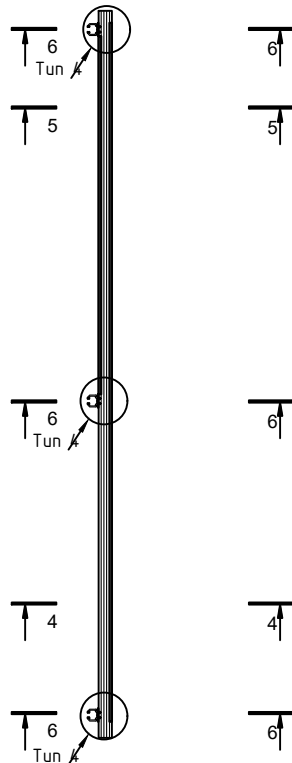


Тип крепления ригельного сухаря см. лист 3

- Примечание.
1. Каждую стойку перед производством работ оклеить защитной пленкой,замаркировать номером стойки и укомплектовать уплотнителями и филлистрами
 2. Стойки укомплектовать подпятниками из 034.5593 L=200 мм и
 3. Манжету 080.9885 и сухарь PC-2 установить на производстве по шаблону. Манжету подрезать по торцу ригеля.
 4. Ригельные сухари PC-1 и PC-2 устанавливать на саморез Ø4,8x13 – 0525330.

						Остров 2 К1			
						" Многофункциональная комплексная жилая застройка , квартал 2, корпус 1, 2, 3, 4, 5, 6 по адресу : г . Москва , внутригородская территория муниципальный округ Хорошёво –Мнёвники."			
Изм.	Кол.уч.	Лист	№ док.	Подп.	Дата	Светопрзрачные конструкции	Стадия	Лист	Листов
Разраб.	Бирюкова				06.23		Р	52	
Проверил									
Н. контр.						Стойки В1, В8, В22, В39, В27, В29	ООО "МАРКА ПОЛА"		
Т. контр.									
Утв.									



Согласовано	ГАП	
Инв. N подл.	ГИП	
Подп. и дата	Взам. инв. N	

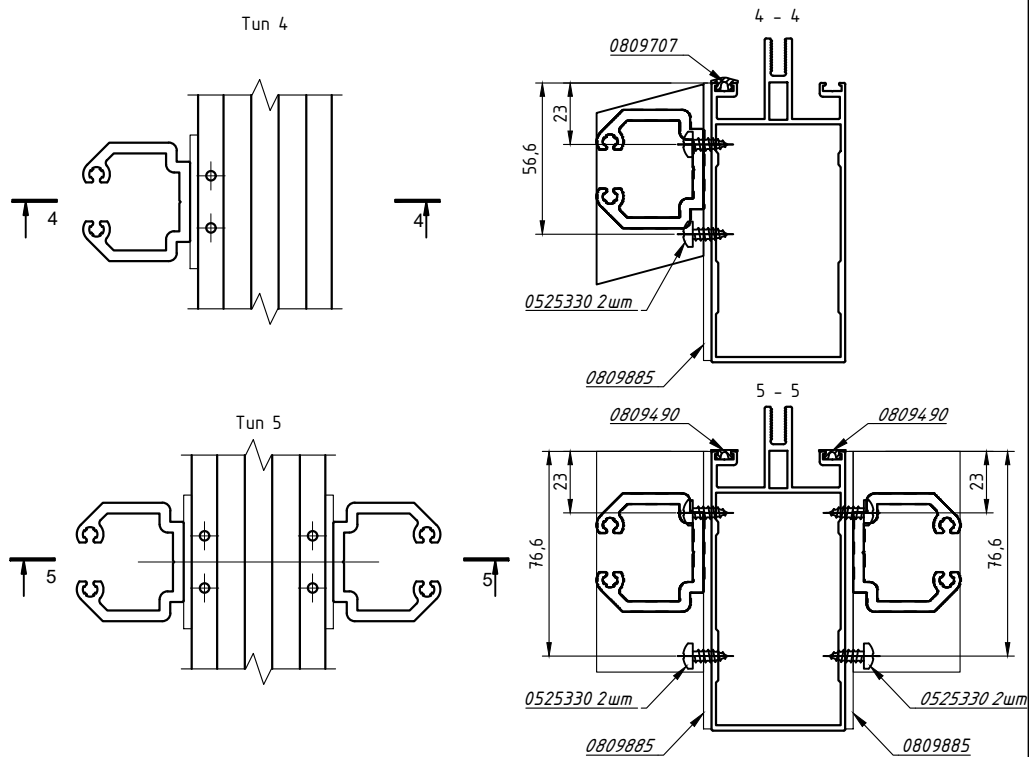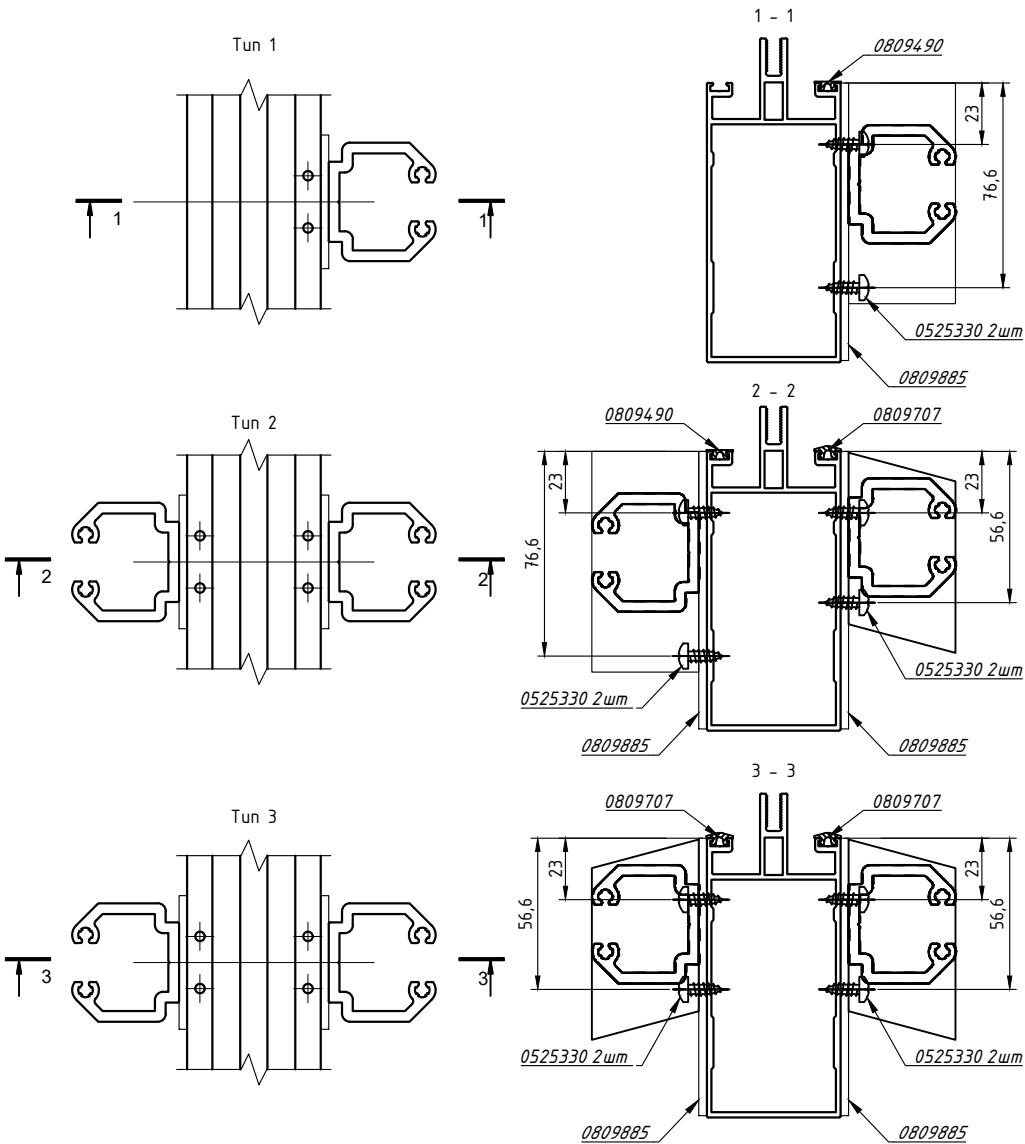

- Примечание.
- Манжету 080.9885 и сухарь РС-2 установить на производстве по шаблону. Манжету подрезать по торцу ригеля.
 - Ригельные сухари РС-1 и РС-2 устанавливать на саморез Ø4,8х13 – 0525330.

						Остров 2 К1			
						" Многофункциональная комплексная жилая застройка , квартал 2, корпус 1, 2, 3, 4, 5, 6 по адресу : г . Москва , внутригородская территория муниципальный округ Хорошёво –Мнёвники."			
Изм.	Кол.уч.	Лист	№ док.	Подп.	Дата	Светопрозрачные конструкции	Стадия	Лист	Листов
Разраб.	Бирюкова				06.23		Р	53	
Проверил									
Н.контр.						Стойки В1, В8, В22, В39, В27, В29	ООО "МАРКА ПОЛА"		
Т.контр.									
Утв.									

Профиль рузеля 0343524
Цвет: 79 7M15

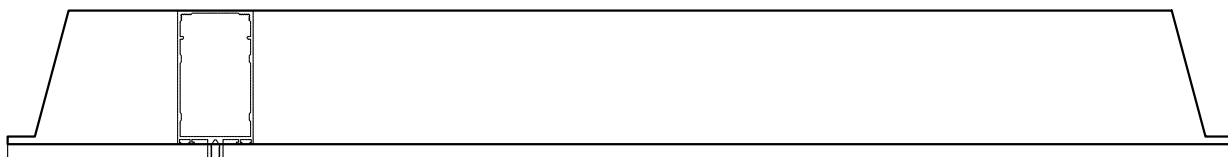
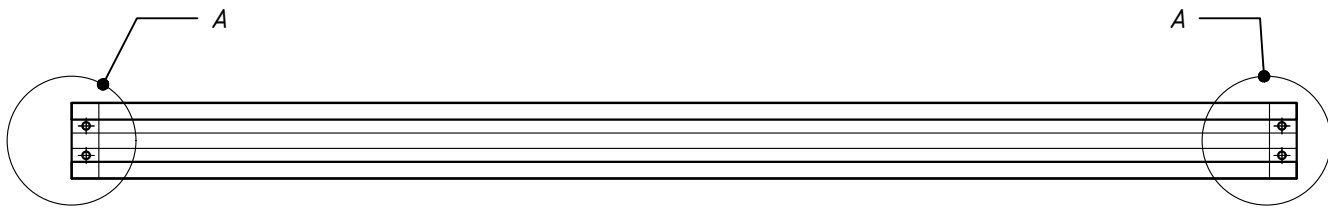


Маркировка	L, мм	Кол-во
K4.B1.R2	569,2	34
K4.B8.R2	590,2	34
K4.B22.R2	587,2	30
K4.B39.R2	629,2	18
K4.B27.R2	598,2	2
K4.B29.R2	598,2	2

Заполнение

*Ригель отгружается без
данного заполнения.
Устанавливается подрядной
организацией, после закупки*

Odyp. A (2:1)

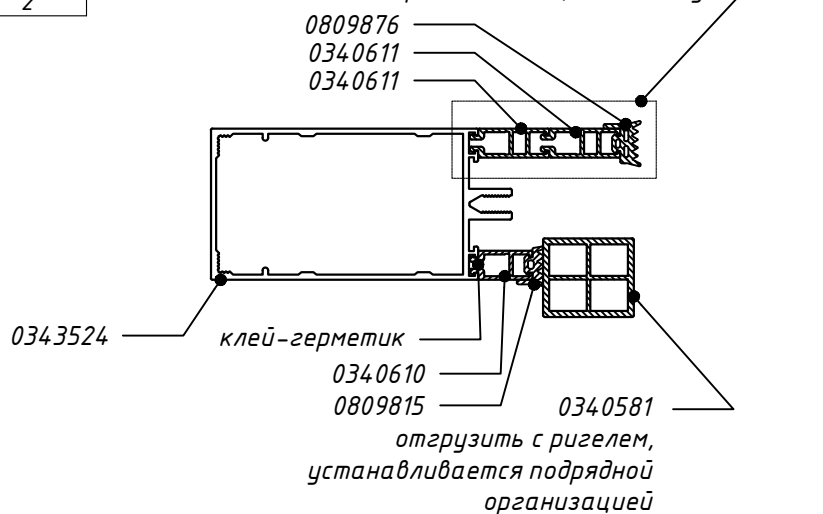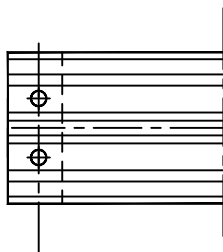


Примечание.

1. Каждый рулель перед производством работ оклеить защитной пленкой, замаркировать номером стойки и укомплектовать уплотнителями и флистрами


						Остров 2 К1			
						" Многофункциональная комплексная жилая застройка , квартал 2, корпус 1, 2, 3, 4, 5, 6 по адресу : г . Москва , внутригородская территория муниципальный округ Хорошёво –Мнёвники."			
Изм.	Кол.уч.	Лист	№ док.	Подп.	Дата				
Разраб.		Бирюкова			06.23	Светопрозрачные конструкции	Стадия	Лист	Листов
Проверил							Р	54	
Н.контр.									
						Ризели	ООО "МАРКА ПОЛА"		
Т.контр.									
Утв.									

Копировал


Профиль рузеля 0343524
Цвем: 79 7M15

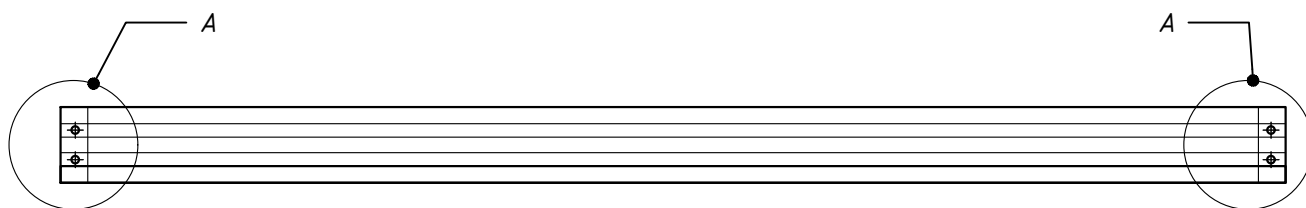

Маркировка	L, мм	Кол-во
K4.B1.R1	569,2	68
K4.B8.R1	590,2	68
K4.B22.R1	587,2	60
K4.B39.R1	629,2	36
K4.B27.R1	598,2	4
K4.B29.R1	598,2	4

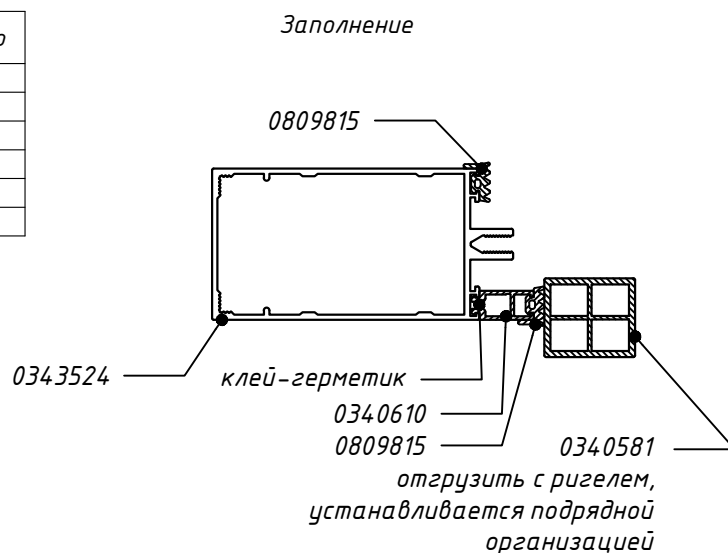

0δρ. A (2:1)

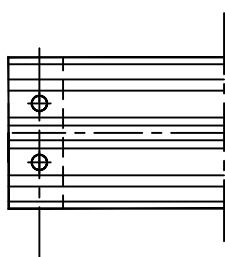



Примечание.

1. Каждый рулель перед производством работ оклеить защитной пленкой, замаркировать номером стойки и укомплектовать уплотнителями и флистрами

						Остров 2 К1			
						" Многофункциональная комплексная жилая застройка , квартал 2, корпус 1, 2, 3, 4, 5, 6 по адресу : г . Москва , внутригородская территория муниципальный округ Хорошёво –Мнёвники."			
Изм.	Кол.уч.	Лист	№ док.	Подп.	Дата				
Разраб.		Бирюкова			06.23	Светопрозрачные конструкции	Стадия	Лист	Листов
Проверил							Р	55	
Н.контр.									
						Ризели	ООО "МАРКА ПОЛА"		
Т.контр.									
Утв.									

Копировал


Профиль рузеля 0343524
Цвем: 79 7M15

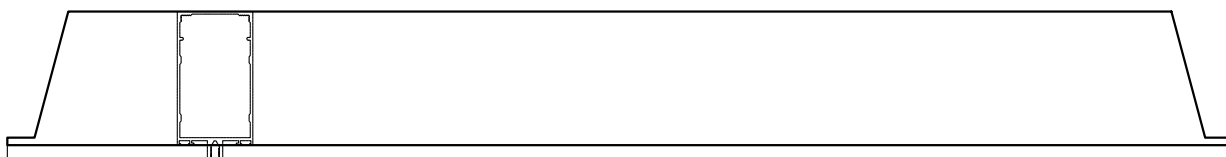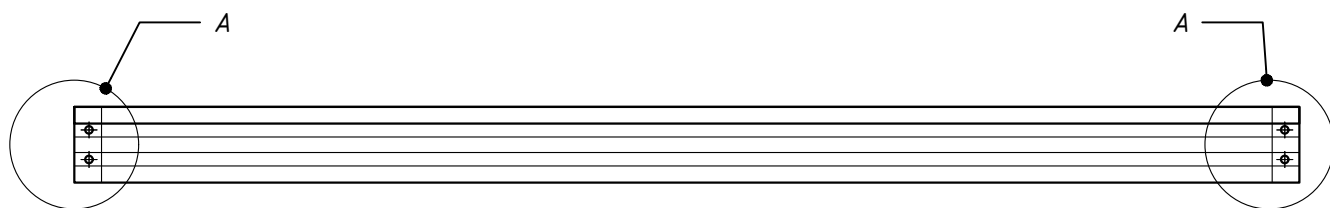


Маркировка	L, мм	Кол-во
K4.B1.R4	569,2	34
K4.B8.R4	590,2	34
K4.B22.R4	587,2	30
K4.B39.R4	629,2	18
K4.B27.R4	598,2	2
K4.B29.R4	598,2	2

Заполнение

Ригель отгружается без
данного заполнения.
Поставляется подрядной
организацией, после закупки

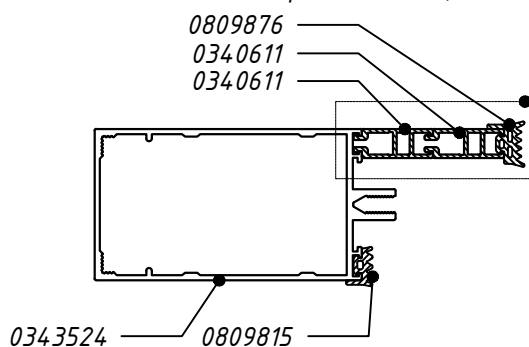

Odypoda A (2:1)

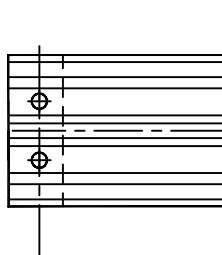

Примечание.

1. Каждый рулель перед производством работ оклеить защитной пленкой, замаркировать номером стойки и укомплектовать уплотнителями и флистерами

Остров 2 К1

" Многофункциональная комплексная жилая застройка , квартал 2, корпус 1, 2, 3, 4, 5, 6 по адресу : г . Москва , внутригородская территория муниципальный округ Хорошёво – Мнёвники."

Светопрозрачные конструкции


Ризели

Листья	Лист	Листов
Р	56	

ООО "МАРКА ПОЛА"


Копировал

Профиль рузеля 0343524
Цвем: 79 7M15

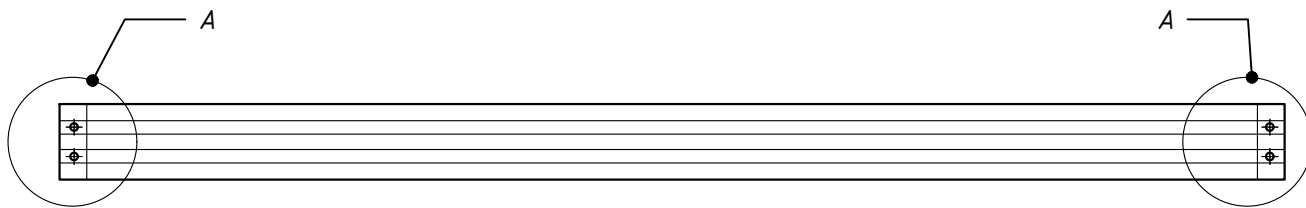


Маркировка	L, мм	Кол-во
K4.B1.R3	569,2	17
K4.B8.R3	590,2	17
K4.B22.R3	587,2	15
K4.B39.R3	629,2	9
K4.B27.R3	598,2	1
K4.B29.R3	598,2	1

Заполнение

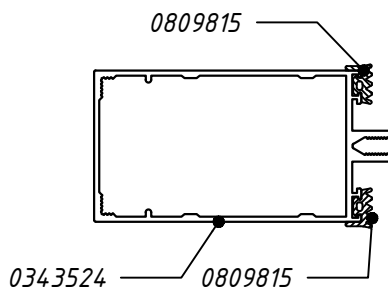

Odor. A (2:1)

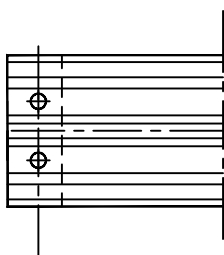


Примечание.

1. Каждый рулель перед производством работ оклеить защитной пленкой, замаркировать номером стойки и укомплектовать уплотнителями и флистерами


						Остров 2 К1			
						" Многофункциональная комплексная жилая застройка , квартал 2, корпус 1, 2, 3, 4, 5, 6 по адресу : г . Москва , внутригородская территория муниципальный округ Хорошёво –Мнёвники."			
Изм.	Кол.уч.	Лист	№ док.	Подп.	Дата				
Разраб.		Бирюкова			06.23	Светопрозрачные конструкции	Стадия	Лист	Листов
Проверил							Р	57	
Н.контр.									
						Ризели	ООО "МАРКА ПОЛА"		
Т.контр.									
Утв.									

Копировал


Профиль рузеля 0343525
Цвет: 79 7M15

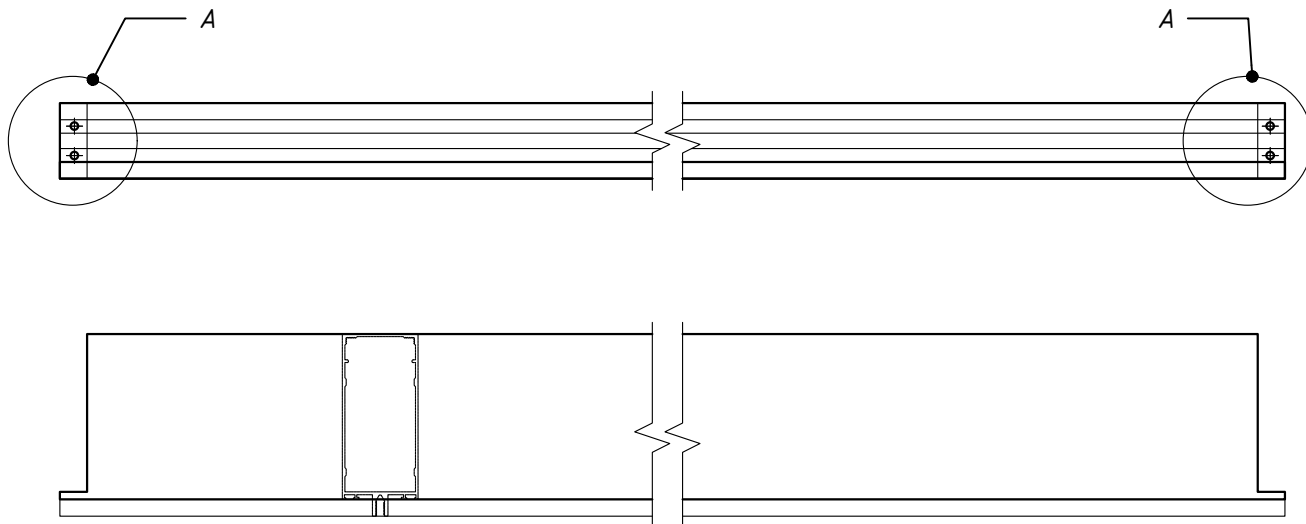

Маркировка	L, мм	Кол-во
K4.B1.R5	710,0	68
K4.B8.R5	710,0	34
K4.B8.R7	715,0	34
K4.B22.R5	600,0	60
K4.B39.R5	560,0	36
K4.B27.R5	835,0	2
K4.B27.R7	840,0	2
K4.B29.R5	835,0	2
K4.B29.R7	840,0	2

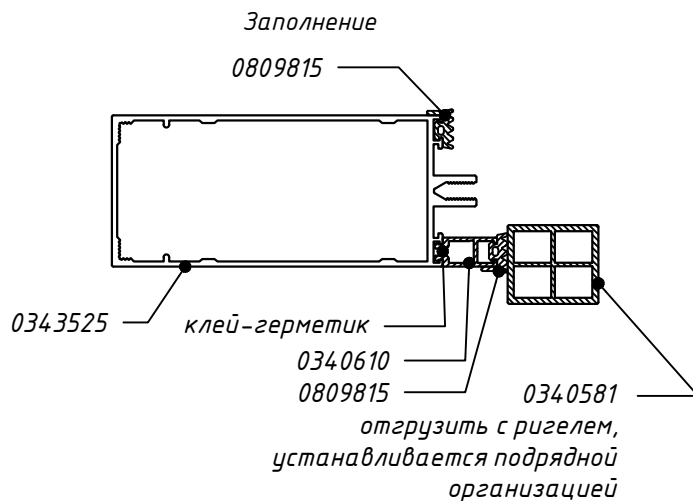

Odor. A (2:1)

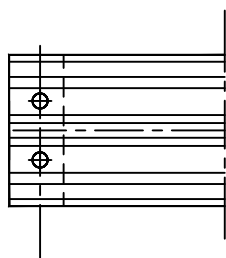

Примечание.

1. Каждый рулель перед производством работ оклеить защитной пленкой, замаркировать номером стойки и укомплектовать уплотнителями и флистерами

						Остров 2 К1			
						" Многофункциональная комплексная жилая застройка , квартал 2, корпус 1, 2, 3, 4, 5, 6 по адресу : г . Москва , внутригородская территория муниципальный округ Хорошёво –Мнёвники."			
Изм.	Кол.уч.	Лист	№ док.	Подп.	Дата	Светопрозрачные конструкции	Стадия	Лист	Листов
Разраб.		Бирюкова			06.23		Р	58	
Проверил									
Н.контр.									
Т.контр.						Ризели	ООО "МАРКА ПОЛА"		
Утв.									

Копировал

Согласовано

ГДП



СИП

Взам. инв. №


Подп. и дата

Инв. N подл.

Инв. N подл.	Подп. и дата	Взам. инв. N	Согласовано	
			ГАП	
			ГИП	

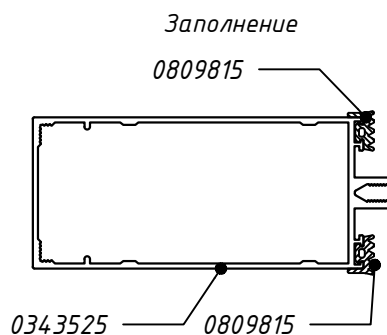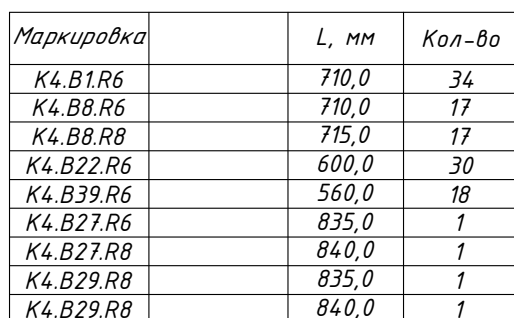



Οδρ. Α (2:1)

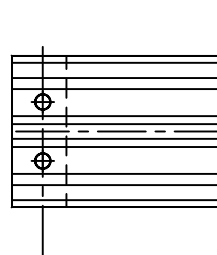

1. Каждый рулель перед производством работ оклеить защитной пленкой, замаркировать номером стойки и укомплектовать уплотнителями и флистерами



						Остров 2 К1			
						" Многофункциональная комплексная жилая застройка , квартал 2, корпус 1, 2, 3, 4, 5, 6 по адресу : г . Москва , внутригородская территория муниципальный округ Хорошёво –Мнёвники."			
Изм.	Кол.уч.	Лист	№ док.	Подп.	Дата				
Разраб.		Бирюкова			06.23	Светопрозрачные конструкции	Стадия	Лист	Листов
Проверил							Р	59	
Н.контр.									
						Ризели	ООО "МАРКА ПОЛА"		
Т.контр.									
Утв.									

Прижимная планка стойки
Цвет: без покраски

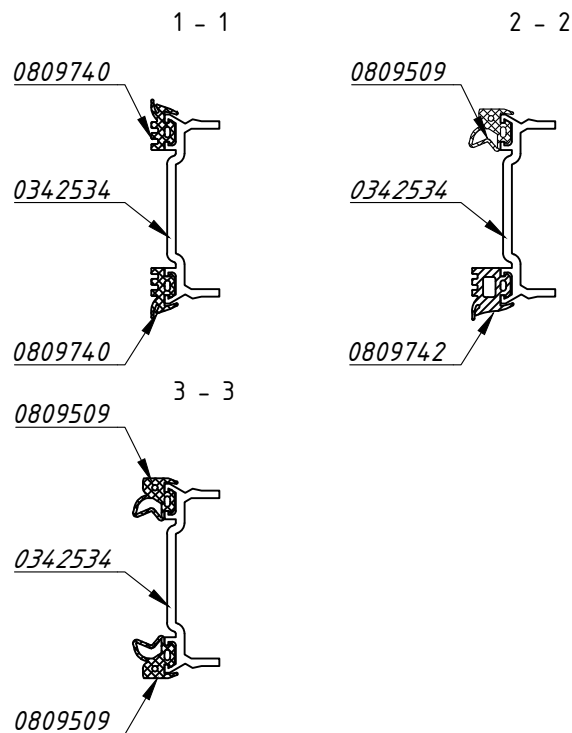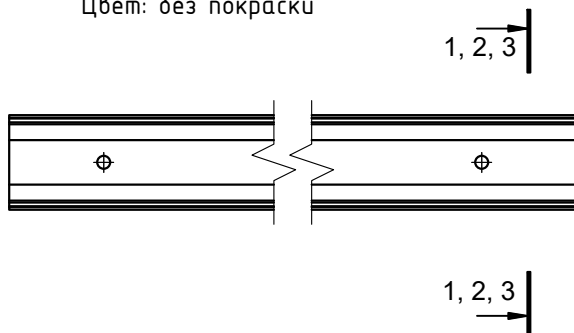

Маркировка	№ Сечения	L, мм	Кол-во
K4.B1.PS1	2 - 2	2615,0	34
K4.B1.PS2	3 - 3	2615,0	34
K4.B1.PS3	1 - 1	2615,0	34
K4.B8.PS1	2 - 2	2615,0	34
K4.B8.PS2	3 - 3	2615,0	34
K4.B8.PS3	1 - 1	2615,0	34
K4.B22.PS1	2 - 2	2615,0	30
K4.B22.PS2	3 - 3	2615,0	30
K4.B22.PS3	1 - 1	2615,0	30
K4.B39.PS1	2 - 2	2615,0	18
K4.B39.PS2	3 - 3	2615,0	18
K4.B39.PS3	1 - 1	2615,0	18
K4.B27.PS1	2 - 2	2615,0	2
K4.B27.PS2	3 - 3	2615,0	2
K4.B27.PS3	1 - 1	2615,0	2
K4.B29.PS1	2 - 2	2615,0	2
K4.B29.PS2	3 - 3	2615,0	2
K4.B29.PS3	1 - 1	2615,0	2

Крышка стойки
Цвет: 79 9M05

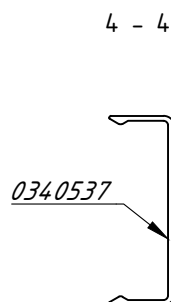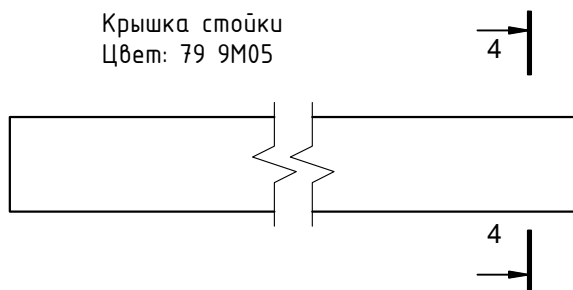

Маркировка	L, мм	Кол-во
K4.B1.KS1	2615,0	102
K4.B8.KS1	2615,0	102
K4.B22.KS1	2615,0	90
K4.B39.KS1	2615,0	54
K4.B27.KS1	2615,0	6
K4.B29.KS1	2615,0	6

Согласовано	ГАП	Взам. инв. №	Подп. и дата	Инв. № подл.	
	ГИП				
Изм.	Кол.уч.	Лист	№ док.	Подп.	Дата
Разраб.	Бирюкова				06.23
Проверил					
Н.контр.					
Т.контр.					
Утв.					

Остров 2 К1

" Многофункциональная комплексная жилая застройка , квартал 2, корпус 1, 2, 3, 4, 5, 6 по адресу : г . Москва , внутригородская территория муниципальный округ Хорошёво -Мнёвники."


Светопрозрачные конструкции

Прижим и крышка стойки


Стадия	Лист	Листов
Р	60	

ООО "МАРКА ПОЛА"

Прижимная планка ригеля
Цвет: без покраски

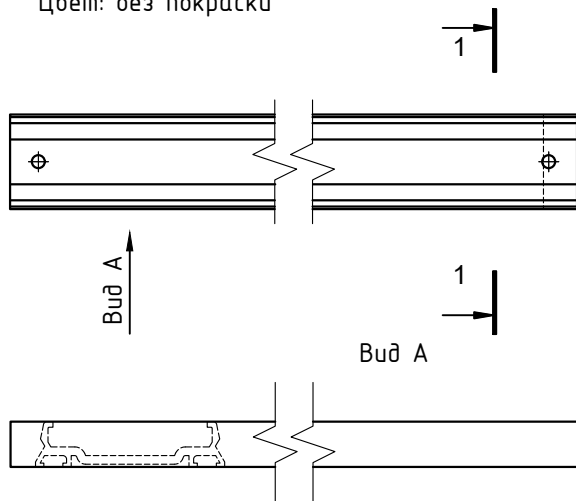


Крышка ригеля
Цвет: 79 9M05

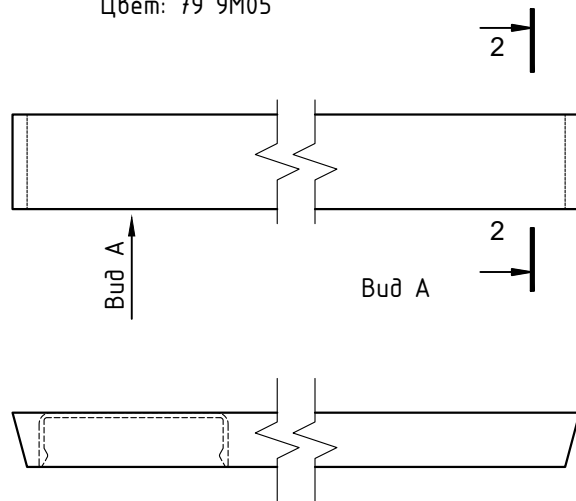

Маркировка		L, мм	Кол-во
K4.B1.PR1		569,0	153
K4.B1.PR2		676,0	102
K4.B8.PR1		590,0	153
K4.B8.PR2		676,0	51
K4.B8.PR3		681,0	51
K4.B22.PR1		587,0	135
K4.B22.PR2		566,0	90
K4.B39.PR1		629,0	81
K4.B39.PR2		526,0	54
K4.B27.PR1		598,0	9
K4.B27.PR2		801,0	3
K4.B27.PR3		806,0	3
K4.B29.PR1		598,0	9
K4.B29.PR2		801,0	3
K4.B29.PR3		806,0	3

Маркировка		L, мм	Кол-во
K4.B1.KR1		579,6	153
K4.B1.KR2	ПРЯМАЯ	678,0	102
K4.B8.KR1		600,6	153
K4.B8.KR2	ПРЯМАЯ	678,0	51
K4.B8.KR3	ПРЯМАЯ	683,0	51
K4.B22.KR1		597,6	135
K4.B22.KR2	ПРЯМАЯ	568,0	90
K4.B39.KR1		639,6	81
K4.B39.KR2	ПРЯМАЯ	528,0	54
K4.B27.KR1		608,6	9
K4.B27.KR2	ПРЯМАЯ	803,0	3
K4.B27.KR3	ПРЯМАЯ	808,0	3
K4.B29.KR1		608,6	9
K4.B29.KR2	ПРЯМАЯ	803,0	3
K4.B29.KR3	ПРЯМАЯ	808,0	3

! ---.---.KR2 и KR3 прямые, без углов запила

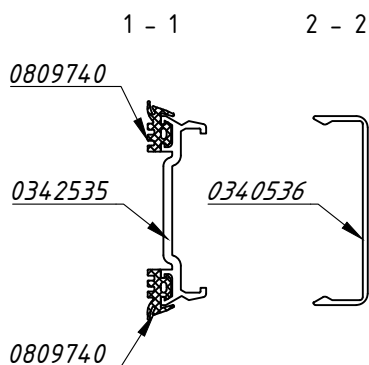


Согласовано	ГАП	Взам. инв. №	Подп. и дата	Инв. № подл.
	ГИП			

						Остров 2 К1			
						" Многофункциональная комплексная жилая застройка , квартал 2, корпус 1, 2, 3, 4, 5, 6 по адресу : г . Москва , внутригородская территория муниципальный округ Хорошёво -Мнёвники."			
Изм.	Кол.уч.	Лист	№ док.	Подп.	Дата	Светопрозрачные конструкции	Стадия	Лист	Листов
Разраб.	Бирюкова				06.23		Р	61	
Проверил									
Н.контр.									
Т.контр.						Прижим и крышка ригеля	ООО "МАРКА ПОЛА"		
Утв.									

Угловой витраж В-1.3 (развертка).



Кол-во: 1 шт.

S=7,61м.кв.

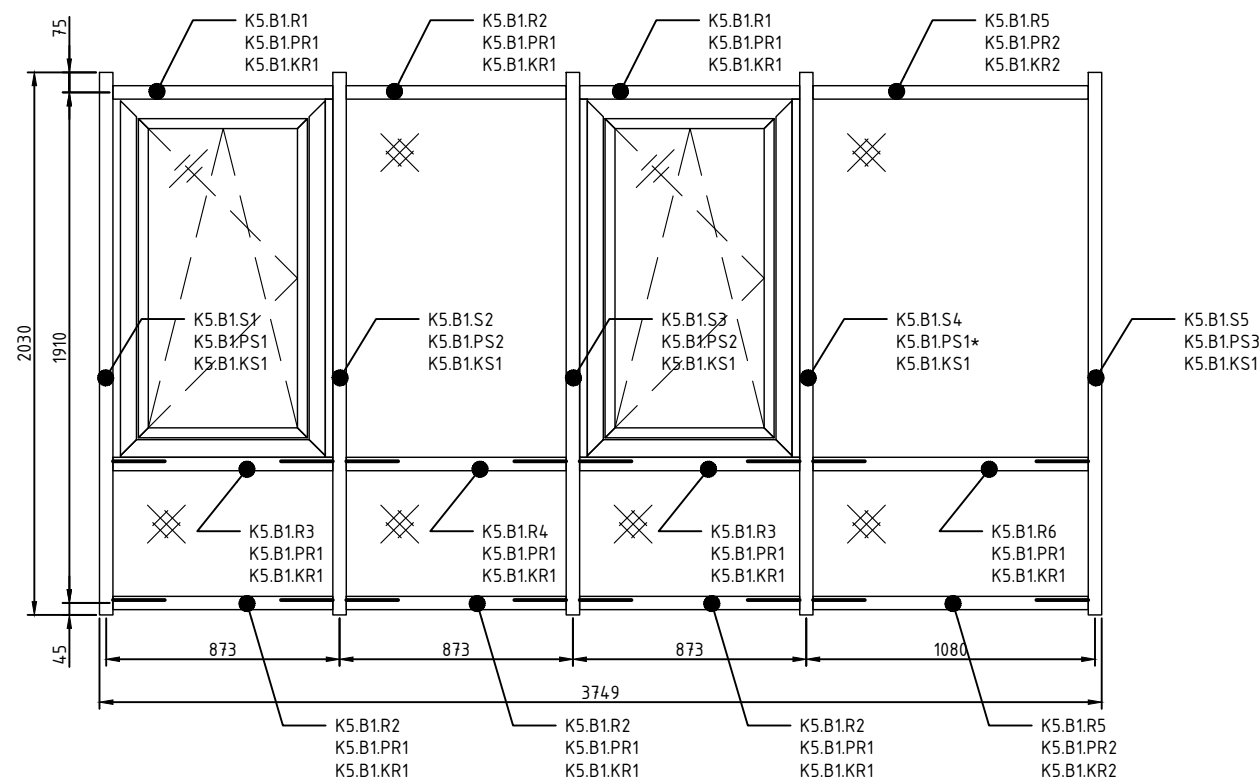

Заполнение термовставки - 0809892 + 0809893.
Под прижимы бутиловая лента - 0849711.
Прижимной саморез:
- прижимы PS1, PS2, PS1* - Ø6,3x67мм - 0535476
- прижимы PS3, PR1, PR2 - Ø6,3x64мм - 0535475

Ризеля крепить саморезом Ø4,2x12,7мм - 0525317

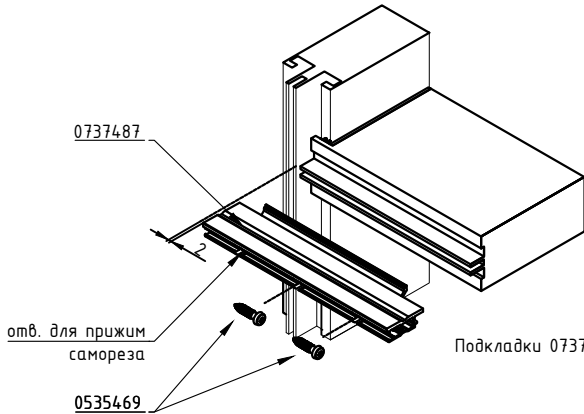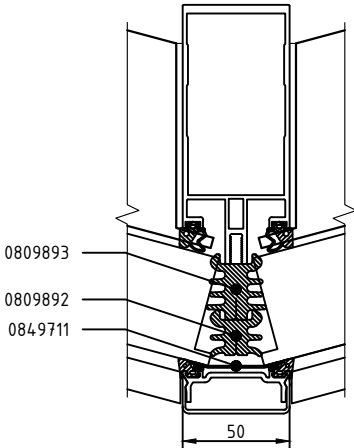

Подкладка 0737487

Подкладки 0737487 напилить из профиля 0340385.

						Остров 2 К1			
						" Многофункциональная комплексная жилая застройка , квартал 2, корпус 1, 2, 3, 4, 5, 6 по адресу : г . Москва , внутригородская территория муниципальный округ Хорошёво -Мнёвники."			
Изм.	Кол.уч.	Лист	№ док.	Подп.	Дата	Светопрозрачные конструкции	Стадия	Лист	Листов
Разраб.		Бирюкова			06.23		Р	62	
Проверил									
Н.контр.						Витраж В1.3	ООО "МАРКА ПОЛА"		
Т.контр.									
Утв.									


Копировал

Согласовано					
ГАП					
ГИП					
Инв. N подл.	Подп. и дата	Взам. инв. N			


Угловой витраж В-6.2 (развертка).

Кол-во: 1 шт.


S=9,07 м.кв.

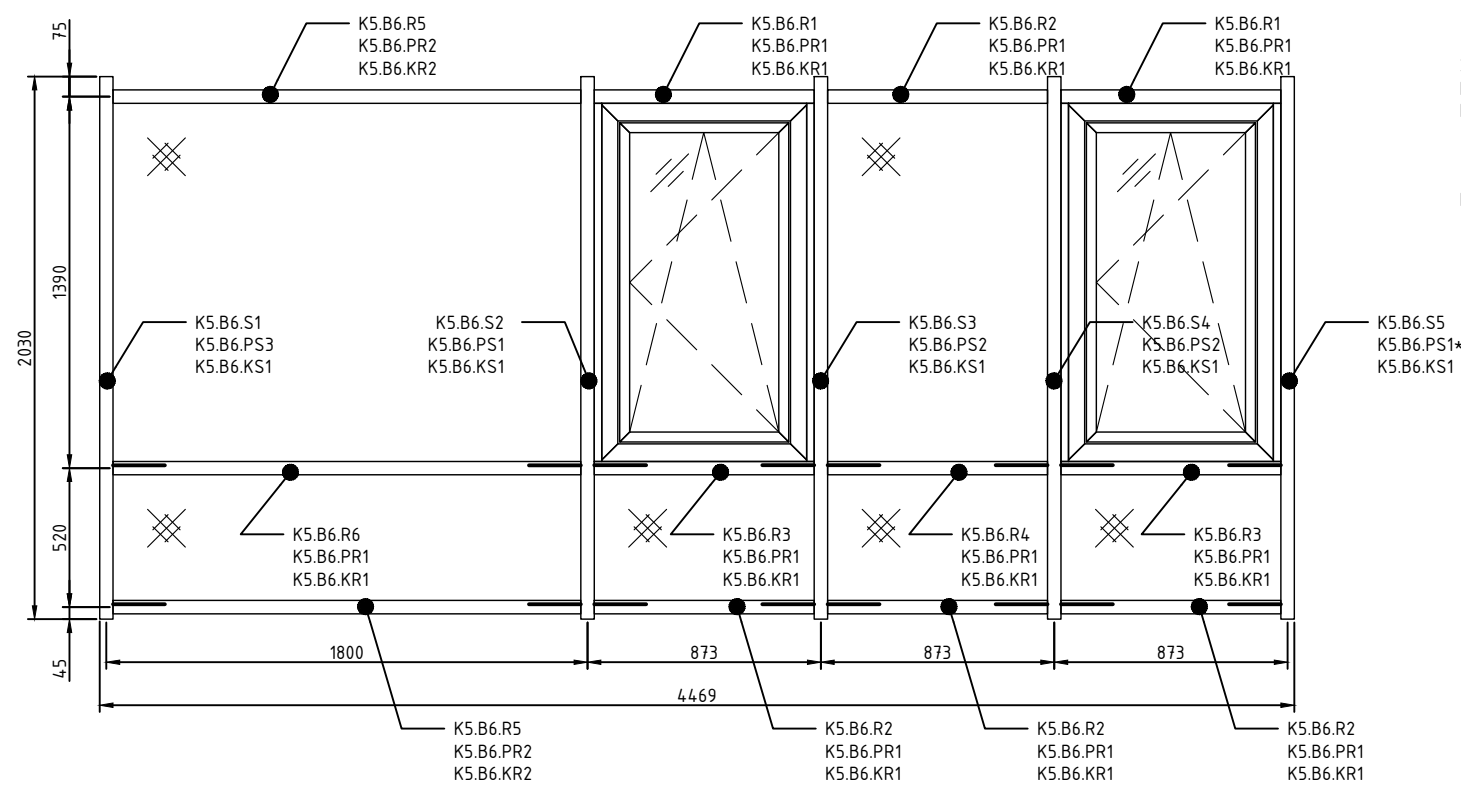

Заполнение термовставки - 0809892 + 0809893.
Под прижимы бутиловая лента - 0849711.
Прижимной саморез:
- прижимы PS1, PS2, PS1* - Ø6,3x67мм - 0535476
- прижимы PS3, PR1, PR2 - Ø6,3x64мм - 0535475
Ригеля крепить саморезом Ø4,2x12,7мм - 0525317

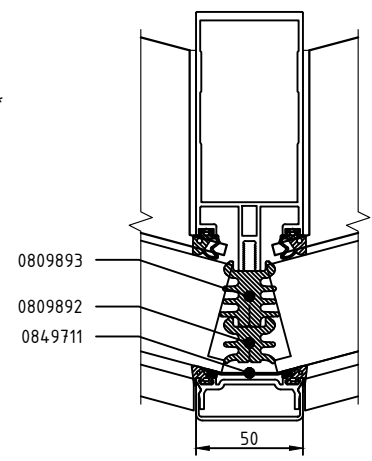

Согласовано	ГАП	ГИП
Инв. и дата	Подп. инв. и дата	Взам. инв. и дата
Инв. и подл.	Подп. инв. и подл.	Взам. инв. и подл.

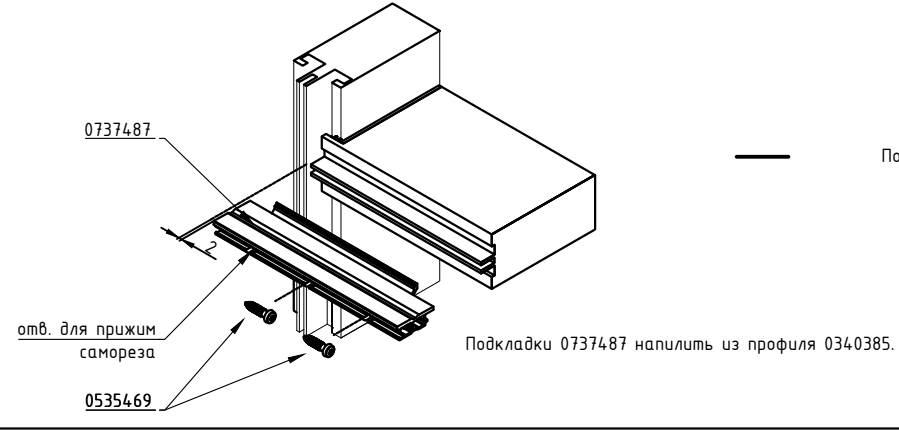


Подкладка 0737487

						Остров 2 К1				
						“ Многофункциональная комплексная жилая застройка , квартал 2, корпус 1, 2, 3, 4, 5, 6 по адресу : г . Москва , внутригородская территория муниципальный округ Хорошёво –Мнёвники.”				
Изм.	Кол.уч.	Лист	№ док	Подп.	Дата	Светопрозрачные конструкции		Стадия	Лист	Листов
Разраб.	Бирюкова				06.23			Р	63	
Проверил										
Н.контр.						Витраж В6.2		ООО “МАРКА ПОЛА”		
Т.контр.										
Утв.										

Угловой витраж В-8.3 (развертка).



Кол-во: 1 шт.

S=9,16 м.кв.

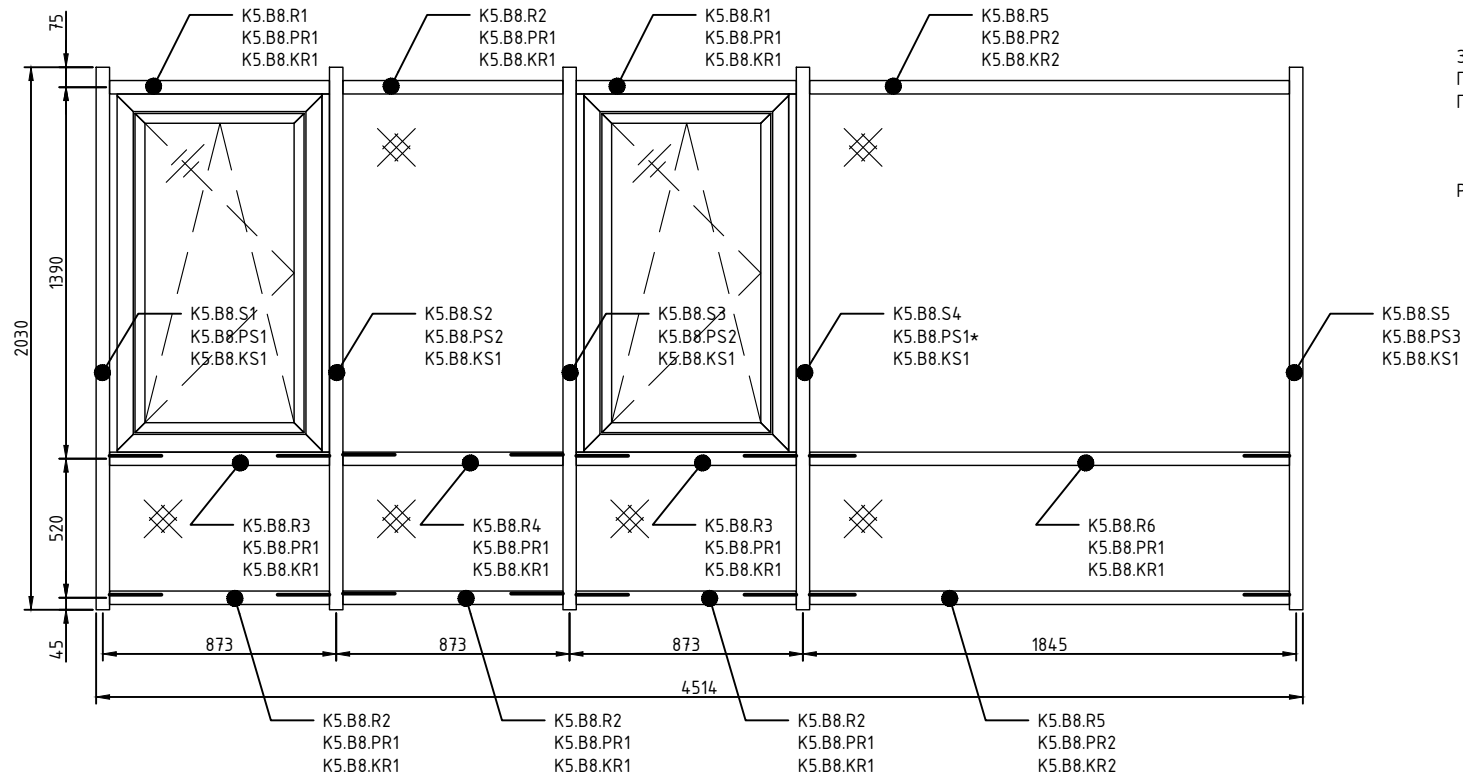

Заполнение термовставки - 0809892 + 0809893.
Под прижимы бутиловая лента - 0849711.
Прижимной саморез:
- прижимы PS1, PS2, PS1* - Ø6,3x67мм - 0535476
- прижимы PS3, PR1, PR2 - Ø6,3x64мм - 0535475

Ригеля крепить саморезом Ø4,2x12,7мм - 0525317

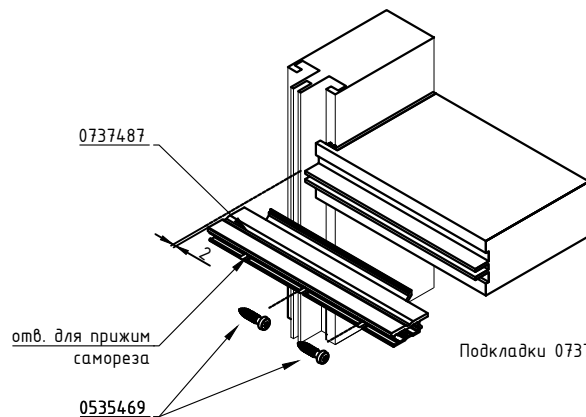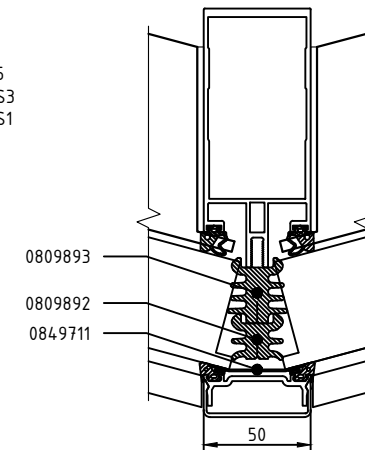

Подкладки 0737487 напилить из профиля 0340385.

Подкладка 0737487

						Остров 2 К1			
						" Многофункциональная комплексная жилая застройка , квартал 2, корпус 1, 2, 3, 4, 5, 6 по адресу : г . Москва , внутригородская территория муниципальный округ Хорошёво -Мнёвники."			
Изм.	Кол.уч.	Лист	№ док.	Подп.	Дата	Светопрозрачные конструкции	Стадия	Лист	Листов
Разраб.	Бирюкова				06.23		Р	64	
Проверил									
Н.контр.						Витраж В8.3	ООО "МАРКА ПОЛА"		
Т.контр.									
Утв.									


Копировал

Согласовано	Взам. инв. №	Подп. и дата	Инв. № подл.
ГАП			
ГИП			

Угловой витраж В-12 (развертка).

Кол-во : 18 шт.

S=12,11 м.кв.

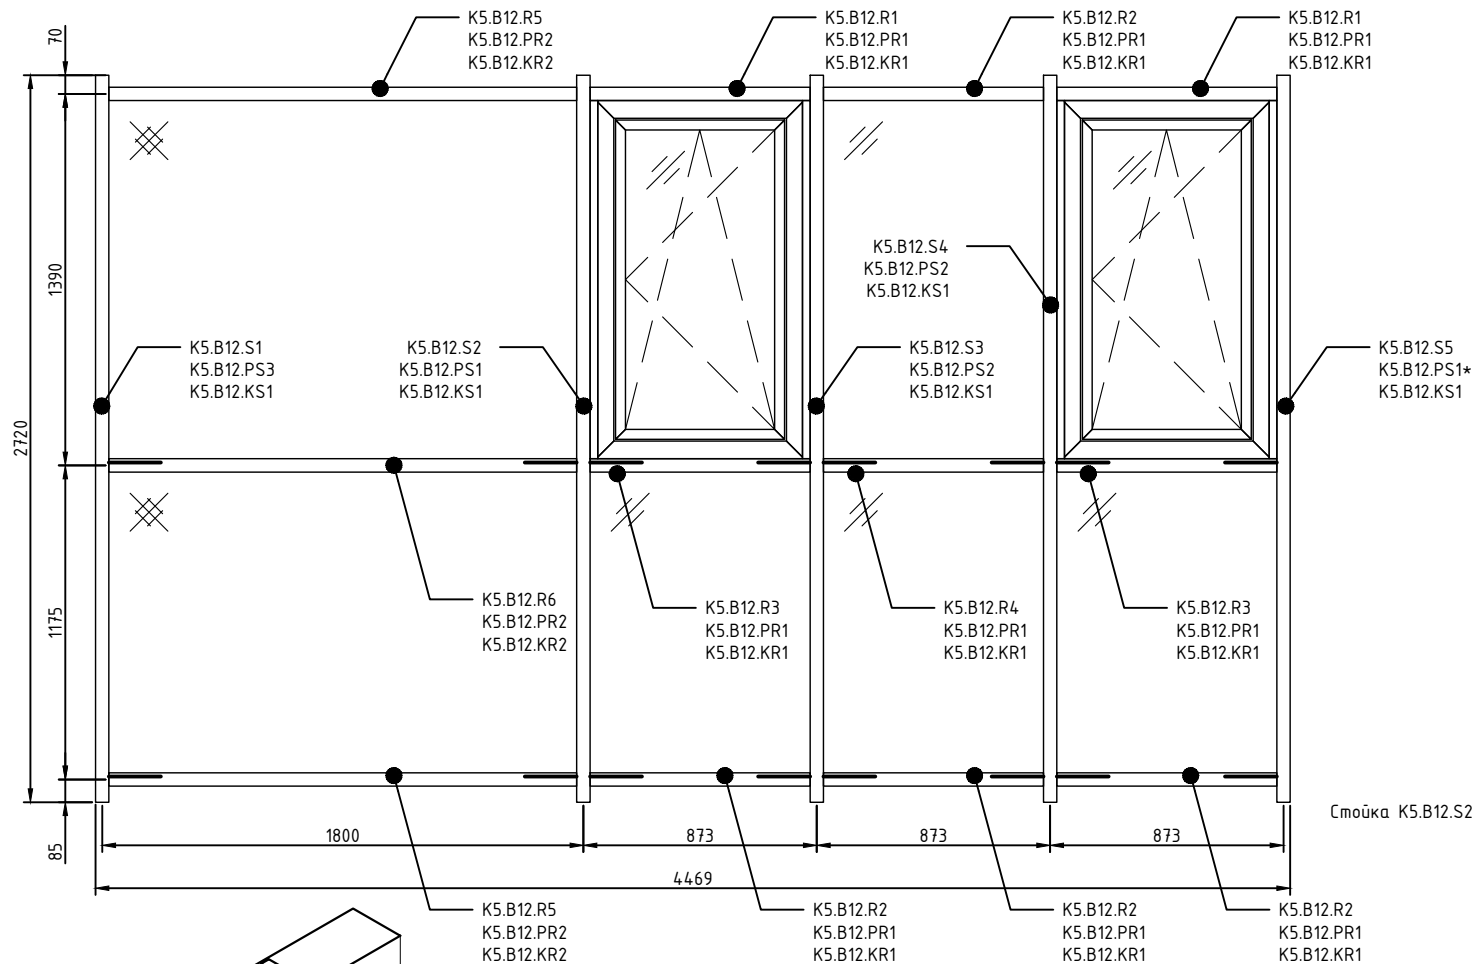


Заполнение термовставки - 0809892 + 0809893.

Под прижимы бутиловая лента - 0849711.

Прижимной саморез:

- прижимы PS1, PS2, PS1* - Ø6,3x67мм - 0535476
- прижимы PS3, PR1, PR2 - Ø6,3x64мм - 0535475

Ригеля крепить саморезом Ø4,2x12,7мм - 0525317

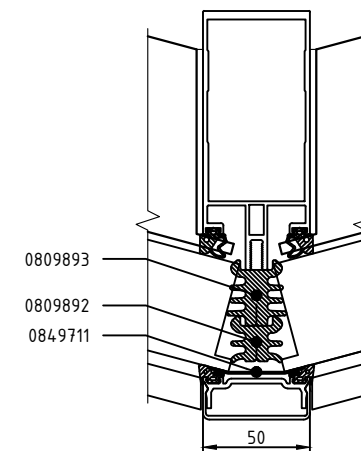

Стойка K5.B12.S2 устанавливается со стоечным сухарем 0345593 во всю длину.

Согласовано

ГАП

ГИП

Взам. инв. №

Подп. и дата

Инв. № подл.

Подкладка 0737487

Подкладки 0737487 напилить из профиля 0340385.

Остров 2 К1

" Многофункциональная комплексная жилая застройка , квартал 2, корпус 1, 2, 3, 4, 5, 6 по адресу : г . Москва , внутригородская территория муниципальный округ Хорошёво -Мнёвники."

Изм.	Кол.уч.	Лист	№ док.	Подп.	Дата
Разраб.	Бирюкова				06.23
Проверил					
Н. контр.					
Т. контр.					
Утв.					

Светопрозрачные конструкции

Стадия	Лист	Листов
Р	65	

Витраж В12


ООО "МАРКА ПОЛА"

Копировал

Угловой витраж В-13 (развертка).

Кол-во : 18 шт.

S=10,16 м.кв.

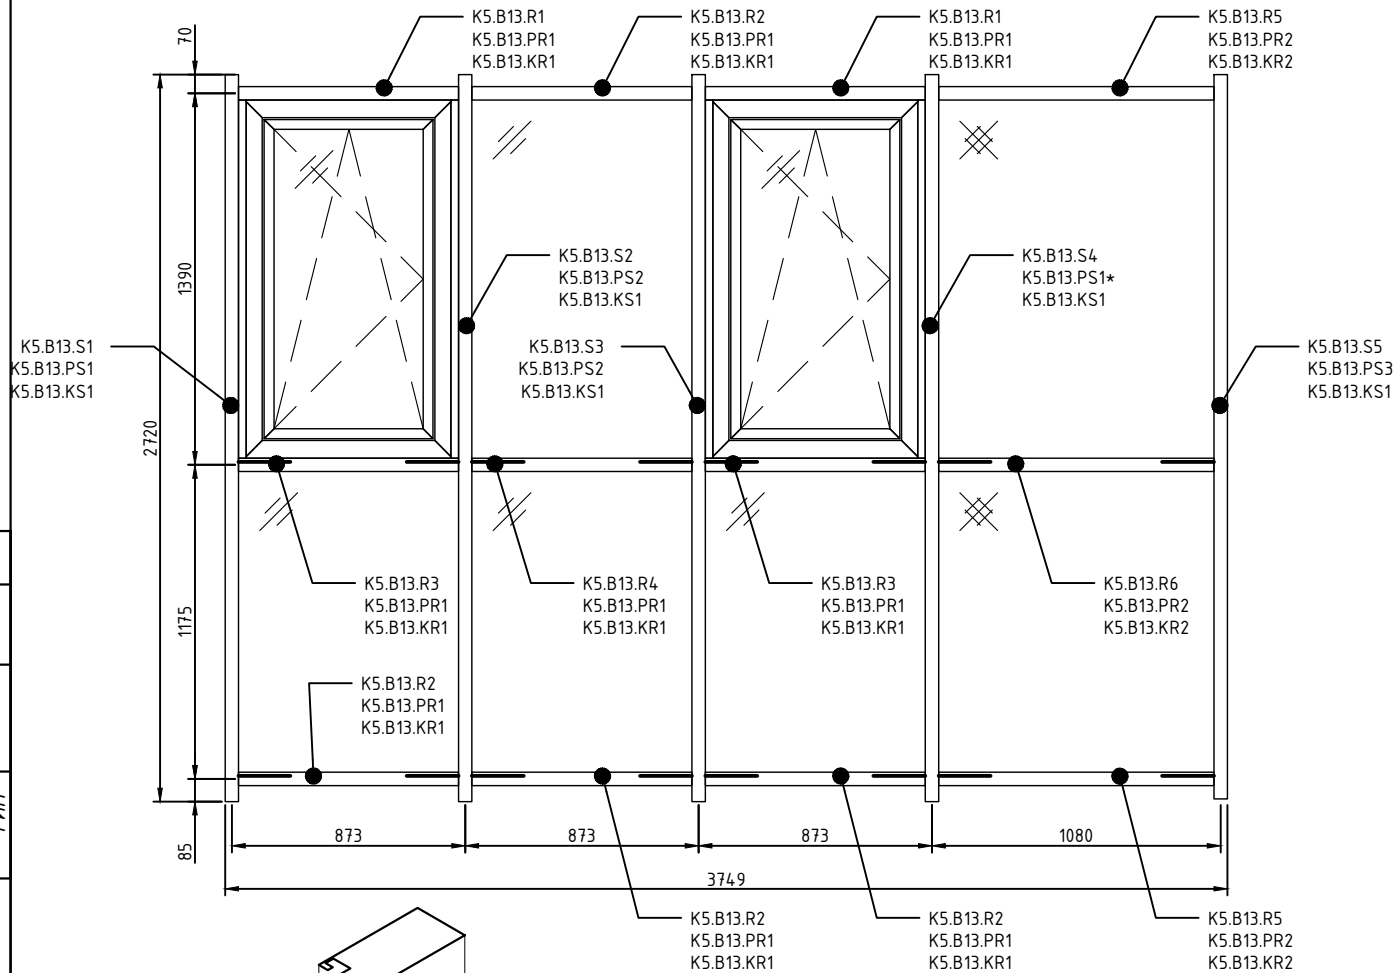



Заполнение термовставки - 0809892 + 0809893.

Под прижимы бутиловая лента - 0849711.

Прижимной саморез:

- прижимы PS1, PS2, PS1* - Ø6,3x67мм - 0535476
- прижимы PS3, PR1, PR2 - Ø6,3x64мм - 0535475

Ригеля крепить саморезом Ø4,2x12,7мм - 0525317

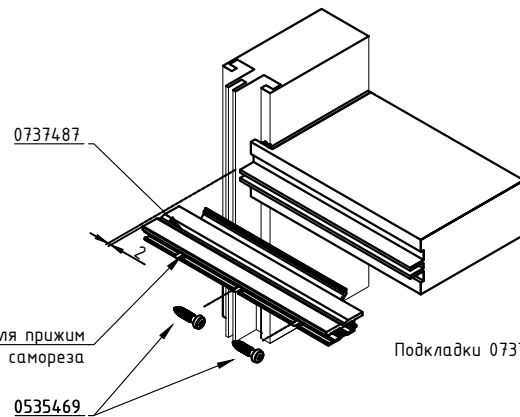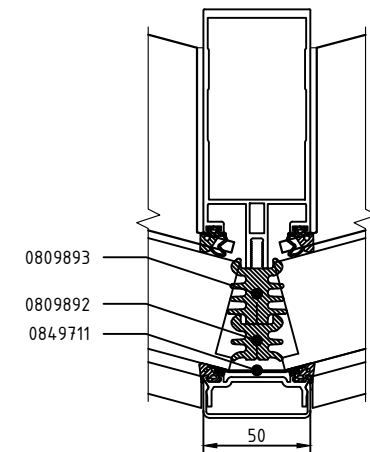

Подкладка 0737487

Подкладки 0737487 напилить из профиля 0340385.

						Остров 2 К1			
						" Многофункциональная комплексная жилая застройка , квартал 2, корпус 1, 2, 3, 4, 5, 6 по адресу : г . Москва , внутригородская территория муниципальный округ Хорошёво -Мнёвники."			
Изм.	Кол.уч.	Лист	№ док.	Подп.	Дата	Светопрзрачные конструкции	Стадия	Лист	Листов
Разраб.	Бирюкова				06.23		Р	66	
Проверил									
Н. контр.									
Т. контр.						Витраж В13			
Утв.						ООО "МАРКА ПОЛА"			


Копировал

Согласовано	ГАП	ГИП
Инв. N подл.	Подп. и дата	Взам. инв. N

Угловой витраж В-14 (развертка).

Кол-во: 18 шт.

S=10,00 м.кв.

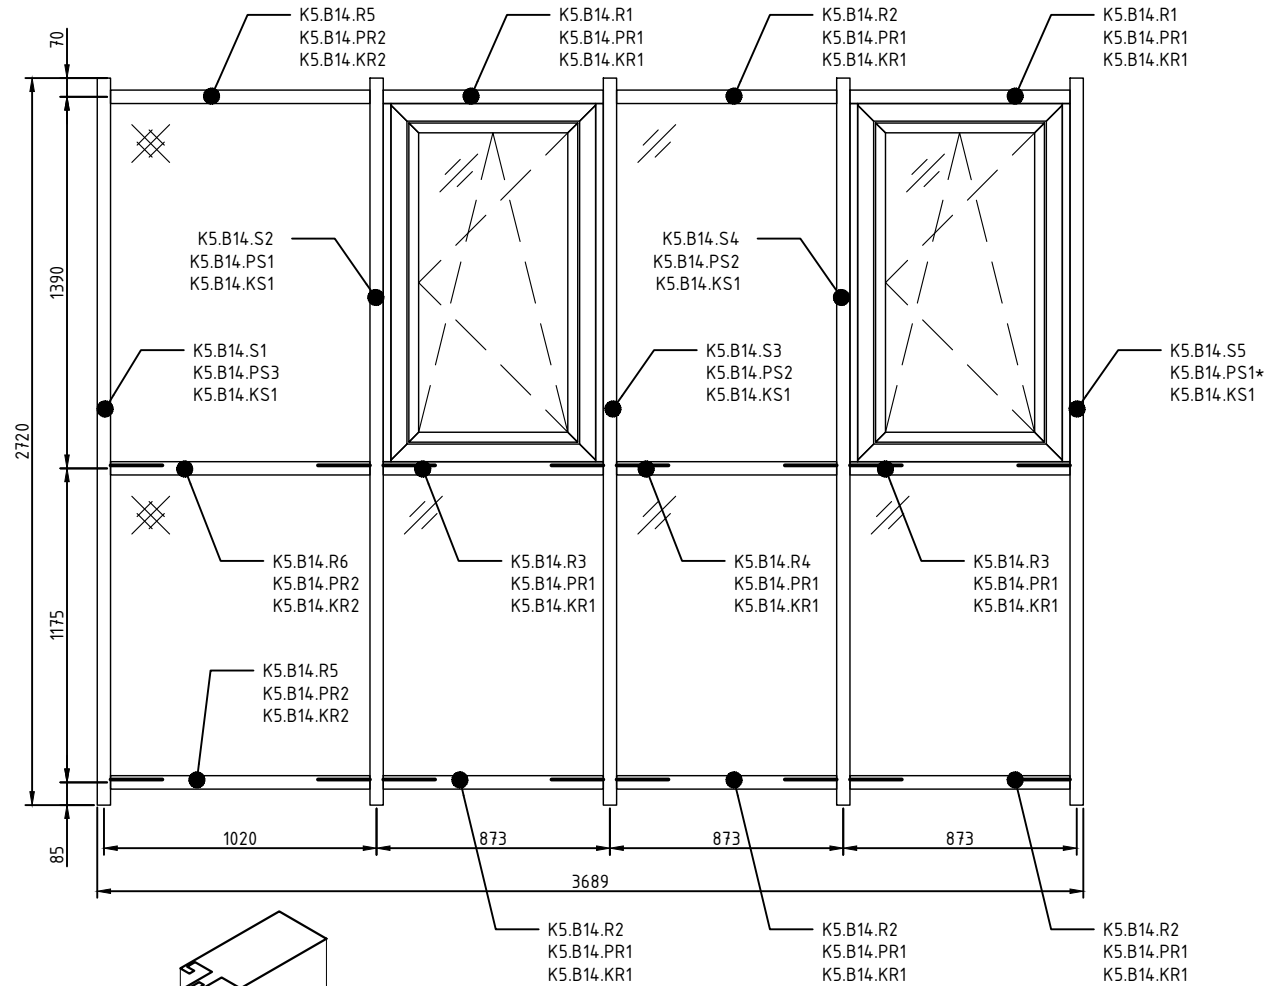



Заполнение термовставки - 0809892 + 0809893.

Под прижимы дублированная лента - 0849711.

Прижимной саморез:

- прижимы PS1, PS2, PS1* - Ø6,3x67мм - 0535476
- прижимы PS3, PR1, PR2 - Ø6,3x64мм - 0535475

Ригеля крепить саморезом Ø4,2x12,7мм - 0525317

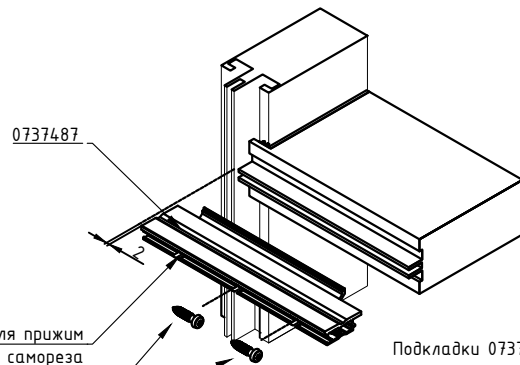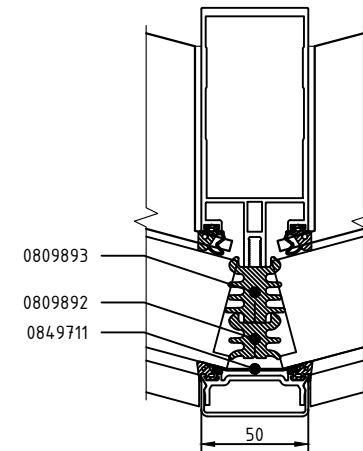

Подкладка 0737487

Подкладки 0737487 напилить из профиля 0340385.

						Остров 2 К1			
						" Многофункциональная комплексная жилая застройка , квартал 2, корпус 1, 2, 3, 4, 5, 6 по адресу : г . Москва , внутригородская территория муниципальный округ Хорошёво -Мнёвники."			
Изм.	Кол.уч.	Лист	№ док	Подп.	Дата	Светопрозрачные конструкции	Стадия	Лист	Листов
Разраб.	Бирюкова				06.23		Р	67	
Проверил									
Н. контр.									
Т. контр.						Витраж В14		ООО "МАРКА ПОЛА"	
Утв.									


Копировал

Согласовано	ГАП	
	ГИП	
Инв. N подл.	Подп. и дата	Взам. инв. N

Угловой витраж В-15 (развертка).

Кол-во : 18 шт.

S=12,23 м.кв.

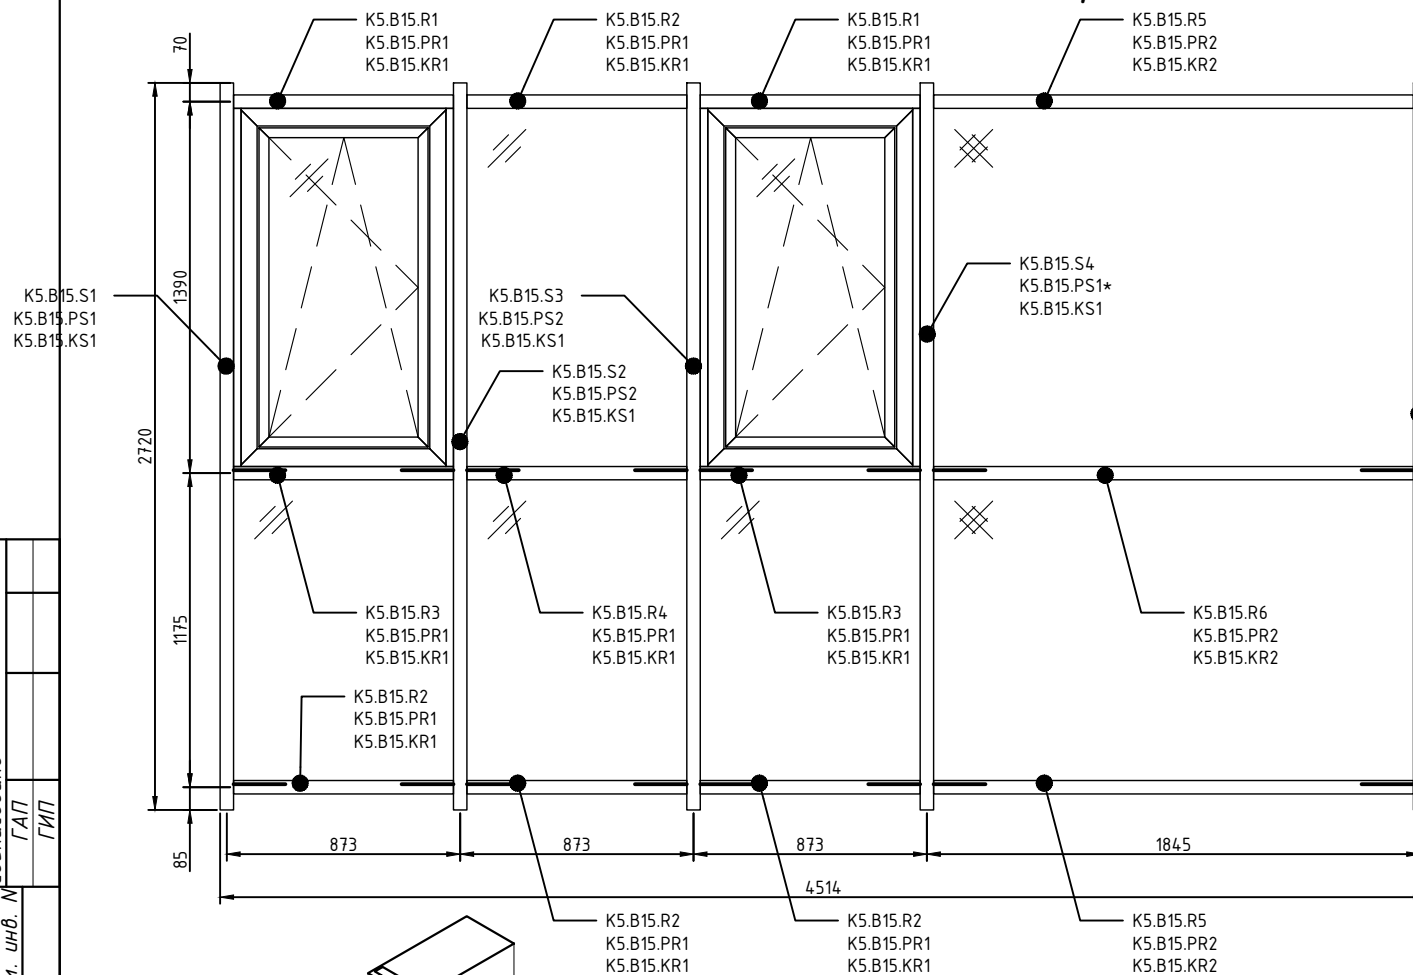


Заполнение термовставки - 0809892 + 0809893.

Под прижимы бутиловая лента - 0849711.

Прижимной саморез:


- прижимы PS1, PS2, PS1* - Ø6,3x67мм - 0535476
- прижимы PS3, PR1, PR2 - Ø6,3x64мм - 0535475

Ригеля крепить саморезом Ø4,2x12,7мм - 0525317

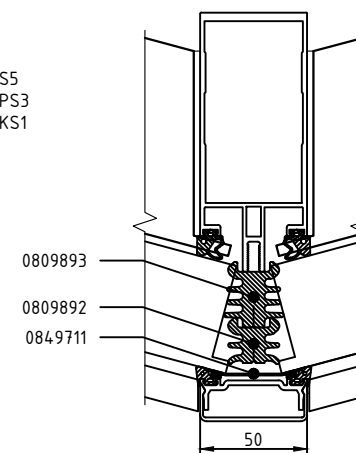

Стойка K5.B15.S4 устанавливается со стоечным сухарем 0345593 во всю длину.

Согласовано	ГАП	ГИП
Инв. № подл.	Подп. и дата	Взам. инв. №

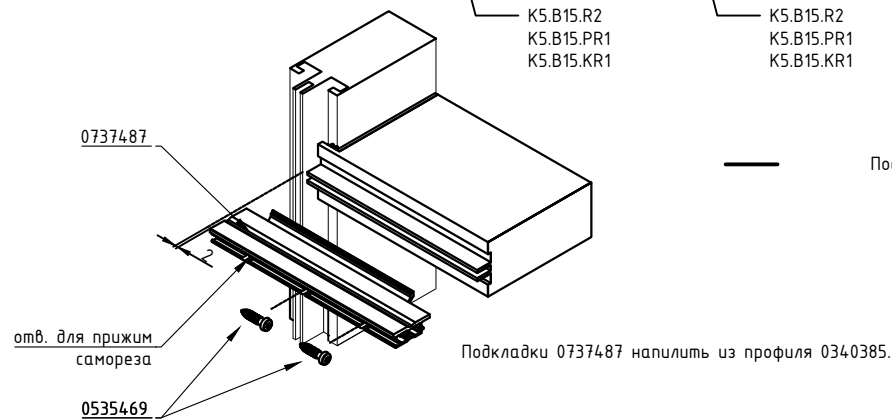

Подкладка 0737487

						Остров 2 К1			
						" Многофункциональная комплексная жилая застройка , квартал 2, корпус 1, 2, 3, 4, 5, 6 по адресу : г . Москва , внутригородская территория муниципальный округ Хорошёво -Мнёвники."			
Изм.	Кол.уч.	Лист	№ док.	Подп.	Дата	Светопрозрачные конструкции	Стадия	Лист	Листов
Разраб.	Бирюкова				06.23		Р	68	
Проверил									
Н.контр.									
Т.контр.						Витраж В15			
Утв.						ООО "МАРКА ПОЛА"			



Копировал

Маркировка:
К5.В1.С1 – 1 шт.
К5.В8.С1 – 1 шт.
К5.В6.С5 – 1шт (зеркально)
Цвет: 79 7М15

Маркировка:
К5.В1.С2 – 1 шт.
К5.В1.С3 – 1шт (зеркально)
К5.В6.С3 – 1 шт.
К5.В6.С4 – 1шт (зеркально)
К5.В8.С2 – 1 шт.
К5.В8.С3 – 1шт (зеркально)
Цвет: 79 7М15

Маркировка:
К5.В1.С4 – 1 шт.
К5.В8.С4 – 1 шт.
К5.В6.С2 – 1шт (зеркально)
Цвет: 79 7М15

Маркировка:
К5.В1.С5 – 1 шт.
К5.В8.С5 – 1 шт.
К5.В6.С1 – 1шт (зеркально)
Цвет: 79 7М15

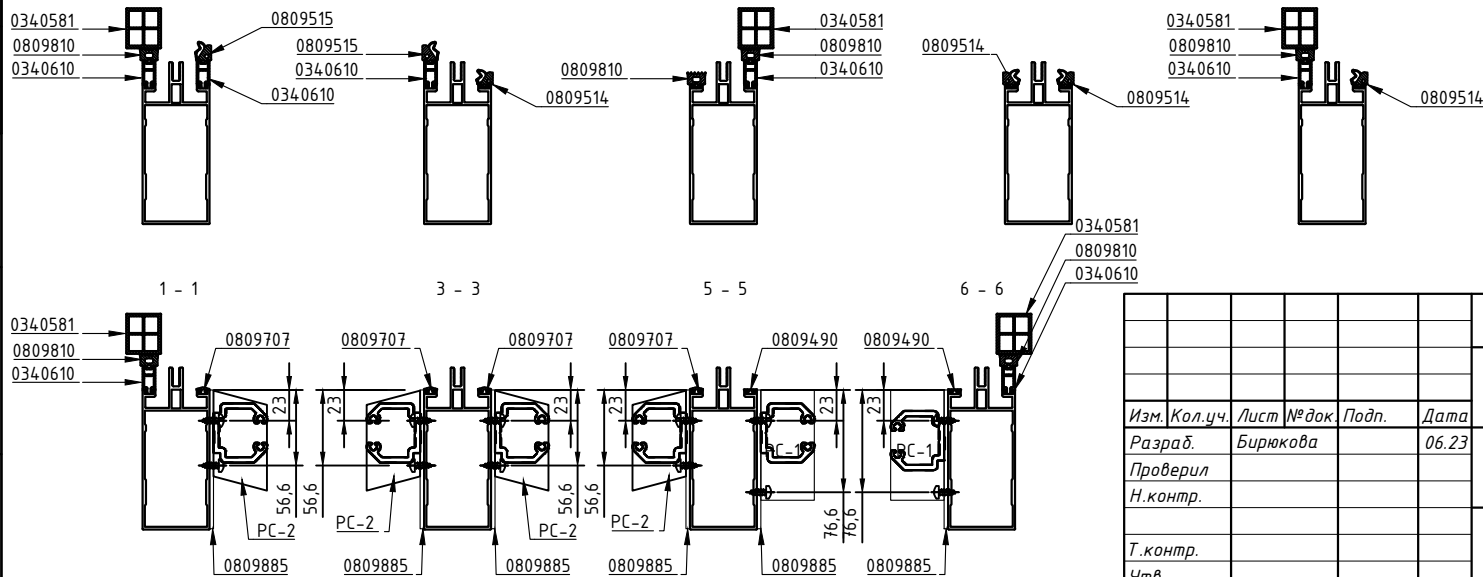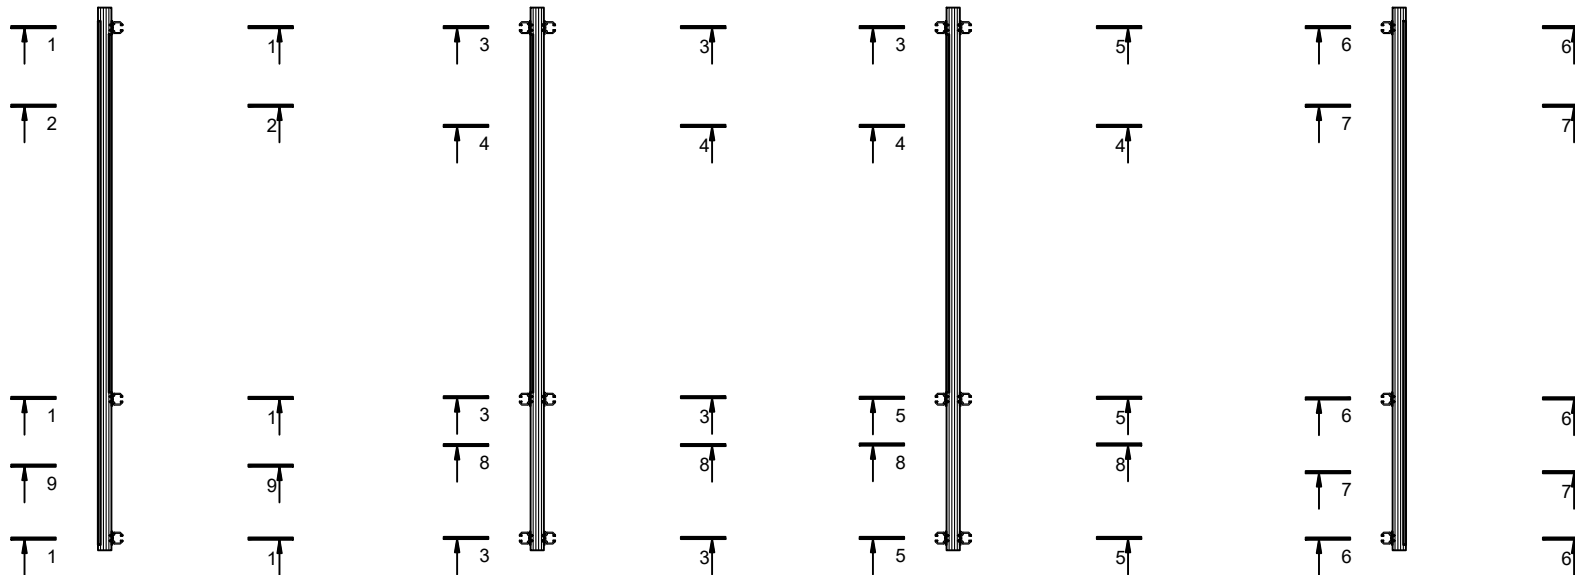

Примечание.

1. Каждую стойку перед производством работ оклеить защитной пленкой, замаркировать номером стойки и укомплектовать уплотнителями и филлистрами
2. Стойки укомплектовать подпятниками из 034.5593 L=150 мм и дренажным лотком 073.8263.04 на винт 050.5029.--
3. Манжету 080.9885 и сухарь РС-2 установить на производстве по шаблону. Манжету подрезать по торцу ригеля.
4. Ригельные сухари РС-1 и РС-2 устанавливать на саморез Ø4,8x13 – 0525330.

Остров 2 К1

“ Многофункциональная комплексная жилая застройка , квартал 2, корпус 1, 2, 3, 4, 5, 6 по адресу : г . Москва , внутригородская территория муниципальный округ Хорошёво –Мнёвники.”


Изм.	Кол.уч.	Лист	№ док.	Подп.	Дата			
Разраб.	Бирюкова	06.23						
Проверил								
Н. контр.								
Т. контр.								
Утв.								
						Стойки В1, В6, В8	Р	69
							000 “МАРКА ПОЛА”	

Копировал

Согласовано			Взам. инв. М	
	ГАП	ГИП		
Инв. М подл.	Подп. и дата			


Маркировка:
K5.B12.S1 - 18 шт.
K5.B13.S5 - 18шт (зеркально)
K5.B14.S1 - 18 шт.
K5.B15.S5 - 18шт (зеркально)

Цвет: 79 7M15

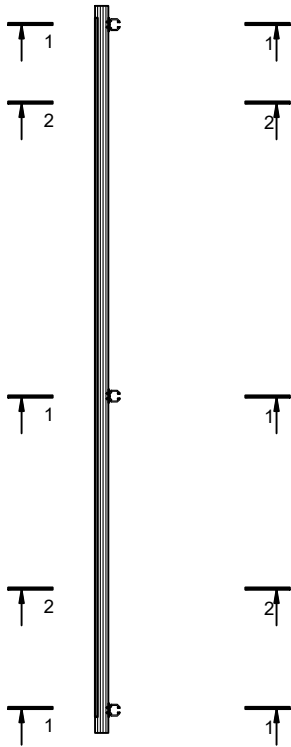


Маркировка:
K5.B12.S2 - 18 шт.
K5.B13.S4 - 18шт (зеркально)
K5.B14.S2 - 18 шт.
K5.B15.S4 - 18шт (зеркально)

Цвет: 79 7M15


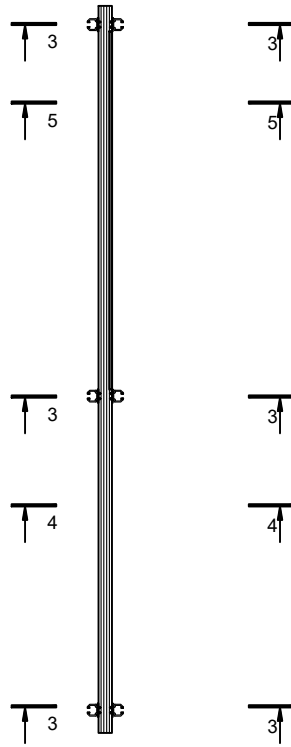


Примечание.


1. Каждую стойку перед производством работ оклеить защитной пленкой, замаркировать номером стойки и укомплектовать уплотнителями и филлистрами
2. Стойки укомплектовать подпятниками из 034.5593 L=150 мм и дренажным лотком 073.8263.04 на винт 050.5029.--
3. Манжету 080.9885 и сухарь РС-2 установить на производстве по шаблону. Манжету подрезать по торцу ригеля.
4. Ригельные сухари РС-1 и РС-2 устанавливать на саморез Ø4,8x13 - 0525330.

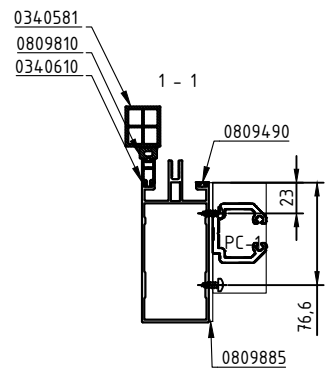


5 - 5

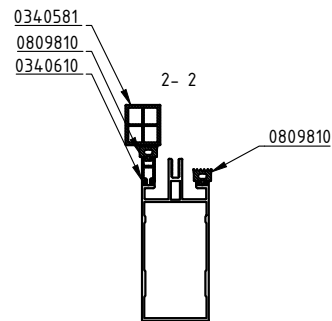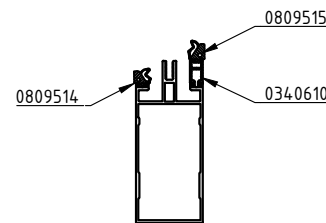

3 - 3

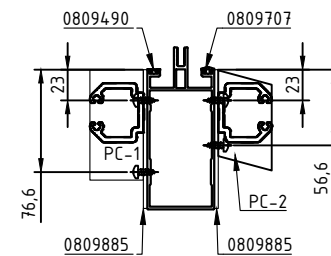







4 - 4

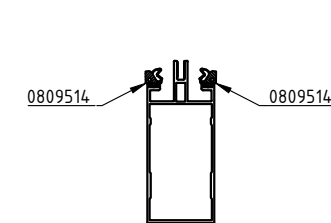

Остров 2 К1						
" Многофункциональная комплексная жилая застройка , квартал 2, корпус 1, 2, 3, 4, 5, 6 по адресу : г . Москва , внутригородская территория муниципальный округ Хорошёво -Мнёвники."						
Изм.	Кол.уч.	Лист	№ док.	Подп.	Дата	
Разраб.	Бирюкова				06.23	
Проверил						
Н. контр.						
Т. контр.						
Утв.						
Светопрозрачные конструкции						Стадия
						Р
						Лист
						70
						Листов
Стойки B12, B13, B14, B15						ООО "МАРКА ПОЛА"


Копировал

Инв. N подл.	Подп. и дата	Взам. инв. N	Согласовано	
			ГАП	ГИП

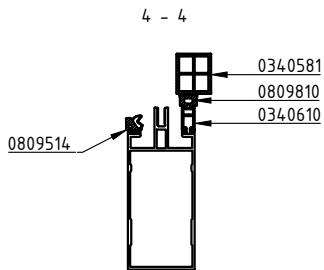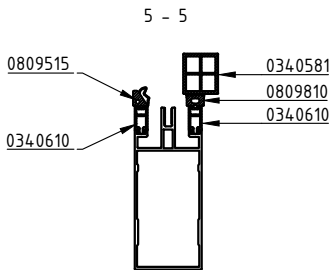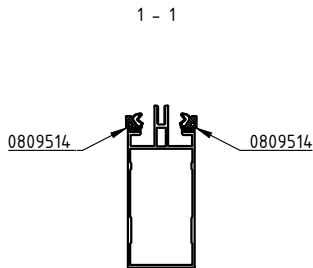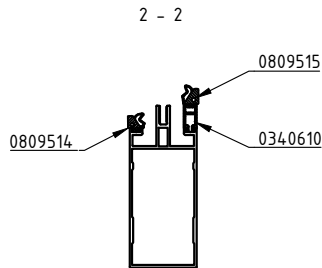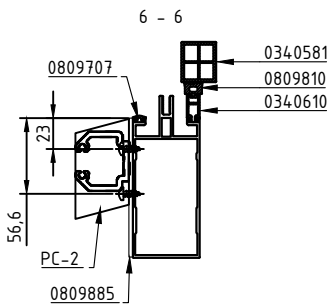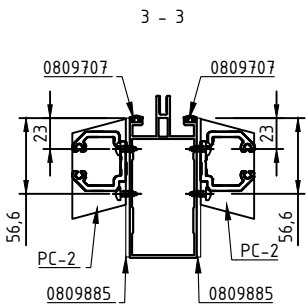


Маркировка:
 К5.В12.С3 – 18 шт.
 К5.В12.С4 – 18шт (зеркально)
 К5.В13.С2 – 18 шт.
 К5.В13.С3 – 18шт (зеркально)
 К5.В14.С3 – 18 шт.
 К5.В14.С4 – 18шт (зеркально)
 К5.В15.С2 – 18 шт.
 К5.В15.С3 – 18шт (зеркально)

Цвет: 79 7М15

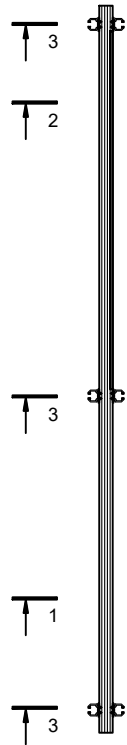

Маркировка:
 К5.В12.С5 – 18 шт.
 К5.В13.С1 – 18шт (зеркально)
 К5.В14.С5 – 18 шт.
 К5.В15.С1 – 18шт (зеркально)

Цвет: 79 7М15

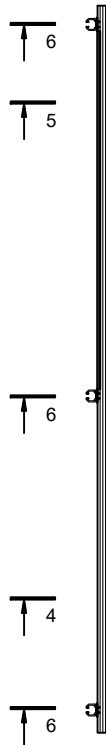



Примечание.

1. Каждую стойку перед производством работ оклеить защитной пленкой,замаркировать номером стойки и укомплектовать уплотнителями и филлистрами
2. Стойки укомплектовать подпятниками из 034.5593 L=150 мм и дренажным лотком 073.8263.04 на винт 050.5029.--
3. Манжету 080.9885 и сухарь PC-2 установить на производстве по шаблону. Манжету подрезать по торцу ригеля.
4. Ригельные сухари PC-1 и PC-2 устанавливать на саморез Ø4,8x13 – 0525330.


						Остров 2 К1		
						" Многофункциональная комплексная жилая застройка , квартал 2, корпус 1, 2, 3, 4, 5, 6 по адресу : г . Москва , внутригородская территория муниципальный округ Хорошёво –Мнёвники."		
Изм.	Кол.уч.	Лист	№ док.	Подп.	Дата	Светопрозрачные конструкции	Стадия	Лист
Разраб.	Бирюкова				06.23		Р	71
Проверил								
Н.контр.						Стойки В12, В13, В14, В15	ООО "МАРКА ПОЛА"	
Т.контр.								
Утв.								

Копировал


Профиль рузеля 0343524
Цвет: 79 7M15

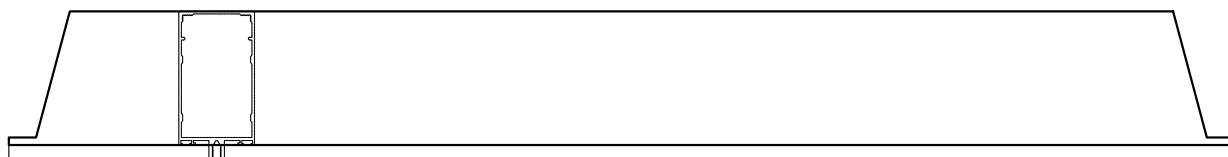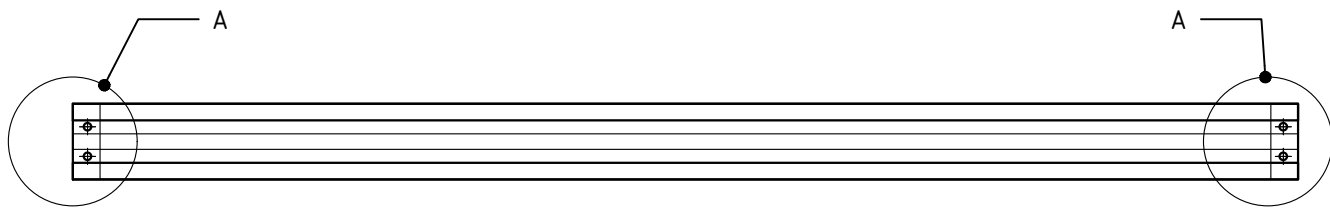

Маркировка		L, мм	Кол-во
K5.B1.R1		810,2	2
K5.B6.R1		810,2	2
K5.B8.R1		810,2	2
K5.B12.R1		810,2	36
K5.B13.R1		810,2	36
K5.B14.R1		810,2	36
K5.B15.R1		810,2	36

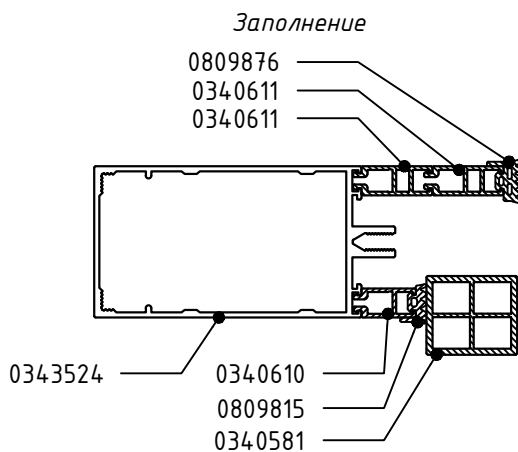

Οδρ. Α (2:1)

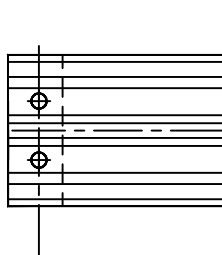


Примечание.

1. Каждый ригель перед производством работ оклеить защитной пленкой, замаркировать номером стойки и укомплектовать уплотнителями и флистами


						Остров 2 К1			
						" Многофункциональная комплексная жилая застройка , квартал 2, корпус 1, 2, 3, 4, 5, 6 по адресу : г . Москва , внутригородская территория муниципальный округ Хорошёво –Мнёвники."			
Изм.	Кол.уч.	Лист	№ док.	Подп.	Дата				
Разраб.		Бирюкова			06.23	Светопрозрачные конструкции	Стадия	Лист	Листов
Проверил							Р	72	
Н.контр.									
						Ризели	ООО "МАРКА ПОЛА"		
Т.контр.									
Утв.									

Копировал


Профиль рузеля 0343524
Цвет: 79 7M15

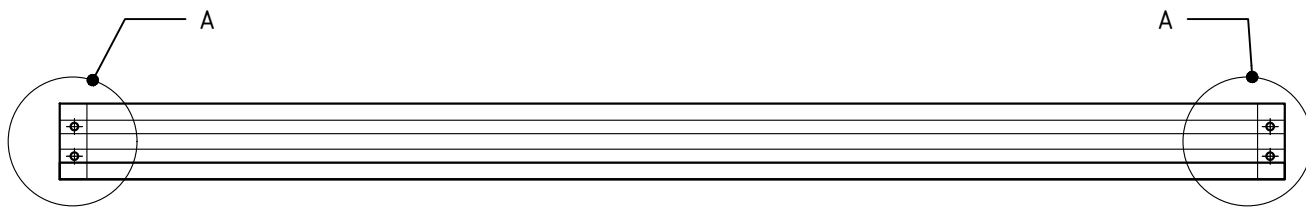

Маркировка		L, мм	Кол-во
K5.B1.R2		810,2	4
K5.B6.R2		810,2	4
K5.B8.R2		810,2	4
K5.B12.R2		810,2	72
K5.B13.R2		810,2	72
K5.B14.R2		810,2	72
K5.B15.R2		810,2	72

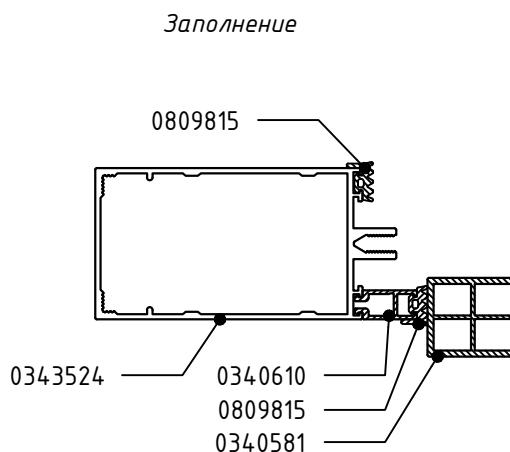

Οδρ. Α (2:1)

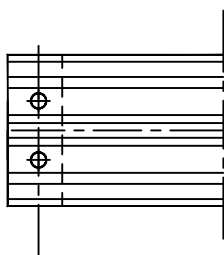



Примечание.

1. Каждый ригель перед производством работ оклеить защитной пленкой, замаркировать номером стойки и укомплектовать уплотнителями и флистами


						Остров 2 К1			
						" Многофункциональная комплексная жилая застройка , квартал 2, корпус 1, 2, 3, 4, 5, 6 по адресу : г . Москва , внутригородская территория муниципальный округ Хорошёво –Мнёвники."			
Изм.	Кол.уч.	Лист	№ док.	Подп.	Дата				
Разраб.		Бирюкова			06.23	Светопрозрачные конструкции	Стадия	Лист	Листов
Проверил							Р	73	
Н.контр.									
						Ризели	ООО "МАРКА ПОЛА"		
Т.контр.									
Утв.									

Копировал


Профиль ригеля 0343524
Цвет: 79 7M15

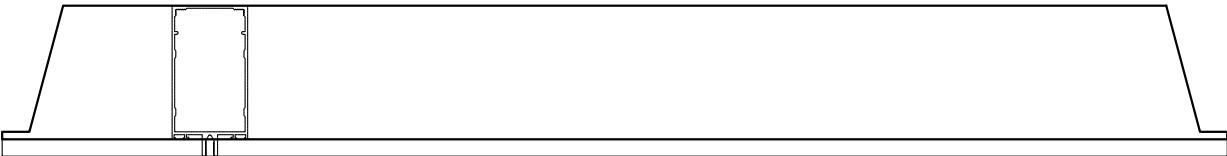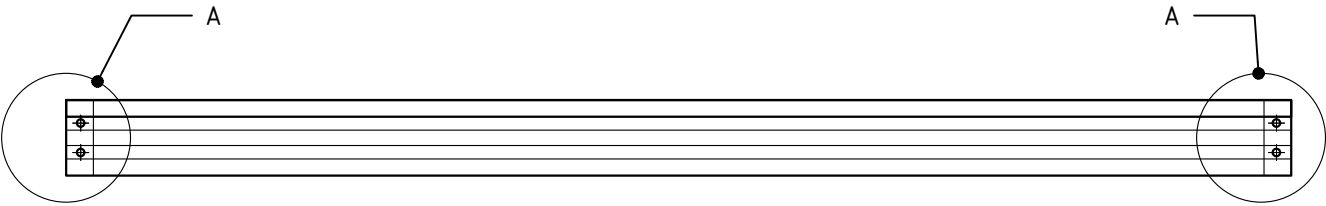

Маркировка		L, мм	Кол-во
K5.B1.R3		810,2	2
K5.B6.R3		810,2	2
K5.B8.R3		810,2	2
K5.B12.R3		810,2	36
K5.B13.R3		810,2	36
K5.B14.R3		810,2	36
K5.B15.R3		810,2	36

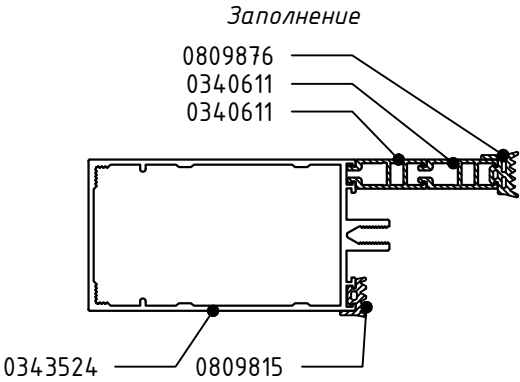

Одр. А (2:1)

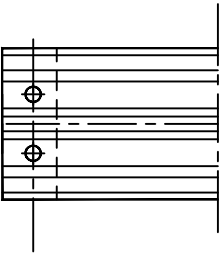

Примечание.
1. Каждый ригель перед производством работ оклеить защитной пленкой,замаркировать номером стойки и укомплектовать уплотнителями и флистрами

Согласовано

ГАП
ГИП


Взам. инв. №

Подп. и дата

Инв. № подл.


Изм.	Кол.уч.	Лист	№ док.	Подп.	Дата	Остров 2 К1			
Разраб.	Бирюкова				06.23	" Многофункциональная комплексная жилая застройка , квартал 2, корпус 1, 2, 3, 4, 5, 6 по адресу : г . Москва , внутригородская территория муниципальный округ Хорошёво –Мнёвники."			
Проверил						Светопрозрачные конструкции	Стадия	Лист	Листов
Н.контр.							Р	74	
Т.контр.						Ригели	ООО "МАРКА ПОЛА"		
Утв.									

Профиль ригеля 0343524
Цвет: 79 7M15

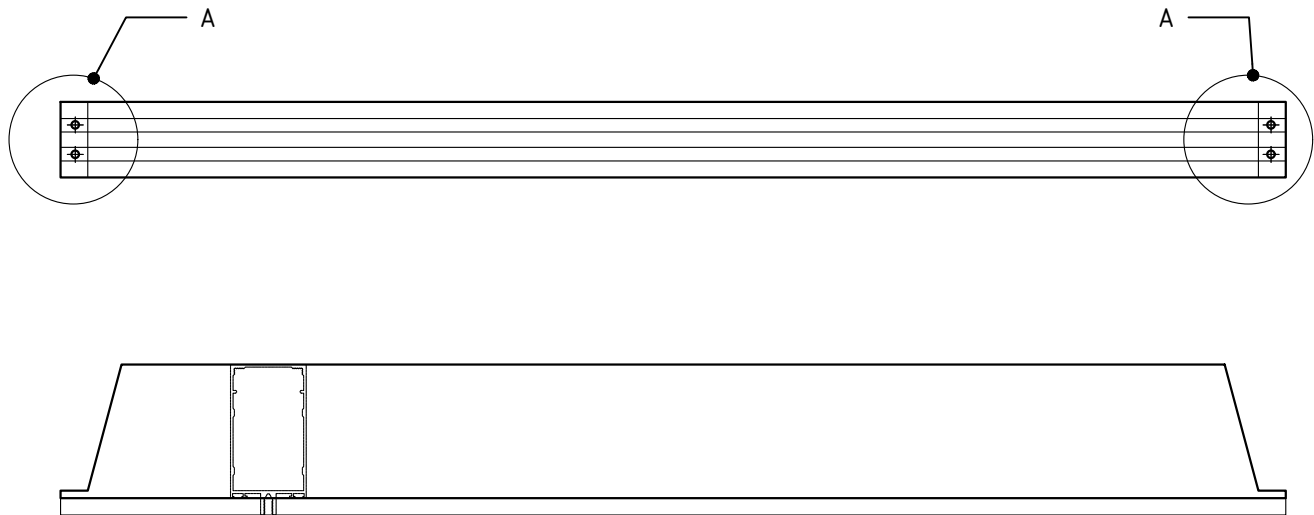


Заполнение

Маркировка		L, мм	Кол-во
K5.B1.R4		810,2	1
K5.B6.R4		810,2	1
K5.B8.R4		810,2	1
K5.B12.R4		810,2	18
K5.B13.R4		810,2	18
K5.B14.R4		810,2	18
K5.B15.R4		810,2	18

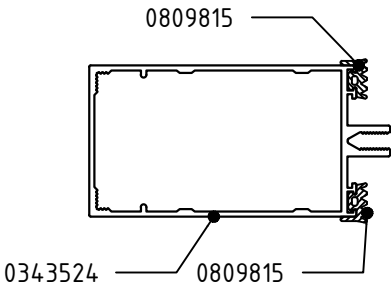

Обр. А (2:1)

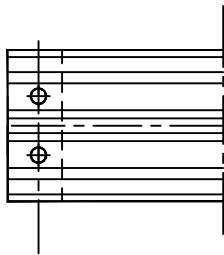


Примечание.
1. Каждый ригель перед производством работ оклеить защитной пленкой,замаркировать номером стойки и укомплектовать уплотнителями и филлистрами

Согласовано				
	ГАП	ГИП		
Взам. инв. N				
Подп. и дата				
Инв. N подл.				


						Остров 2 К1				
						“ Многофункциональная комплексная жилая застройка , квартал 2, корпус 1, 2, 3, 4, 5, 6 по адресу : г . Москва , внутригородская территория муниципальный округ Хорошёво –Мнёвники.”				
Изм.	Кол.уч.	Лист	№ док.	Подп.	Дата	Светопрозрачные конструкции		Стадия	Лист	Листов
Разраб.	Бирюкова				06.23			Р	75	
Проверил										
Н.контр.										
						Ригели		ООО “МАРКА ПОЛА”		
Т.контр.										
Утв.										

Профиль ригеля 0343525
Цвет: 79 7M15

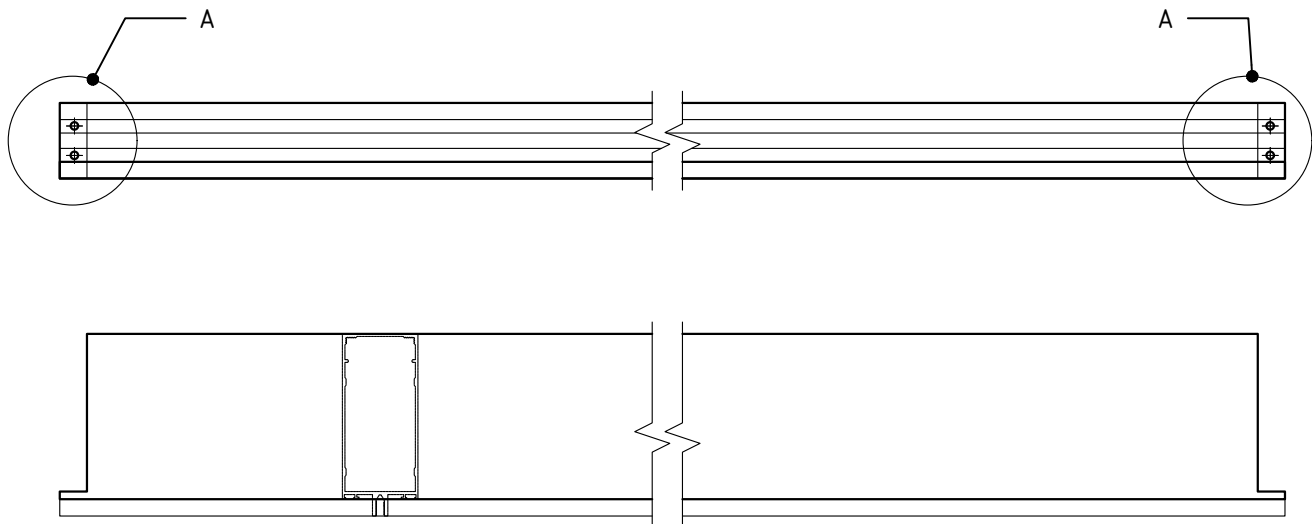


Заполнение

Маркировка		L, мм	Кол-во
K5.B1.R5		1060,0	2
K5.B6.R5		1780,0	2
K5.B8.R5		1825,0	2
K5.B12.R5		1780,0	36
K5.B13.R5		1060,0	36
K5.B14.R5		1000,0	36
K5.B15.R5		1825,0	36

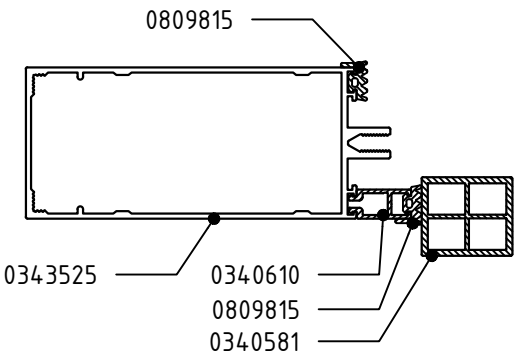

Обр. А (2:1)

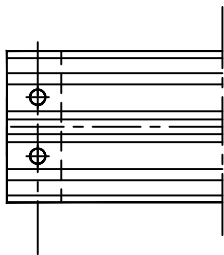


Примечание.
1. Каждый ригель перед производством работ оклеить защитной пленкой, замаркировать номером стойки и укомплектовать уплотнителями и филлистрами

Согласовано	Взам. инв. №		Инв. № подл.	Подп. и дата
	ГАП			
	ГИП			


Остров 2 К1						
" Многофункциональная комплексная жилая застройка , квартал 2, корпус 1, 2, 3, 4, 5, 6 по адресу : г . Москва , внутригородская территория муниципальный округ Хорошёво –Мнёвники."						
Светопрозрачные конструкции			Стадия	Лист	Листов	
Ригели			Р	76	000 "МАРКА ПОЛА"	

Профиль ружья 0343525
Цвет: 79 7M15

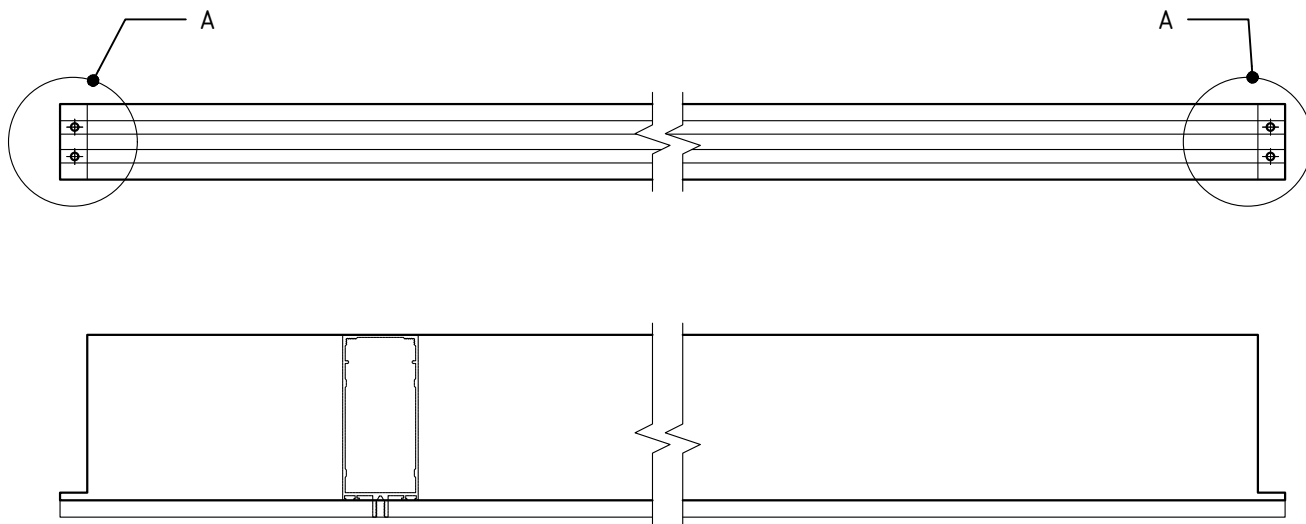


Заполнение

Маркировка	L, мм	Кол-во
K5.B1.R6	1060,0	1
K5.B6.R6	1780,0	1
K5.B8.R6	1825,0	1
K5.B12.R6	1780,0	18
K5.B13.R6	1060,0	18
K5.B14.R6	1000,0	18
K5.B15.R6	1825,0	18

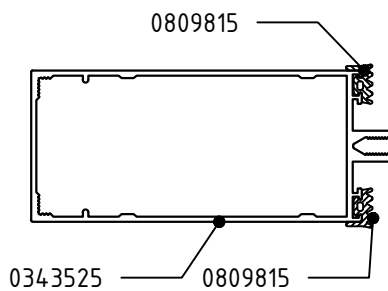

Οδρ. Α (2:1)

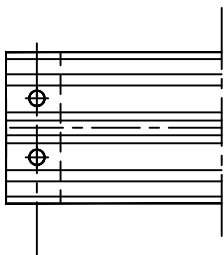





Примечание.

1. Каждый ригель перед производством работ оклеить защитной пленкой, замаркировать номером стойки и укомплектовать уплотнителями и флистами

						Остров 2 К1			
						" Многофункциональная комплексная жилая застройка , квартал 2, корпус 1, 2, 3, 4, 5, 6 по адресу : г . Москва , внутригородская территория муниципальный округ Хорошёво –Мнёвники."			
Изм.	Кол.уч.	Лист	№ док.	Подп.	Дата				
Разраб.	Бирюкова				06.23	Светопрозрачные конструкции	Стадия	Лист	Листов
Проверил							Р	77	
Н.контр.									
Т.контр.						Ризели	ООО "МАРКА ПОЛА"		
Утв.									

Копировал


Прижимная планка стойки
Цвет: без покраски

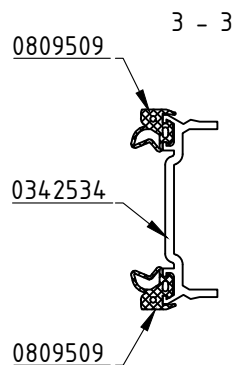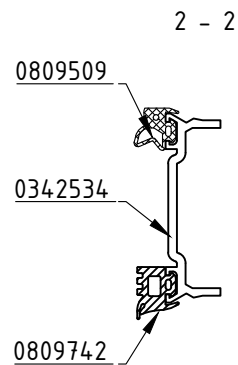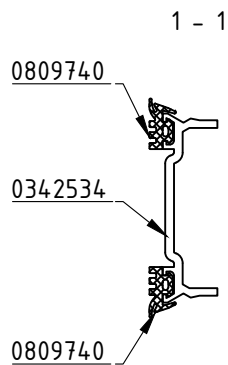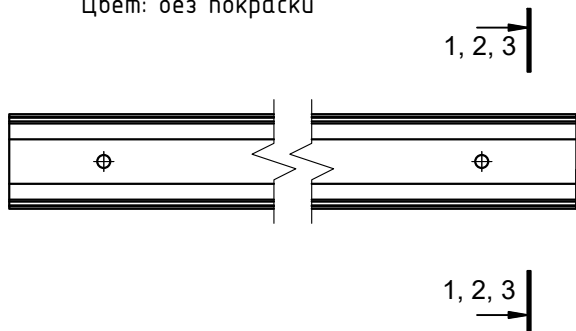


Маркировка	№ Сечения	L, мм	Кол-во
K5.B1.PS1	2 - 2	1960,0	2
K5.B1.PS2	3 - 3	1960,0	2
K5.B1.PS3	1 - 1	1960,0	1
K5.B6.PS1	2 - 2	1960,0	2
K5.B6.PS2	3 - 3	1960,0	2
K5.B6.PS3	1 - 1	1960,0	1
K5.B8.PS1	2 - 2	1960,0	2
K5.B8.PS2	3 - 3	1960,0	2
K5.B8.PS3	1 - 1	1960,0	1
K5.B12.PS1	2 - 2	2615,0	36
K5.B12.PS2	3 - 3	2615,0	36
K5.B12.PS3	1 - 1	2615,0	18
K5.B13.PS1	2 - 2	2615,0	36
K5.B13.PS2	3 - 3	2615,0	36
K5.B13.PS3	1 - 1	2615,0	18
K5.B14.PS1	2 - 2	2615,0	36
K5.B14.PS2	3 - 3	2615,0	36
K5.B14.PS3	1 - 1	2615,0	18

Маркировка	№ Сечения	L, мм	Кол-во
K5.B15.PS1	2 - 2	2615,0	36
K5.B15.PS2	3 - 3	2615,0	36
K5.B15.PS3	1 - 1	2615,0	18

Крышка стойки
Цвет: 79 9M05

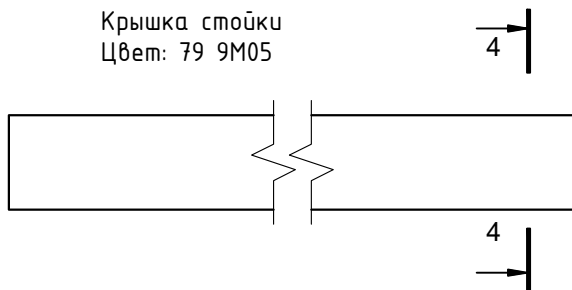

4 - 4

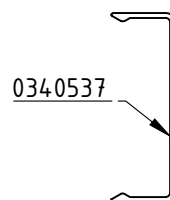

Маркировка	L, мм	Кол-во
K5.B1.KS1	1960,0	5
K5.B6.KS1	1960,0	5
K5.B8.KS1	1960,0	5
K5.B12.KS1	2615,0	90
K5.B13.KS1	2615,0	90
K5.B14.KS1	2615,0	90
K5.B15.KS1	2615,0	90

Согласовано			
	ГАП		
Взам. инв. №			
	ГИП		
Подп. и дата			
Инв. № подл.	Изм.	Кол.уч.	Лист
	Разраб.	Бирюкова	06.23
	Проверил		
	Н.контр.		
	Т.контр.		
Утв.			

Остров 2 К1

" Многофункциональная комплексная жилая застройка , квартал 2, корпус 1, 2, 3, 4, 5, 6 по адресу : г . Москва , внутригородская территория муниципальный округ Хорошёво -Мнёвники."


Светопрозрачные конструкции

Прижим и крышка стойки


Стадия Лист Листов
Р 78

ООО "МАРКА ПОЛА"

Прижимная планка ригеля
Цвет: без покраски

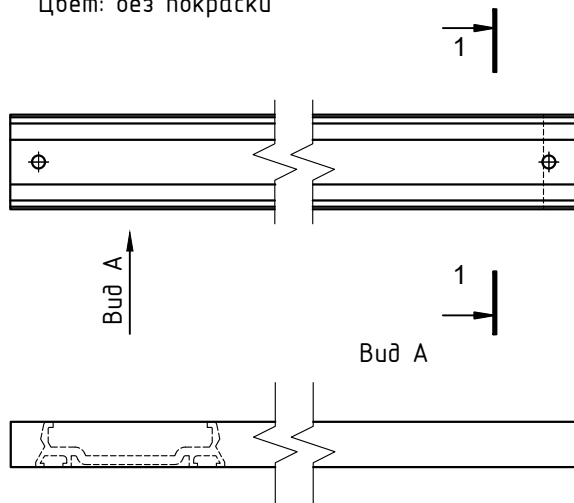


Крышка ригеля
Цвет: 79 9M05

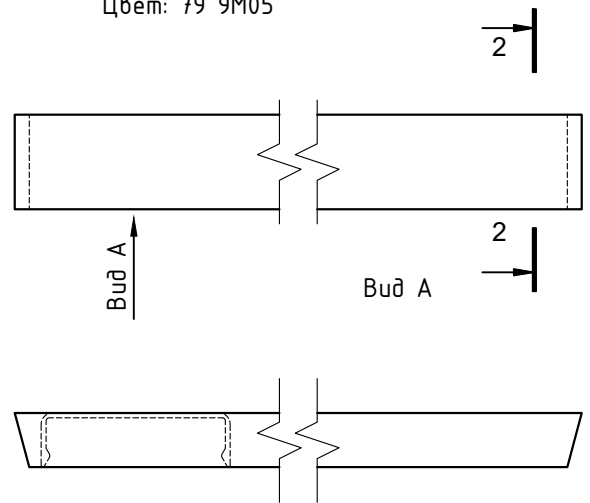

Маркировка		L, мм	Кол-во
K5.B1.PR1		810,0	9
K5.B1.PR2		1026,0	3
K5.B6.PR1		810,0	9
K5.B6.PR2		1746,0	3
K5.B8.PR1		810,0	9
K5.B8.PR2		1791,0	3
K5.B12.PR1		810,0	162
K5.B12.PR2		1746,0	54
K5.B13.PR1		810,0	162
K5.B13.PR2		1026,0	54
K5.B14.PR1		810,0	162
K5.B14.PR2		966,0	54
K5.B15.PR1		810,0	162
K5.B15.PR2		1791,0	54

Маркировка		L, мм	Кол-во
K5.B1.KR1		820,5	9
K5.B1.KR2	ПРЯМАЯ	1028,0	3
K5.B6.KR1		820,5	9
K5.B6.KR2	ПРЯМАЯ	1748,0	3
K5.B8.KR1		820,5	9
K5.B8.KR2	ПРЯМАЯ	1793,0	3
K5.B12.KR1		820,5	162
K5.B12.KR2	ПРЯМАЯ	1748,0	54
K5.B13.KR1		820,5	162
K5.B13.KR2	ПРЯМАЯ	1028,0	54
K5.B14.KR1		820,5	162
K5.B14.KR2	ПРЯМАЯ	968,0	54
K5.B15.KR1		820,5	162
K5.B15.KR2	ПРЯМАЯ	1793,0	54

! ---.---.KR2 прямые, без углов запила

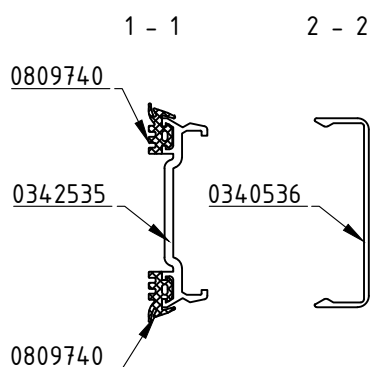


Согласовано	ГАП	Взам. инв. №	Подп. и дата	Инв. № подл.
	ГИП			

						Остров 2 К1				
						" Многофункциональная комплексная жилая застройка , квартал 2, корпус 1, 2, 3, 4, 5, 6 по адресу : г . Москва , внутригородская территория муниципальный округ Хорошёво –Мнёвники."				
Изм.	Кол.уч.	Лист	№ док.	Подп.	Дата					
Разраб.		Бирюкова			06.23	Светопрозрачные конструкции		Стадия	Лист	Листов
Проверил								Р	79	
Н.контр.										
						Прижим и крышка ригеля		ООО "МАРКА ПОЛА"		
Т.контр.										
Утв.										

Угловой витраж В-1.4 (развертка).


Кол-во : 18 шт.

S=11,33 м.кв.

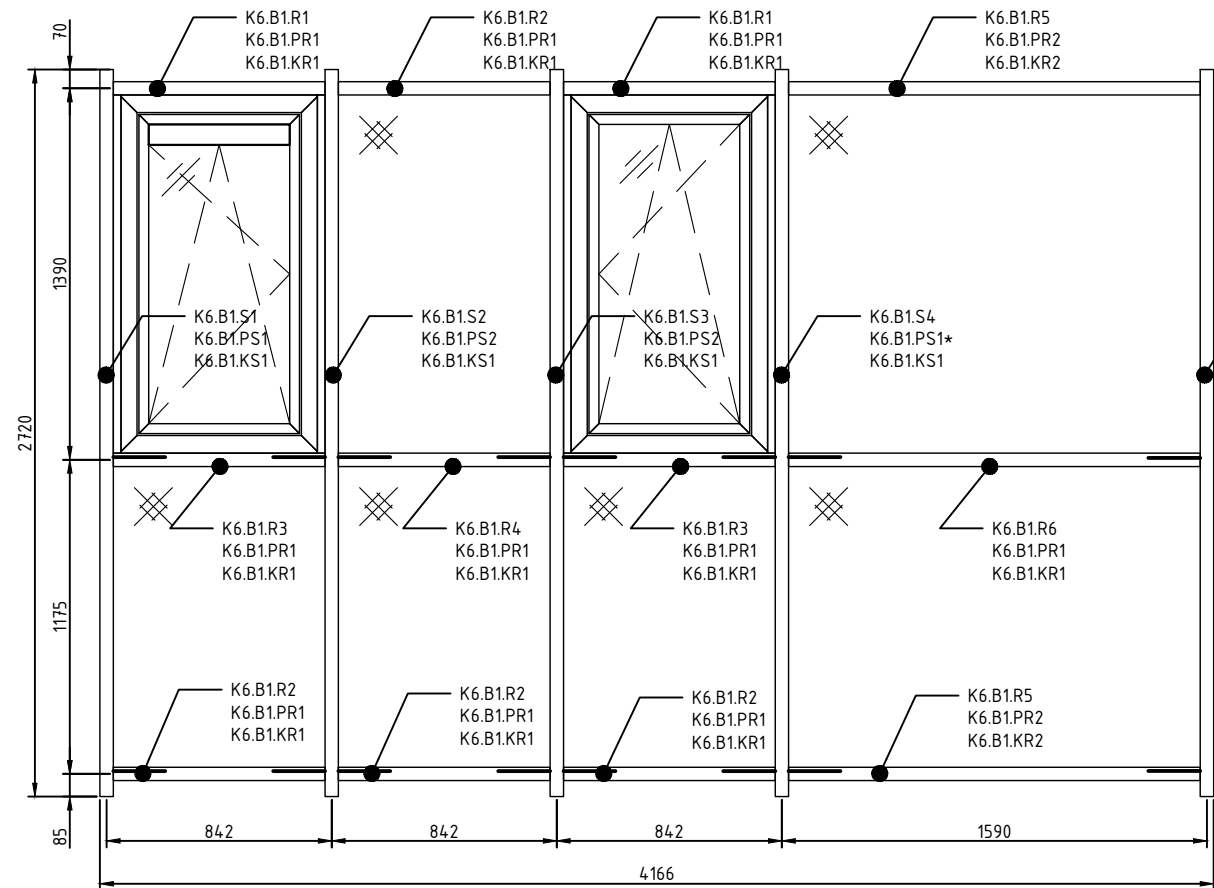


Заполнение термовставки - 0809892 + 0809893.
Под прижимы бутиловая лента - 0849711.
Прижимной саморез:
- прижимы PS1, PS2, PS1* - Ø6,3x67мм - 0535476
- прижимы PS3, PR1, PR2 - Ø6,3x64мм - 0535475

Ригеля крепить саморезом Ø4,2x12,7мм - 0525317

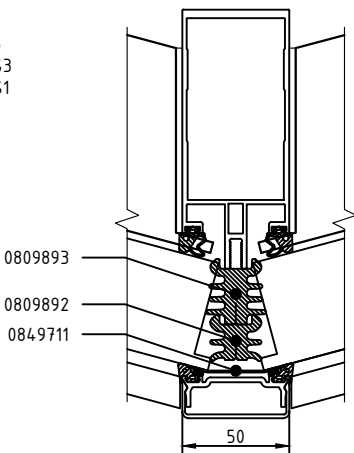

Стойка K6.B1.S4 устанавливается со стоечным сухарем 0345593 во всю длину.

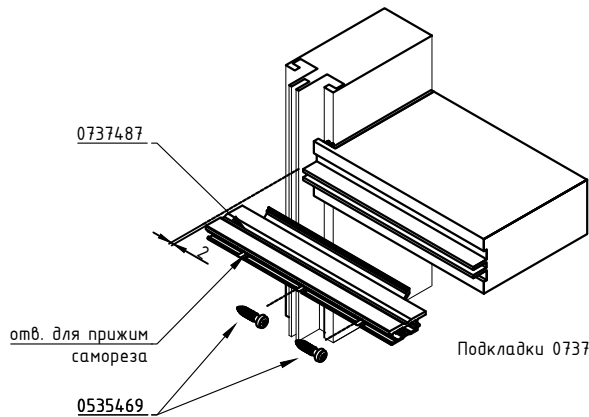

Подкладка 0737487

Подкладки 0737487 напилить из профиля 0340385.


						Остров 2 К1			
						" Многофункциональная комплексная жилая застройка , квартал 2, корпус 1, 2, 3, 4, 5, 6 по адресу : г . Москва , внутригородская территория муниципальный округ Хорошёво -Мнёвники."			
Изм.	Кол.уч.	Лист	№ док.	Подп.	Дата	Светопрозрачные конструкции	Стадия	Лист	Листов
Разраб.	Бирюкова				06.23		Р	80	
Проверил									
Н.контр.						Витраж В1.4	ООО "МАРКА ПОЛА"		
Т.контр.									
Утв.									

Копировал

Угловой витраж В-2.2 (развертка).

Кол-во: 18 шт.

S=11,06 м.кв.

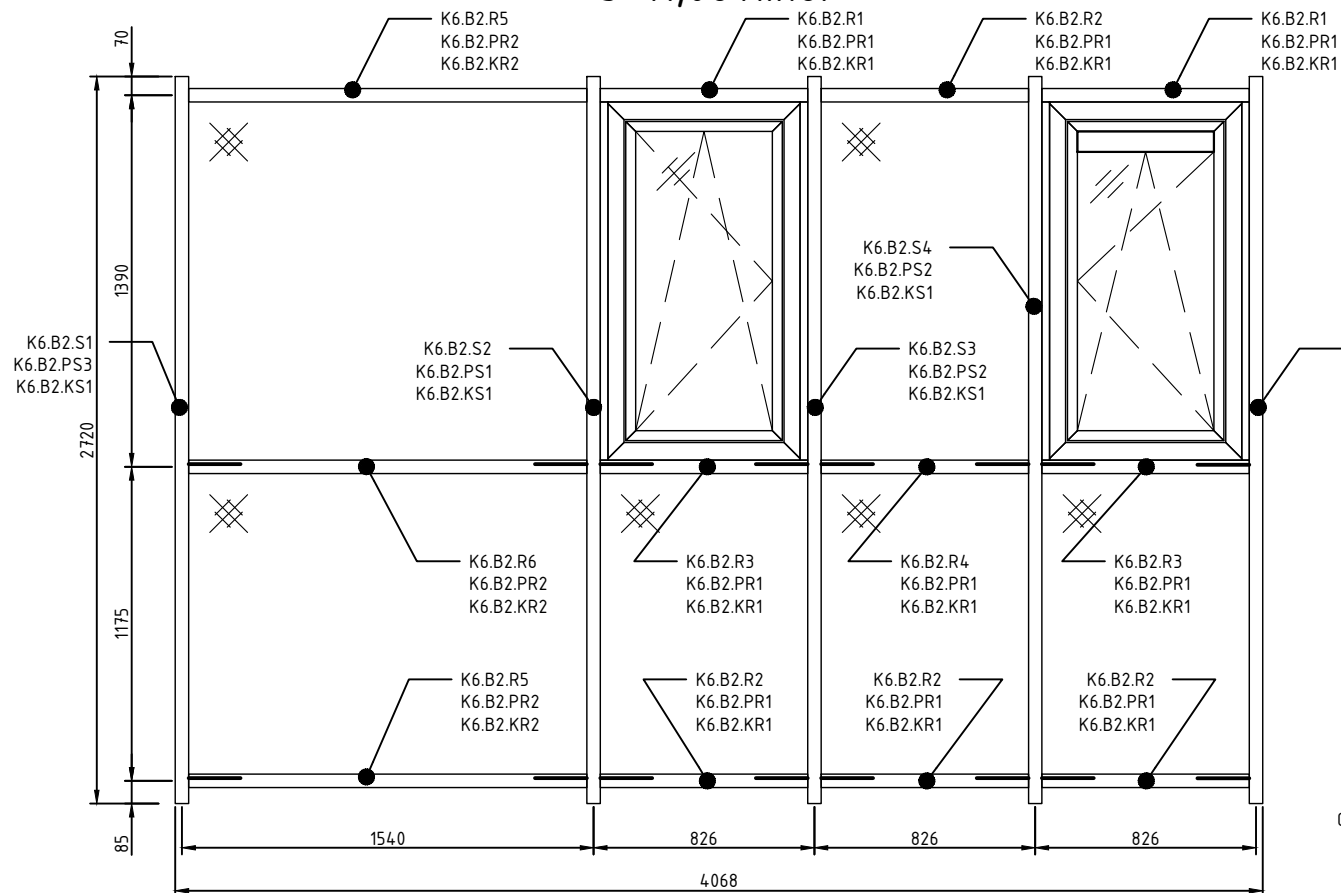


Заполнение термовставки - 0809892 + 0809893.

Под прижимы дутыловая лента - 0849711.


Прижимной саморез:

- прижимы PS1, PS2, PS1* - Ø6,3x67мм - 0535476
- прижимы PS3, PR1, PR2 - Ø6,3x64мм - 0535475

Резеля крепить саморезом Ø4,2x12,7мм - 0525317

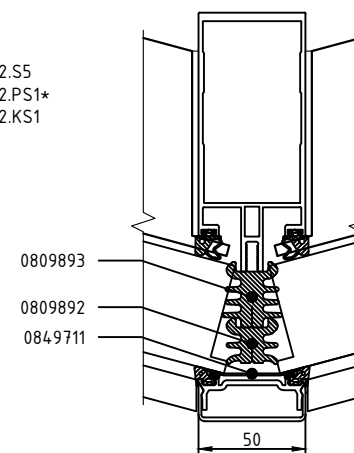

Стойка K6.B2.S2 устанавливается со стоечным сухарем 0345593 во всю длину.

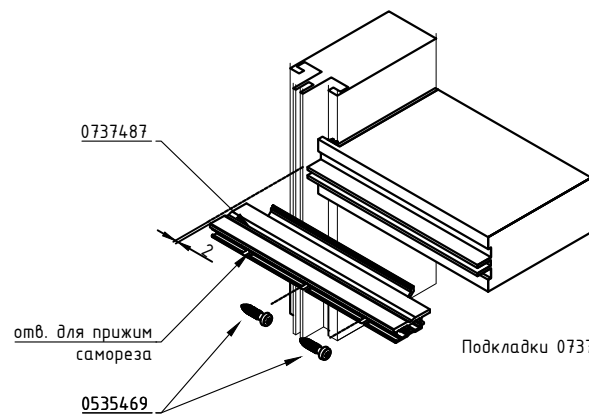

Подкладка 0737487



Подкладки 0737487 напилить из профиля 0340385.

						Остров 2 К1			
						" Многофункциональная комплексная жилая застройка , квартал 2, корпус 1, 2, 3, 4, 5, 6 по адресу : г . Москва , внутригородская территория муниципальный округ Хорошёво -Мнёвники."			
Изм.	Кол.уч.	Лист	№ док.	Подп.	Дата	Светопрзрачные конструкции	Стадия	Лист	Листов
Разраб.	Бирюкова				06.23		Р	81	
Проверил									
Н.контр.									
Т.контр.						Витраж В2.2		ООО "МАРКА ПОЛА"	
Утв.									

Копировал

Согласовано	ГАП	Взам. инв. №
	ГИП	
Инв. № подл.	Подп. и дата	Инв. №

$S=13,27 \text{ м.кВ.}$

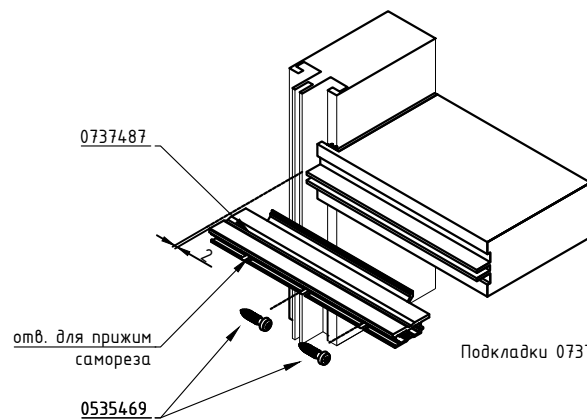 

Подкладки 0737487 напилить из профиля 0340385.

						Остров 2 К1				
						" Многофункциональная комплексная жилая застройка , квартал 2, корпус 1, 2, 3, 4, 5, 6 по адресу : г . Москва , внутригородская территория муниципальный округ Хорошёво -Мнѣвники."				
Изм.	Кол.уч.	Лист	№ док.	Подп.	Дата	Светопрозрачные конструкции		Стадия	Лист	Листов
Разраб.	Бирюкова				06.23			Р	82	
Проверил										
Н.контр.						Визраж Б5.2		ООО "МАРКА ПОЛА"		
Т.контр.										
Утв.										

Копировал

Согласовано

Взам. инв. №


Подп. и дата

Инв. N подл.

Угловой витраж В-16 (развертка).



Кол-во: 13 шт.

S=13,15 м.кв.

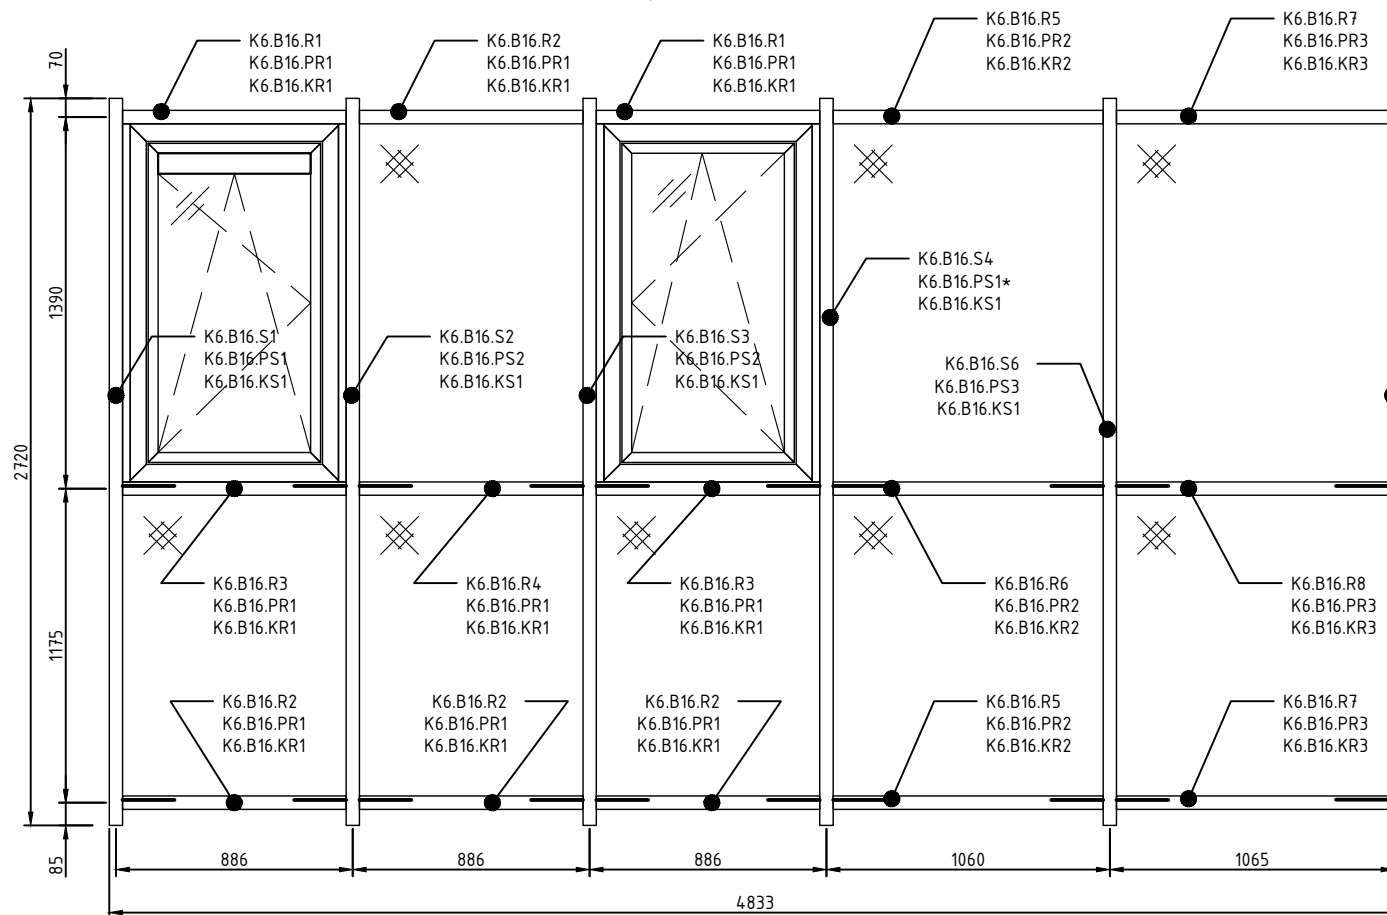

Заполнение термовставки - 0809892 + 0809893.
Под прижимы бутиловая лента - 0849711.
Прижимной саморез:
- прижимы PS1, PS2, PS1* - Ø6,3x67мм - 0535476
- прижимы PS3, PR1, PR2 - Ø6,3x64мм - 0535475

Резеля крепить саморезом Ø4,2x12,7мм - 0525317

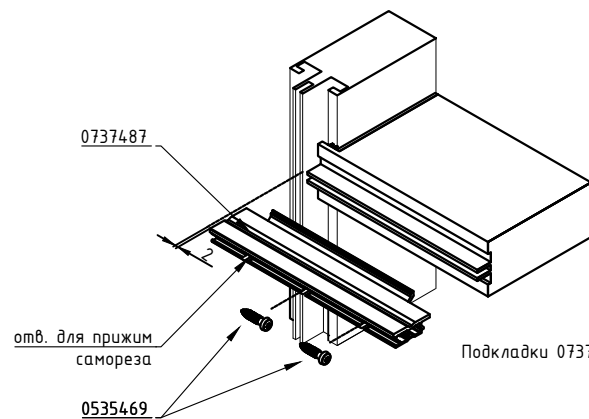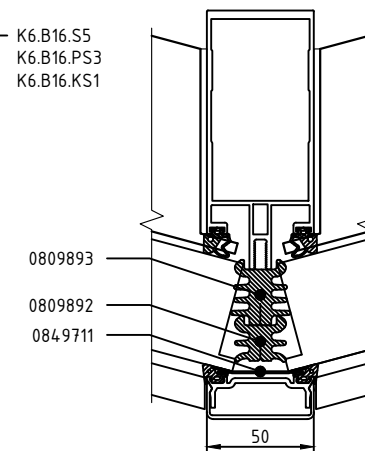

Подкладки 0737487 напилить из профиля 0340385.

Подкладка 0737487

						Остров 2 К1			
						" Многофункциональная комплексная жилая застройка , квартал 2, корпус 1, 2, 3, 4, 5, 6 по адресу : г . Москва , внутригородская территория муниципальный округ Хорошёво -Мнёвники."			
Изм.	Кол.уч.	Лист	№ док.	Подп.	Дата	Светопрозрачные конструкции	Стадия	Лист	Листов
Разраб.	Бирюкова				06.23		Р	83	
Проверил									
Н.контр.									
Т.контр.									
Утв.									
						Витраж В16		ООО "МАРКА ПОЛА"	

Копировал

Согласовано

ГАП

ГИП

Взам. инв. №


Подп. и дата

Инв. № подл.

Угловой витраж В-7.1 (развертка).


Кол-во: 1шт.

S=14,33 м.кв.

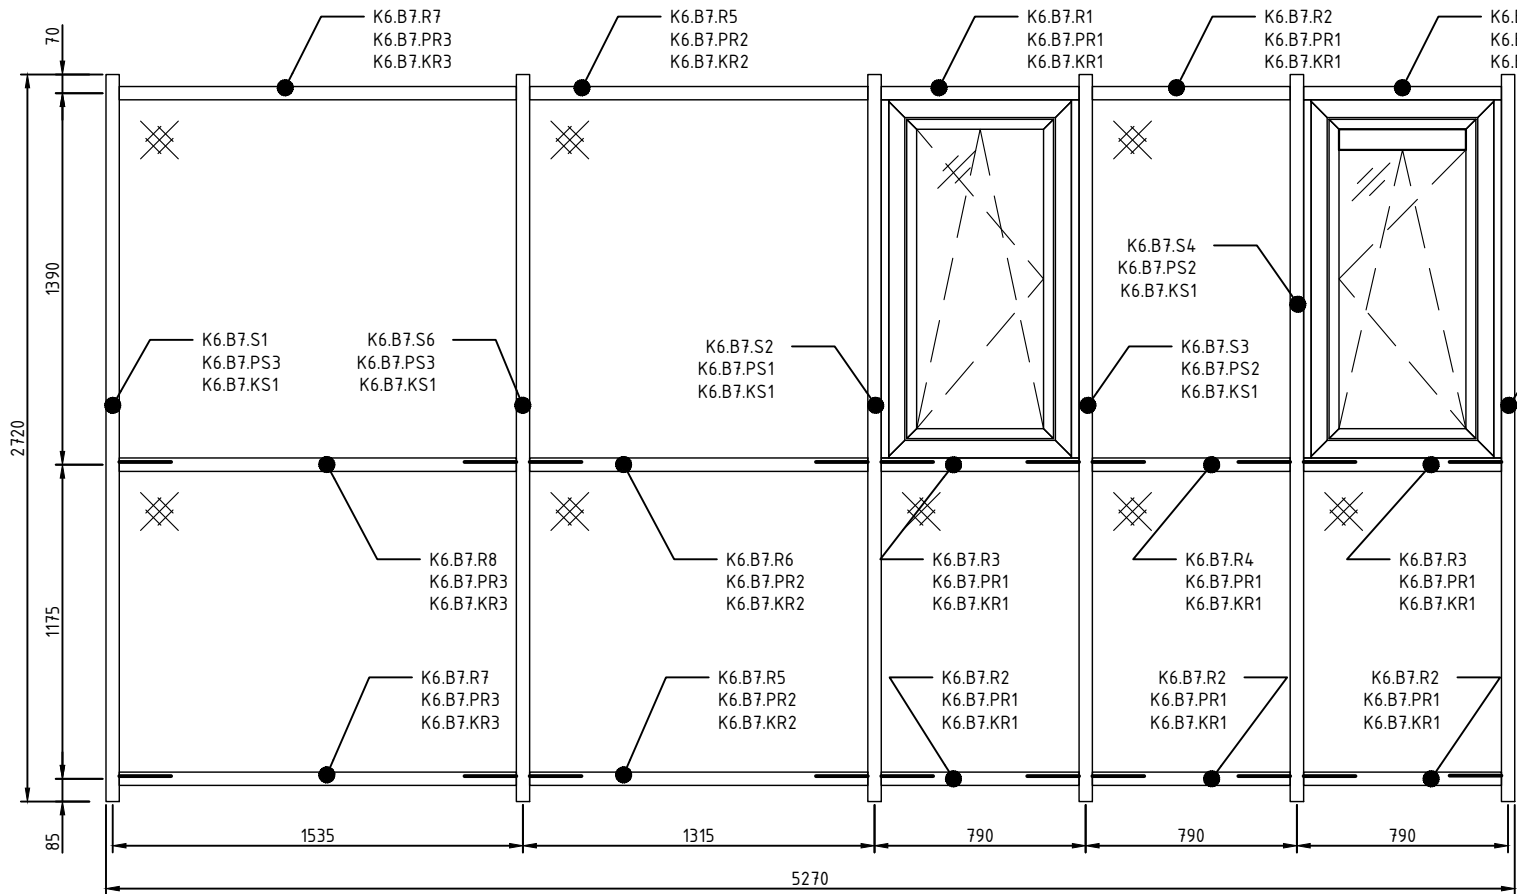


Заполнение термовставки - 0809892 + 0809893.
Под прижимы дутитовая лента - 0849711.
Прижимной саморез:
- прижимы PS1, PS2, PS1* - Ø6,3x67мм - 0535476
- прижимы PS3, PR1, PR2 - Ø6,3x64мм - 0535475

Ригеля крепить саморезом Ø4,2x12,7мм - 0525317

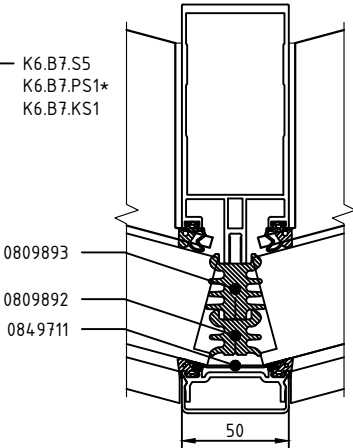

Стойка K6.B7.S2 и K6.B7.S6 устанавливается со стоечным сухарем 0345593 во всю длину.

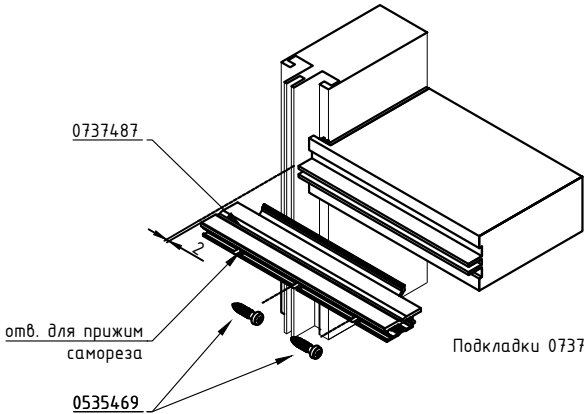

Подкладки 0737487 напилить из профиля 0340385.

Подкладка 0737487


						Остров 2 К1			
						" Многофункциональная комплексная жилая застройка , квартал 2, корпус 1, 2, 3, 4, 5, 6 по адресу : г . Москва , внутригородская территория муниципальный округ Хорошёво -Мнёвники."			
Изм.	Кол.уч.	Лист	№ док.	Подп.	Дата	Светопрозрачные конструкции	Стадия	Лист	Листов
Разраб.	Бирюкова				06.23		Р	84	
Проверил									
Н.контр.									
Т.контр.						Витраж В7.1		ООО "МАРКА ПОЛА"	
Утв.									

Копировал

Угловой витраж В-8.4 (развертка).


Кол-во: 1 шт.

S=11,55 м.кв.

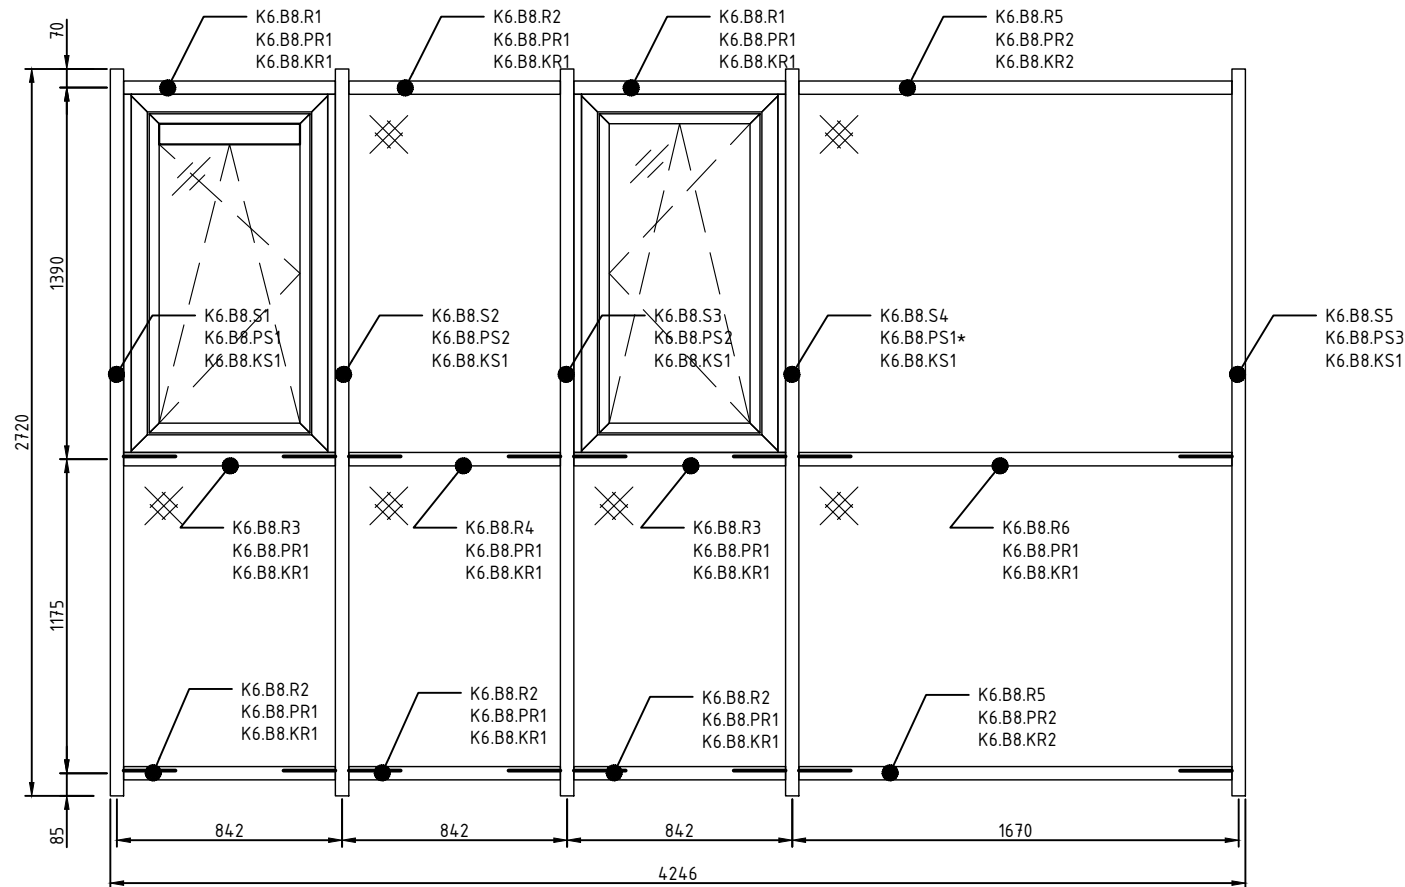


Заполнение термовставки - 0809892 + 0809893.
Под прижимы бутиловая лента - 0849711.
Прижимной саморез:
- прижимы PS1, PS2, PS1* - Ø6,3x67мм - 0535476
- прижимы PS3, PR1, PR2 - Ø6,3x64мм - 0535475

Ригеля крепить саморезом Ø4,2x12,7мм - 0525317

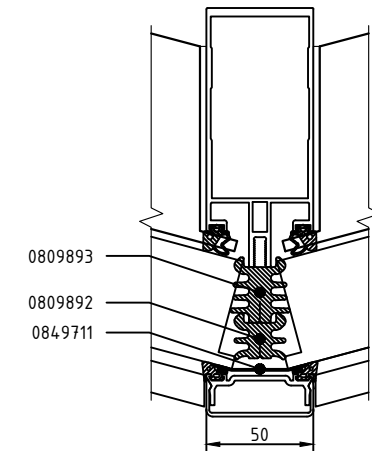

Стойка K6.B8.S4 устанавливается со стоечным сухарем 0345593 во всю длину.

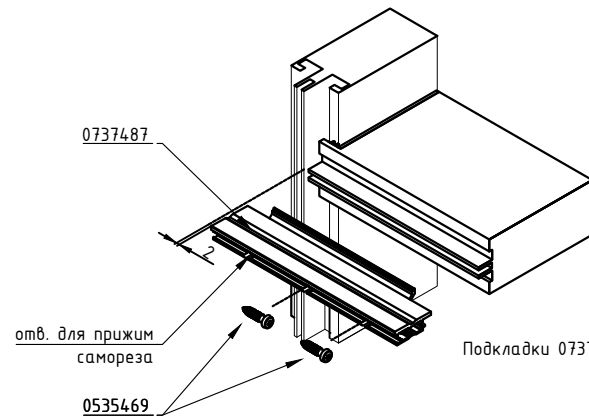

Подкладки 0737487 напилить из профиля 0340385.

Подкладка 0737487

						Остров 2 К1			
						" Многофункциональная комплексная жилая застройка , квартал 2, корпус 1, 2, 3, 4, 5, 6 по адресу : г . Москва , внутригородская территория муниципальный округ Хорошёво -Мнёвники."			
Изм.	Кол.уч.	Лист	№ док.	Подп.	Дата	Светопрозрачные конструкции	Стадия	Лист	Листов
Разраб.	Бирюкова				06.23		Р	85	
Проверил									
Н.контр.									
Т.контр.						Витраж В8.4		ООО "МАРКА ПОЛА"	
Утв.									

Копировал

Согласовано

ГАП

ГИП

Взам. инв. №


Подп. и дата

Инв. № подл.

Угловой витраж В-13.1 (развертка).


Кол-во: 1 шт.

S=11,49 м.кв.

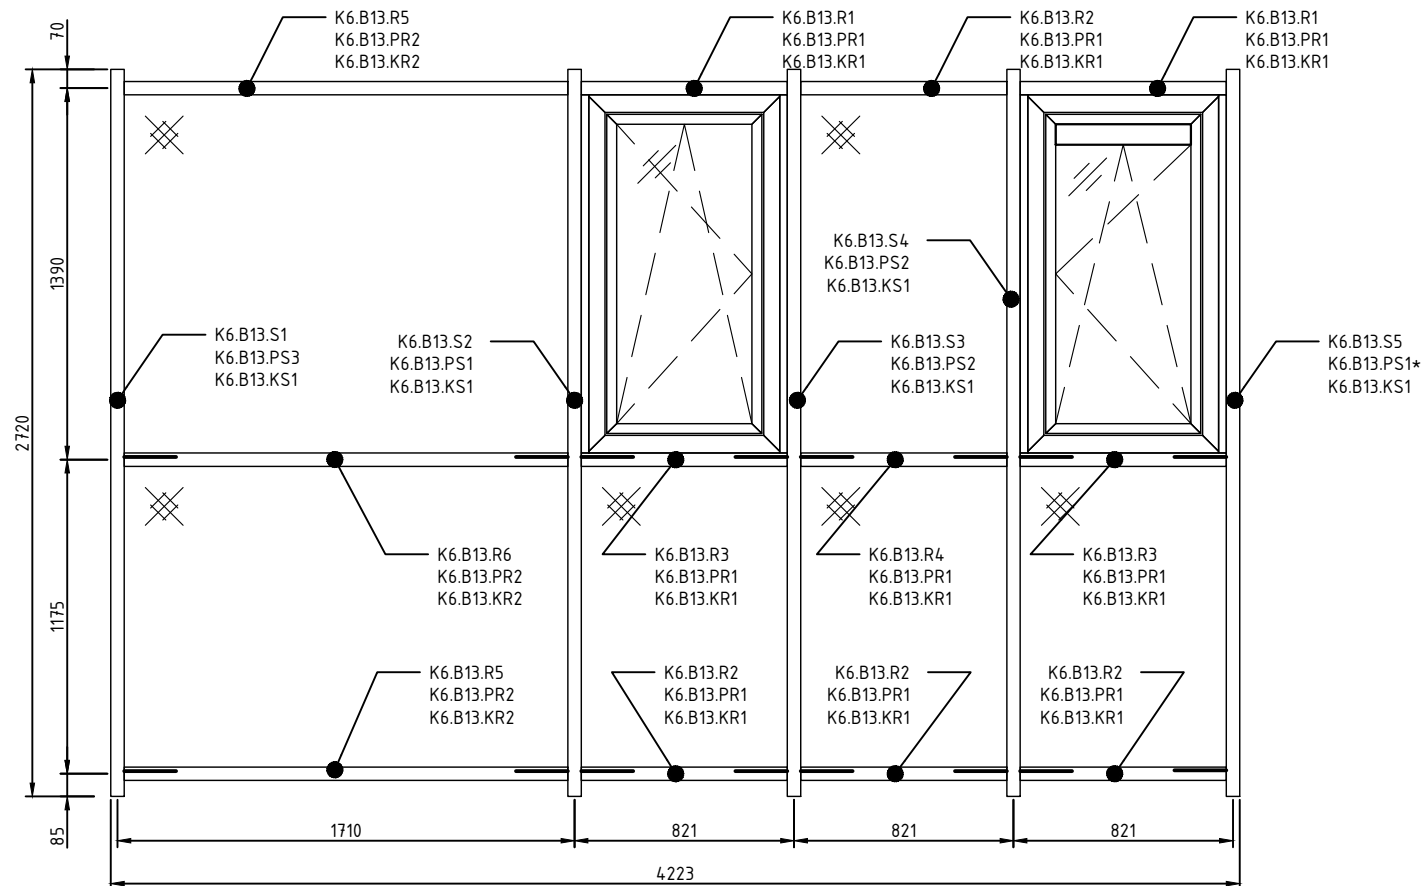


Заполнение термовставки - 0809892 + 0809893.
Под прижимы дутитовая лента - 0849711.
Прижимной саморез:
- прижимы PS1, PS2, PS1* - Ø6,3x67мм - 0535476
- прижимы PS3, PR1, PR2 - Ø6,3x64мм - 0535475

Ригеля крепить саморезом Ø4,2x12,7мм - 0525317

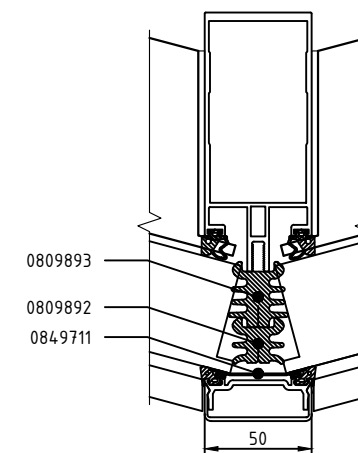

Стойка K6.B13.S2 устанавливается со стоечным сухарем 0345593 во всю длину.

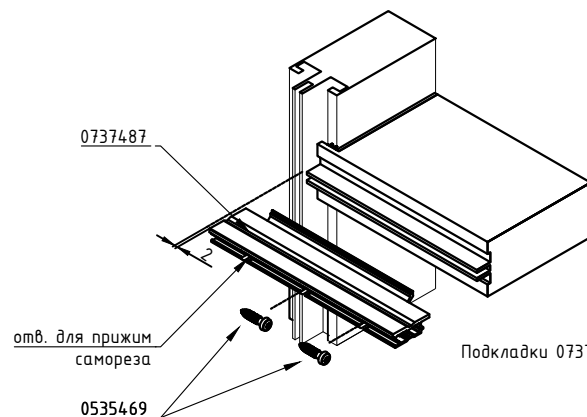

Подкладка 0737487

Подкладки 0737487 напилить из профиля 0340385.

						Остров 2 К1			
						" Многофункциональная комплексная жилая застройка , квартал 2, корпус 1, 2, 3, 4, 5, 6 по адресу : г . Москва , внутригородская территория муниципальный округ Хорошёво - Мнёвники."			
Изм.	Кол.уч.	Лист	№ док.	Подп.	Дата	Светопрзрачные конструкции	Стадия	Лист	Листов
Разраб.	Бирюкова				06.23		Р	86	
Проверил									
Н.контр.									
Т.контр.						Витраж В13.1		ООО "МАРКА ПОЛА"	
Утв.									


Копировал

Согласовано					
ГАП					
ГИП					
Инв. N подл.	Подп. и дата	Взам. инв. N			

Угловой витраж В-6.3 (развертка).



Кол-во : 1 шт.

S=11,33 м.кв.

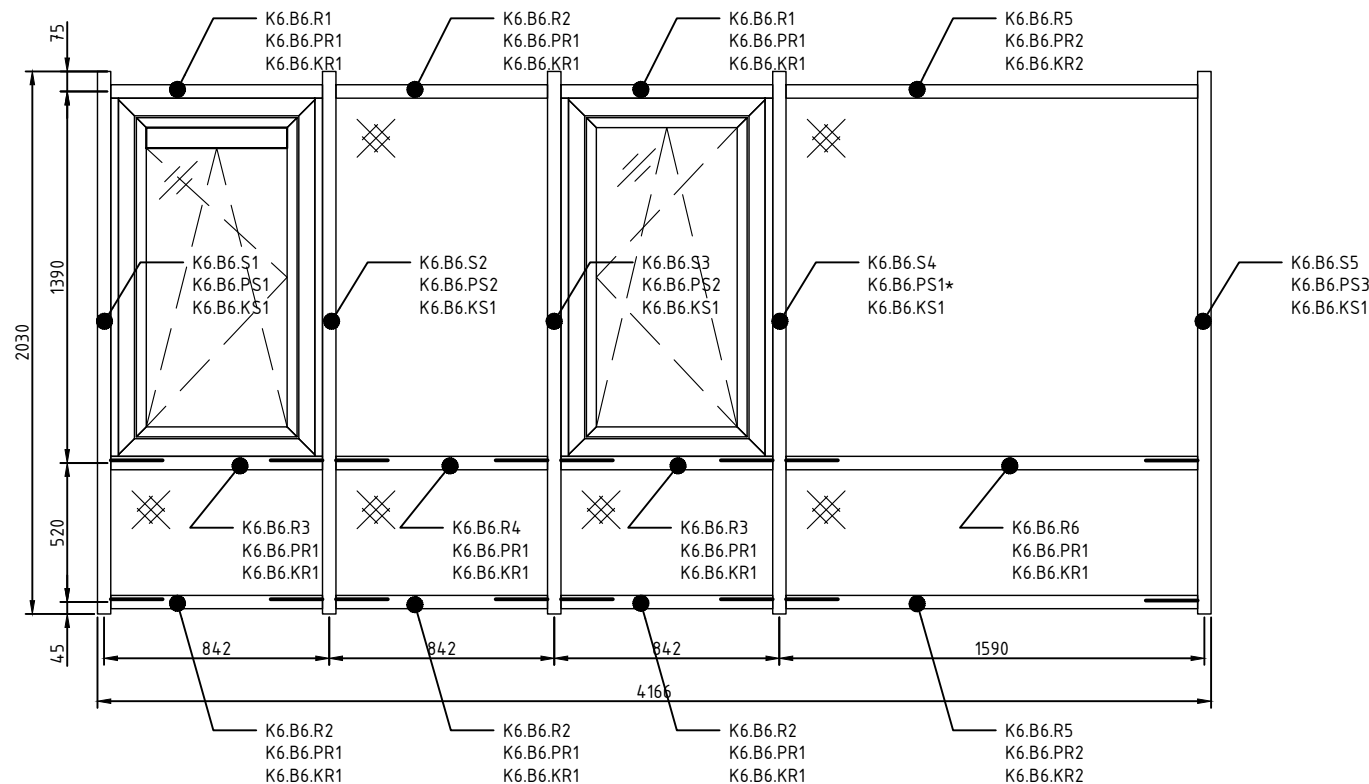

Заполнение термовставки - 0809892 + 0809893.
Под прижимы бутиловая лента - 0849711.
Прижимной саморез:
- прижимы PS1, PS2, PS1* - Ø6,3x67мм - 0535476
- прижимы PS3, PR1, PR2 - Ø6,3x64мм - 0535475

Ригеля крепить саморезом Ø4,2x12,7мм - 0525317

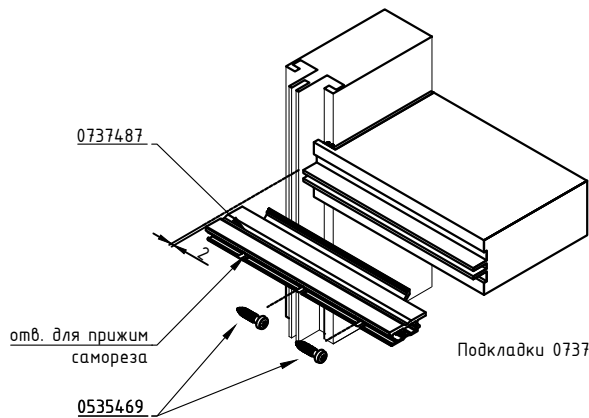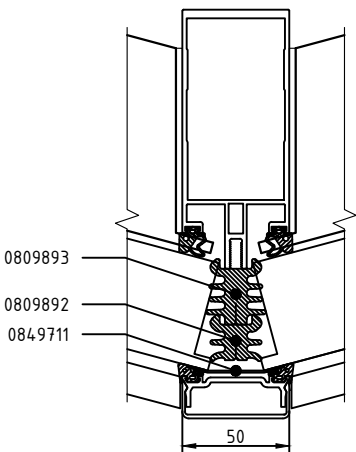

Подкладки 0737487 напилить из профиля 0340385.

Подкладка 0737487

						Остров 2 К1			
						" Многофункциональная комплексная жилая застройка , квартал 2, корпус 1, 2, 3, 4, 5, 6 по адресу : г . Москва , внутригородская территория муниципальный округ Хорошёво -Мнёвники."			
Изм.	Кол.уч.	Лист	№ док.	Подп.	Дата	Светопрозрачные конструкции	Стадия	Лист	Листов
Разраб.	Бирюкова				06.23		Р	87	
Проверил									
Н.контр.						Витраж В6.3	ООО "МАРКА ПОЛА"		
Т.контр.									
Утв.									


Копировала

Согласовано					
Изм.	Кол.уч.	Лист	№ док.	Подп.	Дата
Разраб.	Бирюкова				06.23
Проверил					
Н.контр.					
Т.контр.					
Утв.					

Угловой витраж В-11 (развертка).

Кол-во: 1 шт.

S=9,90 м.кв.

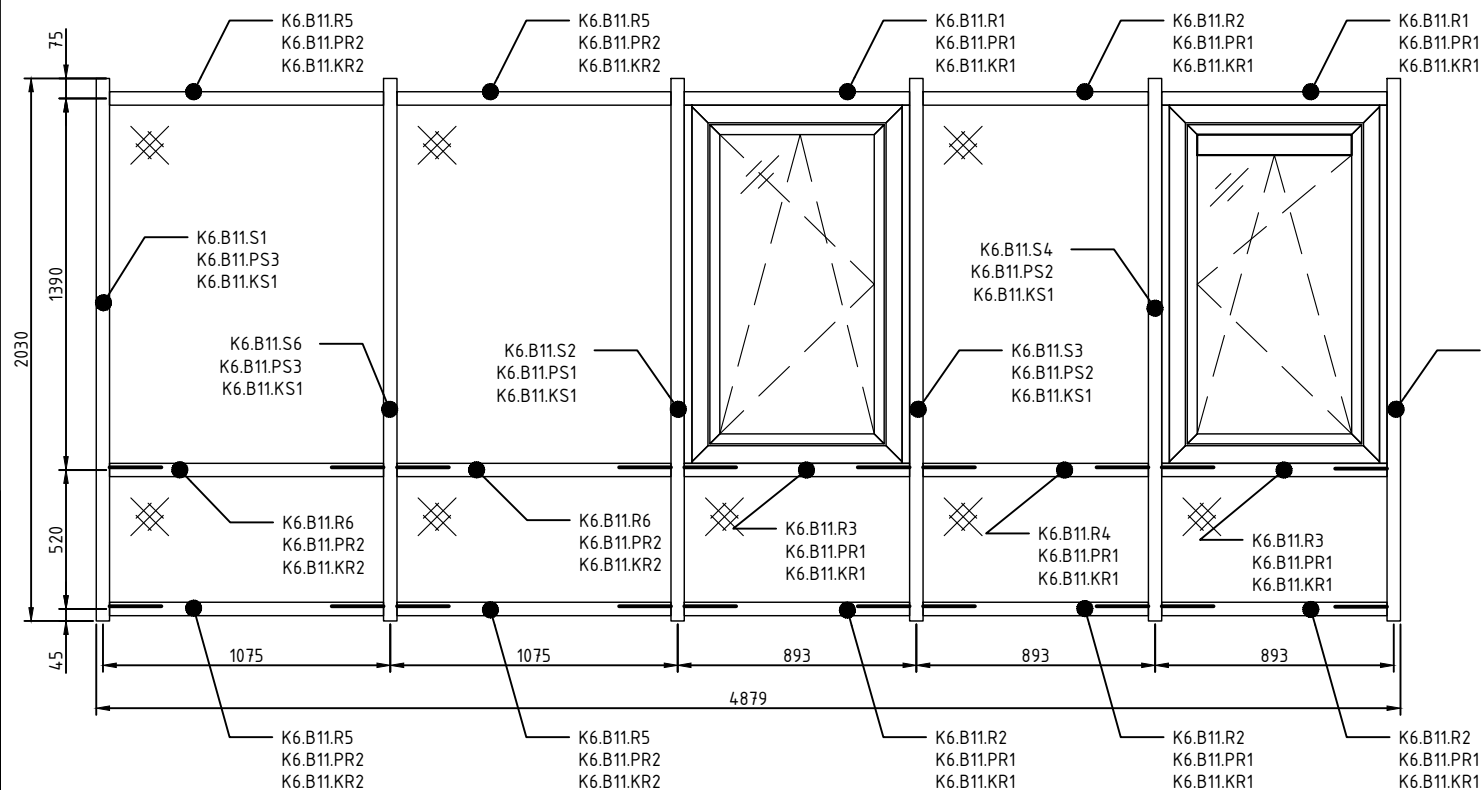



Заполнение термовставки - 0809892 + 0809893.

Под прижимы джутовая лента - 0849711.

Прижимной саморез:

- прижимы PS1, PS2, PS1* - Ø6,3x67мм - 0535476
- прижимы PS3, PR1, PR2 - Ø6,3x64мм - 0535475

Ригеля крепить саморезом Ø4,2x12,7мм - 0525317

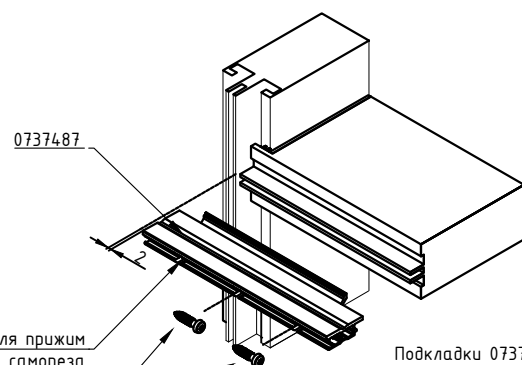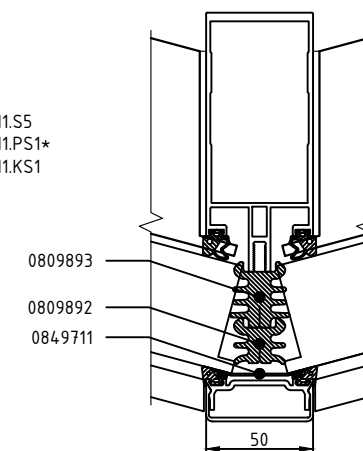

Подкладка 0737487

Подкладки 0737487 напилить из профиля 0340385.

						Остров 2 К1			
						" Многофункциональная комплексная жилая застройка , квартал 2, корпус 1, 2, 3, 4, 5, 6 по адресу : г . Москва , внутригородская территория муниципальный округ Хорошёво -Мнёвники."			
Изм.	Кол.уч.	Лист	№ док.	Подп.	Дата	Светопрозрачные конструкции	Стадия	Лист	Листов
Разраб.	Бирюкова				06.23		Р	88	
Проверил									
Н.контр.									
Т.контр.						Витраж В11		ООО "МАРКА ПОЛА"	
Утв.									


Копировал

Согласовано	ГАП	ГИП
Инв. N подл.	Подп. и дата	Взам. инв. N

Угловой витраж В-18 (развертка).

Кол-во: 1 шт.

S=9,90 м.кв.

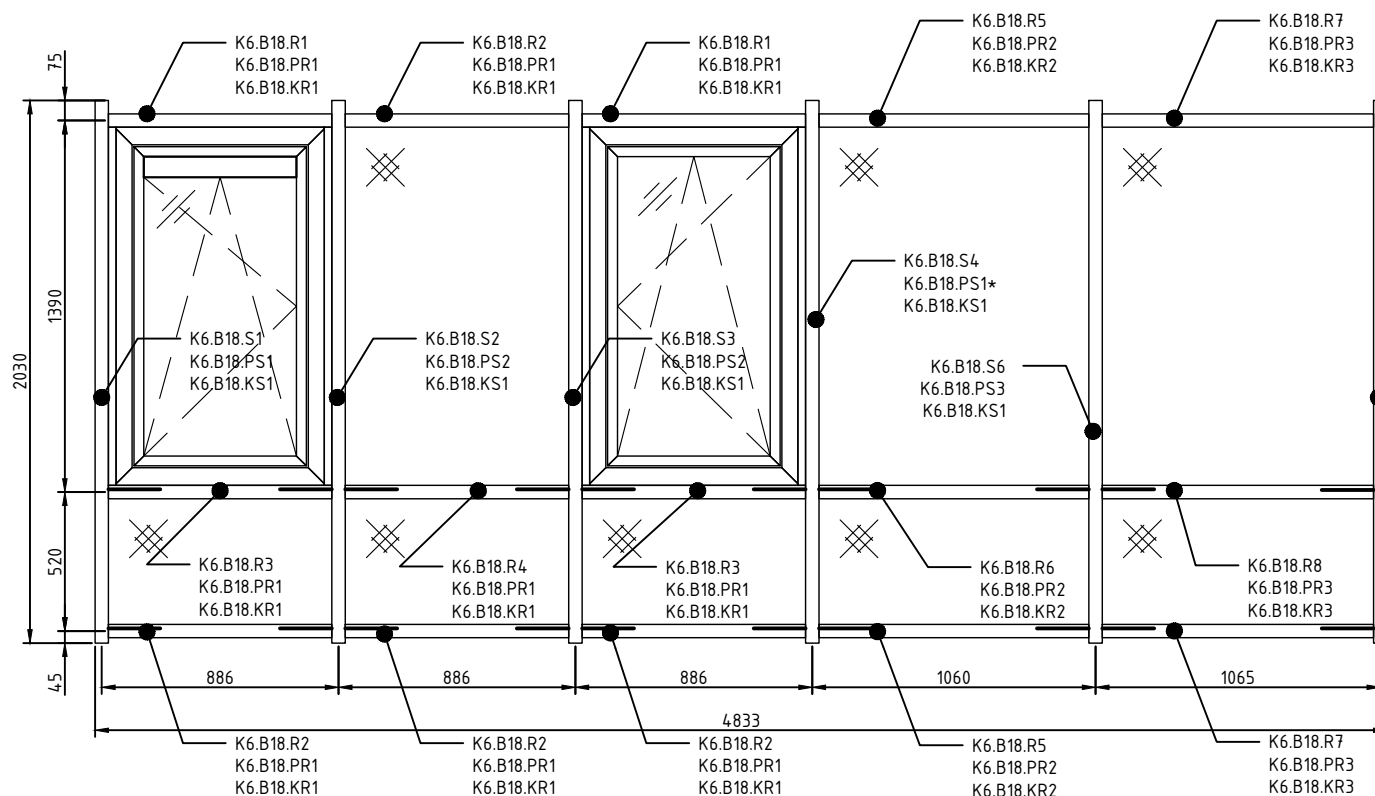



Заполнение термовставки - 0809892 + 0809893.

Под прижимы бутиловая лента - 0849711.

Прижимной саморез:

- прижимы PS1, PS2, PS1* - Ø6,3x67мм - 0535476
- прижимы PS3, PR1, PR2 - Ø6,3x64мм - 0535475

Ригеля крепить саморезом Ø4,2x12,7мм - 0525317

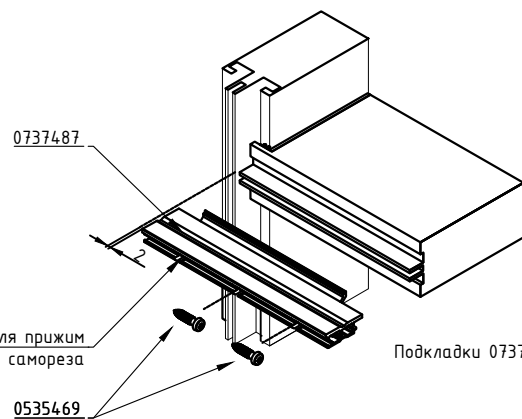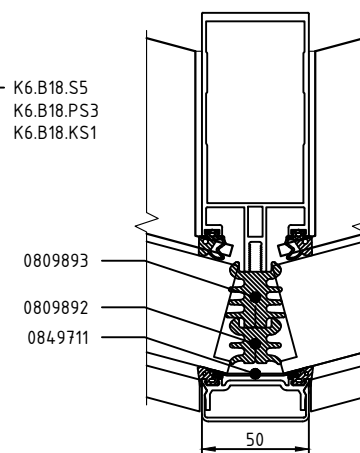

Подкладка 0737487

Подкладки 0737487 напилить из профиля 0340385.

						Остров 2 К1			
						" Многофункциональная комплексная жилая застройка , квартал 2, корпус 1, 2, 3, 4, 5, 6 по адресу : г . Москва , внутригородская территория муниципальный округ Хорошёво -Мнёвники."			
Изм.	Кол.уч.	Лист	№ док.	Подп.	Дата	Светопрозрачные конструкции	Стадия	Лист	Листов
Разраб.	Бирякова				06.23		Р	89	
Проверил									
Н. контр.									
Т. контр.									
Утв.									
						Витраж В18		ООО "МАРКА ПОЛА"	

Копировал

Согласовано

ГАП
ГИП

Взам. инв. №


Подп. и дата

Инв. № подл.

Угловой витраж В-19 (развертка).

Кол-во: 1 шт.

S=5,13 м.кв.

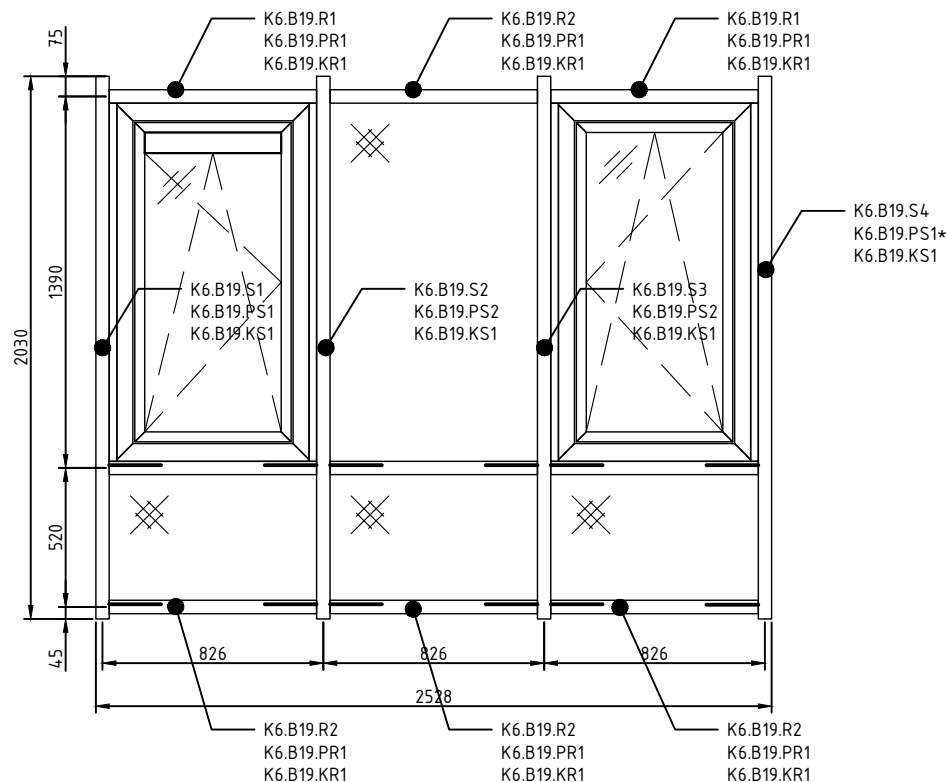



Заполнение термовставки - 0809892 + 0809893.

Под прижимы дутыловая лента - 0849711.

Прижимной саморез:

- прижимы PS1, PS2, PS1* - Ø6,3x67мм - 0535476
- прижимы PS3, PR1, PR2 - Ø6,3x64мм - 0535475

Ригеля крепить саморезом Ø4,2x12,7мм - 0525317

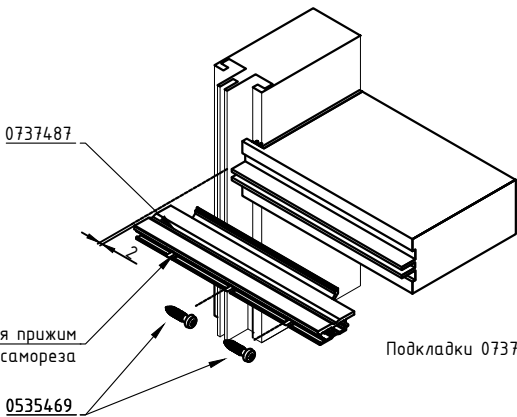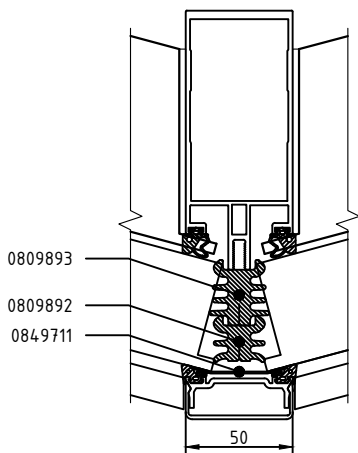

Подкладка 0737487

Подкладки 0737487 напилить из профиля 0340385.


						Остров 2 К1			
						" Многофункциональная комплексная жилая застройка , квартал 2, корпус 1, 2, 3, 4, 5, 6 по адресу : г . Москва , внутригородская территория муниципальный округ Хорошёво -Мнёвники."			
Изм.	Кол.уч.	Лист	№ док.	Подп.	Дата	Светопрозрачные конструкции	Стадия	Лист	Листов
Разраб.	Бирюкова				06.23		Р	90	
Проверил									
Н.контр.						Витраж В19	ООО "МАРКА ПОЛА"		
Т.контр.									
Утв.									

Копировал


Угловой витраж В-9 (развертка).

Кол-во: 1 шт.


S=15,13 м.кв.

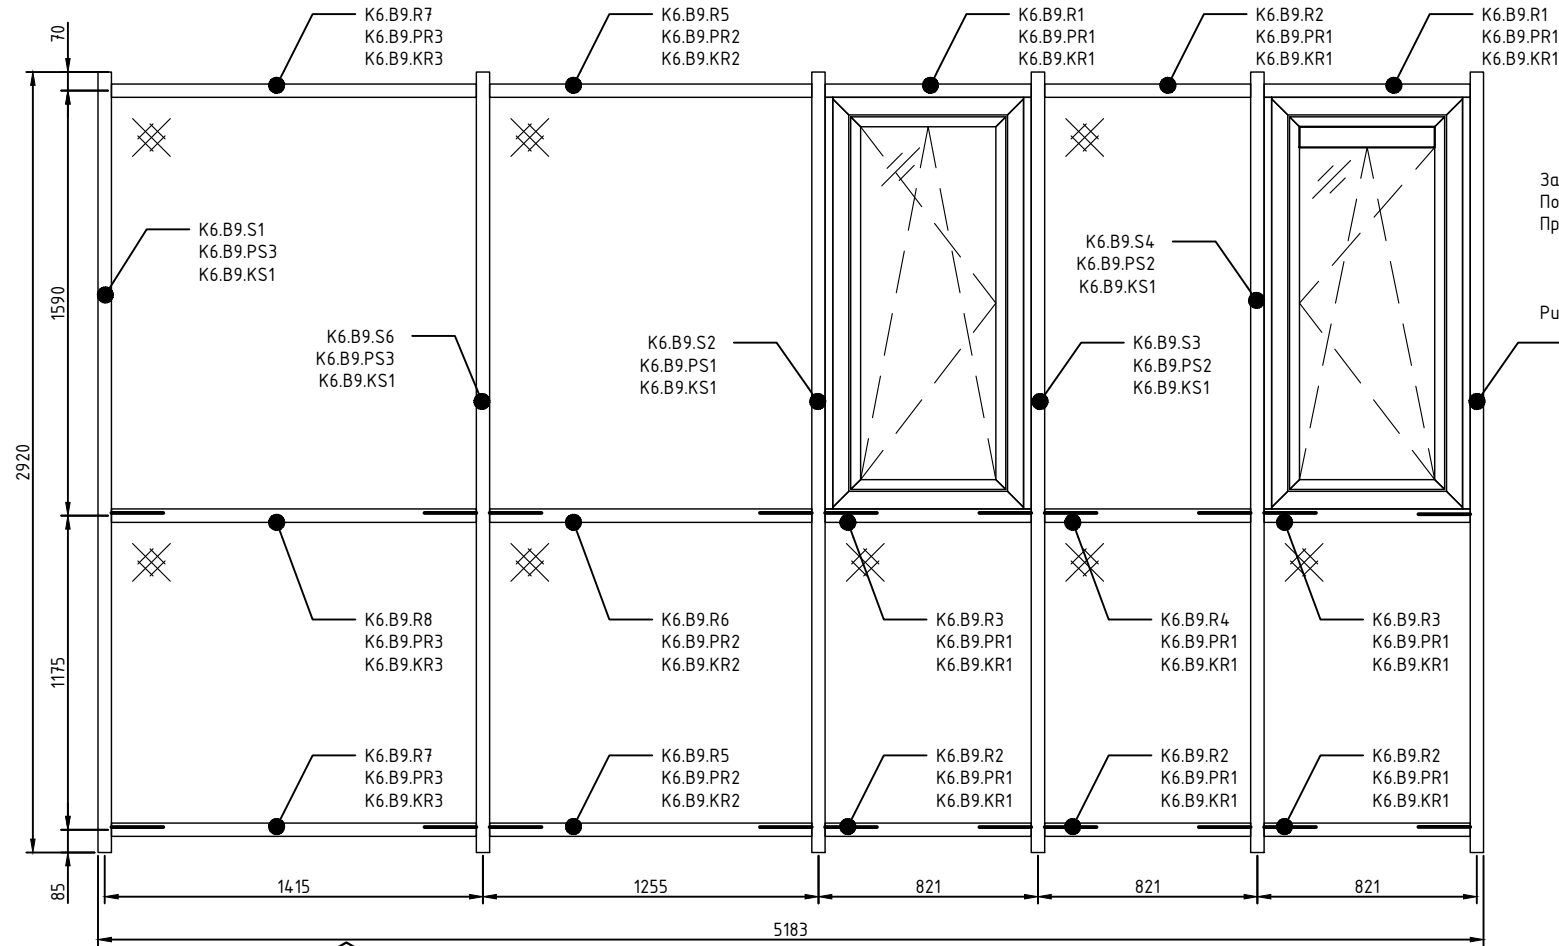

Заполнение термовставки - 0809892 + 0809893.
Под прижимы бутиловая лента - 0849711.
Прижимной саморез:
- прижимы PS1, PS2, PS1* - Ø6,3x67мм - 0535476
- прижимы PS3, PR1, PR2 - Ø6,3x64мм - 0535475
Ригеля крепить саморезом Ø4,2x12,7мм - 0525317

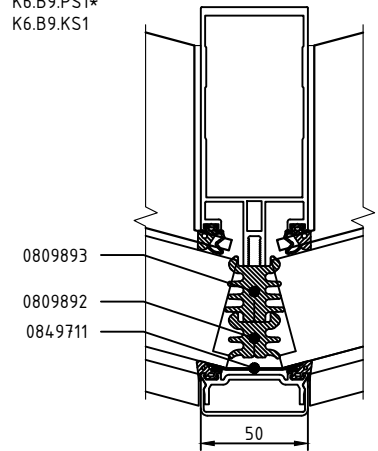

Стойка K6.B9.S6 и K6.B9.S2 устанавливается со стоечным сухарем 0345593 во всю длину.

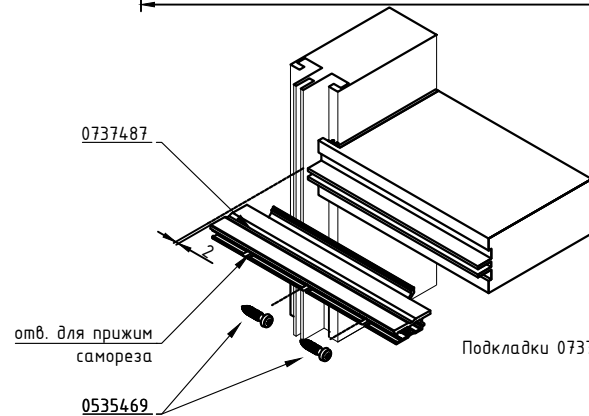

Подкладка 0737487

Подкладки 0737487 напилить из профиля 0340385.

						Остров 2 К1			
						" Многофункциональная комплексная жилая застройка , квартал 2, корпус 1, 2, 3, 4, 5, 6 по адресу : г . Москва , внутригородская территория муниципальный округ Хорошёво -Мнёвники."			
Изм.	Кол.уч.	Лист	№ док.	Подп.	Дата	Светопрозрачные конструкции	Стадия	Лист	Листов
Разраб.	Бирюкова				06.23		Р	91	
Проверил									
Н. контр.									
Т. контр.						Угловой витраж В-9.2		ООО "МАРКА ПОЛА"	
Утв.									


Копировала

Согласовано	ГАП	
	ГИП	
Инв. N подл.	Подп. и дата	Взам. инв. N


Угловой витраж В-10 (развертка).

Кол-во: 1 шт.


S=15,13 м.кв.

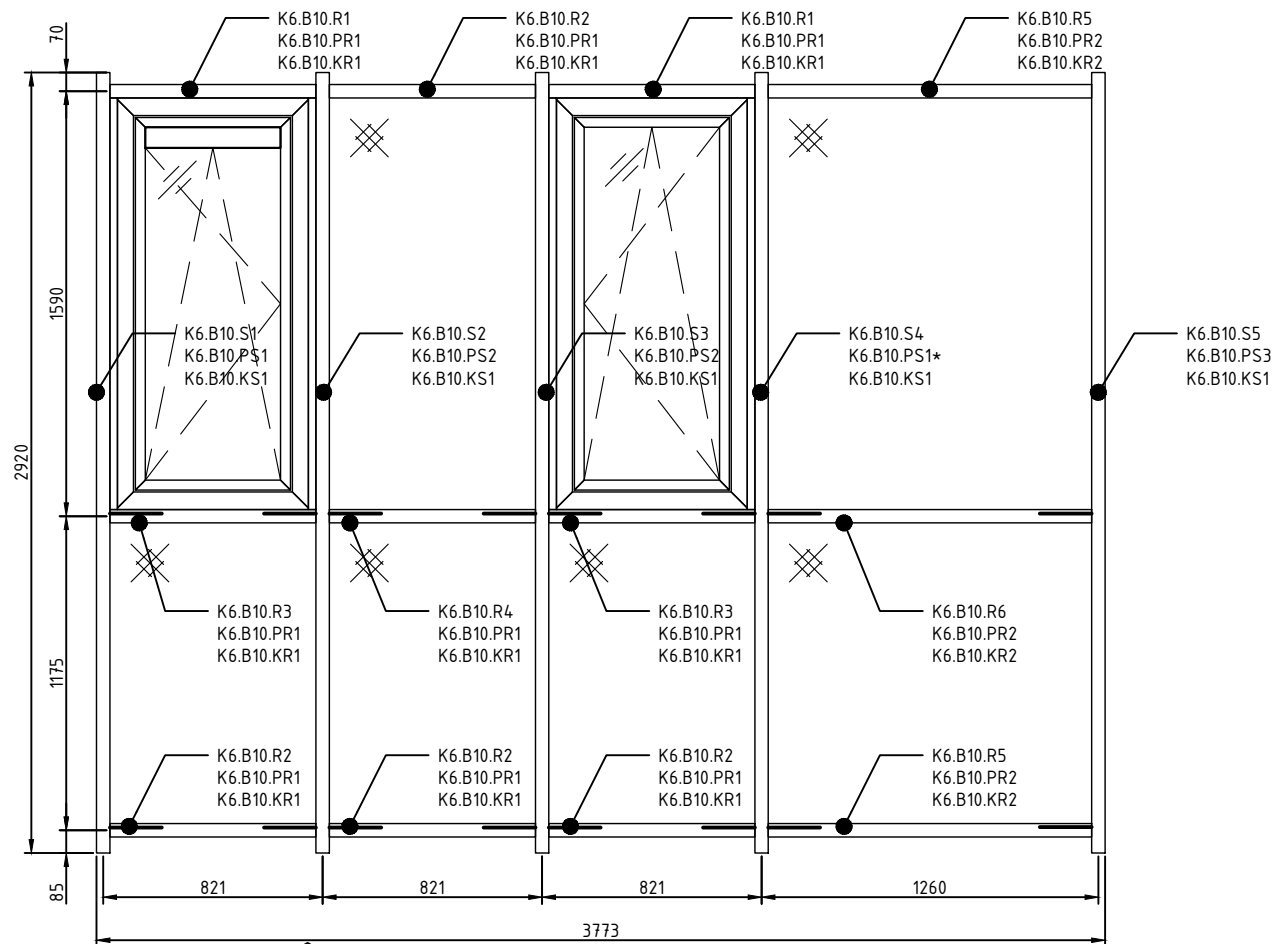

Заполнение термовставки - 0809892 + 0809893.
Под прижимы бутиловая лента - 0849711.
Прижимной саморез:
- прижимы PS1, PS2, PS1* - Ø6,3x67мм - 0535476
- прижимы PS3, PR1, PR2 - Ø6,3x64мм - 0535475
Резеля крепить саморезом Ø4,2x12,7мм - 0525317

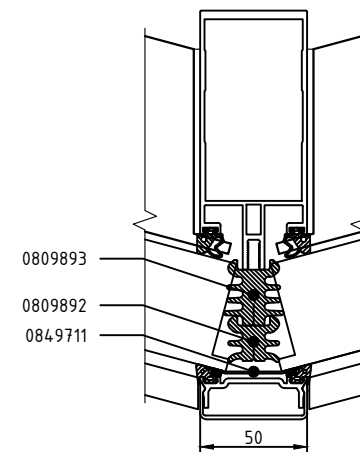

Стойка K6.B1.S4 устанавливается со стоечным сухарем 0345593 во всю длину.



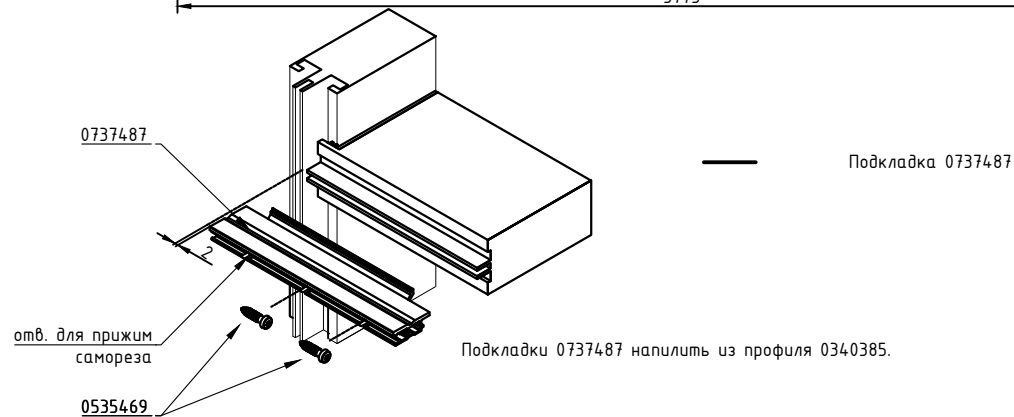


						Остров 2 К1			
						" Многофункциональная комплексная жилая застройка , квартал 2, корпус 1, 2, 3, 4, 5, 6 по адресу : г . Москва , внутригородская территория муниципальный округ Хорошёво -Мнёвники."			
Изм.	Кол.уч.	Лист	№ док.	Подп.	Дата	Светопрозрачные конструкции	Стадия	Лист	Листов
Разраб.	Бирякова				06.23		Р	92	
Проверил									
Н.контр.									
Т.контр.						Угловой витраж В-10.1		ООО "МАРКА ПОЛА"	
Утв.									

Копировал

Согласовано	ГАП	ГИП	Взам. инв. Н	Подп. и дата	Инв. Н подл.

$S=11,98$ м.кв.

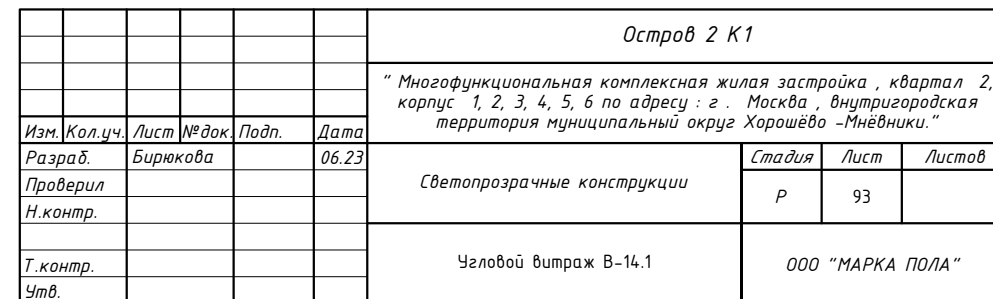 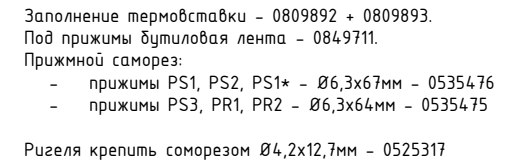

Копировал


Согласовано

Инв. N подл.	Подп. и дата	Взам. инв. N
--------------	--------------	--------------

Угловой витраж В-3 (развертка).


Кол-во: 1 шт.

S=13,15 м.кв.

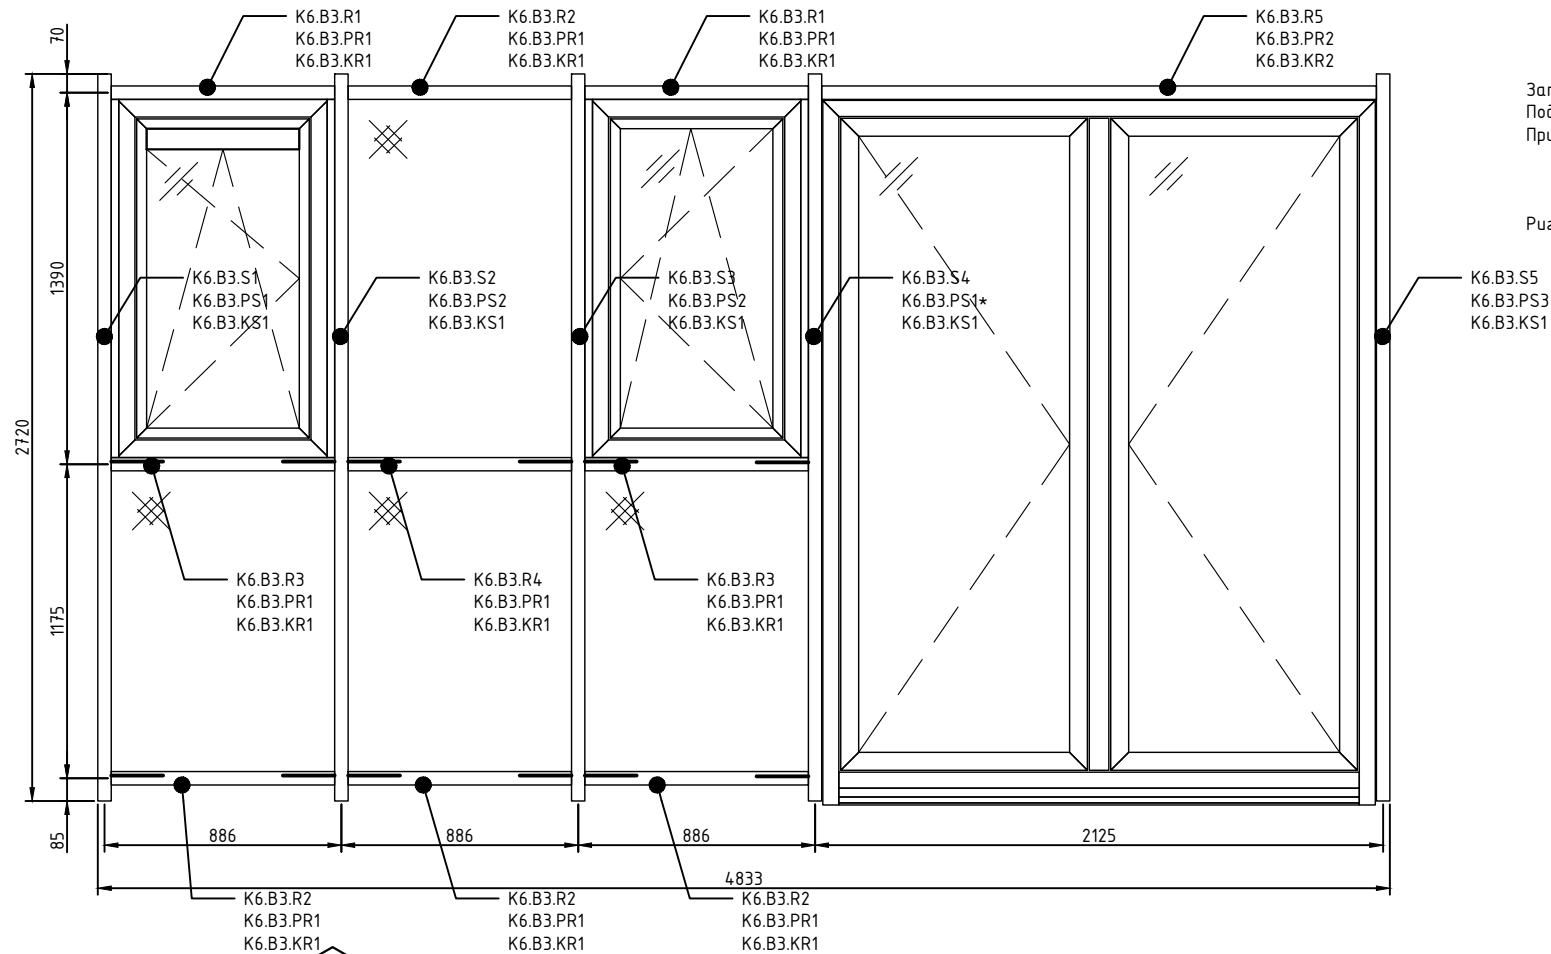


Заполнение термовставки - 0809892 + 0809893.
Под прижимы дутитовая лента - 0849711.
Прижимной саморез:
- прижимы PS1, PS2, PS1* - Ø6,3x67мм - 0535476
- прижимы PS3, PR1, PR2 - Ø6,3x64мм - 0535475

Ригеля крепить саморезом Ø4,2x12,7мм - 0525317

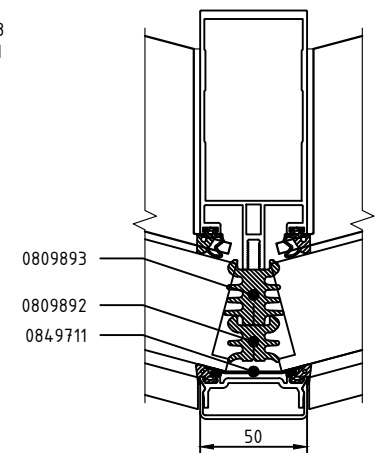

Стойка K6.B3.S4 устанавливается со стоечным сухарем 0345593 во всю длину.

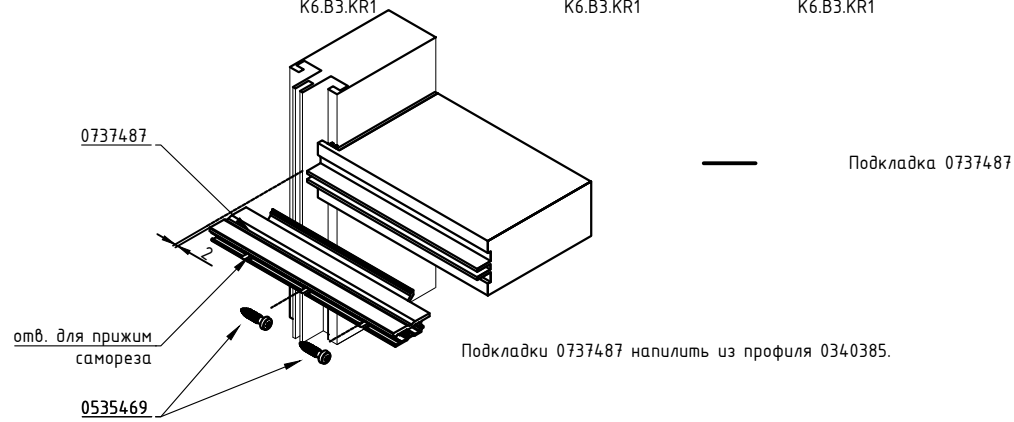

						Остров 2 К1			
						" Многофункциональная комплексная жилая застройка , квартал 2, корпус 1, 2, 3, 4, 5, 6 по адресу : г . Москва , внутригородская территория муниципальный округ Хорошёво -Мнёвники."			
Изм.	Кол.уч.	Лист	№ док.	Подп.	Дата	Светопрзрачные конструкции	Стадия	Лист	Листов
Разраб.	Бирякова				06.23		Р	94	
Проверил									
Н.контр.									
Т.контр.						Угловой витраж В-3.2		ООО "МАРКА ПОЛА"	
Утв.									


Копировал

Согласовано	ГАП	ГИП
Инв. и подл.	Подп. и дата	Взам. инв. и

Угловой витраж В-4 (развертка).

Кол-во : 5 шт.

S=13,27 м.кв.

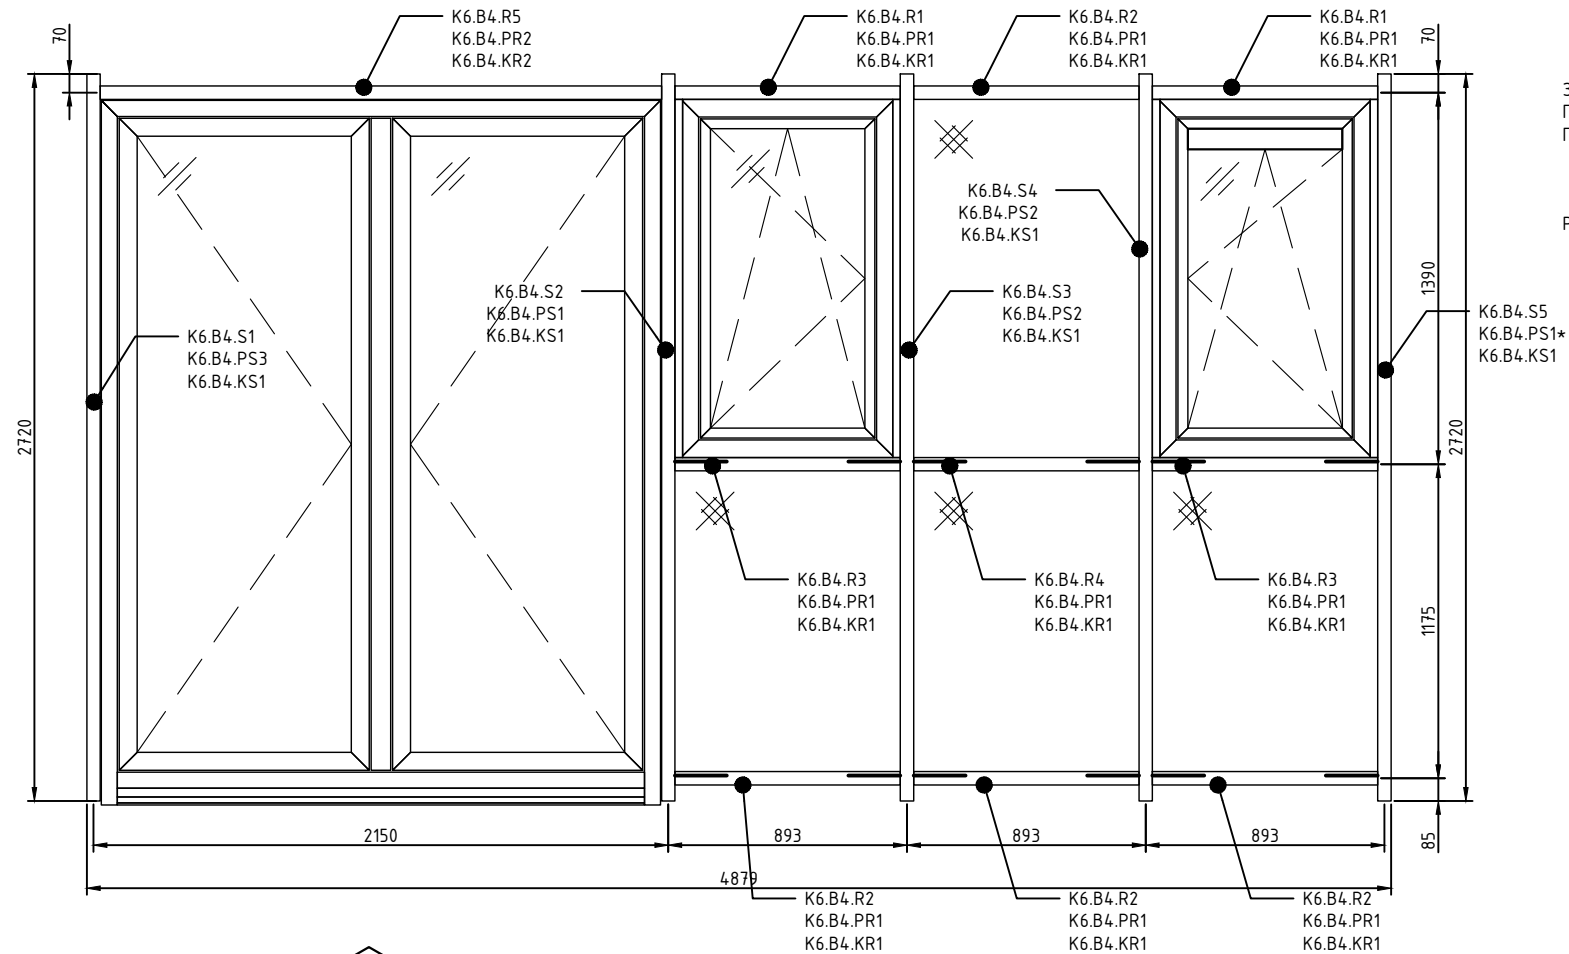


Заполнение термовставки - 0809892 + 0809893.

Под прижимы дутитовая лента - 0849711.


Прижимной саморез:

- прижимы PS1, PS2, PS1* - Ø6,3x67мм - 0535476
- прижимы PS3, PR1, PR2 - Ø6,3x64мм - 0535475

Ригеля крепить саморезом Ø4,2x12,7мм - 0525317

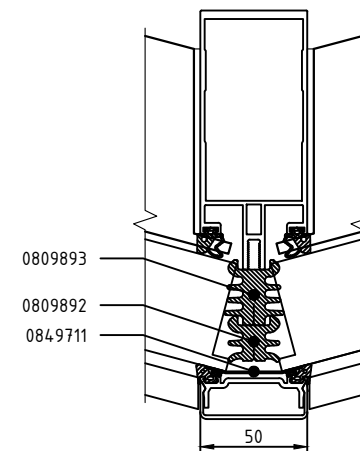

Стойка K6.B4.S2 устанавливается со стоечным сухарем 0345593 во всю длину.

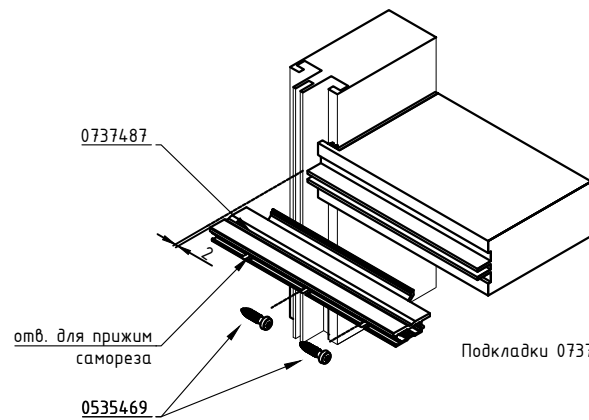

Подкладки 0737487 напиль из профиля 0340385.



Подкладка 0737487

						Остров 2 К1			
						" Многофункциональная комплексная жилая застройка , квартал 2, корпус 1, 2, 3, 4, 5, 6 по адресу : г . Москва , внутригородская территория муниципальный округ Хорошёво - Мнёвники."			
Изм.	Кол.уч.	Лист	№ док.	Подп.	Дата	Светопрзрачные конструкции	Стадия	Лист	Листов
Разраб.	Бирюкова				06.23		Р	95	
Проверил									
Н.контр.									
Т.контр.						Угловой витраж В-4.2		ООО "МАРКА ПОЛА"	
Утв.									

Копировал

Согласовано					
ГАП					
ГИП					
Взам. инв. Н					
Подп. и дата					
Инв. Н подл.					



$S=13,15$ м.кв.

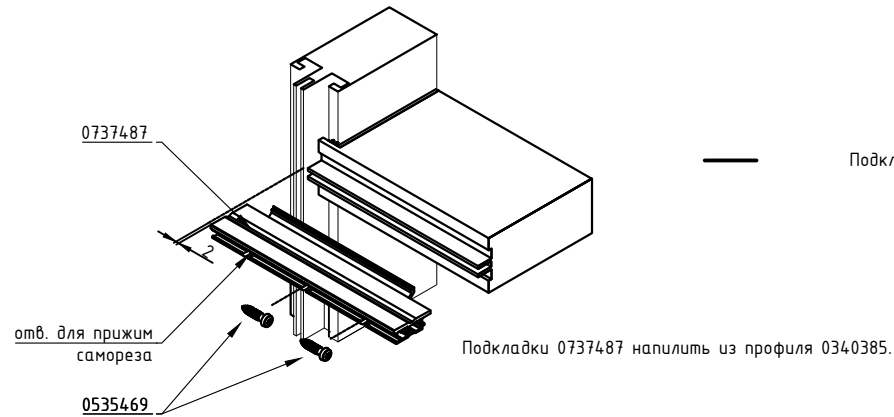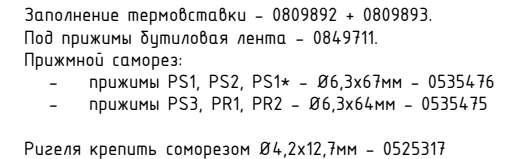

Подкладки 0737487 напилить из профиля 0340385.

						Остров 2 К1			
						" Многофункциональная комплексная жилая застройка , квартал 2, корпус 1, 2, 3, 4, 5, 6 по адресу : г . Москва , внутригородская территория муниципального округа Хорошёво –Мнёвники."			
Изм.	Кол.уч.	Лист	№ док	Подп.	Дата	Светопрозрачные конструкции	Стадия	Лист	Листов
Разраб.		Бирюкова			06.23		Р	96	
Проверил									
Н.контр.									
Т.контр.						Узловой витраж В-17	ООО "МАРКА ПОЛА"		
Утв.									

Копировал
 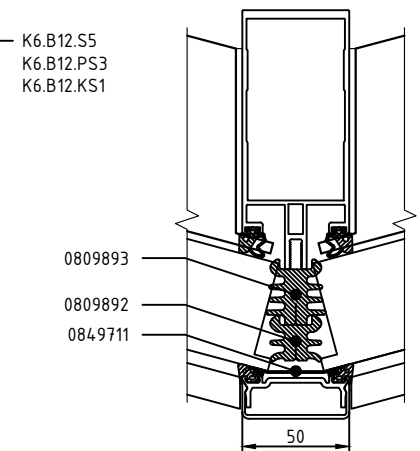
$$S=14,40 \text{ м.кВ.}$$


Стойка K6.B12.S4 и K6.B12.S6 устанавливается со стоечным сухарем 0345593 во всю длину.


Копировал

Инв. N подл.	Подп. и дата	Взам. инв. N
--------------	--------------	--------------

Угловой витраж В-15 (развертка).

Кол-во: 1 шт.

S=14,02 м.кв.

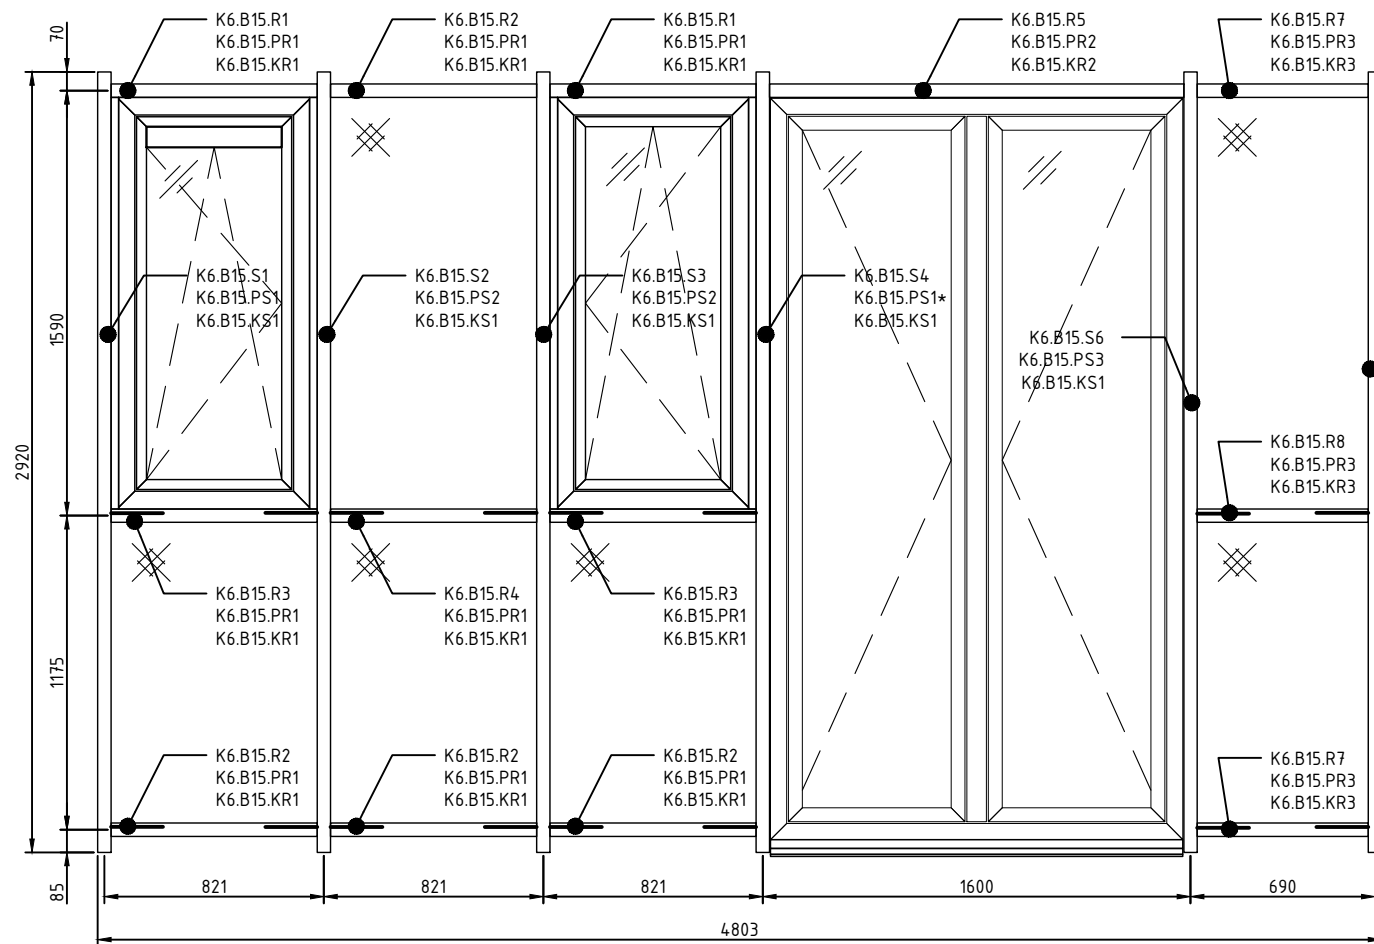


Заполнение термовставки - 0809892 + 0809893.

Под прижимы дутитовая лента - 0849711.


Прижимной саморез:

- прижимы PS1, PS2, PS1* - Ø6,3x67мм - 0535476
- прижимы PS3, PR1, PR2 - Ø6,3x64мм - 0535475

Ригеля крепить саморезом Ø4,2x12,7мм - 0525317

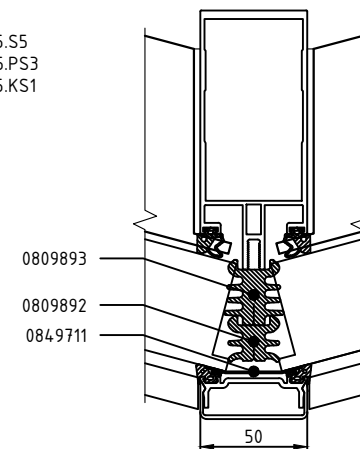

Стойка K6.B15.S4 и K6.B15.S6 устанавливается со стоечным сухарем 0345593 во всю длину.

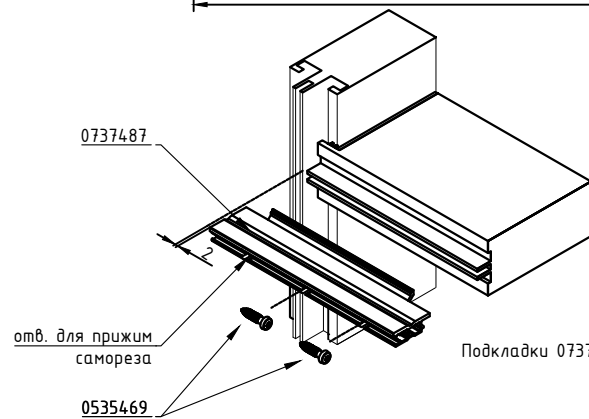

Подкладки 0737487 напильник из профиля 0340385.

Подкладка 0737487

						Остров 2 К1			
						" Многофункциональная комплексная жилая застройка , квартал 2, корпус 1, 2, 3, 4, 5, 6 по адресу : г . Москва , внутригородская территория муниципальный округ Хорошёво - Мнёвники."			
Изм.	Кол.уч.	Лист	№ док.	Подп.	Дата	Светопрозрачные конструкции	Стадия	Лист	Листов
Разраб.	Бирюкова				06.23		Р	98	
Проверил									
Н.контр.									
Т.контр.						Витраж В15.1		ООО "МАРКА ПОЛА"	
Утв.									


Копировал

Согласовано					
ГАП					
ГИП					
Инв. N подл.	Подп. и дата	Взам. инв. N			

Согласовано	ГАП	ГИП
Взам. инв. №		
Подп. и дата		
Инв. № подл.		


Маркировка:
 К6.В1.55 – 18 шт. (зеркально)
 К6.В2.51 – 18 шт.
 К6.В5.51 – 13 шт.
 К6.В16.55 – 13 шт. (зеркально)
 К6.В7.51 – 1 шт.
 К6.В8.55 – 1 шт. (зеркально)
 К6.В13.51 – 1 шт.
 К6.В12.55 – 1 шт. (зеркально)

Цвет: 79 7М15





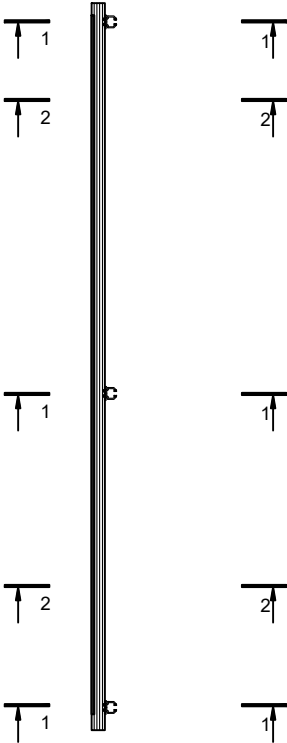


Маркировка:
 К6.В1.54 – 18 шт. (зеркально)
 К6.В2.52 – 18 шт.
 К6.В5.52 – 13 шт.
 К6.В16.54 – 13 шт. (зеркально)
 К6.В7.52 – 1 шт.
 К6.В8.54 – 1 шт. (зеркально)
 К6.В13.52 – 1 шт.
 К6.В17.54 – 4 шт. (зеркально)

Цвет: 79 7М15

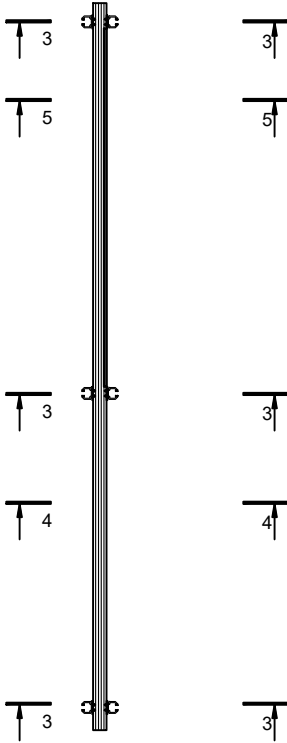







- Примечание.
1. Каждую стойку перед производством работ оклеить защитной пленкой,замаркировать номером стойки и укомплектовать уплотнителями и флистрами
 2. Стойки укомплектовать подпятниками из 034.5593 L=150 мм и дренажным лотком 073.8263.04 на винт 050.5029.--
 3. Манжету 080.9885 и сухарь РС-2 установить на производсве по шаблону. Манжету подрезать по торцу ригеля.
 4. Ригельные сухари РС-1 и РС-2 устанавливать на саморез Ø4,8x13 – 0525330.

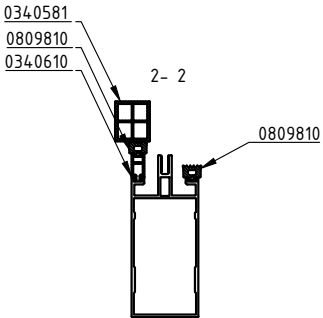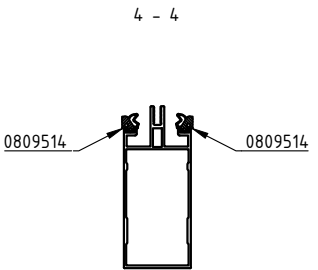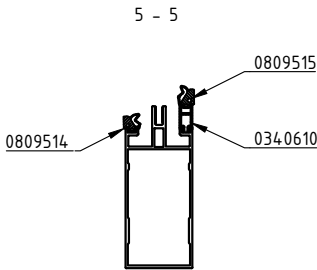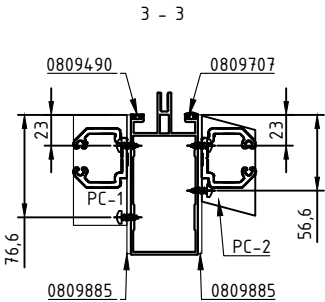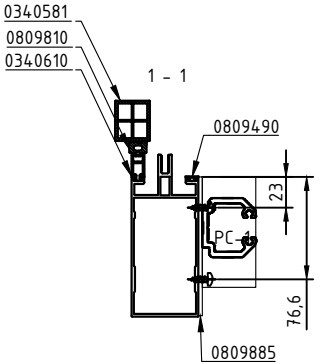

						Остров 2 К1			
						" Многофункциональная комплексная жилая застройка , квартал 2, корпус 1, 2, 3, 4, 5, 6 по адресу : г . Москва , внутригородская территория муниципальный округ Хорошёво –Мнёвники."			
Изм.	Кол.уч.	Лист	№ док.	Подп.	Дата	Светопрзрачные конструкции	Стадия	Лист	Листов
Разраб.	Бирякова				06.23		Р	99	
Проверил									
Н.контр.						Стойки В12, В13, В14, В15	ООО "МАРКА ПОЛА"		
Т.контр.									
Утв.									

Копировал

Инв. N подл.	Подп. и дата	Взам. инв. N	Согласовано	
			ГАП	
			ГИП	

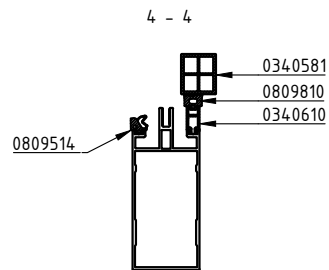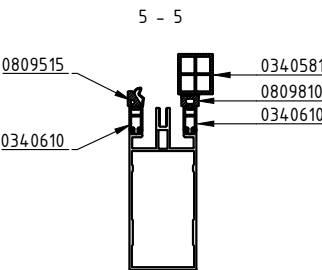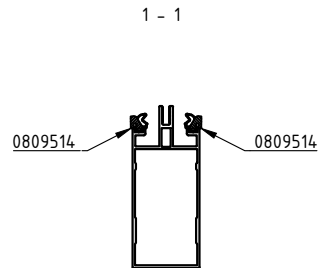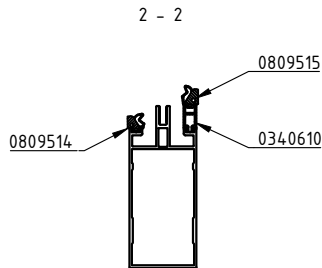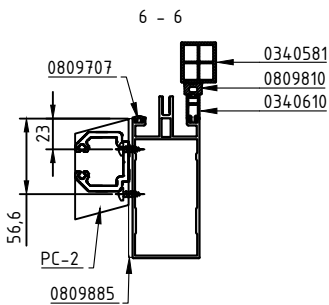
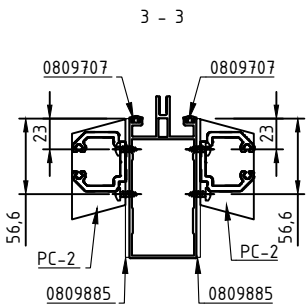


Маркировка:
 К6.В1.С3 – 18 шт.
 К6.В1.С2 – 18 шт (зеркально)
 К6.В2.С4 – 18 шт.
 К6.В2.С3 – 18 шт (зеркально)
 К6.В5.С4 – 13 шт.
 К6.В5.С3 – 13 шт (зеркально)
 К6.В16.С3 – 13 шт.
 К6.В16.С2 – 13 шт (зеркально)
 К6.В7.С4 – 1 шт.
 К6.В7.С3 – 1 шт (зеркально)
 К6.В8.С3 – 1 шт.
 К6.В8.С2 – 1 шт (зеркально)
 К6.В13.С4 – 1 шт.
 К6.В13.С3 – 1 шт (зеркально)
 К6.В3.С3 – 1 шт.
 К6.В3.С2 – 1шт (зеркально)
 К6.В4.С4 – 5 шт.
 К6.В4.С3 – 5 шт (зеркально)
 К6.В17.С3 – 4 шт.
 К6.В17.С2 – 4 шт (зеркально)
 К6.В12.С3 – 1 шт.
 К6.В12.С2 – 1 шт (зеркально)

Цвет: 79 7М15

Маркировка:
 К6.В1.С1 – 18 шт. (зеркально)
 К6.В2.С5 – 18 шт
 К6.В5.С5 – 13 шт.
 К6.В16.С1 – 13 шт. (зеркально)
 К6.В7.С5 – 1 шт.
 К6.В8.С1 – 1 шт. (зеркально)
 К6.В13.С5 – 1 шт.
 К6.В3.С1 – 1 шт. (зеркально)
 К6.В4.С5 – 5 шт.
 К6.В17.С1 – 4 шт. (зеркально)
 К6.В12.С1 – 1 шт. (зеркально)

Цвет: 79 7М15

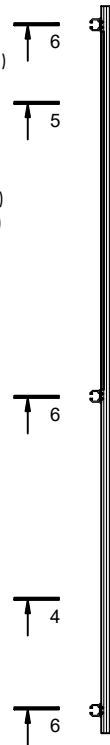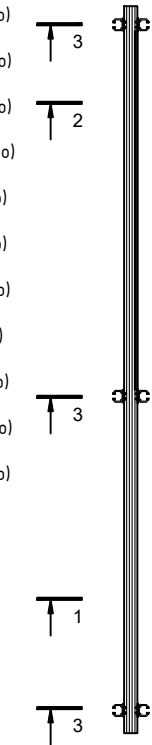

- Примечание.
1. Каждую стойку перед производством работ оклеить защитной пленкой,замаркировать номером стойки и укомплектовать уплотнителями и филлистрами
 2. Стойки укомплектовать подпятниками из 034.5593 L=150 мм и дренажным лотком 073.8263.04 на винт 050.5029.--
 3. Манжету 080.9885 и сухарь РС-2 установить на производстве по шаблону. Манжету подрезать по торцу ригеля.
 4. Ригельные сухари РС-1 и РС-2 устанавливать на саморез Ø4,8x13 – 0525330.

						Остров 2 К1			
						" Многофункциональная комплексная жилая застройка , квартал 2, корпус 1, 2, 3, 4, 5, 6 по адресу : г . Москва , внутригородская территория муниципальный округ Хорошёво –Мнёвники."			
Изм.	Кол.уч.	Лист	№ док.	Подп.	Дата	Светопрозрачные конструкции	Стадия	Лист	Листов
Разраб.	Бирюкова				06.23		Р	100	
Проверил									
Н.контр.									
Т.контр.						Стойки В12, В13, В14, В15		ООО "МАРКА ПОЛА"	
Утв.									

Копировал

Маркировка:
К6.В3.С4 - 1 шт.
К6.В4.С2 - 5 шт. (зеркально)
К6.В12.С4 - 1 шт.

Цвет: 79 7М15

Маркировка:
К6.В3.С5 - 1 шт. (зеркально)
К6.В4.С1 - 5 шт.
К6.В17.С5 - 4 шт. (зеркально)

Цвет: 79 7М15


Маркировка:
К6.В17.С6 - 4 шт.
К6.В12.С6 - 1 шт.

Цвет: 79 7М15


Маркировка:
К6.В5.С6 - 13 шт.
К6.В16.С6 - 1 шт.
К6.В7.С6 - 1 шт.

Цвет: 79 7М15



6* - 6*

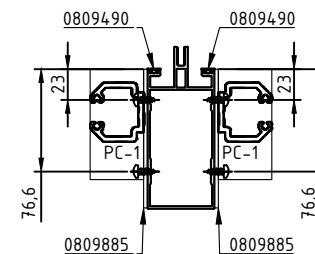

6 - 6

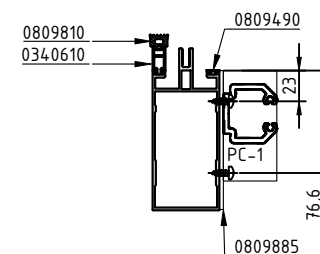


7 - 7

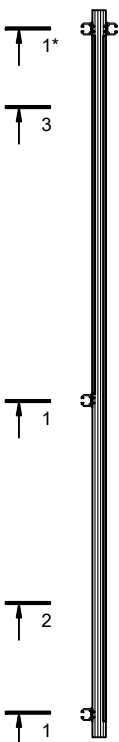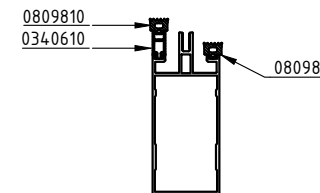



1 - 1




1* - 1*

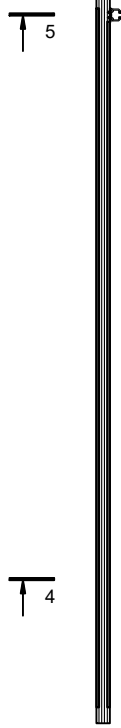


4 - 4

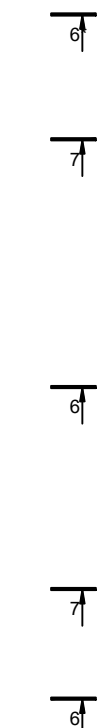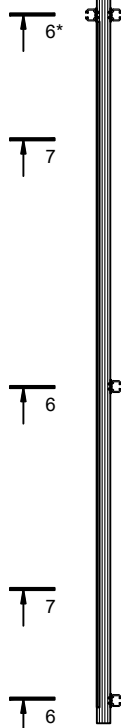


8 - 8

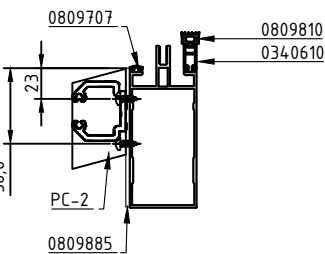



2 - 2

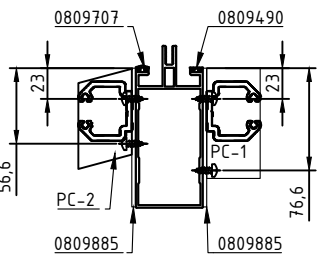


3 - 3

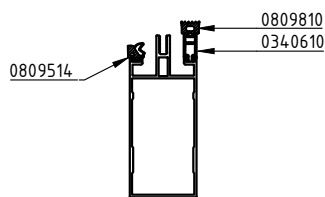


5 - 5

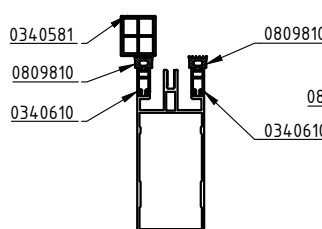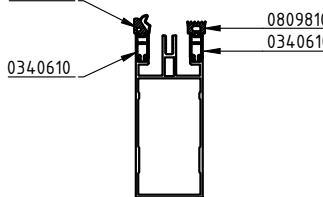

5 - 5

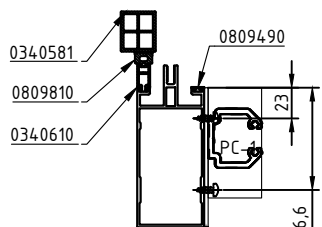

5 - 5

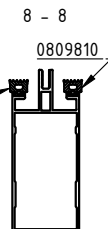

8 - 8

Примечание.

1. Каждую стойку перед производством работ оклеить защитной пленкой, замаркировать номером стойки и укомплектовать уплотнителями и флистрами
2. Стойки укомплектовать подпятниками из 034.5593 L=150 мм и дренажным лотком 073.8263.04 на винт 050.5029.--
3. Манжеты 080.9885 и сухарь РС-2 установить на производстве по шаблону. Манжету подрезать по торцу ригеля.
4. Ригельные сухари РС-1 и РС-2 устанавливать на саморез Ø4,8x13 - 0525330.

Остров 2 К1

" Многофункциональная комплексная жилая застройка , квартал 2, корпус 1, 2, 3, 4, 5, 6 по адресу : г . Москва , внутригородская территория муниципальный округ Хорошёво - Мнёвники."

Светопрозрачные конструкции

Стадия Лист Листов
Р 101




ООО "МАРКА ПОЛА"

Копировал

Согласовано		
	ГАП	ГИП
Взам. инв. №		
Подп. и дата		
Инв. № подл.		




Маркировка:
 К6.В6.55 – 1 шт. (зеркально)
 К6.В11.51 – 1 шт.
 К6.В18.55 – 1 шт. (зеркально)

Цвет: 79 7М15

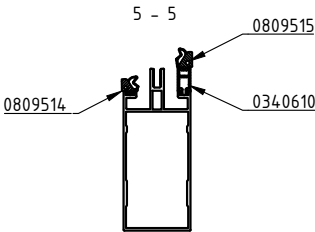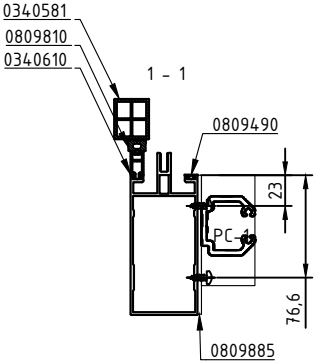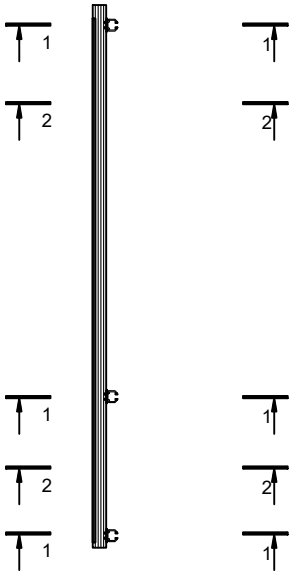



Маркировка:
 К6.В6.54 – 1 шт. (зеркально)
 К6.В11.52 – 1 шт.
 К6.В18.54 – 1 шт. (зеркально)

Цвет: 79 7М15

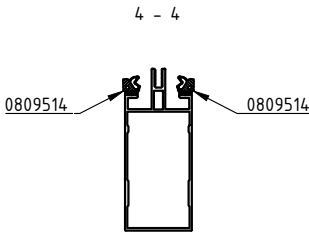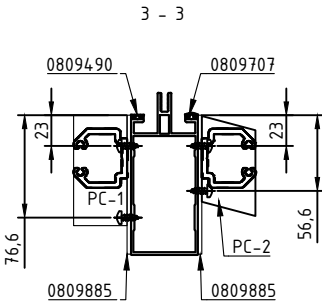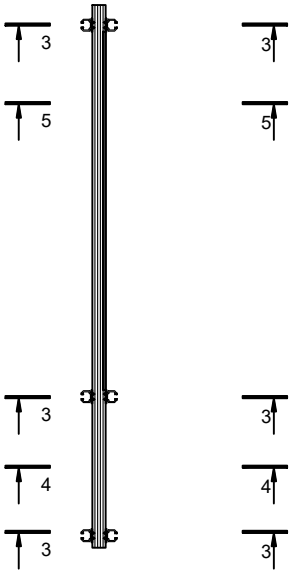


Маркировка:
 К6.В11.56 – 1 шт.
 К6.В18.56 – 1 шт.







Цвет: 79 7М15

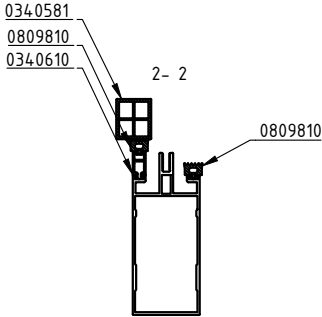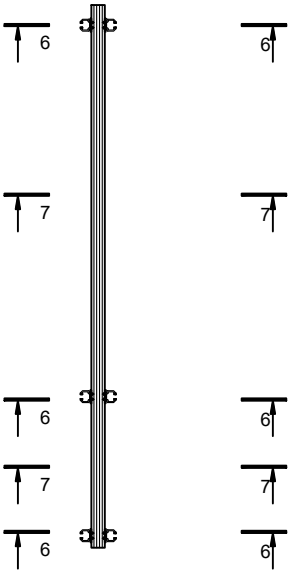

- Примечание.
1. Каждую стойку перед производством работ оклеить защитной пленкой, замаркировать номером стойки и укомплектовать уплотнителями и филлистрами
 2. Стойки укомплектовать подпятниками из 034.5593 L=150 мм и дренажным лотком 073.8263.04 на винт 050.5029.--
 3. Манжету 080.9885 и сухарь PC-2 установить на производстве по шаблону. Манжету подрезать по торцу ригеля.
 4. Ригельные сухари PC-1 и PC-2 устанавливать на саморез Ø4,8x13 – 0525330.

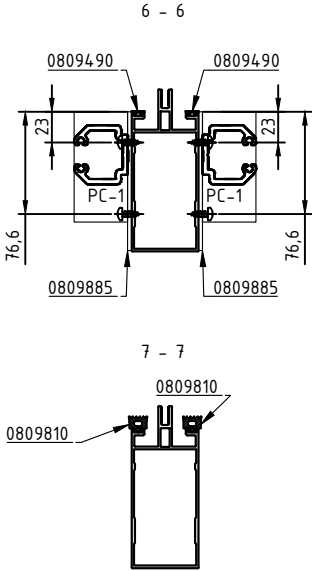


						Остров 2 К1			
						" Многофункциональная комплексная жилая застройка , квартал 2, корпус 1, 2, 3, 4, 5, 6 по адресу : г . Москва , внутригородская территория муниципальный округ Хорошёво –Мнёвники."			
Изм.	Кол.уч.	Лист	№ док.	Подп.	Дата	Светопрзрачные конструкции	Стадия	Лист	Листов
Разраб.	Бирякова				06.23		Р	102	
Проверил									
Н.контр.									
Т.контр.						Стойки В12, В13, В14, В15		ООО "МАРКА ПОЛА"	
Утв.									

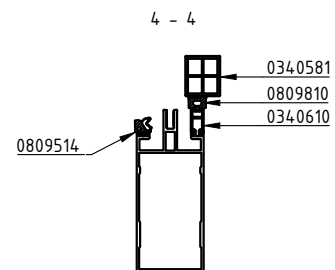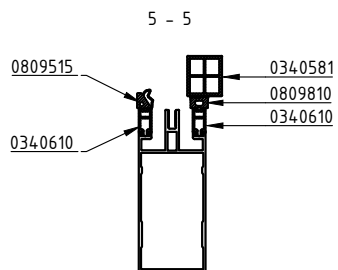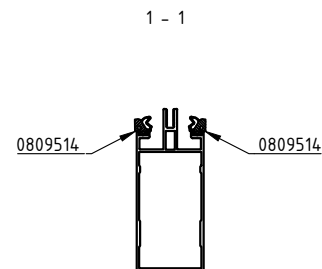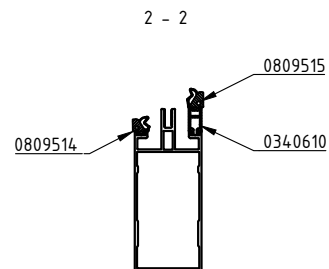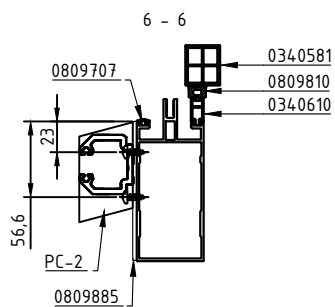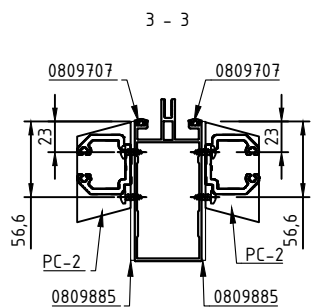

Маркировка:
 К6.В6.С3 – 1 шт.
 К6.В6.С2 – 1 шт (зеркально)
 К6.В11.С4 – 1 шт.
 К6.В11.С3 – 1 шт (зеркально)
 К6.В18.С3 – 1 шт.
 К6.В18.С2 – 1 шт (зеркально)
 К6.В19.С3 – 1 шт.
 К6.В19.С2 – 1 шт (зеркально)

Цвет: 79 7M15

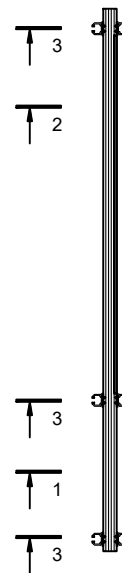

Маркировка:
 К6.В6.С1 – 1 шт. (зеркально)
 К6.В11.С5 – 1 шт
 К6.В18.С1 – 1 шт. (зеркально)
 К6.В19.С4 – 1 шт.
 К6.В19.С1 – 1 шт. (зеркально)

Цвет: 79 7M15



Примечание.

1. Каждую стойку перед производством работ оклеить защитной пленкой, замаркировать номером стойки и укомплектовать уплотнителями и филлистрами
2. Стойки укомплектовать подпятниками из 034.5593 L=150 мм и дренажным лотком 073.8263.04 на винт 050.5029.--
3. Манжету 080.9885 и сухарь PC-2 установить на производстве по шаблону. Манжету подрезать по торцу ригеля.
4. Ригельные сухари PC-1 и PC-2 устанавливать на саморез Ø4,8x13 – 0525330.


Согласовано		
	ГАП	ГИП
Инв. N подл.		
	Подп. и дата	Взам. инв. N

						Остров 2 К1			
						" Многофункциональная комплексная жилая застройка , квартал 2, корпус 1, 2, 3, 4, 5, 6 по адресу : г . Москва , внутригородская территория муниципальный округ Хорошёво –Мнёвники."			
Изм.	Кол.уч.	Лист	№ док.	Подп.	Дата	Светопрзрачные конструкции	Стадия	Лист	Листов
Разраб.	Бирюкова				06.23		Р	103	
Проверил									
Н.контр.						Стойки В12, В13, В14, В15	ООО "МАРКА ПОЛА"		
Т.контр.									
Утв.									


Копировал

Согласовано		
	ГАП	ГИП
Инв. N подл.		
	Подп. и дата	Взам. инв. N






Маркировка:
 К6.В10.С5 – 1 шт. (зеркально)
 К6.В9.С1 – 1 шт.
 К6.В14.С1 – 1 шт.
 К6.В15.С5 – 1 шт. (зеркально)
 Цвет: 79 7М15

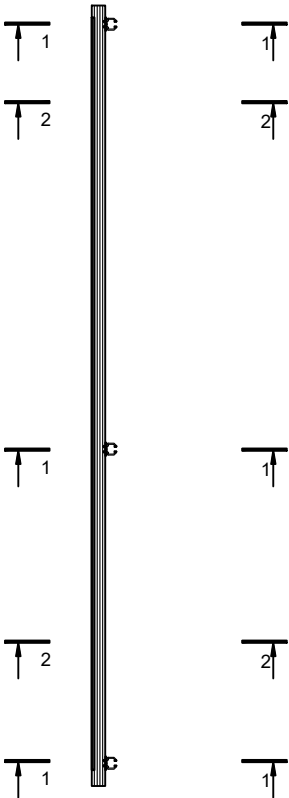

Маркировка:
 К6.В10.С4 – 1 шт. (зеркально)
 К6.В9.С2 – 1 шт.
 К6.В14.С2 – 1 шт.
 Цвет: 79 7М15






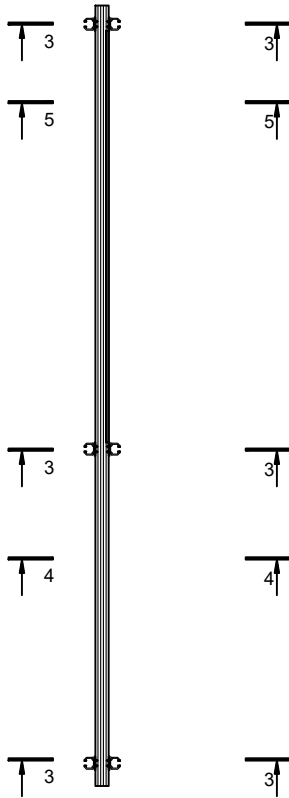


- Примечание.
1. Каждую стойку перед производством работ оклеить защитной пленкой,замаркировать номером стойки и укомплектовать уплотнителями и флистрами
 2. Стойки укомплектовать подпятниками из 034.5593 L=150 мм и дренажным лотком 073.8263.04 на винт 050.5029.--
 3. Манжету 080.9885 и сухарь РС-2 установить на производсве по шаблону. Манжету подрезать по торцу ригеля.
 4. Ригельные сухари РС-1 и РС-2 устанавливать на саморез Ø4,8x13 – 0525330.

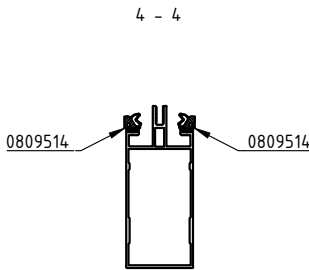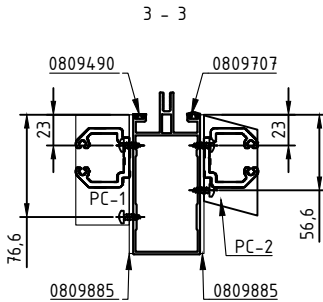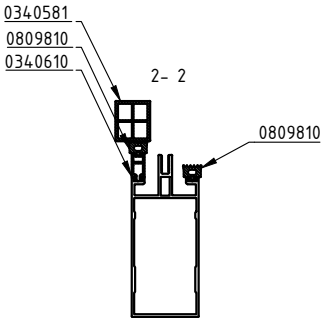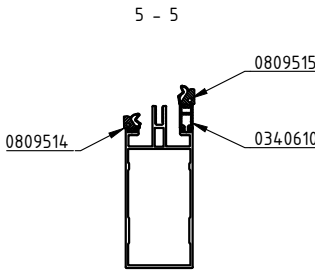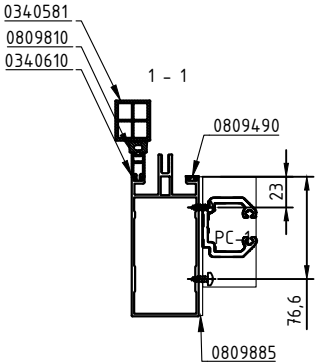

Остров 2 К1						
" Многофункциональная комплексная жилая застройка , квартал 2, корпус 1, 2, 3, 4, 5, 6 по адресу : г . Москва , внутригородская территория муниципальный округ Хорошёво –Мнёвники."						
Изм.	Кол.уч.	Лист	№ док.	Подп.	Дата	
Разраб.	Бирюкова		06.23			
Проверил						
Н. контр.						
Т. контр.						
Утв.						
Стойки В12, В13, В14, В15						000 "МАРКА ПОЛА"



Согласовано			Взам. инв. №	Подп. и дата	Инв. № подл.
	ГАП				
ГИП					

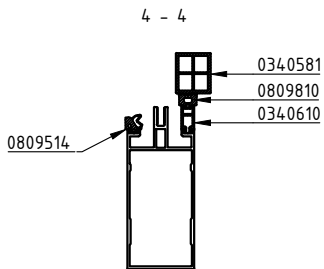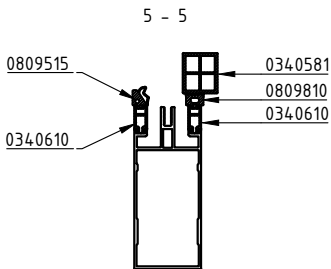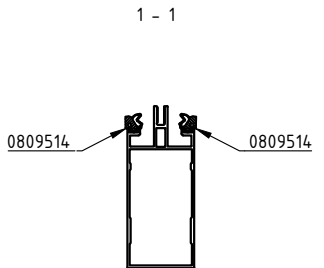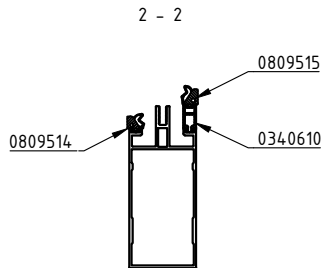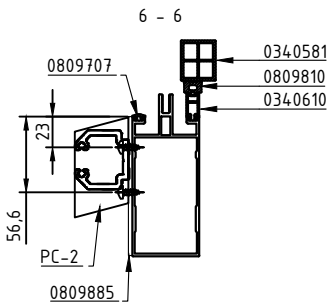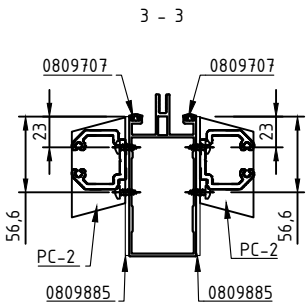

Маркировка:
 К6.В9.С4 – 1 шт.
 К6.В9.С3 – 1 шт. (зеркально)
 К6.В10.С3 – 1 шт.
 К6.В10.С2 – 1 шт. (зеркально)
 К6.В14.С4 – 1 шт.
 К6.В14.С3 – 1 шт. (зеркально)
 К6.В15.С3 – 1 шт.
 К6.В15.С2 – 1 шт. (зеркально)

Цвет: 79 7М15

Маркировка:
 К6.В10.С1 – 1 шт. (зеркально)
 К6.В9.С5 – 1 шт.
 К6.В10.С5 – 1 шт.
 К6.В15.С1 – 1 шт. (зеркально)
 Цвет: 79 7М15

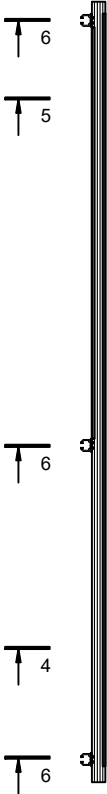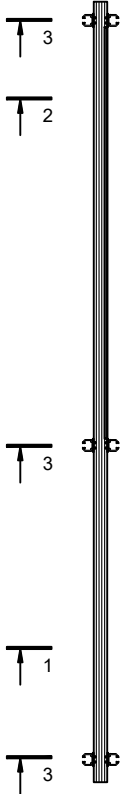

Примечание.
 1. Каждую стойку перед производством работ оклеить защитной пленкой, замаркировать номером стойки и укомплектовать уплотнителями и филлистрами
 2. Стойки укомплектовать подпятниками из 034.5593 L=150 мм и дренажным лотком 073.8263.04 на винт 050.5029.--
 3. Манжету 080.9885 и сухарь РС-2 установить на производстве по шаблону. Манжету подрезать по торцу ригеля.
 4. Ригельные сухари РС-1 и РС-2 устанавливать на саморез Ø4,8x13 – 0525330.

						Остров 2 К1		
						" Многофункциональная комплексная жилая застройка , квартал 2, корпус 1, 2, 3, 4, 5, 6 по адресу : г . Москва , внутригородская территория муниципальный округ Хорошёво –Мнёвники."		
Изм.	Кол.уч.	Лист	№ док.	Подп.	Дата	Светопрзрачные конструкции	Стадия	Лист
Разраб.	Бирюкова				06.23		Р	105
Проверил								
Н.контр.						Стойки В12, В13, В14, В15		ООО "МАРКА ПОЛА"
Т.контр.								
Утв.								

Копировал

Маркировка:
К6.В15.54 - 1 шт.

Цвет: 79 7М15


Маркировка:
К6.В15.56 - 1 шт.

Цвет: 79 7М15


Маркировка:
К6.В9.56 - 1 шт.

Цвет: 79 7М15



6* - 6*

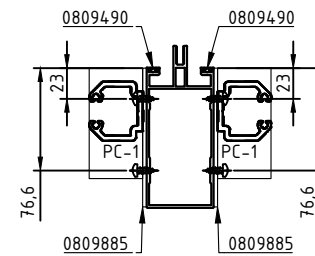

6 - 6

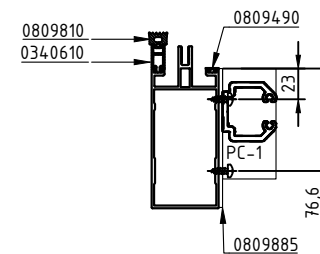


7 - 7

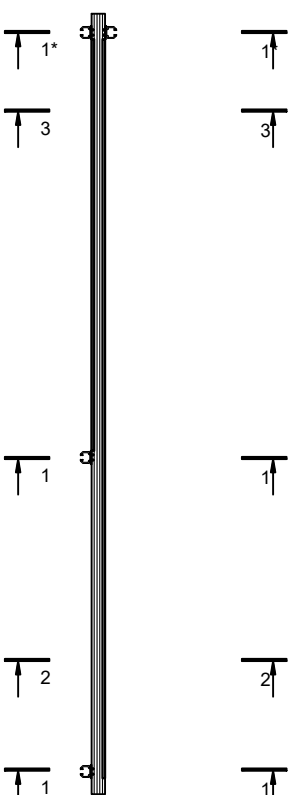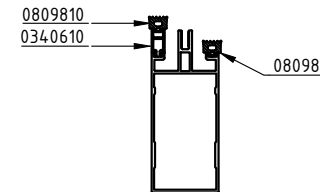



1 - 1

1* - 1*

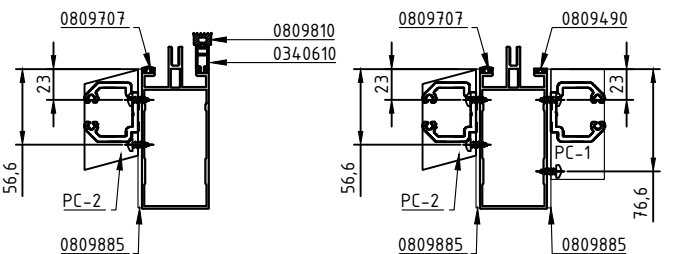


2 - 2

3 - 3

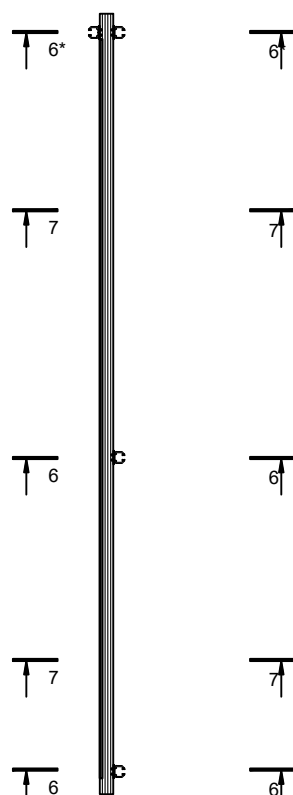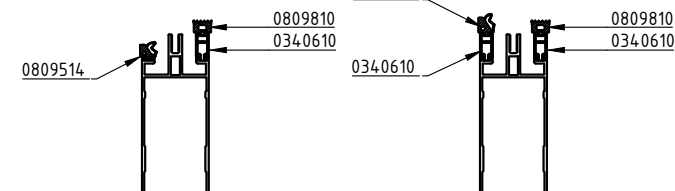

8 - 8

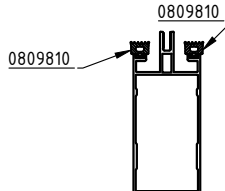


Примечание.

1. Каждую стойку перед производством работ оклеить защитной пленкой, замаркировать номером стойки и укомплектовать уплотнителями и флистрами
2. Стойки укомплектовать подпятниками из 034.5593 L=150 мм и дренажным лотком 073.8263.04 на винт 050.5029.--
3. Манжету 080.9885 и сухарь PC-2 установить на производстве по шаблону. Манжету подрезать по торцу ригеля.
4. Ригельные сухари PC-1 и PC-2 устанавливать на саморез Ø4,8x13 - 0525330.


						Остров 2 К1			
						" Многофункциональная комплексная жилая застройка , квартал 2, корпус 1, 2, 3, 4, 5, 6 по адресу : г . Москва , внутригородская территория муниципальный округ Хорошёво - Мнёвники."			
Изм.	Кол.уч.	Лист	№ док.	Подп.	Дата	Светопрозрачные конструкции	Стадия	Лист	Листов
Разраб.	Бирякова				06.23		Р	106	
Проверил									
Н.контр.						000 "МАРКА ПОЛА"			
Т.контр.									
Утв.									

Копировал

Профиль ригеля 0343524
Цвет: 79 7M15

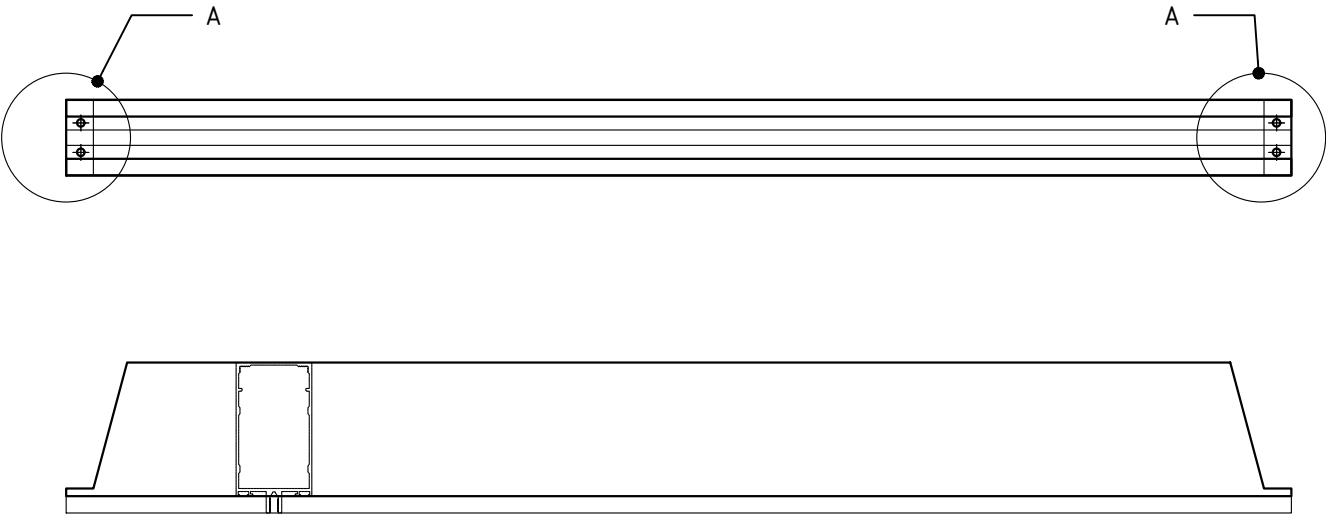


Маркировка		L, мм	Кол-во
K6.B1.R1		779,2	36
K6.B2.R1		763,2	36
K6.B5.R1		830,2	26
K6.B16.R1		823,2	26
K6.B7.R1		727,2	2
K6.B8.R1		779,2	2
K6.B13.R1		758,2	2
K6.B6.R1		779,2	2
K6.B11.R1		830,2	2
K6.B18.R1		823,2	2
K6.B19.R1		763,2	2
K6.B9.R1		758,2	2
K6.B10.R1		758,2	2
K6.B14.R1		758,2	2
K6.B3.R1		823,2	2
K6.B4.R1		830,2	10
K6.B17.R1		823,2	8
K6.B12.R1		758,2	2
K6.B15.R1		758,2	2

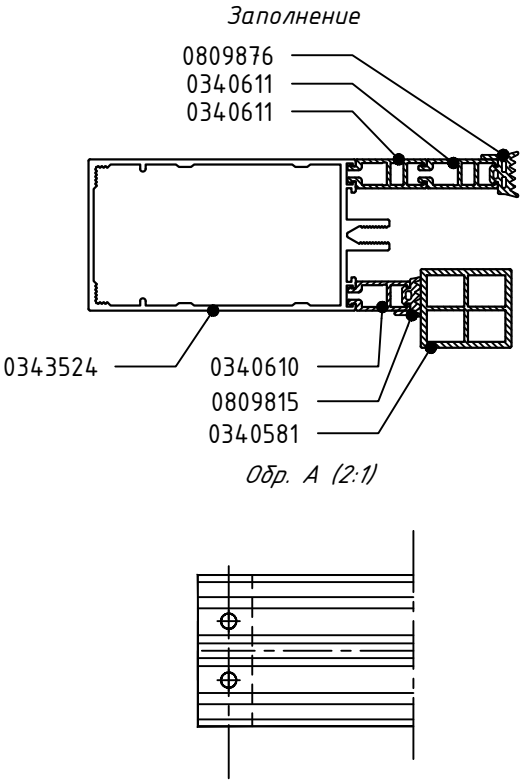


Примечание.
1. Каждый ригель перед производством работ оклеить защитной пленкой, замаркировать номером стойки и укомплектовать уплотнителями и флистрами

Согласовано	
-------------	--	--	

Профиль ригеля 0343524
Цвет: 79 7M15

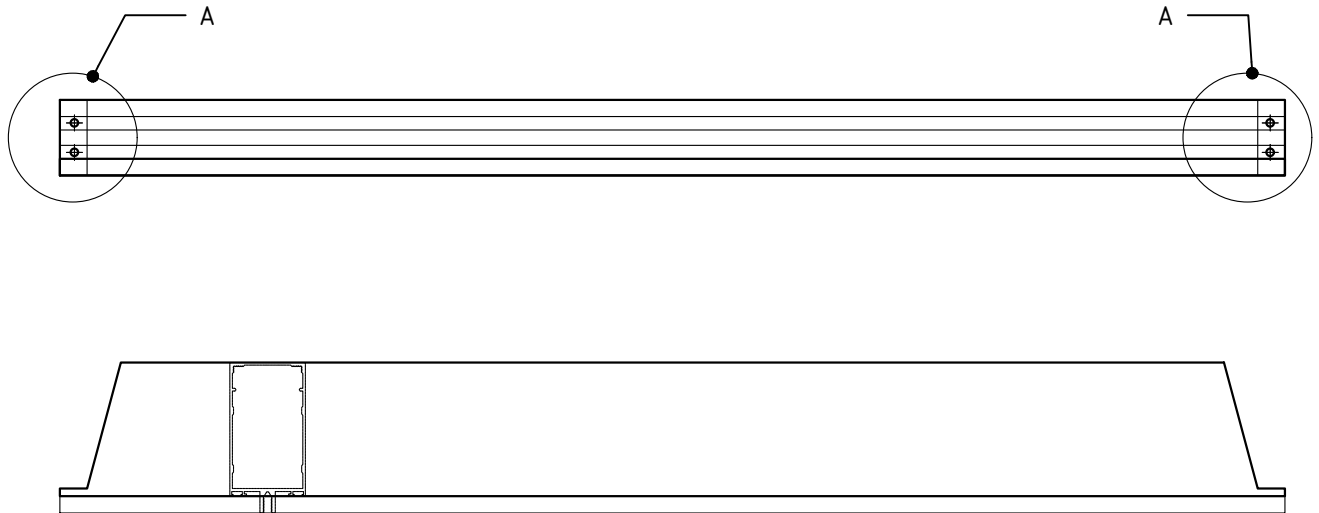


Маркировка		L, мм	Кол-во
K6.B1.R2		779,2	72
K6.B2.R2		763,2	72
K6.B5.R2		830,2	52
K6.B16.R2		823,2	52
K6.B7.R2		727,2	4
K6.B8.R2		779,2	4
K6.B13.R2		758,2	4
K6.B6.R2		779,2	4
K6.B11.R2		830,2	4
K6.B18.R2		823,2	4
K6.B19.R2		763,2	4
K6.B9.R2		758,2	4
K6.B10.R2		758,2	4
K6.B14.R2		758,2	4
K6.B3.R2		823,2	4
K6.B4.R2		830,2	20
K6.B17.R2		823,2	16
K6.B12.R2		758,2	4
K6.B15.R2		758,2	4

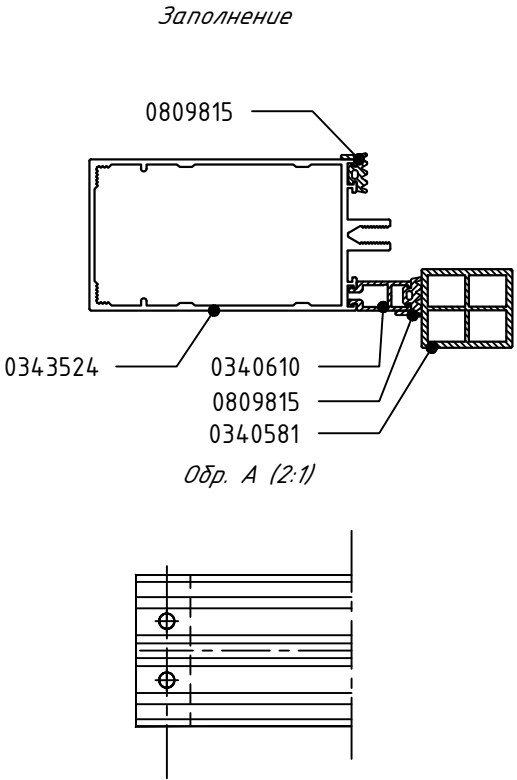


Примечание.
1. Каждый ригель перед производством работ оклеить защитной пленкой, замаркировать номером стойки и укомплектовать уплотнителями и флистрами

Согласовано	</
-------------	--	--	----


Профиль ригеля 0343524
Цвет: 79 7M15

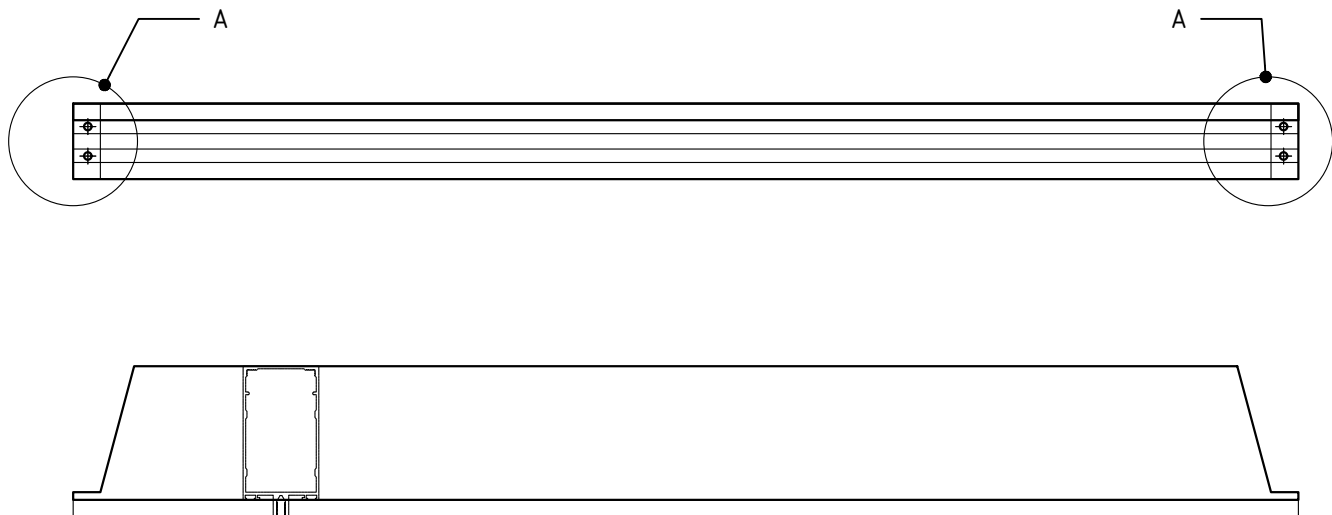

Маркировка		L, мм	Кол-во
K6.B1.R3		779,2	36
K6.B2.R3		763,2	36
K6.B5.R3		830,2	26
K6.B16.R3		823,2	26
K6.B7.R3		727,2	2
K6.B8.R3		779,2	2
K6.B13.R3		758,2	2
K6.B6.R3		779,2	2
K6.B11.R3		830,2	2
K6.B18.R3		823,2	2
K6.B19.R3		763,2	2
K6.B9.R3		758,2	2
K6.B10.R3		758,2	2
K6.B14.R3		758,2	2
K6.B3.R3		823,2	2
K6.B4.R3		830,2	10
K6.B17.R3		823,2	8
K6.B12.R3		758,2	2
K6.B15.R3		758,2	2

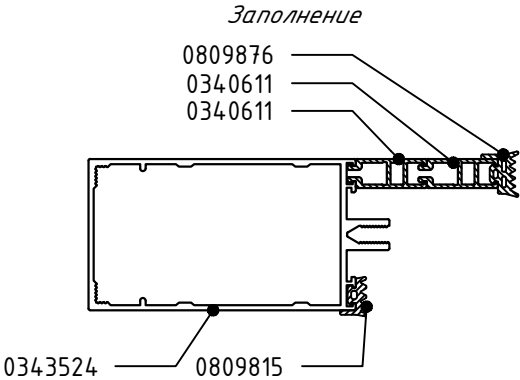


Одр. А (2:1)

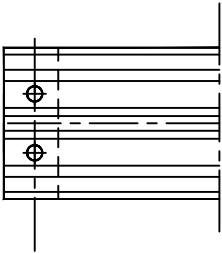

Примечание.
1. Каждый ригель перед производством работ оклеить защитной пленкой, замаркировать номером стойки и укомплектовать уплотнителями и флистрами


Согласовано	
-------------	--	--	

Профиль ризеля 0343524
Цвет: 79 7M15

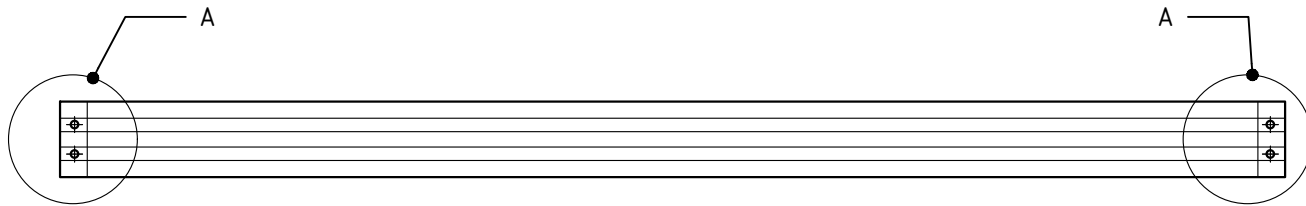


Маркировка		L, мм	Кол-во
K6.B1.R4		779,2	18
K6.B2.R4		763,2	18
K6.B5.R4		830,2	13
K6.B16.R4		823,2	13
K6.B7.R4		727,2	1
K6.B8.R4		779,2	1
K6.B13.R4		758,2	1
K6.B6.R4		779,2	1
K6.B11.R4		830,2	1
K6.B18.R4		823,2	1
K6.B19.R4		763,2	1
K6.B9.R4		758,2	1
K6.B10.R4		758,2	1
K6.B14.R4		758,2	1
K6.B3.R4		823,2	1
K6.B4.R4		830,2	5
K6.B17.R4		823,2	4
K6.B12.R4		758,2	1
K6.B15.R4		758,2	1

Заполнение

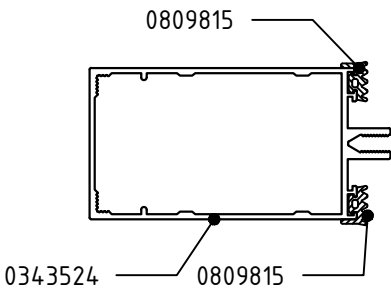

Одр. А (2:1)


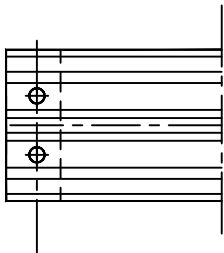


Примечание.
1. Каждый ризель перед производством работ оклеить защитной пленкой, замаркировать номером стойки и укомплектовать уплотнителями и флистрами


Согласовано					
	ГАП	ГИП			
Взам. инв. №					
Подп. и дата					
Инв. № подл.					

						Остров 2 К1			
						" Многофункциональная комплексная жилая застройка , квартал 2, корпус 1, 2, 3, 4, 5, 6 по адресу : г . Москва , внутригородская территория муниципальный округ Хорошёво –Мнёвники."			
Изм.	Кол.уч.	Лист	№ док.	Подп.	Дата	Светопрозрачные конструкции	Стадия	Лист	Листов
Разраб.	Бирюкова				06.23		Р	110	
Проверил									
Н.контр.									
Т.контр.						Ризели	ООО "МАРКА ПОЛА"		
Утв.									


Профиль ригеля 0343525
Цвет: 79 7M15

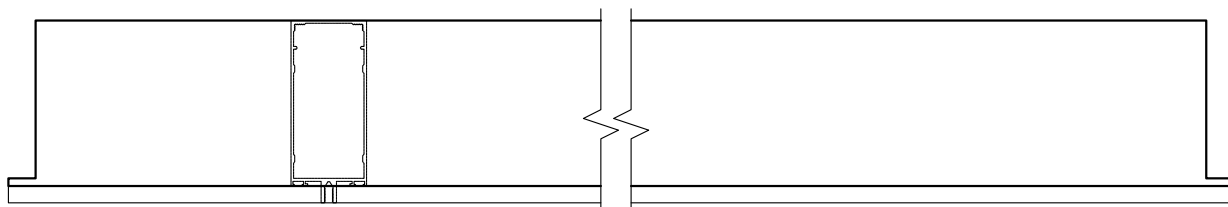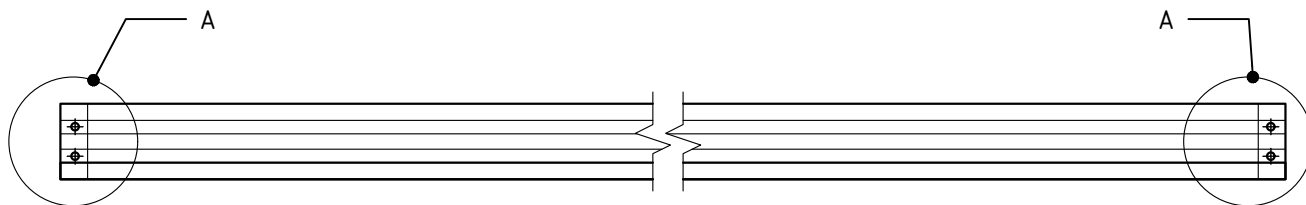

Маркировка	L, мм	Кол-во
K6.B1.R5	1570,0	36
K6.B2.R5	1520,0	36
K6.B5.R5	1055,0	52
K6.B16.R5	1040,0	26
K6.B16.R7	1045,0	26
K6.B7.R5	1295,0	2
K6.B7.R7	1510,0	2
K6.B8.R5	1650,0	2
K6.B13.R5	1690,0	2
K6.B6.R5	1570,0	2
K6.B11.R5	1055,0	4
K6.B18.R5	1040,0	2
K6.B18.R7	1045,0	2
K6.B9.R5	1235,0	2
K6.B9.R7	1395,0	2
K6.B10.R5	1240,0	2
K6.B14.R5	1570,0	2
K6.B17.R7	1040,0	8
K6.B12.R7	1160,0	2
K6.B15.R7	670,0	2

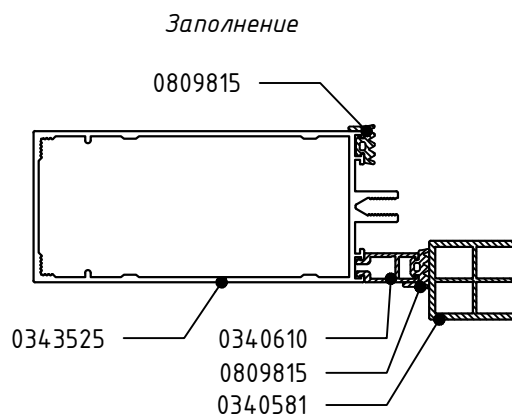

Обр. А (2:1)

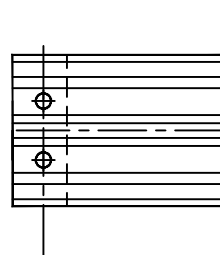

Примечание.


1. Каждый ригель перед производством работ оклеить защитной пленкой, замаркировать номером стойки и укомплектовать уплотнителями и филлистами

Согласовано	ГАП	ГИП
Взам. инв. №		
Подп. и дата		
Инв. № подл.		


						Остров 2 К1			
						“ Многофункциональная комплексная жилая застройка , квартал 2, корпус 1, 2, 3, 4, 5, 6 по адресу : г . Москва , внутригородская территория муниципальный округ Хорошёво –Мнёвники.”			
Изм.	Кол.уч.	Лист	№ док.	Подп.	Дата	Светопрозрачные конструкции	Стадия	Лист	Листов
Разраб.	Бирюкова				06.23		Р	111	
Проверил									
Н.контр.									
Т.контр.						Ригели	ООО “МАРКА ПОЛА”		
Утв.									

Копировал


Профиль ригеля 0343525
Цвет: 79 7M15

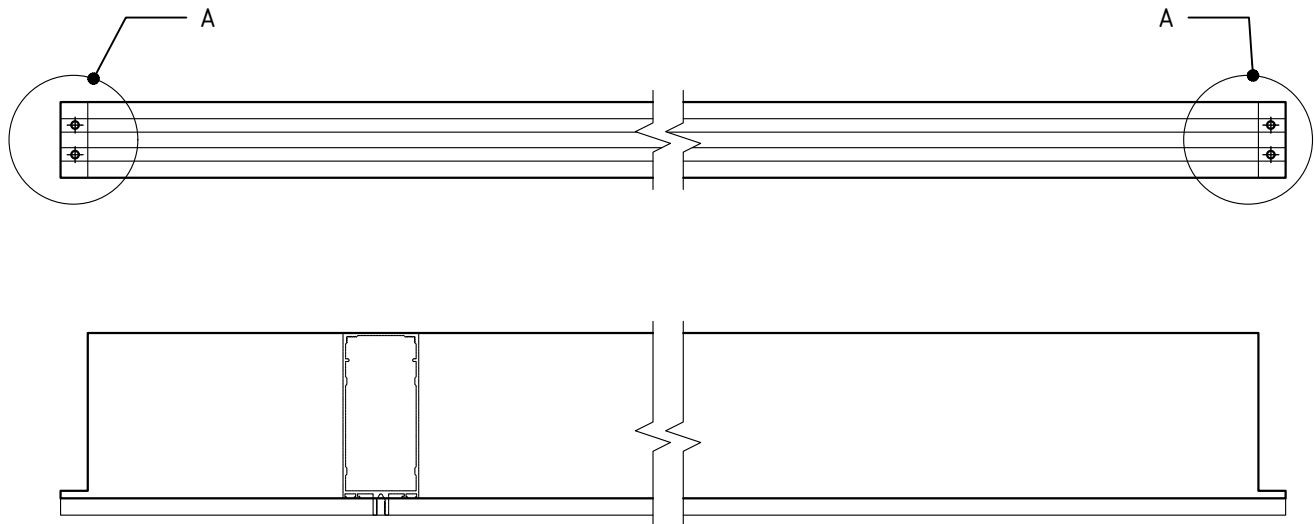

Маркировка	L, мм	Кол-во
K6.B1.R6	1570,0	18
K6.B2.R6	1520,0	18
K6.B5.R6	1055,0	26
K6.B16.R6	1040,0	13
K6.B16.R8	1045,0	13
K6.B7.R6	1295,0	1
K6.B7.R8	1510,0	1
K6.B8.R6	1650,0	1
K6.B13.R6	1690,0	1
K6.B6.R6	1570,0	1
K6.B11.R6	1055,0	2
K6.B18.R6	1040,0	1
K6.B18.R8	1045,0	1
K6.B9.R6	1235,0	1
K6.B9.R8	1395,0	1
K6.B10.R6	1240,0	1
K6.B14.R6	1570,0	1
K6.B17.R8	1040,0	4
K6.B12.R8	1160,0	1
K6.B15.R8	670,0	1

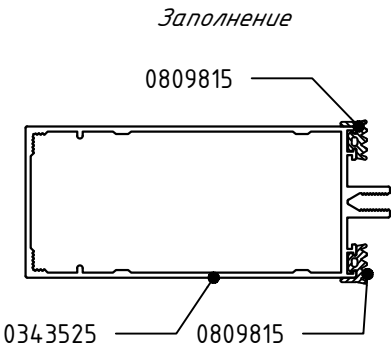


Одр. А (2:1)

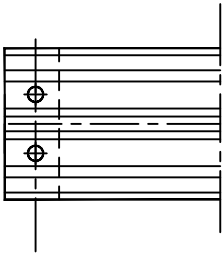

Примечание.
1. Каждый ригель перед производством работ оклеить защитной пленкой, замаркировать номером стойки и укомплектовать уплотнителями и филлистами


Согласовано	ГАП	ГИП								
	Взам. инв. №	Подп. и дата								
Инв. № подл.	Изм.	Кол.уч.	Лист	№ док.	Подп.	Дата	Остров 2 К1			
	Разраб.	Бирюкова				06.23	" Многофункциональная комплексная жилая застройка , квартал 2, корпус 1, 2, 3, 4, 5, 6 по адресу : г . Москва , внутригородская территория муниципального округа Хорошёво –Мнёвники."			
Инв. № подл.	Проверил						Светопрозрачные конструкции	Стадия	Лист	Листов
	Н.контр.							Р	112	
	Т.контр.							Ригели		
Утв.							ООО "МАРКА ПОЛА"			

Профиль ригеля 0343525
Цвет: 79 7M15

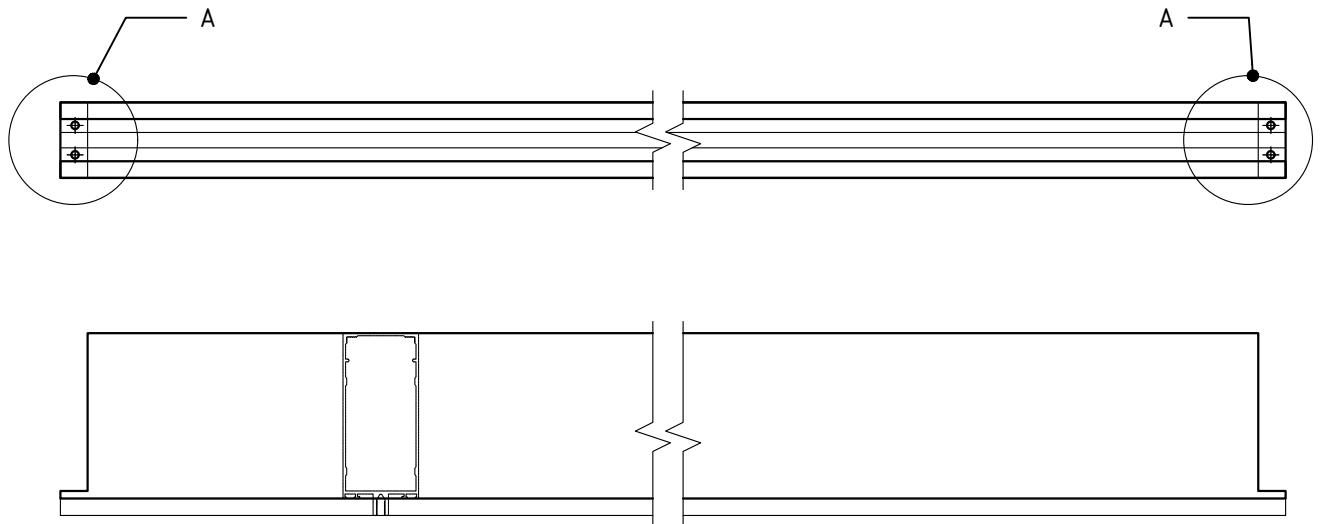


Маркировка	L, мм	Кол-во
K6.B9.R5	2105,0	1
K6.B4.R5	2130,0	5
K6.B17.R5	1045,0	4
K6.B12.R5	1580,0	1
K6.B15.R5	1580,0	1

Заполнение

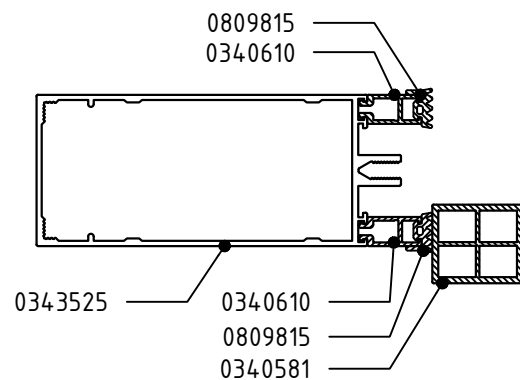

Обр. А (2:1)

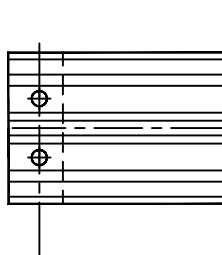

Примечание.


1. Каждый ригель перед производством работ оклеить защитной пленкой, замаркировать номером стойки и укомплектовать уплотнителями и флистрами

Согласовано				
	ГАП	ГИП		
Взам. инв. №				
Подп. и дата				
Инв. № подл.				

						Остров 2 К1		
						" Многофункциональная комплексная жилая застройка , квартал 2, корпус 1, 2, 3, 4, 5, 6 по адресу : г . Москва , внутригородская территория муниципальный округ Хорошёво –Мнёвники."		
Изм.	Кол.уч.	Лист	№ док.	Подп.	Дата	Светопрозрачные конструкции	Стадия	Лист
Разраб.	Бирюкова				06.23		Р	113
Проверил						Ригели	ООО "МАРКА ПОЛА"	
Н.контр.								
Т.контр.								
Утв.								

Копировал

Прижимная планка стойки
Цвет: без покраски

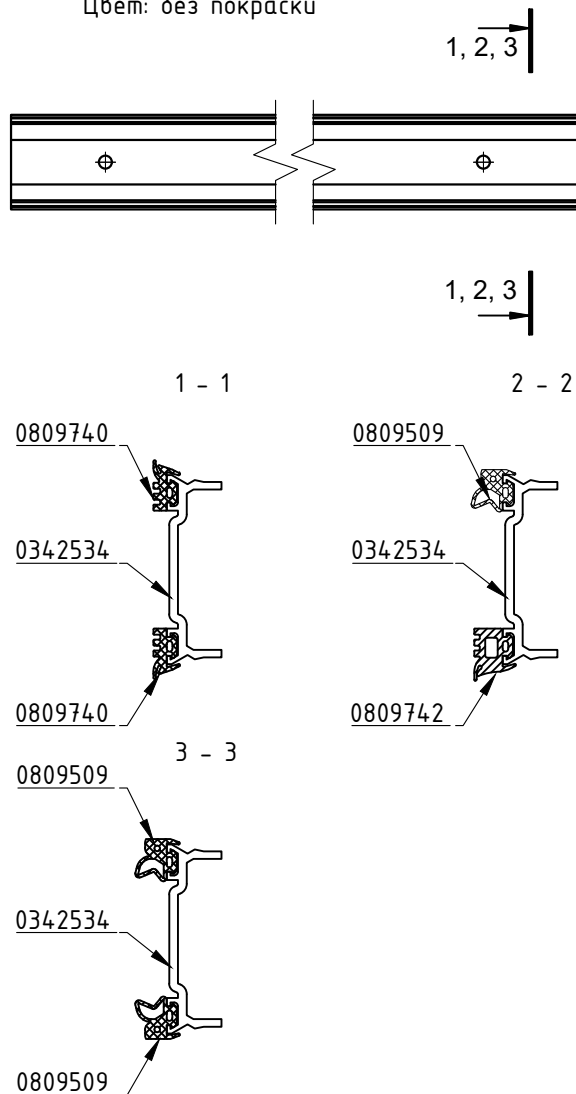

Маркировка	№ Сечения	L, мм	Кол-во
K6.B1.PS1	2 - 2	2615,0	36
K6.B1.PS2	3 - 3	2615,0	36
K6.B1.PS3	1 - 1	2615,0	18
K6.B2.PS1	2 - 2	2615,0	36
K6.B2.PS2	3 - 3	2615,0	36
K6.B2.PS3	1 - 1	2615,0	18
K6.B5.PS1	2 - 2	2615,0	26
K6.B5.PS2	3 - 3	2615,0	26
K6.B5.PS3	1 - 1	2615,0	26
K6.B16.PS1	2 - 2	2615,0	26
K6.B16.PS2	3 - 3	2615,0	26
K6.B16.PS3	1 - 1	2615,0	26
K6.B7.PS1	2 - 2	2615,0	2
K6.B7.PS2	3 - 3	2615,0	2
K6.B7.PS3	1 - 1	2615,0	2
K6.B8.PS1	2 - 2	2615,0	2
K6.B8.PS2	3 - 3	2615,0	2
K6.B8.PS3	1 - 1	2615,0	1
K6.B13.PS1	2 - 2	2615,0	2
K6.B13.PS2	3 - 3	2615,0	2
K6.B13.PS3	1 - 1	2615,0	1
K6.B6.PS1	2 - 2	1960,0	2
K6.B6.PS2	3 - 3	1960,0	2
K6.B6.PS3	1 - 1	1960,0	1
K6.B11.PS1	2 - 2	1960,0	2
K6.B11.PS2	3 - 3	1960,0	2
K6.B11.PS3	1 - 1	1960,0	2
K6.B18.PS1	2 - 2	1960,0	2
K6.B18.PS2	3 - 3	1960,0	2
K6.B18.PS3	1 - 1	1960,0	2
K6.B19.PS1	2 - 2	1960,0	2
K6.B19.PS2	3 - 3	1960,0	2
K6.B9.PS1	2 - 2	2815,0	2
K6.B9.PS2	3 - 3	2815,0	2
K6.B9.PS3	1 - 1	2815,0	2
K6.B10.PS1	2 - 2	2815,0	2
K6.B10.PS2	3 - 3	2815,0	2
K6.B10.PS3	1 - 1	2815,0	1
K6.B14.PS1	2 - 2	2815,0	2
K6.B14.PS2	3 - 3	2815,0	2
K6.B14.PS3	1 - 1	2815,0	1
K6.B3.PS1	2 - 2	2615,0	2
K6.B3.PS2	3 - 3	2615,0	2
K6.B3.PS3	1 - 1	2615,0	1
K6.B4.PS1	2 - 2	2615,0	10
K6.B4.PS2	3 - 3	2615,0	10
K6.B4.PS3	1 - 1	2615,0	5
K6.B17.PS1	2 - 2	2615,0	8
K6.B17.PS2	3 - 3	2615,0	8
K6.B17.PS3	1 - 1	2615,0	8

Маркировка	№ Сечения	L, мм	Кол-во
K6.B12.PS1	2 - 2	2615,0	2
K6.B12.PS2	3 - 3	2615,0	2
K6.B12.PS3	1 - 1	2615,0	2
K6.B15.PS1	2 - 2	2815,0	2
K6.B15.PS2	3 - 3	2815,0	2
K6.B15.PS3	1 - 1	2815,0	2

Инв. N подл.	Подп. и дата	Взам. инв. N	Согласовано		
			ГАП		
			ГИП		

Остров 2 К1

" Многофункциональная комплексная жилая застройка , квартал 2, корпус 1, 2, 3, 4, 5, 6 по адресу : г . Москва , внутригородская территория муниципальный округ Хорошёво -Мнёвники."


Светопрозрачные конструкции

Прижим и крышка стойки


Стадия	Лист	Листов
Р	114	

ООО "МАРКА ПОЛА"

Крышка стойки
Цвет: 79 9M05

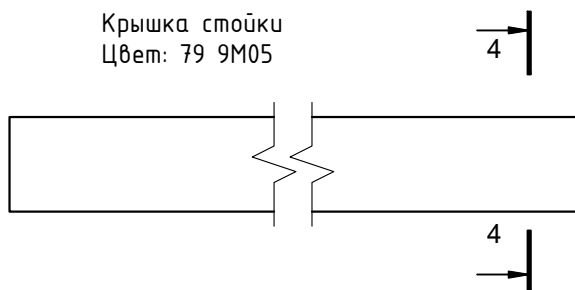



4 - 4

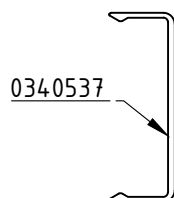

Маркировка		L, мм	Кол-во
K6.B1.KS1		2615,0	90
K6.B2.KS1		2615,0	90
K6.B5.KS1		2615,0	78
K6.B16.KS1		2615,0	78
K6.B7.KS1		2615,0	6
K6.B8.KS1		2615,0	5
K6.B13.KS1		2615,0	5
K6.B6.KS1		1960,0	5
K6.B11.KS1		1960,0	6
K6.B18.KS1		1960,0	6
K6.B19.KS1		1960,0	4
K6.B9.KS1		2815,0	6
K6.B10.KS1		2815,0	5
K6.B14.KS1		2815,0	5
K6.B3.KS1		2615,0	5
K6.B4.KS1		2615,0	25
K6.B17.KS1		2615,0	24
K6.B12.KS1		2615,0	6
K6.B15.KS1		2815,0	6

Согласовано	ГАП		Взам. инв. №		Подп. и дата		Изм.	Кол.уч.	Лист	№ док.	Подп.	Дата	Остров 2 К1				
	ГИП			" Многофункциональная комплексная жилая застройка , квартал 2, корпус 1, 2, 3, 4, 5, 6 по адресу : г . Москва , внутригородская территория муниципальный округ Хорошево -Мневники."													
Инв. № подл.	Проверил													Светопрзрачные конструкции	Стадия	Лист	Листов
	Н.контр.														Р	115	
	Т.контр.													Крышка стойки	ООО "МАРКА ПОЛА"		
	Утв.																


Прижимная планка ригели
Цвет: без покраски

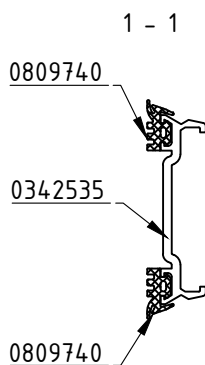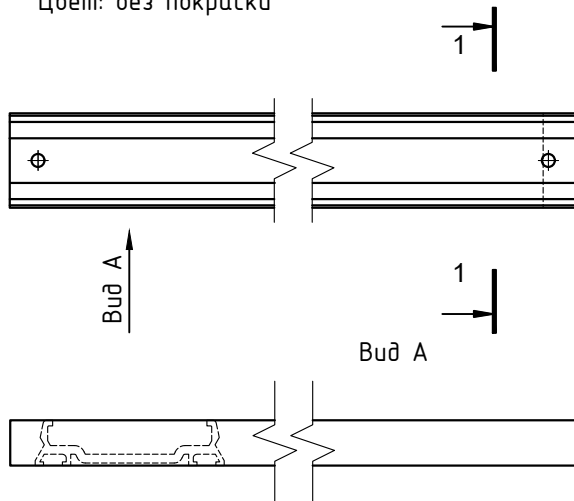


Маркировка		L, мм	Кол-во
K6.B1.PR1		779,0	162
K6.B1.PR2		1536,0	54
K6.B2.PR1		763,0	162
K6.B2.PR2		1486,0	54
K6.B5.PR1		830,0	117
K6.B5.PR2		1021,0	78
K6.B16.PR1		823,0	117
K6.B16.PR2		1006,0	39
K6.B16.PR3		1011,0	39
K6.B7.PR1		727,0	9
K6.B7.PR2		1261,0	3
K6.B7.PR3		1481,0	3
K6.B8.PR1		779,0	9
K6.B8.PR2		1616,0	3
K6.B13.PR1		758,0	9
K6.B13.PR2		1656,0	3
K6.B6.PR1		779,0	9
K6.B6.PR2		1536,0	3
K6.B11.PR1		830,0	9
K6.B11.PR2		1021,0	6
K6.B18.PR1		823,0	9
K6.B18.PR2		1006,0	3
K6.B18.PR3		1011,0	3
K6.B19.PR1		763,0	9
K6.B9.PR1		758,0	9
K6.B9.PR2		1201,0	3
K6.B9.PR3		1361,0	3
K6.B10.PR1		758,0	9
K6.B10.PR2		1206,0	3
K6.B14.PR1		758,0	9
K6.B14.PR2		1536,0	3
K6.B3.PR1		823,0	9
K6.B3.PR2		2071,0	1
K6.B4.PR1		830,0	45
K6.B4.PR2		2096,0	5
K6.B17.PR1		823,0	36
K6.B17.PR2		1011,0	4
K6.B17.PR3		1006,0	12
K6.B12.PR1		758,0	9
K6.B12.PR2		1546,0	1
K6.B12.PR3		1126,0	3
K6.B15.PR1		758,0	9
K6.B15.PR2		1546,0	1
K6.B15.PR3		636,0	3

Согласовано	ГАП	ГИП	Взам. инв. №	Подп. и дата	Инв. № подл.	Изм.	Кол.уч.	Лист	№ док.	Подп.	Дата	Остров 2 К1			
	" Многофункциональная комплексная жилая застройка , квартал 2, корпус 1, 2, 3, 4, 5, 6 по адресу : г . Москва , внутригородская территория муниципальный округ Хорошёво -Мнёвники."														
Инв. № подл.	Разраб.	Бирюкова		06.23	Светопрозрачные конструкции	Стадия	Лист	Листов							
	Проверил					Р	116								
	Н.контр.					000 "МАРКА ПОЛА"									
	Т.контр.														
Утв.															

Крышка ригеля
Цвет: 79 9M05

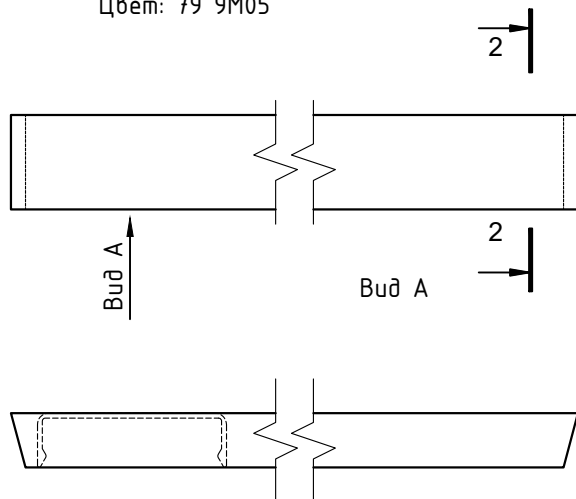

2 - 2

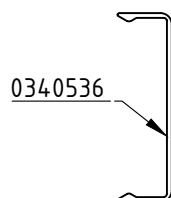





! ---.---.KR2 и ---.---.KR3 прямые, без углов запила

Маркировка		L, мм	Кол-во
K6.B1.KR1		789,6	162
K6.B1.KR2	ПРЯМАЯ	1538,0	54
K6.B2.KR1		773,6	162
K6.B2.KR2	ПРЯМАЯ	1488,0	54
K6.B5.KR1		840,6	117
K6.B5.KR2	ПРЯМАЯ	1023,0	78
K6.B16.KR1		833,6	117
K6.B16.KR2	ПРЯМАЯ	1008,0	39
K6.B16.KR3	ПРЯМАЯ	1013,0	39
K6.B7.KR1		737,6	9
K6.B7.KR2	ПРЯМАЯ	1262,0	3
K6.B7.KR3	ПРЯМАЯ	1483,0	3
K6.B8.KR1		789,6	9
K6.B8.KR2	ПРЯМАЯ	1618,0	3
K6.B13.KR1		768,6	9
K6.B13.KR2	ПРЯМАЯ	1658,0	3
K6.B6.KR1		789,6	9
K6.B6.KR2	ПРЯМАЯ	1538,0	3
K6.B11.KR1		840,6	9
K6.B11.KR2	ПРЯМАЯ	1023,0	6
K6.B18.KR1		833,6	9
K6.B18.KR2	ПРЯМАЯ	1008,0	3
K6.B18.KR3	ПРЯМАЯ	1013,0	3
K6.B19.KR1		773,6	9
K6.B9.KR1		768,6	9
K6.B9.KR2	ПРЯМАЯ	1203,0	3
K6.B9.KR3	ПРЯМАЯ	1363,0	3
K6.B10.KR1		768,6	9
K6.B10.KR2	ПРЯМАЯ	1208,0	3
K6.B14.KR1		768,6	9
K6.B14.KR2	ПРЯМАЯ	1538,0	3
K6.B3.KR1		833,6	9
K6.B3.KR2	ПРЯМАЯ	2073,0	1
K6.B4.KR1		840,6	45
K6.B4.KR2	ПРЯМАЯ	2098,0	5
K6.B17.KR1		833,6	36
K6.B17.KR2	ПРЯМАЯ	1013,0	4
K6.B17.KR3	ПРЯМАЯ	1008,0	12
K6.B12.KR1		768,6	9
K6.B12.KR2	ПРЯМАЯ	1548,0	1
K6.B12.KR3	ПРЯМАЯ	1128,0	3
K6.B15.KR1		768,6	9
K6.B15.KR2	ПРЯМАЯ	1548,0	1
K6.B15.KR3	ПРЯМАЯ	638,0	3

Согласовано	ГАП	ГИП
	Взам. инв. №	Подп. и дата
Инв. № подл.	Изм.	Кол.уч.
	Разраб.	Бирюкова
	Проверил	
	Н.контр.	
	Т.контр.	
	Утв.	


Остров 2 К1					
" Многофункциональная комплексная жилая застройка , квартал 2, корпус 1, 2, 3, 4, 5, 6 по адресу : г . Москва , внутригородская территория муниципальный округ Хорошёво -Мнёвники."					
Изм.	Кол.уч.	Лист	№ док.	Подп.	Дата
Разраб.	Бирюкова				06.23
Проверил					
Н.контр.					
Т.контр.					
Утв.					
Светопрозрачные конструкции			Стадия	Лист	Листов
			P	117	
Крышка ригеля			ООО "МАРКА ПОЛА"		

Обработка ригельных прижимов и крышек

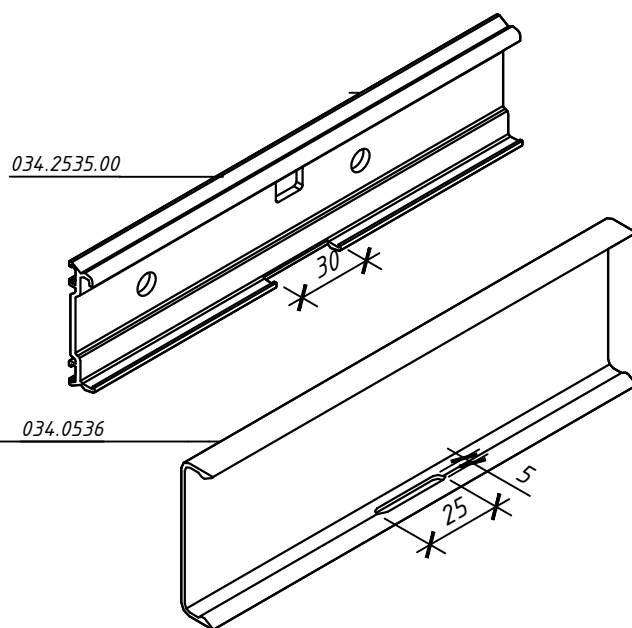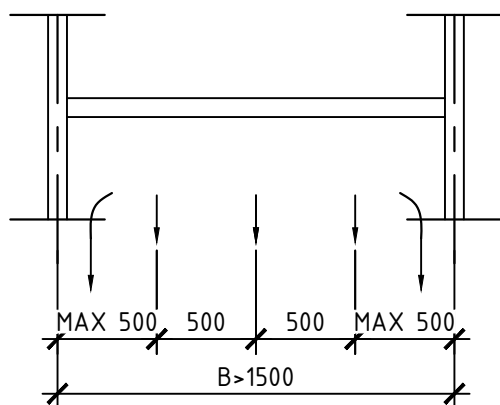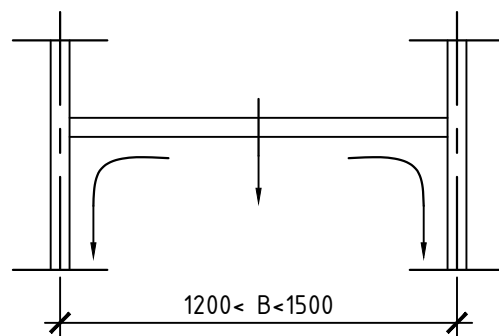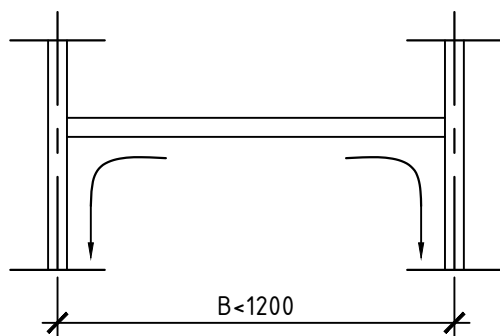


Согласовано		Взам. инв. №		Подп. и дата								Остров 2 К1												
		ГАП																						
		ГИП																						
Инв. № подл.	Изм.	Кол.уч.	Лист	№ док.	Подп.	Дата	" Многофункциональная комплексная жилая застройка , квартал 2, корпус 1, 2, 3, 4, 5, 6 по адресу : г . Москва , внутригородская территория муниципальный округ Хорошёво -Мнёвники."																	
Инв. № подл.							Разраб.						Бирюкова						Стадия		Лист		Листов	
							Проверил												Р		118			
							Н.контр.																	
							Т.контр.												ООО "МАРКА ПОЛА"					
							Утв.																	

Профиль 0341511

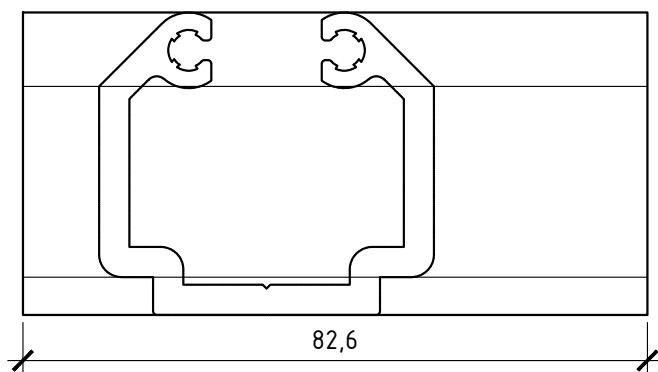

РС-1 – 492 шт.

Профиль 0341511

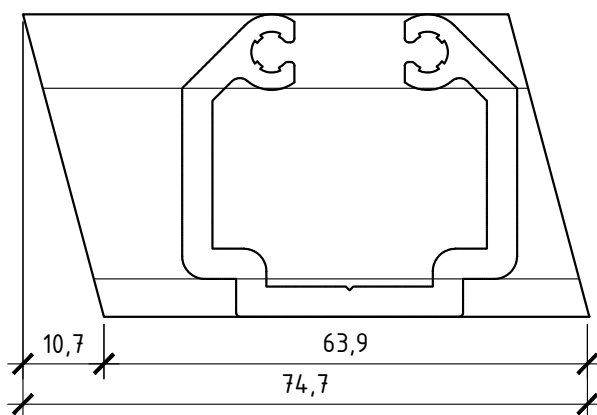


РС-2 – 1476 шт.

Согласовано					
	ГАП	ГИП			
Взам. инв. №					
Подп. и дата					
Инв. № подл.					

						Остров 2 К1			
						“ Многофункциональная комплексная жилая застройка , квартал 2, корпус 1, 2, 3, 4, 5, 6 по адресу : г . Москва , внутригородская территория муниципальный округ Хорошёво –Мнёвники.”			
Изм.	Кол.уч.	Лист	№ док.	Подп.	Дата	Светопрозрачные конструкции	Стадия	Лист	Листов
Разраб.		Бирюкова			06.23		Р	119	
Проверил									
Н.контр.									
						Ригельные сухари РС-1 и РС-2	ООО “МАРКА ПОЛА”		
Т.контр.									
Утв.									

Согласовано						
	ГАП					
Взам. инв. №	ГИП					
Подп. и дата						
Инв. № подл.	Изм.	Кол.уч.	Лист	№ док.	Подп.	Дата
	Разраб.	Бирюкова				06.23
	Проверил					
	Н.контр.					
	Т.контр.					
	Утв.					

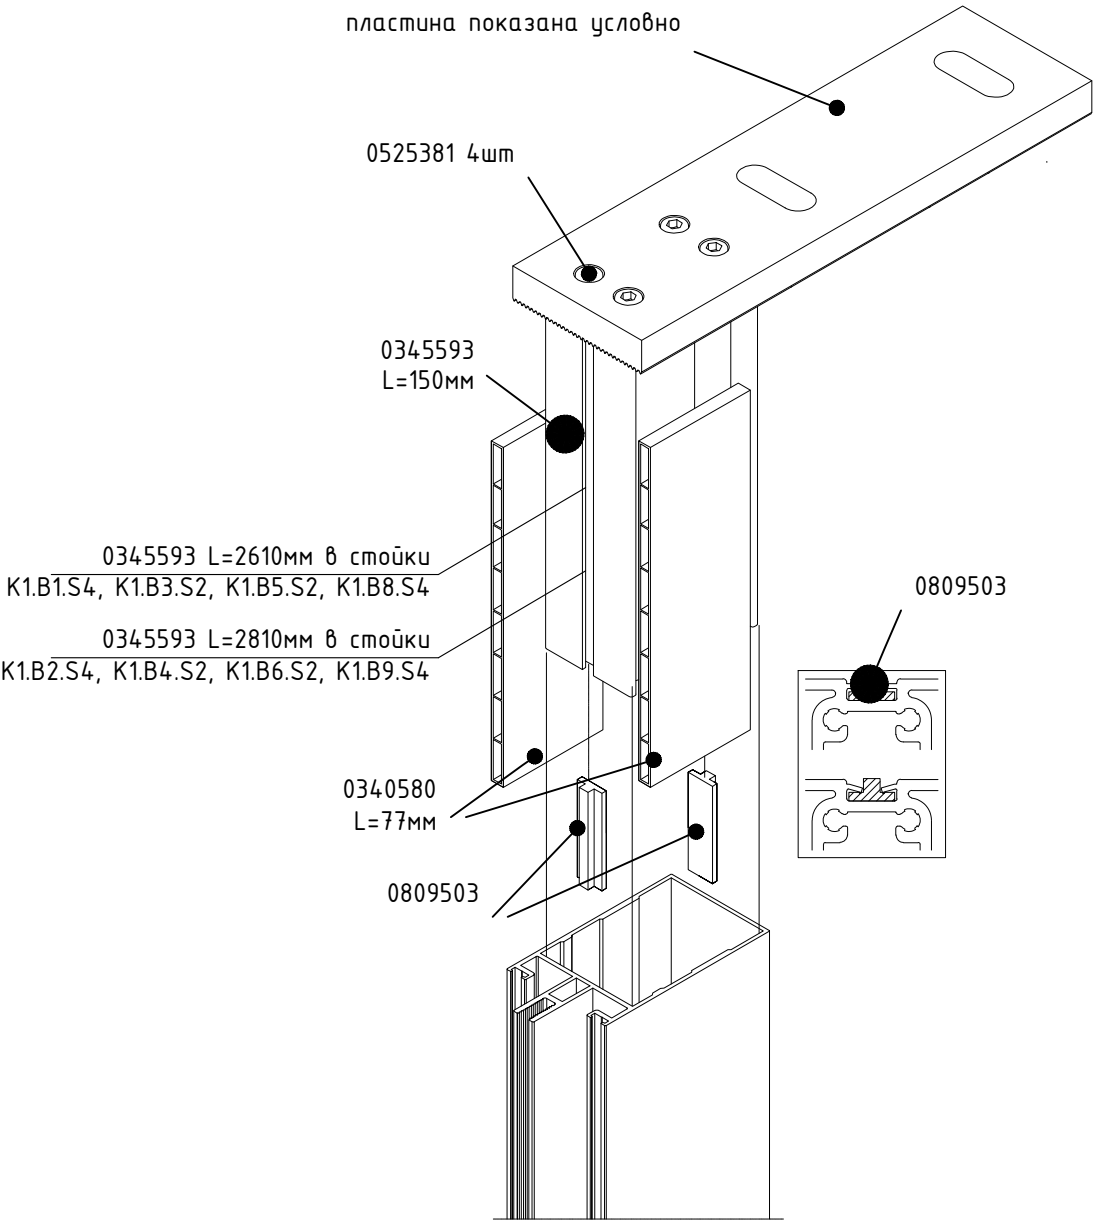

						Остров 2 К1				
						" Многофункциональная комплексная жилая застройка , квартал 2, корпус 1, 2, 3, 4, 5, 6 по адресу : г . Москва , внутригородская территория муниципальный округ Хорошёво –Мнёвники."				
Изм.	Кол.уч.	Лист	№ док.	Подп.	Дата	Светопрозрачные конструкции		Стадия	Лист	Листов
Разраб.		Бирюкова			06.23			Р	120	
Проверил										
Н.контр.										
						Столечные опорные детали		ООО "МАРКА ПОЛА"		
Т.контр.										
Утв.										